

# 리틀 포레스트 봉뜨락 조성공사

(건축, 구조)

2024.


봉 화 군

[illegible]

| 도면번호                 | 도면명                  | 측척     |        | 비고 |
|----------------------|----------------------|--------|--------|----|
|                      |                      | A1     | A3     |    |
| 근린생활시설 (석평리 1214-21) |                      |        |        |    |
| A01 - 001            | 배치도 및 건축개요           | 1 /150 | 1 /300 |    |
|                      |                      |        |        |    |
| A01 - 010            | 면적 산출표-1             | 1 /100 | 1 /200 |    |
| A01 - 011            | 면적 산출표-2             | 1 /100 | 1 /200 |    |
|                      |                      |        |        |    |
| A01 - 021            | 실내재료 마감표             | NONE   | NONE   |    |
| A01 - 022            | 실내재료 마감상세도-1         | 1 /5   | 1 /10  |    |
| A01 - 023            | 실내재료 마감상세도-2         | 1 /5   | 1 /10  |    |
|                      |                      |        |        |    |
| A01 - 101            | PIT층 평면도 (변경후)       | 1 /50  | 1 /100 |    |
| A01 - 102            | 1층 평면도 (변경후)         | 1 /50  | 1 /100 |    |
| A01 - 103            | 지붕 평면도 (변경후)         | 1 /50  | 1 /100 |    |
|                      |                      |        |        |    |
| A01 - 201            | 정면도 (변경후)            | 1 /50  | 1 /100 |    |
| A01 - 202            | 배면도 (변경후)            | 1 /50  | 1 /100 |    |
| A01 - 203            | 우측면도 (변경후)           | 1 /50  | 1 /100 |    |
| A01 - 204            | 좌측면도 (변경후)           | 1 /50  | 1 /100 |    |
|                      |                      |        |        |    |
| A01 - 301            | 중단면도 (변경후)           | 1 /40  | 1 /80  |    |
| A01 - 302            | 횡단면도 (변경후)           | 1 /40  | 1 /80  |    |
| A01 - 303            | 부분 입단면상세도 (변경후)      | 1 /40  | 1 /80  |    |
|                      |                      |        |        |    |
| A01 - 401            | 1층 창호평면도 (변경후)       | 1 /50  | 1 /100 |    |
| A01 - 402            | 창호 일람표-1 (변경후)       | 1 /40  | 1 /80  |    |
| A01 - 403            | 창호 일람표-2 (변경후)       | 1 /40  | 1 /80  |    |
|                      |                      |        |        |    |
| A01 - 501            | 화장실 전개도 (변경후)        | 1 /30  | 1 /60  |    |
|                      |                      |        |        |    |
| A01 - 901            | 형별성능내역-1 (벽 체)       | 1 /5   | 1 /10  |    |
| A01 - 902            | 형별성능내역-2 (바닥, 지붕)    | 1 /10  | 1 /20  |    |
| A01 - 903            | 형별성능내역-3 (문, 창문)     | 1 /10  | 1 /20  |    |
| A01 - 904            | 지상1층 바닥 및 외벽 단열 위치도  | 1 /50  | 1 /100 |    |
| A01 - 905            | 지붕 단열 위치도            | 1 /50  | 1 /100 |    |
|                      |                      |        |        |    |
| A01 - 1001           | 주1-1층 벽체평면도 (철 거)    | 1 /50  | 1 /100 |    |
| A01 - 1002           | 주1-1층 바닥평면도 (철 거)    | 1 /50  | 1 /100 |    |
| A01 - 1003           | 주1-1층 천장평면도 (철 거)    | 1 /50  | 1 /100 |    |
| A01 - 1004           | 주1-정면도 (철 거)         | 1 /50  | 1 /100 |    |
| A01 - 1005           | 주1-배면도 (철 거)         | 1 /50  | 1 /100 |    |
| A01 - 1006           | 주1-우측면도 (철 거)        | 1 /50  | 1 /100 |    |
| A01 - 1007           | 주1-좌측면도 (철 거)        | 1 /50  | 1 /100 |    |
| A01 - 1008           | 주1-중단면도 (철 거)        | 1 /40  | 1 /80  |    |
| A01 - 1009           | 주1-횡단면도 (철 거)        | 1 /40  | 1 /80  |    |
| A01 - 1010           | 주1-부분 입단면상세도 (철 거)   | 1 /40  | 1 /80  |    |
| A01 - 1011           | 주1-1층 창호평면도 (철 거)    | 1 /50  | 1 /100 |    |
| A01 - 1012           | 주1-창호 일람표-1 (철 거)    | 1 /40  | 1 /80  |    |
| A01 - 1013           | 주1-창호 일람표-2 (철 거)    | 1 /40  | 1 /80  |    |
|                      |                      |        |        |    |
| A01 - 1021           | 부1-1층 및 지붕 평면도 (철 거) | 1 /25  | 1 /50  |    |
| A01 - 1022           | 부1-A,B 입면도 (철 거)     | 1 /30  | 1 /60  |    |
| A01 - 1023           | 부1-C,D 입면도 (철 거)     | 1 /25  | 1 /50  |    |
| A01 - 1024           | 부1-주단면 상세도 (철 거)     | 1 /10  | 1 /20  |    |

| 도면번호               | 도            | 면 | 명        | 측      |        | 비 |
|--------------------|--------------|---|----------|--------|--------|---|
|                    |              |   |          | A1     | A3     |   |
| 운동시설 (석평리 1214-22) |              |   |          |        |        |   |
| A02 - 001          | 배치도 및 건축개요   |   |          | 1 /300 | 1 /600 |   |
|                    |              |   |          |        |        |   |
| A02 - 010          | 면적 산출표       |   |          | 1 /100 | 1 /200 |   |
|                    |              |   |          |        |        |   |
| A02 - 021          | 실내재료 마감표     |   |          | NONE   | NONE   |   |
| A02 - 022          | 실내재료 마감상세도-1 |   |          | 1 /5   | 1 /10  |   |
| A02 - 023          | 실내재료 마감상세도-2 |   |          | 1 /5   | 1 /10  |   |
|                    |              |   |          |        |        |   |
| A02 - 101          | 1층 평면도       |   | (변경후)    | 1 /75  | 1 /150 |   |
| A02 - 102          | 지붕 평면도       |   | (변경후)    | 1 /75  | 1 /150 |   |
|                    |              |   |          |        |        |   |
| A02 - 201          | 입면도-1        |   | (변경후)    | 1 /75  | 1 /150 |   |
| A02 - 202          | 입면도-2        |   | (변경후)    | 1 /75  | 1 /150 |   |
|                    |              |   |          |        |        |   |
| A02 - 301          | 주단면도-1       |   | (변경후)    | 1 /50  | 1 /100 |   |
| A02 - 302          | 주단면도-2       |   | (변경후)    | 1 /50  | 1 /100 |   |
| A02 - 303          | 주단면도-3       |   | (변경후)    | 1 /50  | 1 /100 |   |
| A02 - 304          | 주단면도-4       |   | (변경후)    | 1 /50  | 1 /100 |   |
| A02 - 305          | 주단면도-5       |   | (변경후)    | 1 /50  | 1 /100 |   |
| A02 - 306          | 주단면도-6       |   | (변경후)    | 1 /50  | 1 /100 |   |
|                    |              |   |          |        |        |   |
| A02 - 311          | 부분 단면상세도-1,2 |   | (변경후)    | 1 /50  | 1 /100 |   |
| A02 - 312          | 부분 단면상세도-3,4 |   | (변경후)    | 1 /50  | 1 /100 |   |
| A02 - 313          | 부분 단면상세도-5,6 |   | (변경후)    | 1 /50  | 1 /100 |   |
|                    |              |   |          |        |        |   |
| A02 - 401          | 1층 창호평면도     |   | (변경후)    | 1 /75  | 1 /150 |   |
| A02 - 402          | 창호 일람표       |   | (변경후)    | 1 /40  | 1 /80  |   |
|                    |              |   |          |        |        |   |
| A02 - 501          | 화장실 전개도-1    |   | (변경후)    | 1 /30  | 1 /60  |   |
| A02 - 502          | 화장실 전개도-2    |   | (변경후)    | 1 /30  | 1 /60  |   |
|                    |              |   |          |        |        |   |
| A02 - 901          | 형별기능내역-1     |   | (벽 체)    | 1 /5   | 1 /10  |   |
| A02 - 902          | 형별기능내역-2     |   | (바닥, 지붕) | 1 /10  | 1 /20  |   |
| A02 - 903          | 형별기능내역-3     |   | (문, 창문)  | 1 /10  | 1 /20  |   |
| A02 - 904          | 외피 전개도-1     |   | (외 벽)    | 1 /75  | 1 /150 |   |
| A02 - 905          | 외피 전개도-2     |   | (바 닥)    | 1 /75  | 1 /150 |   |
| A02 - 906          | 외피 전개도-3     |   | (지 붐)    | 1 /75  | 1 /150 |   |
|                    |              |   |          |        |        |   |
| A02 - 1001         | 1층 평면도       |   | (첼 거)    | 1 /75  | 1 /150 |   |
| A02 - 1002         | 입면도-1        |   | (첼 거)    | 1 /75  | 1 /150 |   |
| A02 - 1003         | 입면도-2        |   | (첼 거)    | 1 /75  | 1 /150 |   |
|                    |              |   |          |        |        |   |
|                    |              |   |          |        |        |   |
|                    |              |   |          |        |        |   |
|                    |              |   |          |        |        |   |
| S01 - 101          | 기초 구조평면도     |   |          | 1 /75  | 1 /150 |   |
| S01 - 102          | 1층 구조평면도     |   |          | 1 /75  | 1 /150 |   |
| S01 - 103          | 지붕 구조평면도     |   |          | 1 /75  | 1 /150 |   |
|                    |              |   |          |        |        |   |
| S02 - 101          | 보 일람표        |   |          | 1 /30  | 1 /60  |   |
| S02 - 102          | 슬라브 일람표      |   |          | 1 /30  | 1 /60  |   |
| S02 - 103          | 벽체 배근도       |   |          | 1 /15  | 1 /30  |   |

|               |   |
|---------------|---|
| PROJECT TITLE | 리틀 포레스트<br>봉뜨락 조성사업   |
| PROJECT NO    |   |
| NOTE          |   |
| KEY PLAN      |   |
| DESIGN CORP.  |  (주)이을건축사사무소<br>ADD. 대구광역시 동구 장동로 81, 5F<br>TEL. 053.716.0776 FAX. 0505.720.0776<br>E-mail. e-ul2020@naver.com<br>Web. eul2020 / 0776 |
| APPROVED BY   | 대표이사 / 건축사 권오섭   |
| CHECKED BY    |   |
| DRAWN BY      |   |
| DATE          | 2023. 04.   |
| DRAWING TITLE | 도면목록표   |
| SCALE         | A3 : 1/ NONE   |
| DRAWING NO.   | A00-001   |

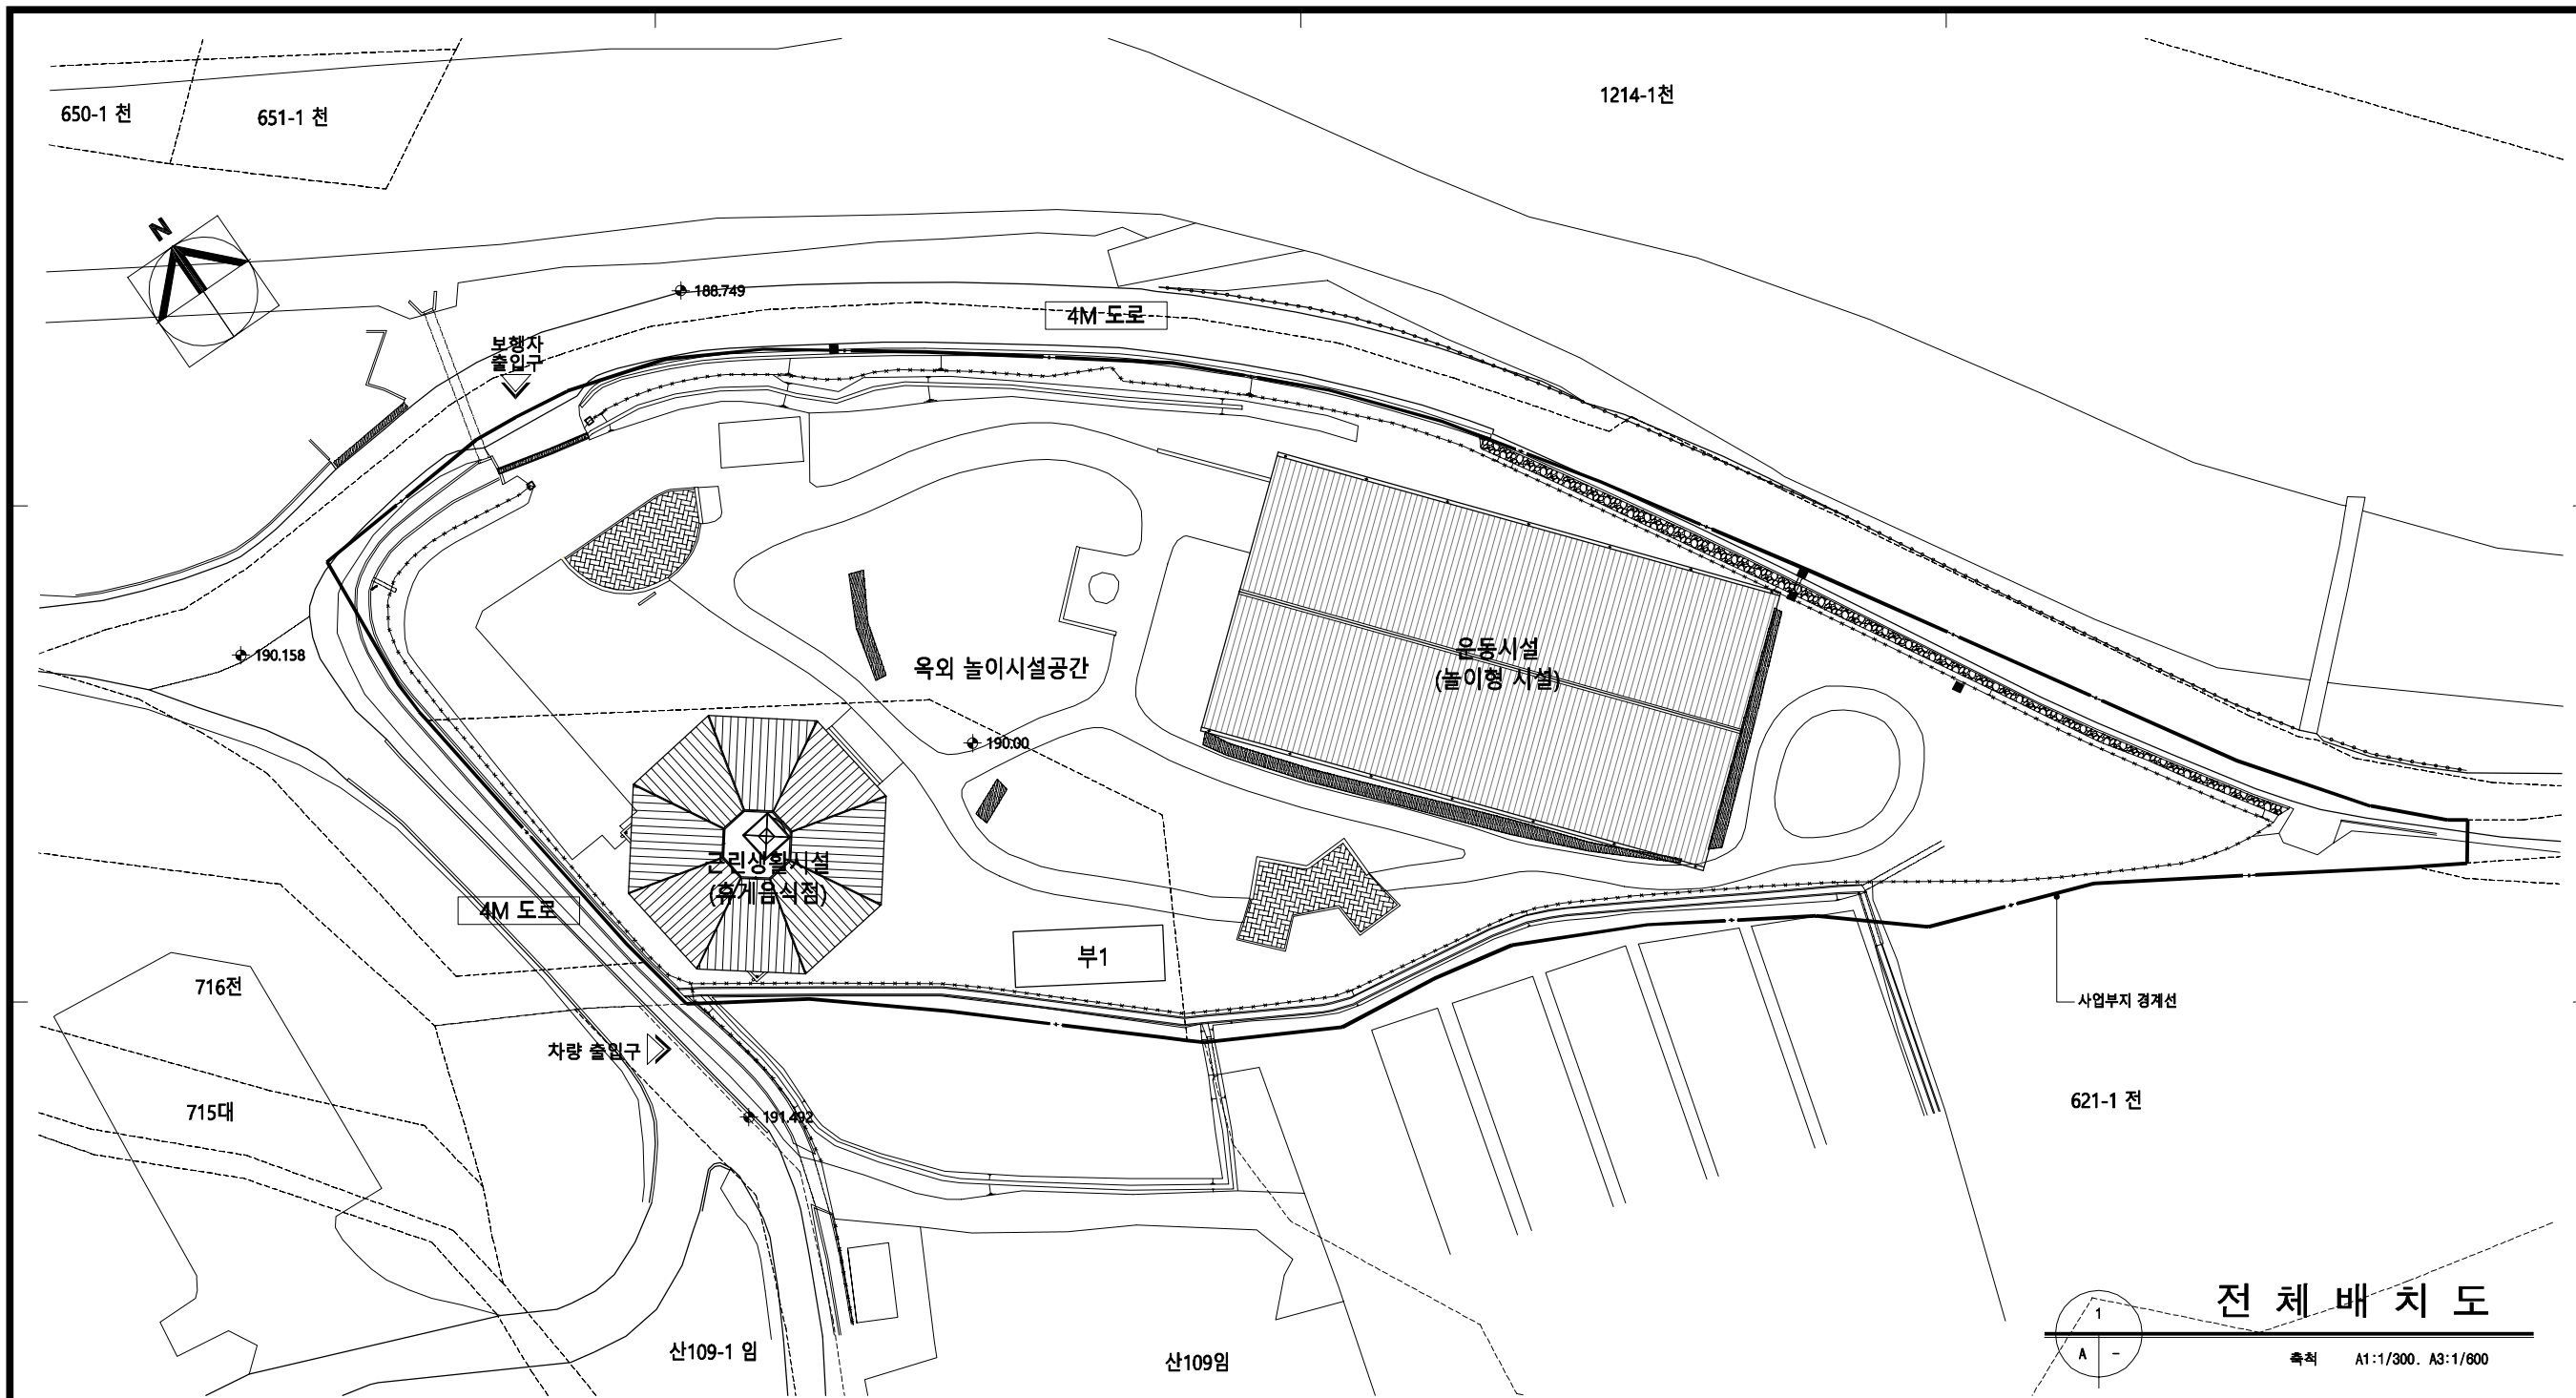

전 체 사 업 개 요

|         |                                  |                                   |             |         |     |     |             |          |          |         |   |       |       |
|---------|----------------------------------|-----------------------------------|-------------|---------|-----|-----|-------------|----------|----------|---------|---|-------|-------|
| 대 지 위 치 |                                  | 경상북도 봉화군 봉화읍 석평리 1214-21, 1241-22 |             | 바 닥 면 적 | 층 별 | 용 도 | 면 적         |          | 소 계      | 주 차     | 법 정   | 해당없음. | 0.0 대 |
| 대 지 면 적 | 석평리 1214-21                      | 1,214.00                          | 석평리 1214-21 |         |     |     | 석평리 1214-22 | 설 계      |          |         | -   | 0.0 대 |       |
|         | 석평리 1214-22                      | 5,009.00                          |             |         |     |     |             |          |          |         |   |       |       |
|         |                                  |                                   |             |         |     |     |             |          |          |         |   |       |       |
|         | 계                                | 6,223.00                          |             |         |     |     |             |          |          |         |   |       |       |
| 지 역 지 구 | 계획관리지역                           |                                   |             | 건 축 면 적 |     |     | 363.41      | 924.00   | 1,287.41 | 기 타     | 1. 석평리 1214-21<br><br>주1 건축물을 운동시설에서 제1종 근생으로 변경, 부1은 철거예정<br><br>주요구조부의 변경 없이 비내력벽만 변경하는 공사임.<br><br>2. 석평리 1214-22<br><br>운동시설(승마장)에서 운동시설(놀이형시설)로 기재사항변경임.<br><br>주요구조부의 변경 없는 실내공사임. |       |       |
| 도 로 현 황 | 북측 : 4M도로 / 서측 : 4M도로            |                                   |             | 연 면 적   |     |     | 351.99      | 924.00   | 1,275.99 |         |   |       |       |
| 건 물 용 도 | 제1종 근린생활시설 (휴게음식점), 운동시설(놀이형 시설) |                                   |             | 건 폐 율   |     | 법 정 | 40.00 %     | 40.00 %  | 40.00 %  |         |   |       |       |
|         |                                  |                                   |             |         |     |     | 설 계         | 29.93 %  | 18.45 %  |         |   |       |       |
| 층 수     | 지상 1층 / 지상 1층                    |                                   |             | 용 적 율   |     | 법 정 | 100.00 %    | 100.00 % | 100.00 % |         |   |       |       |
| 건 물 높 이 | 8.97 M / 6.55 M                  |                                   |             |         |     |     | 설 계         | 28.99 %  | 18.45 %  | 20.50 % |   |       |       |

PROJECT TITLE

리틀 포레스트  
봉뜨락 조성사업

PROJECT NO

NOTE

KEY PLAN

전 체 배 치 도

축척 A1:1/300. A3:1/600

DESIGN CORP.

**이원** (주)이원건축사사무소

ADD. 대구광역시 동구 장동로 81, 5F  
TEL. 053.716.0776 FAX. 0505.720.0776  
E-mail. e-ul2020@naver.com  
Web. eul2020 / 0776

APPROVED BY  
대 표 이 사 / 건 축 사 권 오 설  
CHECKED BY

DRAWN BY


DATE 2023. 04.

DRAWING TITLE

전체 배치도 및  
전체 사업개요

SCALE A3 : 1/ 600

DRAWING NO. A00- 101

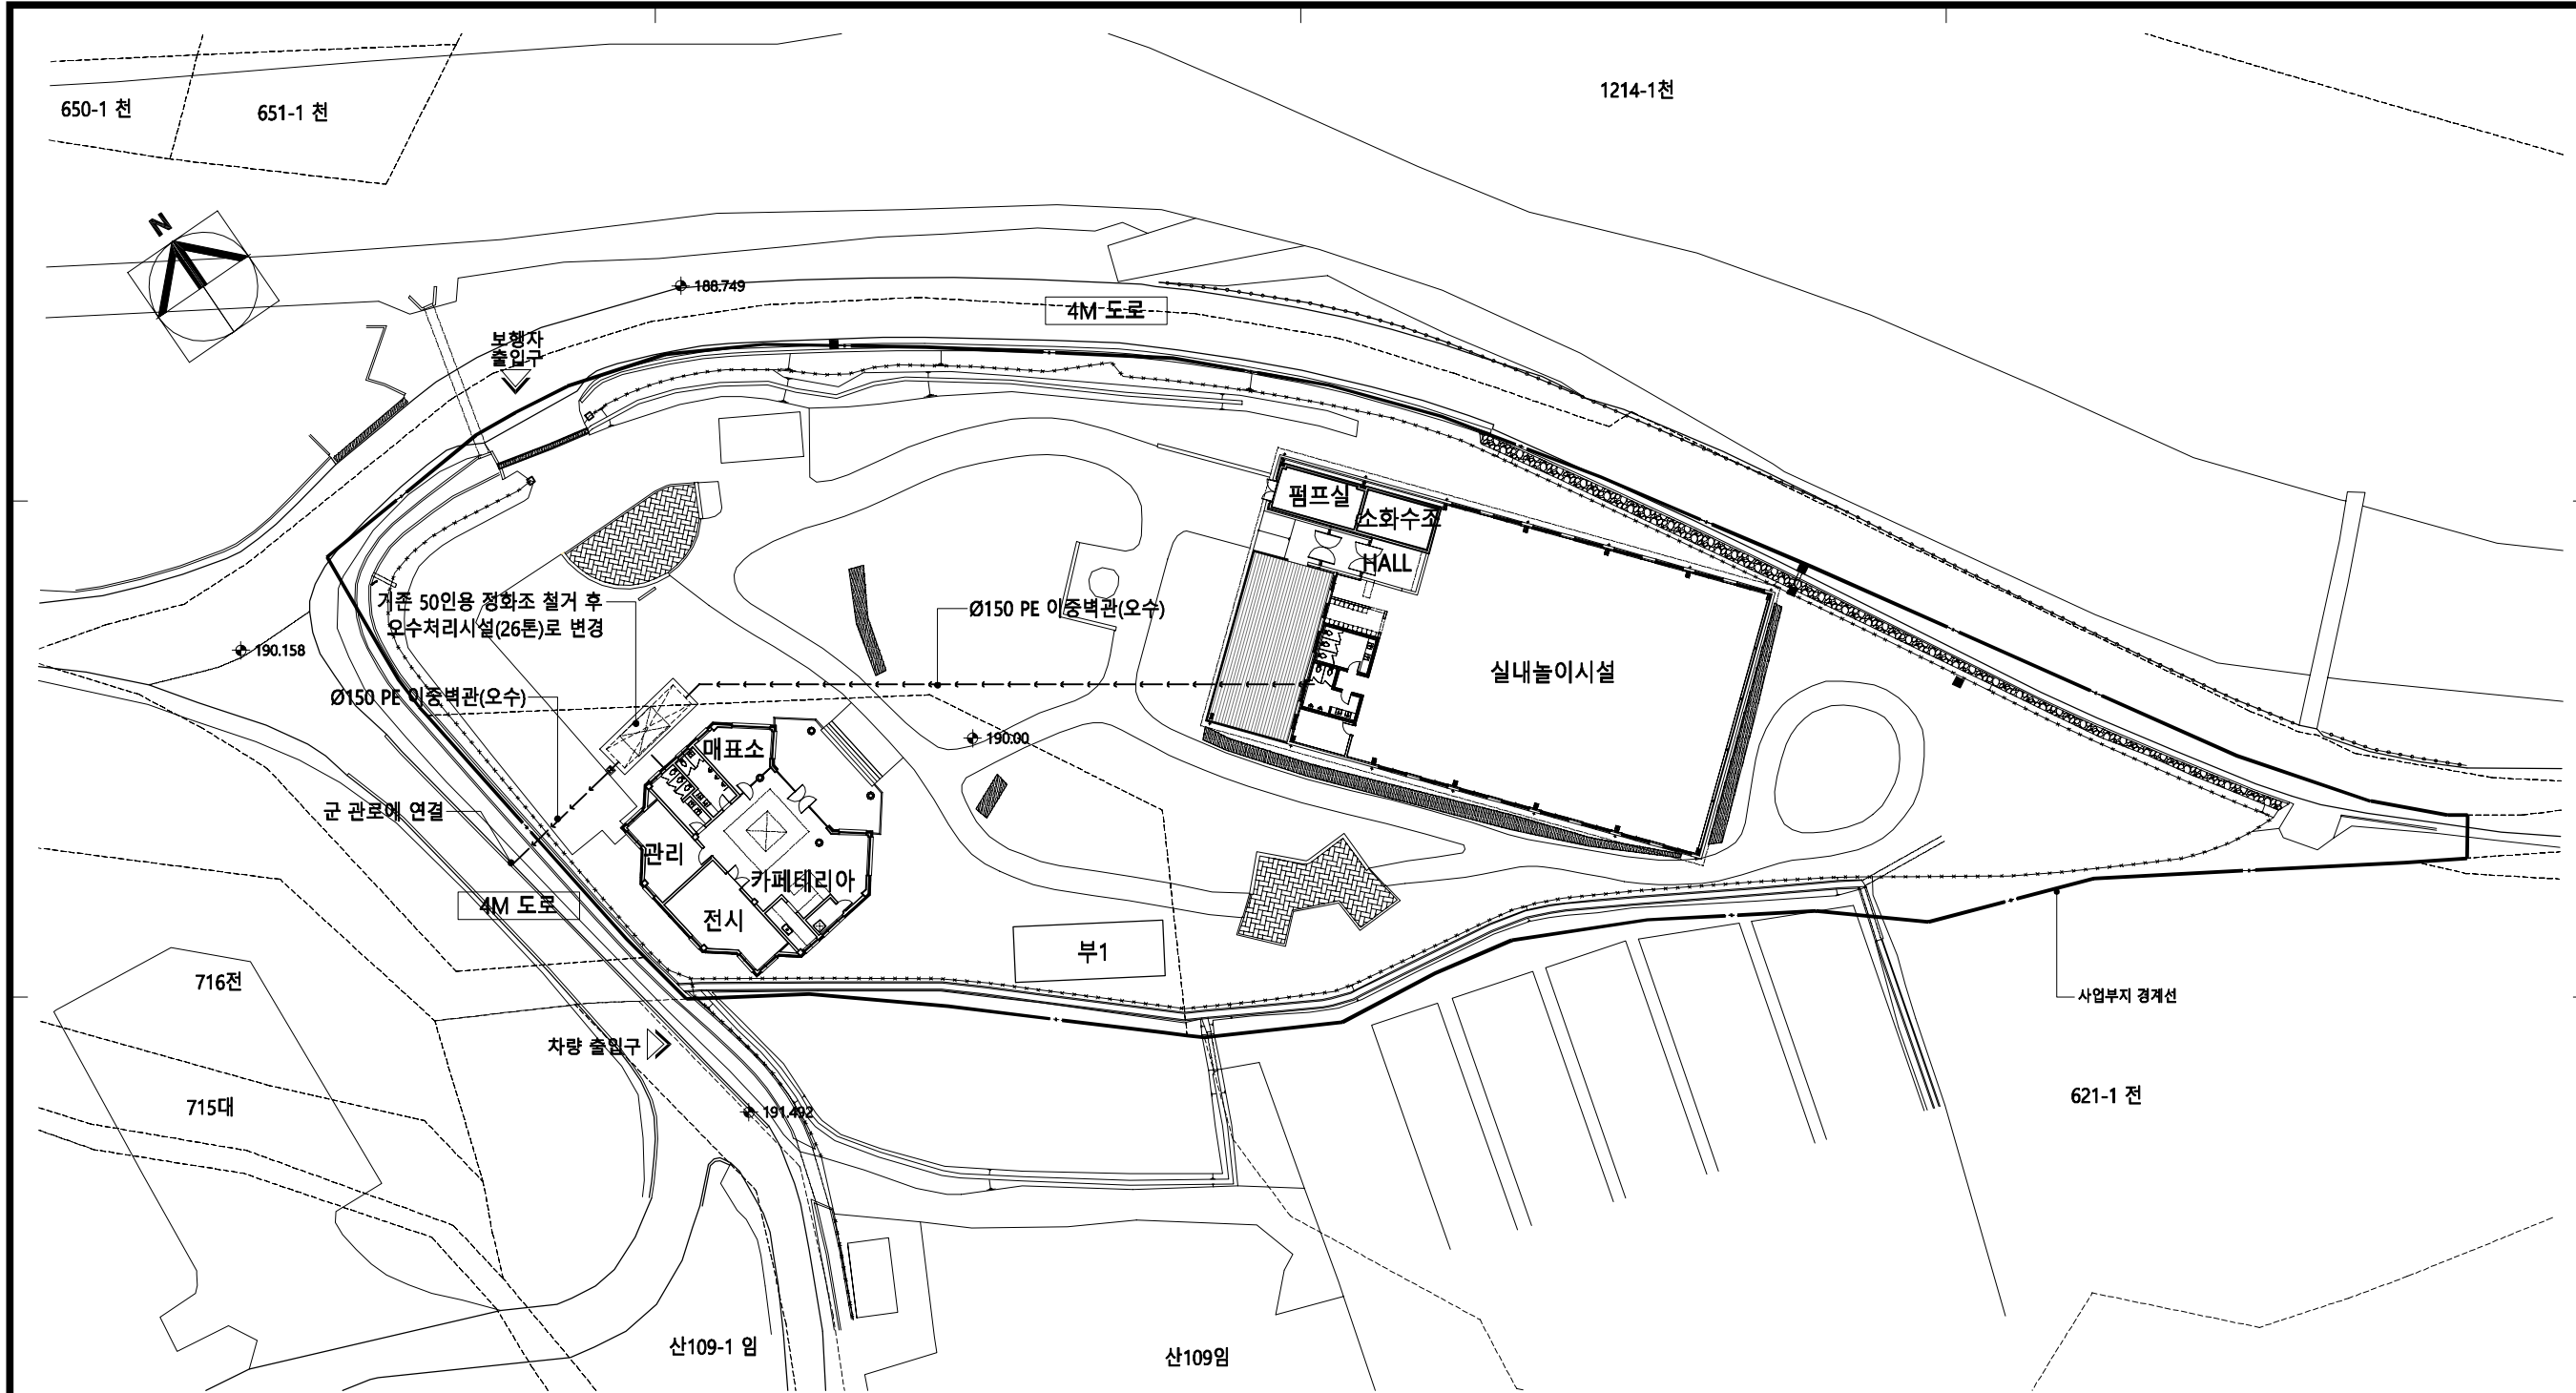

1  
A -  
축척 A1:1/300, A3:1/600

## 오 수 계 획 도

### 오 수 설 비

| 구 분       | 구 격           | 단 위 | 수 량   | 비 고 |
|-----------|---------------|-----|-------|-----|
| ☒ 스크린오수면물 | 600 x 600     | 개   | 1     |     |
| → 오수관     | Ø 150 PE 이중벽관 | M   | 71.50 |     |
|           |               |     |       |     |
|           |               |     |       |     |

PROJECT TITLE  
리틀 포레스트  
봉뜨락 조성사업

PROJECT NO

NOTE

KEY PLAN

DESIGN CORP.  
**에이엘** (주)아을건축사사무소  
ADD. 대구광역시 동구 장동로 81, 5F  
TEL. 053.716.0776 FAX. 0505.720.0776  
E-mail. e-ul2020@naver.com  
Web. eul2020 / 0776

APPROVED BY  
대표이사 / 건축사 권 오 설

CHECKED BY

DRAWN BY

DATE  
2023. 04.

DRAWING TITLE  
오수계획도

SCALE  
A3 : 1/ 600

DRAWING NO.  
A00- 201

PROJECT TITLE

리틀 포레스트  
봉뜨락 조성사업

PROJECT NO

NOTE

KEY PLAN

DESIGN CORP.

**OHM** (주)아울건축사사무소

ADD. 대구광역시 동구 장동로 81, 5F  
TEL. 053.716.0776 FAX. 0505.720.0776  
E-mail. e-ul2020@naver.com  
Web. eul2020 / 0776

APPROVED BY  
대표이사 / 건축사 권오섭

CHECKED BY

DRAWN BY


DATE  
2023. 04.

DRAWING TITLE



오수처리시설 골조도

SCALE  
A3 : 1/ 60


DRAWING NO.  
A00- 211

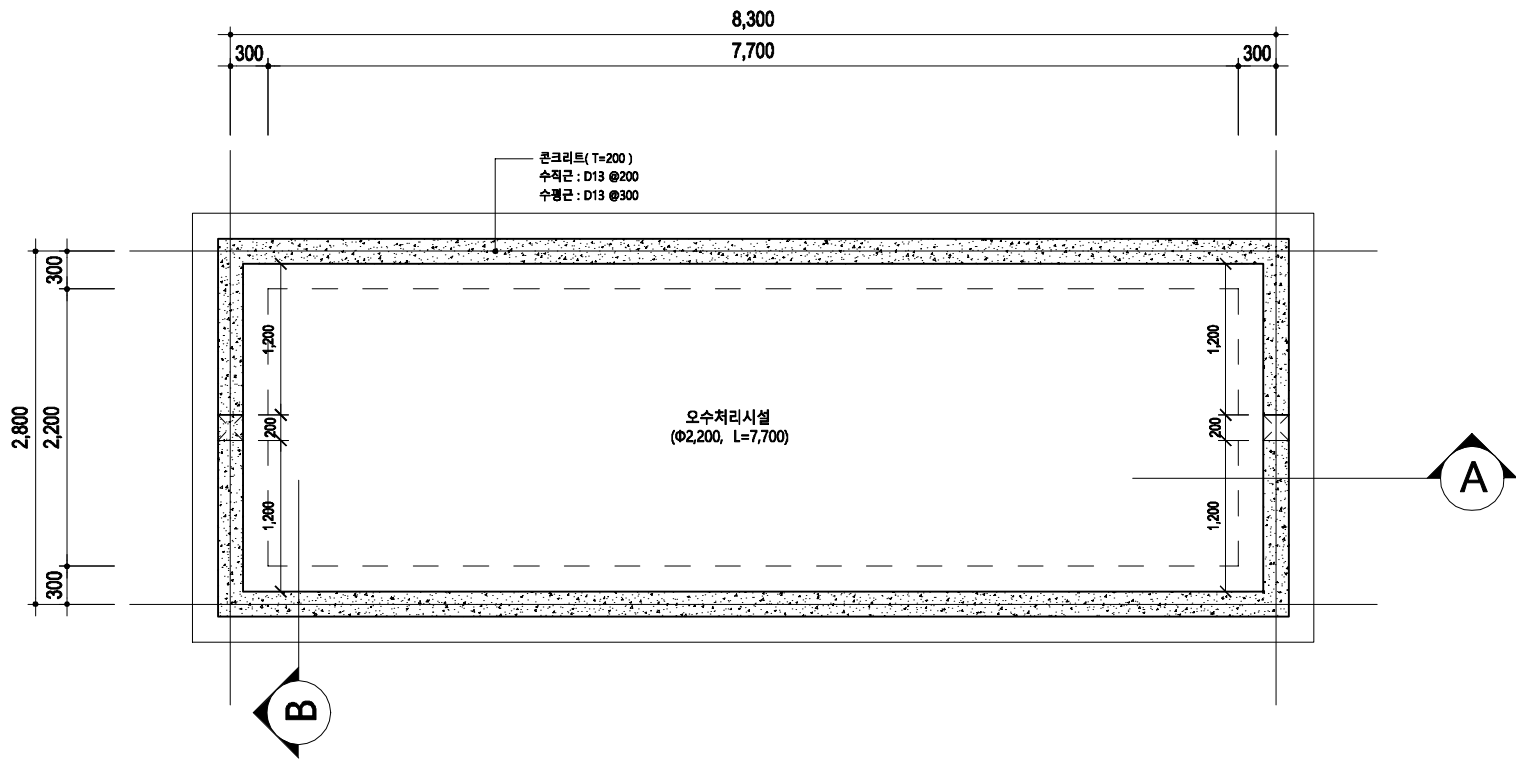


평면도

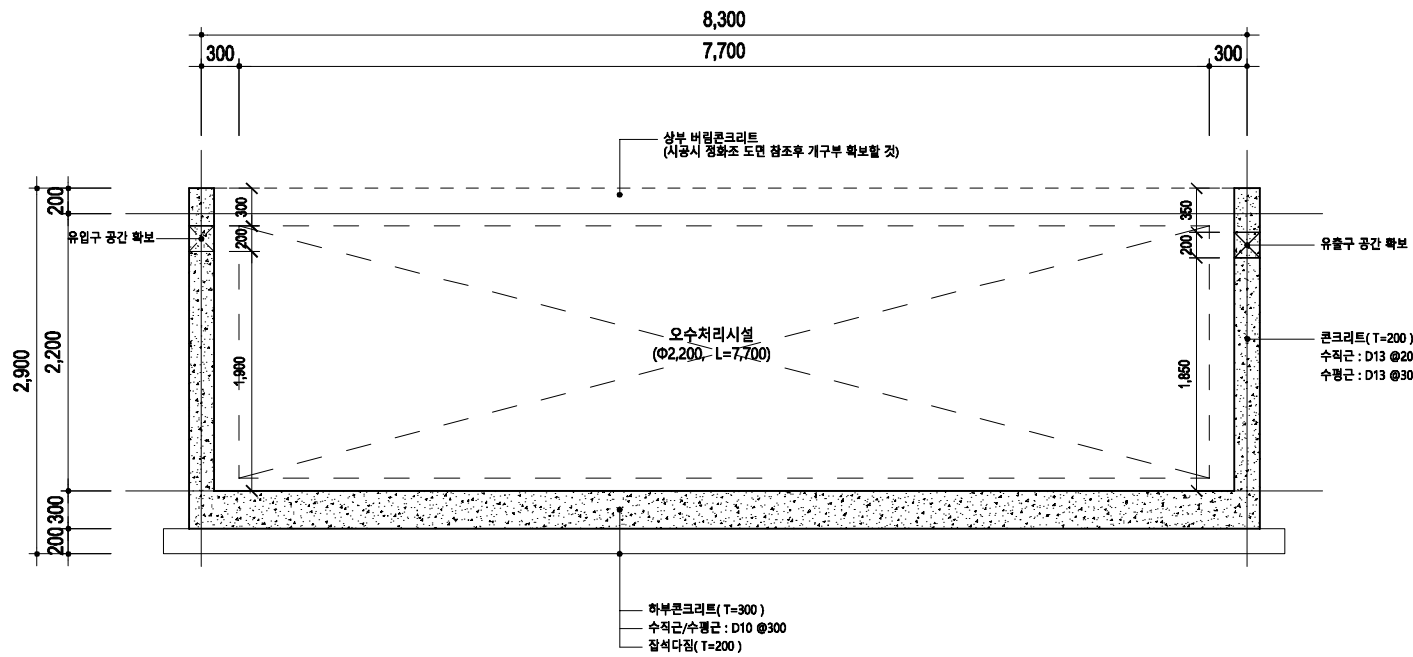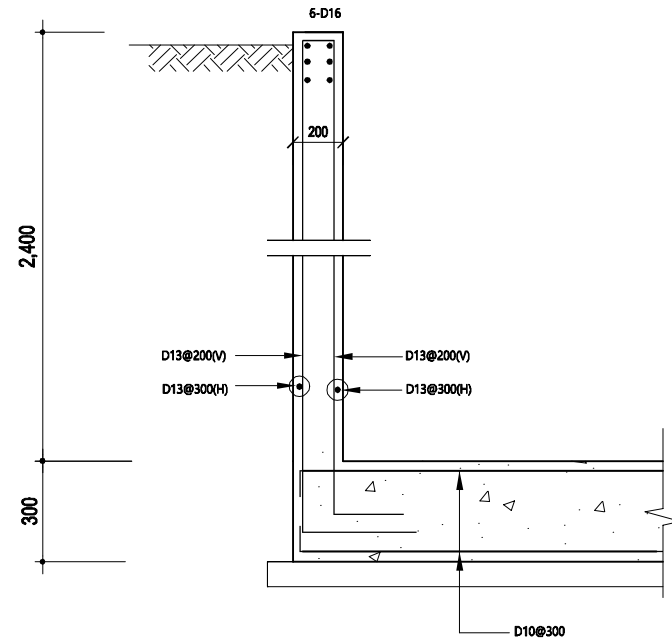

A 단면도

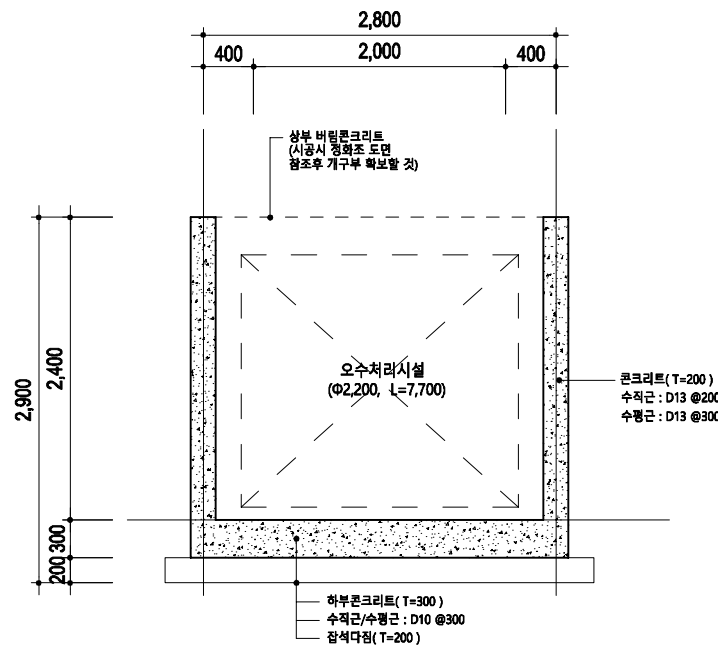

B 단면도

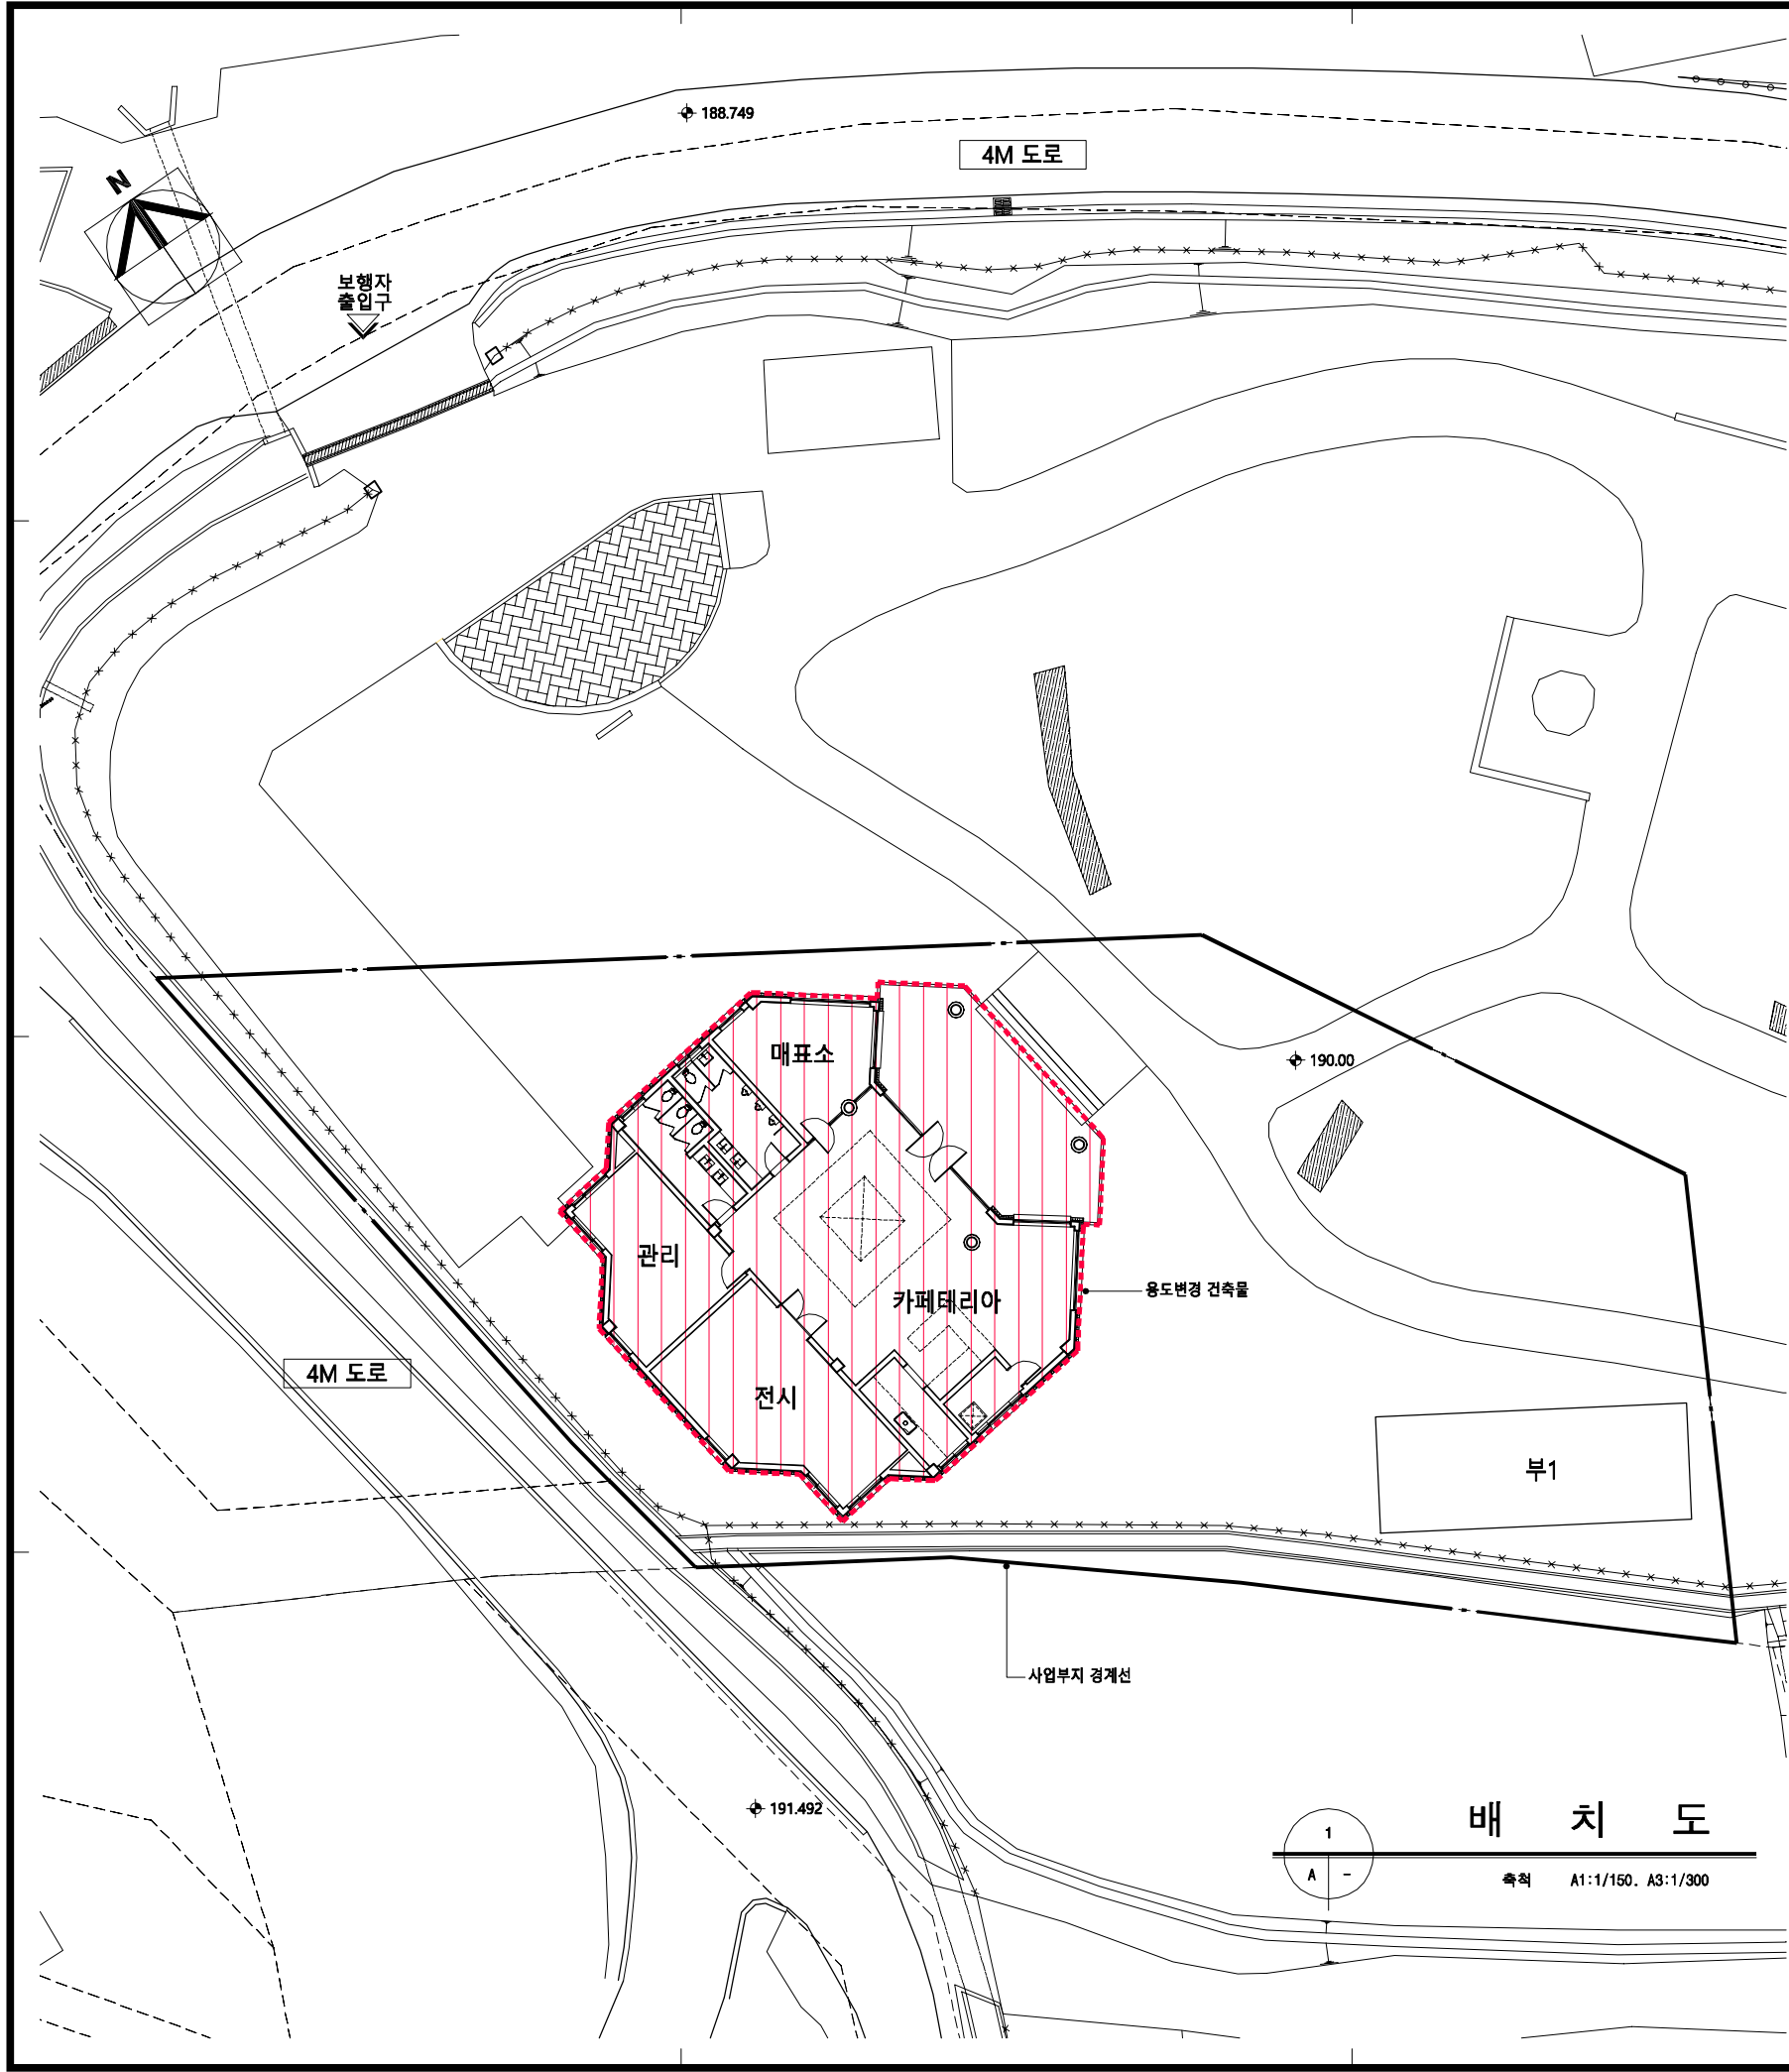

■ 건축 개요

단위: m²

|         |   |                 |              |
|---------|---|-----------------|--------------|
| 대 지 위 치 | 경상북도 봉화군 봉화읍 석평리 1214-21   |                 |              |
| 대 지 면 적 | 석평리 1214-21   |                 | 1,214.00     |
|         |   |                 |              |
|         | 계   |                 | 1,214.00     |
| 지 역 지 구 | 계획관리지역   |                 |              |
| 도 로 현 황 | 서측 : 4M도로   |                 |              |
| 건 물 용 도 | 주1: 제1종 근린생활시설 (휴게음식점) / 부1: 운동시설(승마장)   |                 |              |
| 구 조     | 주1: 철근콘크리트구조 / 부1: 경량철골조   |                 |              |
| 층 수     | 주1: 지상 1층 / 부1: 지상 1층   |                 |              |
| 건 물 높 이 | 주1: 8.97 M / 부1: 3.9 M   |                 |              |
| 바 닥 면 적 | 변 경 전   |                 |              |
|         | 구분   | 층별 용 도          | 면 적          |
|         | 주1   | 1 운동시설(승마장)     | 297.99       |
|         | 부1   | 1 운동시설(승마장)     | 54.00        |
|         | 계   |                 | 351.99       |
| 건 축 면 적 | 363.41   |                 |              |
| 연 면 적   | 351.99   |                 |              |
| 건 폐 율   | 법 정   | 40.00 %         | 법 정 40.00 %  |
|         | 설 계   | 29.93 %         | 설 계 29.93 %  |
| 용 적 율   | 법 정   | 100.00 %        | 법 정 100.00 % |
|         | 설 계   | 28.99 %         | 설 계 28.99 %  |
| 주 차     | 법 정   | 해당없음.           | 0.0 대        |
|         | 설 계   | -               | 0.0 대        |
| 오수처리시설  | 법 정   | 297.99 X 35l/m² | 10.43 (m³/일) |
|         | 설 계   |                 | 26.00 (m³/일) |
| 기 타     | 1. 주1 건축물을 운동시설에서 제1종 근생으로 변경하고자 함.<br>2. 주요구조부의 변경 없이 비내력벽만 변경하는 공사임.<br>3. 건축구조기준설계하중 (KDS 41 10 05) 기준에 따라 설계하중이 5%미만의 용도변경일 경우 구조안전확인서 제출대상에서 제외됨.<br>체육시설(5.0kN/m2) → 식당(5.0kN/m2)으로 용도변경 이며 설계하중의 변경이 없으므로 구조안전확인서 제출을 제외함. |                 |              |

PROJECT TITLE

리틀 포레스트  
봉뜨락 조성사업

PROJECT NO

NOTE

KEY PLAN

DESIGN CORP.

ADD. 대구광역시 동구 장동로 81, 5F  
TEL. 053.716.0776 FAX. 0505.720.0776  
E-mail. e-ul2020@naver.com  
Web. eul2020 / 0776

APPROVED BY

대표이사 / 건축사 권오섭

CHECKED BY

DRAWN BY

DATE

2023. 04.

DRAWING TITLE

배치도 및 건축개요  
(석평리 1214-21)


SCALE

A3 : 1/ 300


DRAWING NO.

A01-001

주1  
1층 바닥 면적 산출표

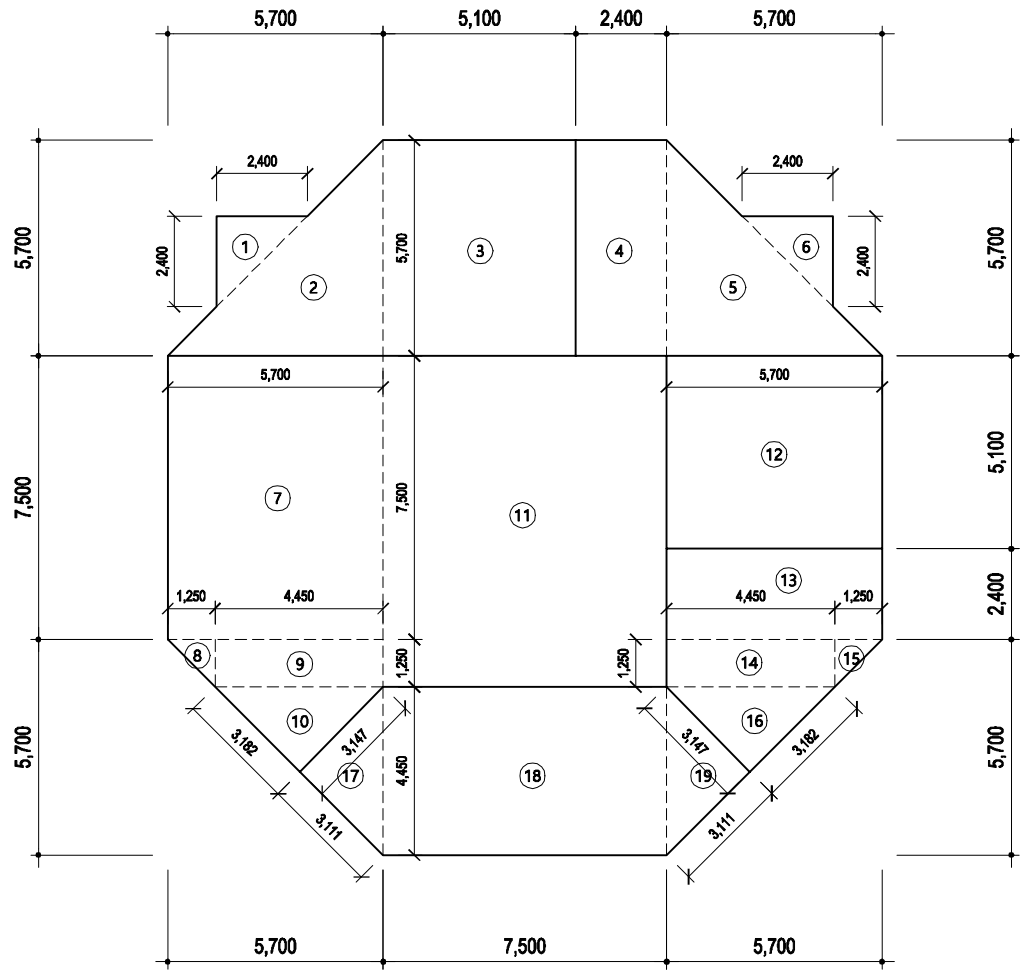

주1  
건축면적 산출표

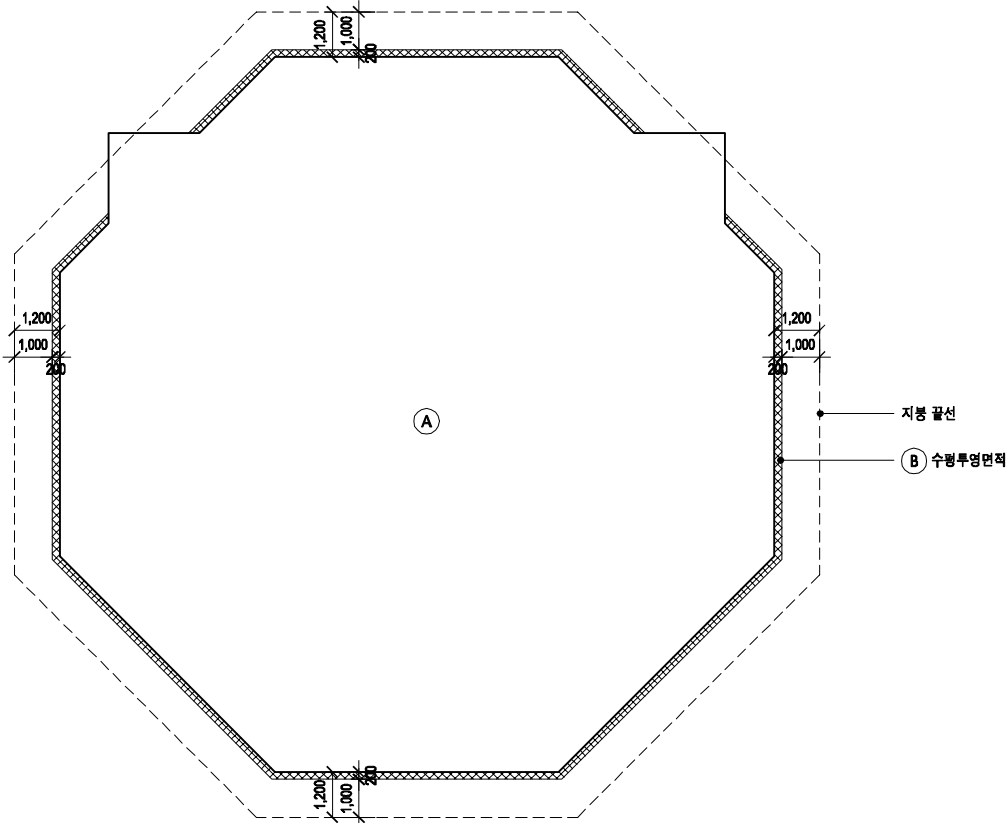

| 구 분   |   | 산 출 근 거             | 면 적     |
|-------|---|---------------------|---------|
| 전 시 실 | ① | 2.400 X 2.400 X 0.5 | 2.880   |
|       | ② | 5.700 X 5.700 X 0.5 | 16.245  |
|       | ③ | 5.100 X 5.700       | 29.070  |
| 관 리 실 | ④ | 2.400 X 5.700       | 13.680  |
|       | ⑤ | 5.700 X 5.700 X 0.5 | 16.245  |
|       | ⑥ | 2.400 X 2.400 X 0.5 | 2.880   |
| 카페테리아 | ⑦ | 5.700 X 7.500       | 42.750  |
|       | ⑧ | 1.250 X 1.250 X 0.5 | 0.781   |
|       | ⑨ | 4.450 X 1.250       | 5.563   |
|       | ⑩ | 3.182 X 3.147 X 0.5 | 5.006   |
|       | ⑪ | 7.500 X 8.750       | 65.625  |
| 화 장 실 | ⑫ | 5.700 X 5.100       | 29.070  |
| 매 표 소 | ⑬ | 5.700 X 2.400       | 13.680  |
|       | ⑭ | 4.450 X 1.250       | 5.563   |
|       | ⑮ | 1.250 X 1.250 X 0.5 | 0.781   |
| 휴게데크  | ⑯ | 3.182 X 3.147 X 0.5 | 5.006   |
|       | ⑰ | 3.111 X 3.147 X 0.5 | 4.895   |
|       | ⑱ | 7.500 X 4.450       | 33.375  |
|       | ⑲ | 3.111 X 3.147 X 0.5 | 4.895   |
| 합 계   |   |                     | 297.990 |

| 구 분     |   | 산 출 근 거 | 면 적     |
|---------|---|---------|---------|
| 1층 바닥면적 | Ⓐ |         | 297.990 |
| 수평투영면적  | Ⓑ | CAD 구적  | 11.420  |
| 합 계     |   |         | 309.410 |

PROJECT TITLE  
리틀 포레스트  
봉뜨락 조성사업

PROJECT NO

NOTE

KEY PLAN

DESIGN CORP.  
  
ADD. 대구광역시 동구 장동로 81, 5F  
TEL. 053.716.0776 FAX. 0505.720.0776  
E-mail. e-ul2020@naver.com  
Web. eul2020 / 0776

APPROVED BY  
대표이사 / 건축사 권오섭

CHECKED BY

DRAWN BY


DATE  
2023. 04.

DRAWING TITLE  
면적산출표-1

SCALE  
A3 : 1/ 200

DRAWING NO.  
A01-010

|              |  |                                                          |                                                          |       |                |                |                                                                        |     |
|--------------|--|----------------------------------------------------------|----------------------------------------------------------|-------|----------------|----------------|------------------------------------------------------------------------|-----|
| 부1           |  | <div><div>12,000</div><div>4,500</div><div>①</div></div> | 구 분                                                      |       | 산 출 근 거        | 면 적            | PROJECT TITLE<br><br>리틀 포레스트<br>봉뜨락 조성사업<br><br>PROJECT NO<br><br>NOTE |     |
| 1층 바닥 면적 산출표 |  |                                                          | 부속건축물                                                    | ①     | 12.000 X 4.500 | 54.000         |                                                                        |     |
|              |  |                                                          |                                                          |       |                |                |                                                                        |     |
|              |  |                                                          | 합 계                                                      |       |                | 54.000         |                                                                        |     |
| 부1           |  |                                                          | <div><div>12,000</div><div>4,500</div><div>Ⓐ</div></div> | 구 분   |                | 산 출 근 거        |                                                                        | 면 적 |
| 건축면적 산출표     |  |                                                          |                                                          | 부속건축물 | Ⓐ              | 12.000 X 4.500 | 54.000                                                                 |     |
|              |  |                                                          |                                                          |       |                |                |                                                                        |     |
|              |  |                                                          |                                                          | 합 계   |                |                | 54.000                                                                 |     |

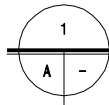

# 실내재료 마감표

축척 A1, A3: 1/NONE

| 구 분            | 바 닥          |                      |     | 걸 레 받 이     |          |     | 벽                   |                       |     | 천 장                    |                        |                | 상세번호 | 비 고 |
|----------------|--------------|----------------------|-----|-------------|----------|-----|---------------------|-----------------------|-----|------------------------|------------------------|----------------|------|-----|
| 실 명            | 바 랑          | 마 갑                  | 두 께 | 바 랑         | 마 갑      | 높 이 | 바 랑                 | 마 갑                   | 두 께 | 바 랑                    | 마 갑                    | 천장고            |      |     |
| 홀              | THK97 시멘트몰탈  | THK3 데코타일            | 100 | THK18 시멘트몰탈 | 수성페인트 2회 | 100 | THK18 시멘트몰탈         | 수성페인트 2회              | -   | 경량철골 천정틀(M-BAR)        | THK9.5 석고보드 / 수성페인트 2회 | 3,600 or 4,700 | 01A  |     |
|                | THK47 시멘트몰탈  |                      | 50  | THK9.5 석고보드 |          |     | THK9.5 석고보드         |                       |     |                        |                        |                | 01B  |     |
| 카페테리아          | THK97 시멘트몰탈  | THK3 데코타일            | 100 | THK9.5 석고보드 | 수성페인트 2회 | 100 | THK9.5 석고보드         | 수성페인트 2회              | -   | 경량철골 천정틀(M-BAR)        | THK9.5 석고보드 / 수성페인트 2회 | 3,600          | 02   |     |
| 보조주방           | THK97 시멘트몰탈  | THK3 데코타일            | 100 | THK9.5 석고보드 | 수성페인트 2회 | 100 | THK9.5 석고보드         | 수성페인트 2회              | -   | 경량철골 천정틀(M-BAR)        | 지정텍스                   | 2,900          | 03A  |     |
| 매표소            | THK97 시멘트몰탈  | THK3 데코타일            | 100 | THK18 시멘트몰탈 | 수성페인트 2회 | 100 | THK18 시멘트몰탈         | 수성페인트 2회              | -   | 경량철골 천정틀(M-BAR)        | 지정텍스                   | 2,900          | 03A  |     |
|                |              |                      |     | THK9.5 석고보드 |          |     | THK9.5 석고보드         |                       |     |                        |                        |                | 03B  |     |
| 전시실            | THK47 시멘트몰탈  | THK3 데코타일            | 50  | THK9.5 석고보드 | 수성페인트 2회 | 100 | THK9.5 석고보드         | 수성페인트 2회              | -   | 경량철골 천정틀(M-BAR)        | 지정텍스                   | 2,300 or 2,900 | 04A  |     |
| 관리실            | THK47 시멘트몰탈  | THK3 데코타일            | 50  | THK18 시멘트몰탈 | 수성페인트 2회 | 100 | THK18 시멘트몰탈         | 수성페인트 2회              | -   | 경량철골 천정틀(M-BAR)        | 지정텍스                   | 2,300 or 2,900 | 04A  |     |
|                |              |                      |     | THK9.5 석고보드 |          |     | THK9.5 석고보드         |                       |     |                        |                        |                | 04B  |     |
| 화장실(남), 화장실(여) | 액체방수 / 구배몰탈  | THK5 자기질타일 (300X300) | 100 | THK18 시멘트몰탈 | -        | -   | 액체방수(h=1,200), 보호몰탈 | THK7 도기질벽타일 (300X600) | -   | 경량철골 천정틀 (AL CLIP-BAR) | PVC 천정재                | 2,400          | 05   |     |
| PIT 점검실        | THK100 시멘트몰탈 | 에폭시 페인트              | 100 | THK9.5 석고보드 | -        | -   | THK9.5 석고보드         | 수성페인트 2회              | -   | 경량철골 천정틀(M-BAR)        | 지정텍스                   | 2,400          | 06   |     |
|                |              |                      |     |             |          |     |                     |                       |     |                        |                        |                |      |     |
PROJECT TITLE

리틀 포레스트  
봉뜨락 조성사업

PROJECT NO

NOTE

KEY PLAN

DESIGN CORP.



ADD. 대구광역시 동구 장동로 81, 5F  
TEL. 053.716.0776 FAX. 0505.720.0776  
E-mail. e-ul2020@naver.com  
Web. eul2020 / 0776

APPROVED BY  
대표이사 / 건축사 권오섭

CHECKED BY

DRAWN BY


DATE 2023. 04.

DRAWING TITLE

실내재료 마감표

SCALE A3 : 1/ NONE

DRAWING NO. A01-021

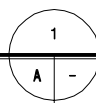

실내재료마감 상세도-1

축척 A1:1/5, A3:1/10

PROJECT TITLE

리틀 포레스트  
봉뜨락 조성사업

PROJECT NO

NOTE

KEY PLAN

DESIGN CORP.



ADD. 대구광역시 동구 장동로 81, 5F  
TEL. 053.716.0776 FAX. 0505.720.0776  
E-mail. e-ul2020@naver.com  
Web. eul2020 / 0776

APPROVED BY  
대표이사 / 건축사 권오섭

CHECKED BY

DRAWN BY


DATE  
2023. 04.


DRAWING TITLE

실내재료마감 상세도-1

SCALE  
A3 : 1/ 10

DRAWING NO.  
A01-022

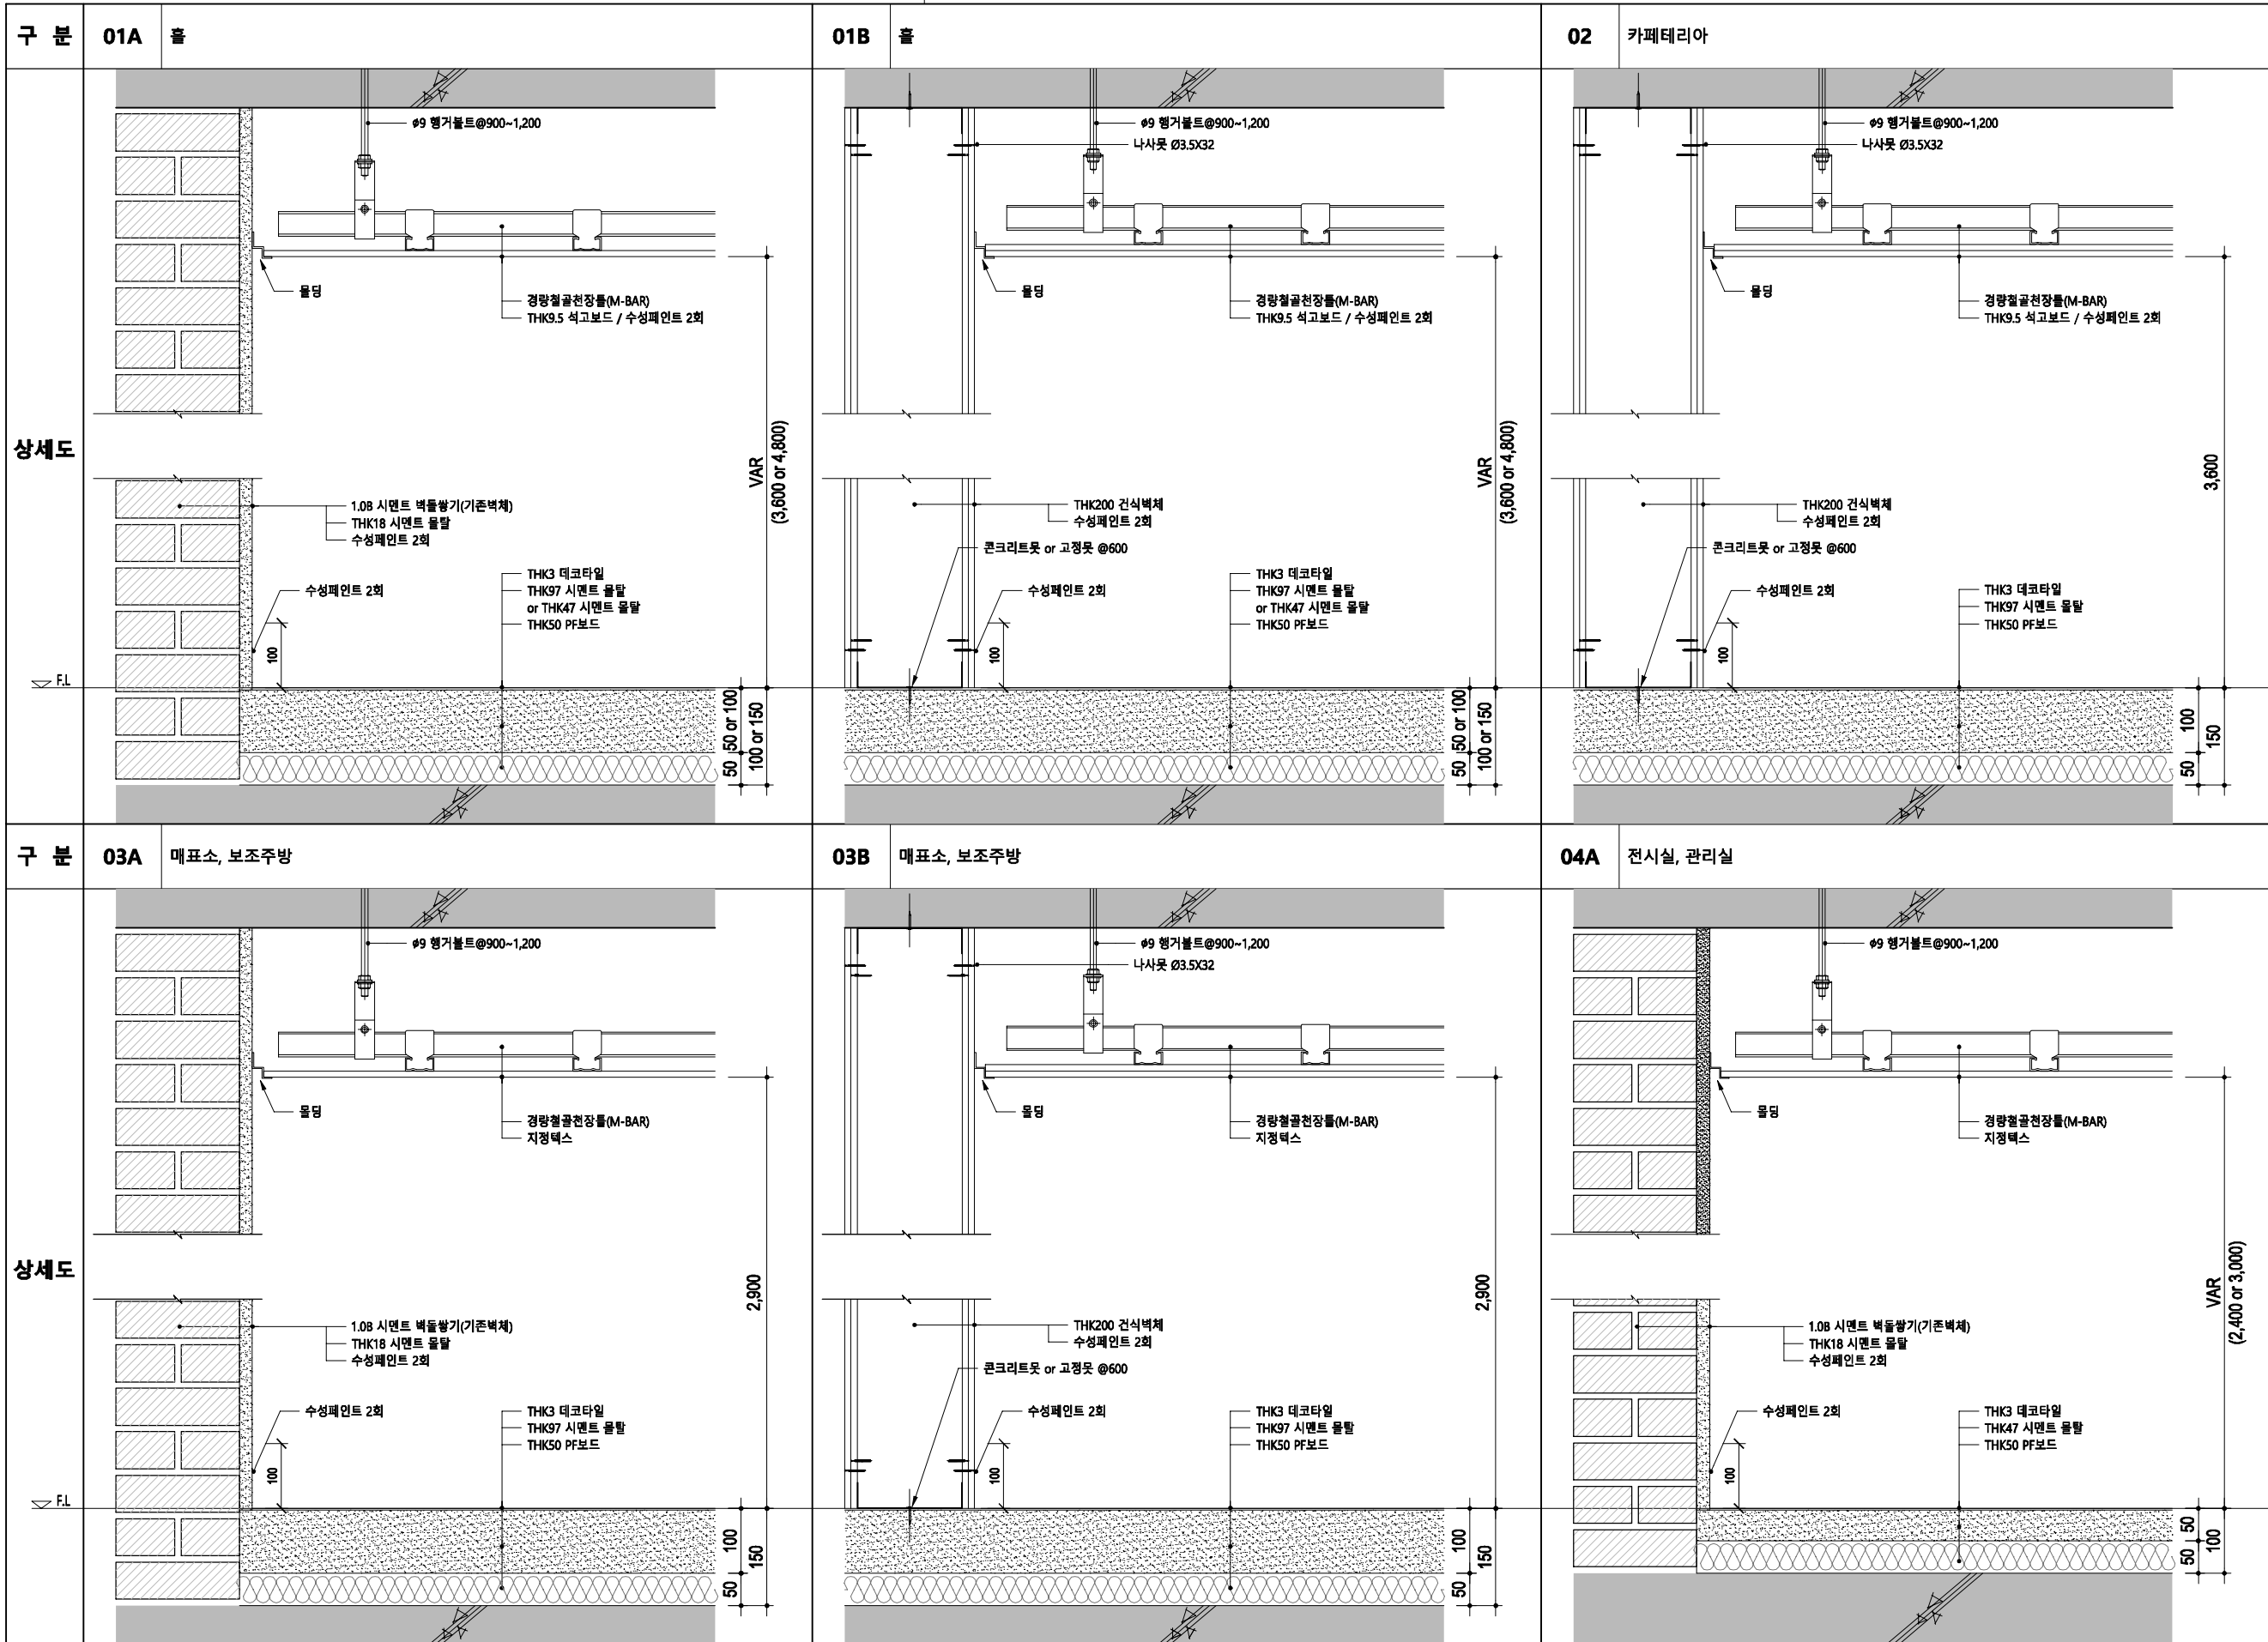

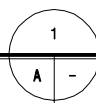

실내재료마감 상세도-2

축척 A1:1/5, A3:1/10

| 구 분 |  | 04B 전시실, 관리실 | 05 화장실 (남), 화장실 (여) | 06 PIT 점검실 |
|-----|--|--------------|---------------------|------------|
| 상세도 |  |              |                     |            |
|     |  |              |                     |            |
| 구 분 |  |              |                     |            |
| 상세도 |  |              |                     |            |
|     |  |              |                     |            |

PROJECT TITLE  
리틀 포레스트  
봉뜨락 조성사업

PROJECT NO

NOTE

KEY PLAN

DESIGN CORP.  
  
ADD. 대구광역시 동구 장동로 81, 5F  
TEL. 053.716.0776 FAX. 0505.720.0776  
E-mail. e-ul2020@naver.com  
Web. eul2020 / 0776

APPROVED BY  
대표이사 / 건축사 권오섭

CHECKED BY



DRAWN BY

DATE  
2023. 04.

DRAWING TITLE  
실내재료마감 상세도-2

SCALE  
A3 : 1/ 10

DRAWING NO.  
A01-023

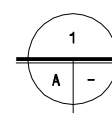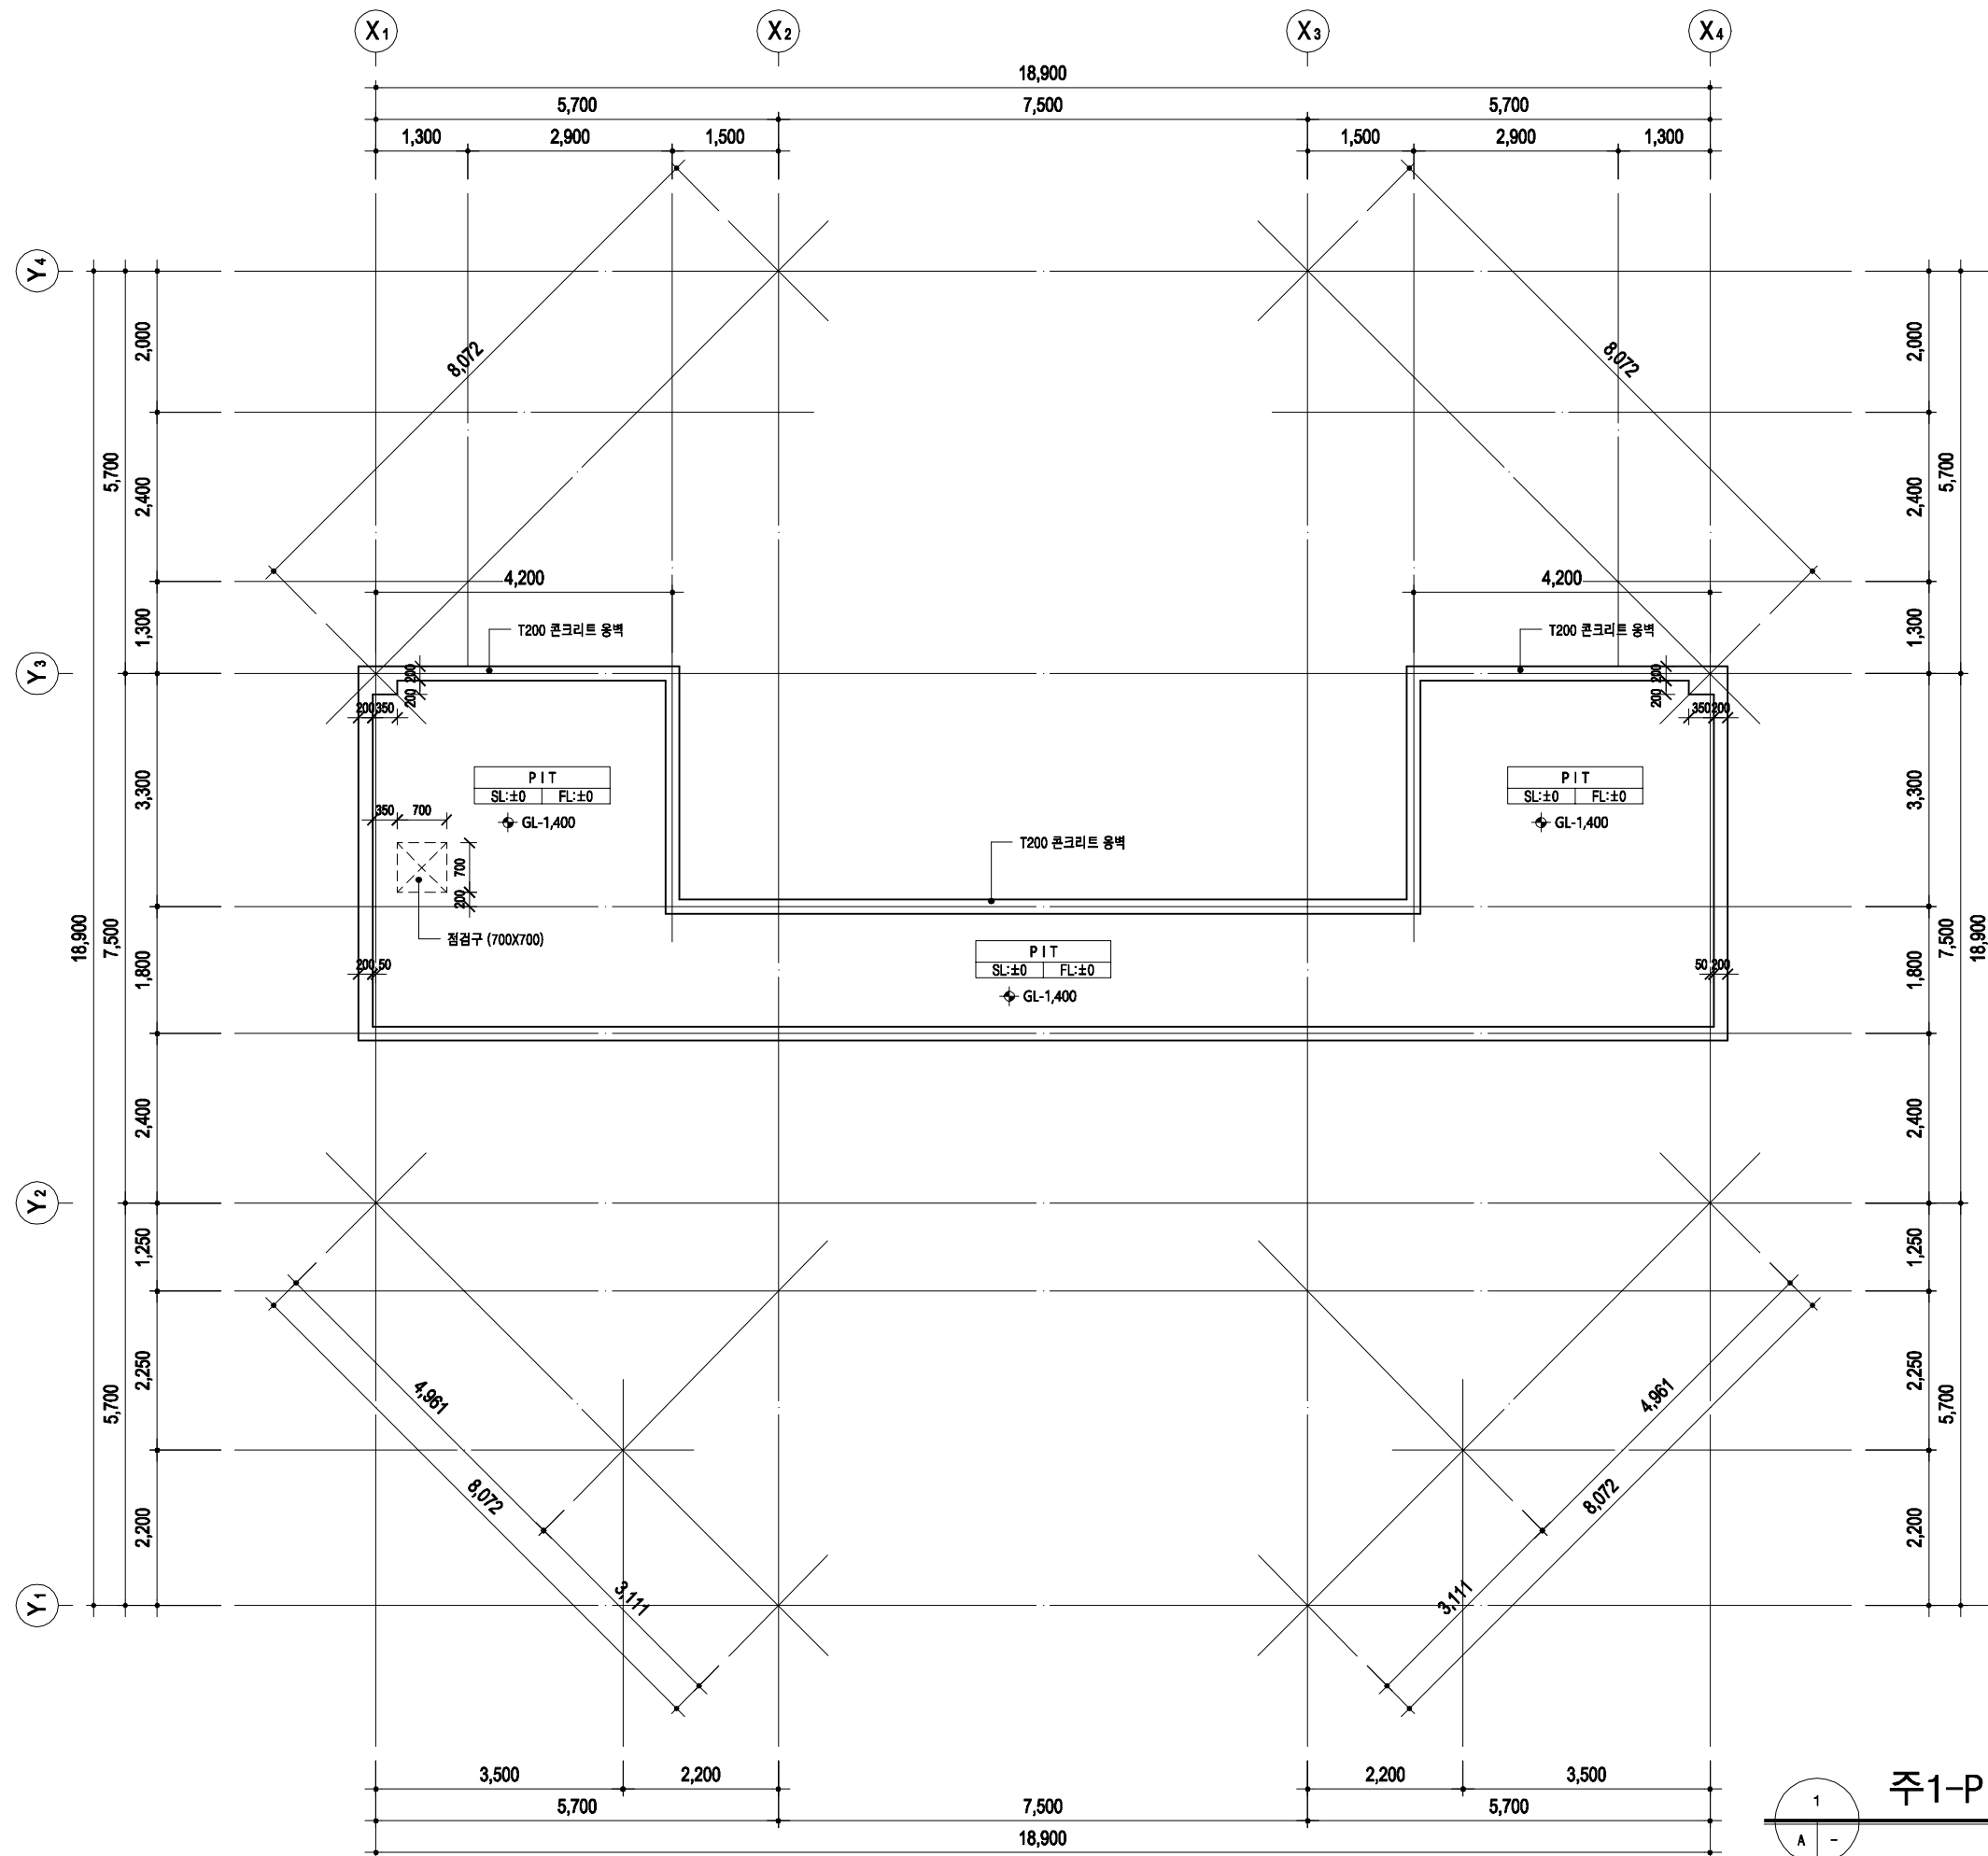

주1-PIT층 평면도(변경후)

축척 A1:1/50, A3:1/100

PROJECT TITLE  
리틀 포레스트  
봉뜨락 조성사업

PROJECT NO

NOTE

KEY PLAN

DESIGN CORP.  
 (주)아울건축사사무소  
ADD. 대구광역시 동구 장동로 81, 5F  
TEL. 053.716.0776 FAX. 0505.720.0776  
E-mail. e-ul2020@naver.com  
Web. eul2020 / 0776

APPROVED BY  
대표이사 / 건축사 권오섭

CHECKED BY

DRAWN BY



DATE  
2023. 04.

DRAWING TITLE  
주1-PIT층 평면도  
(변경후)

SCALE  
A3 : 1/ 100

DRAWING NO.  
A01-101



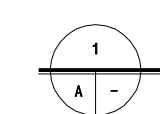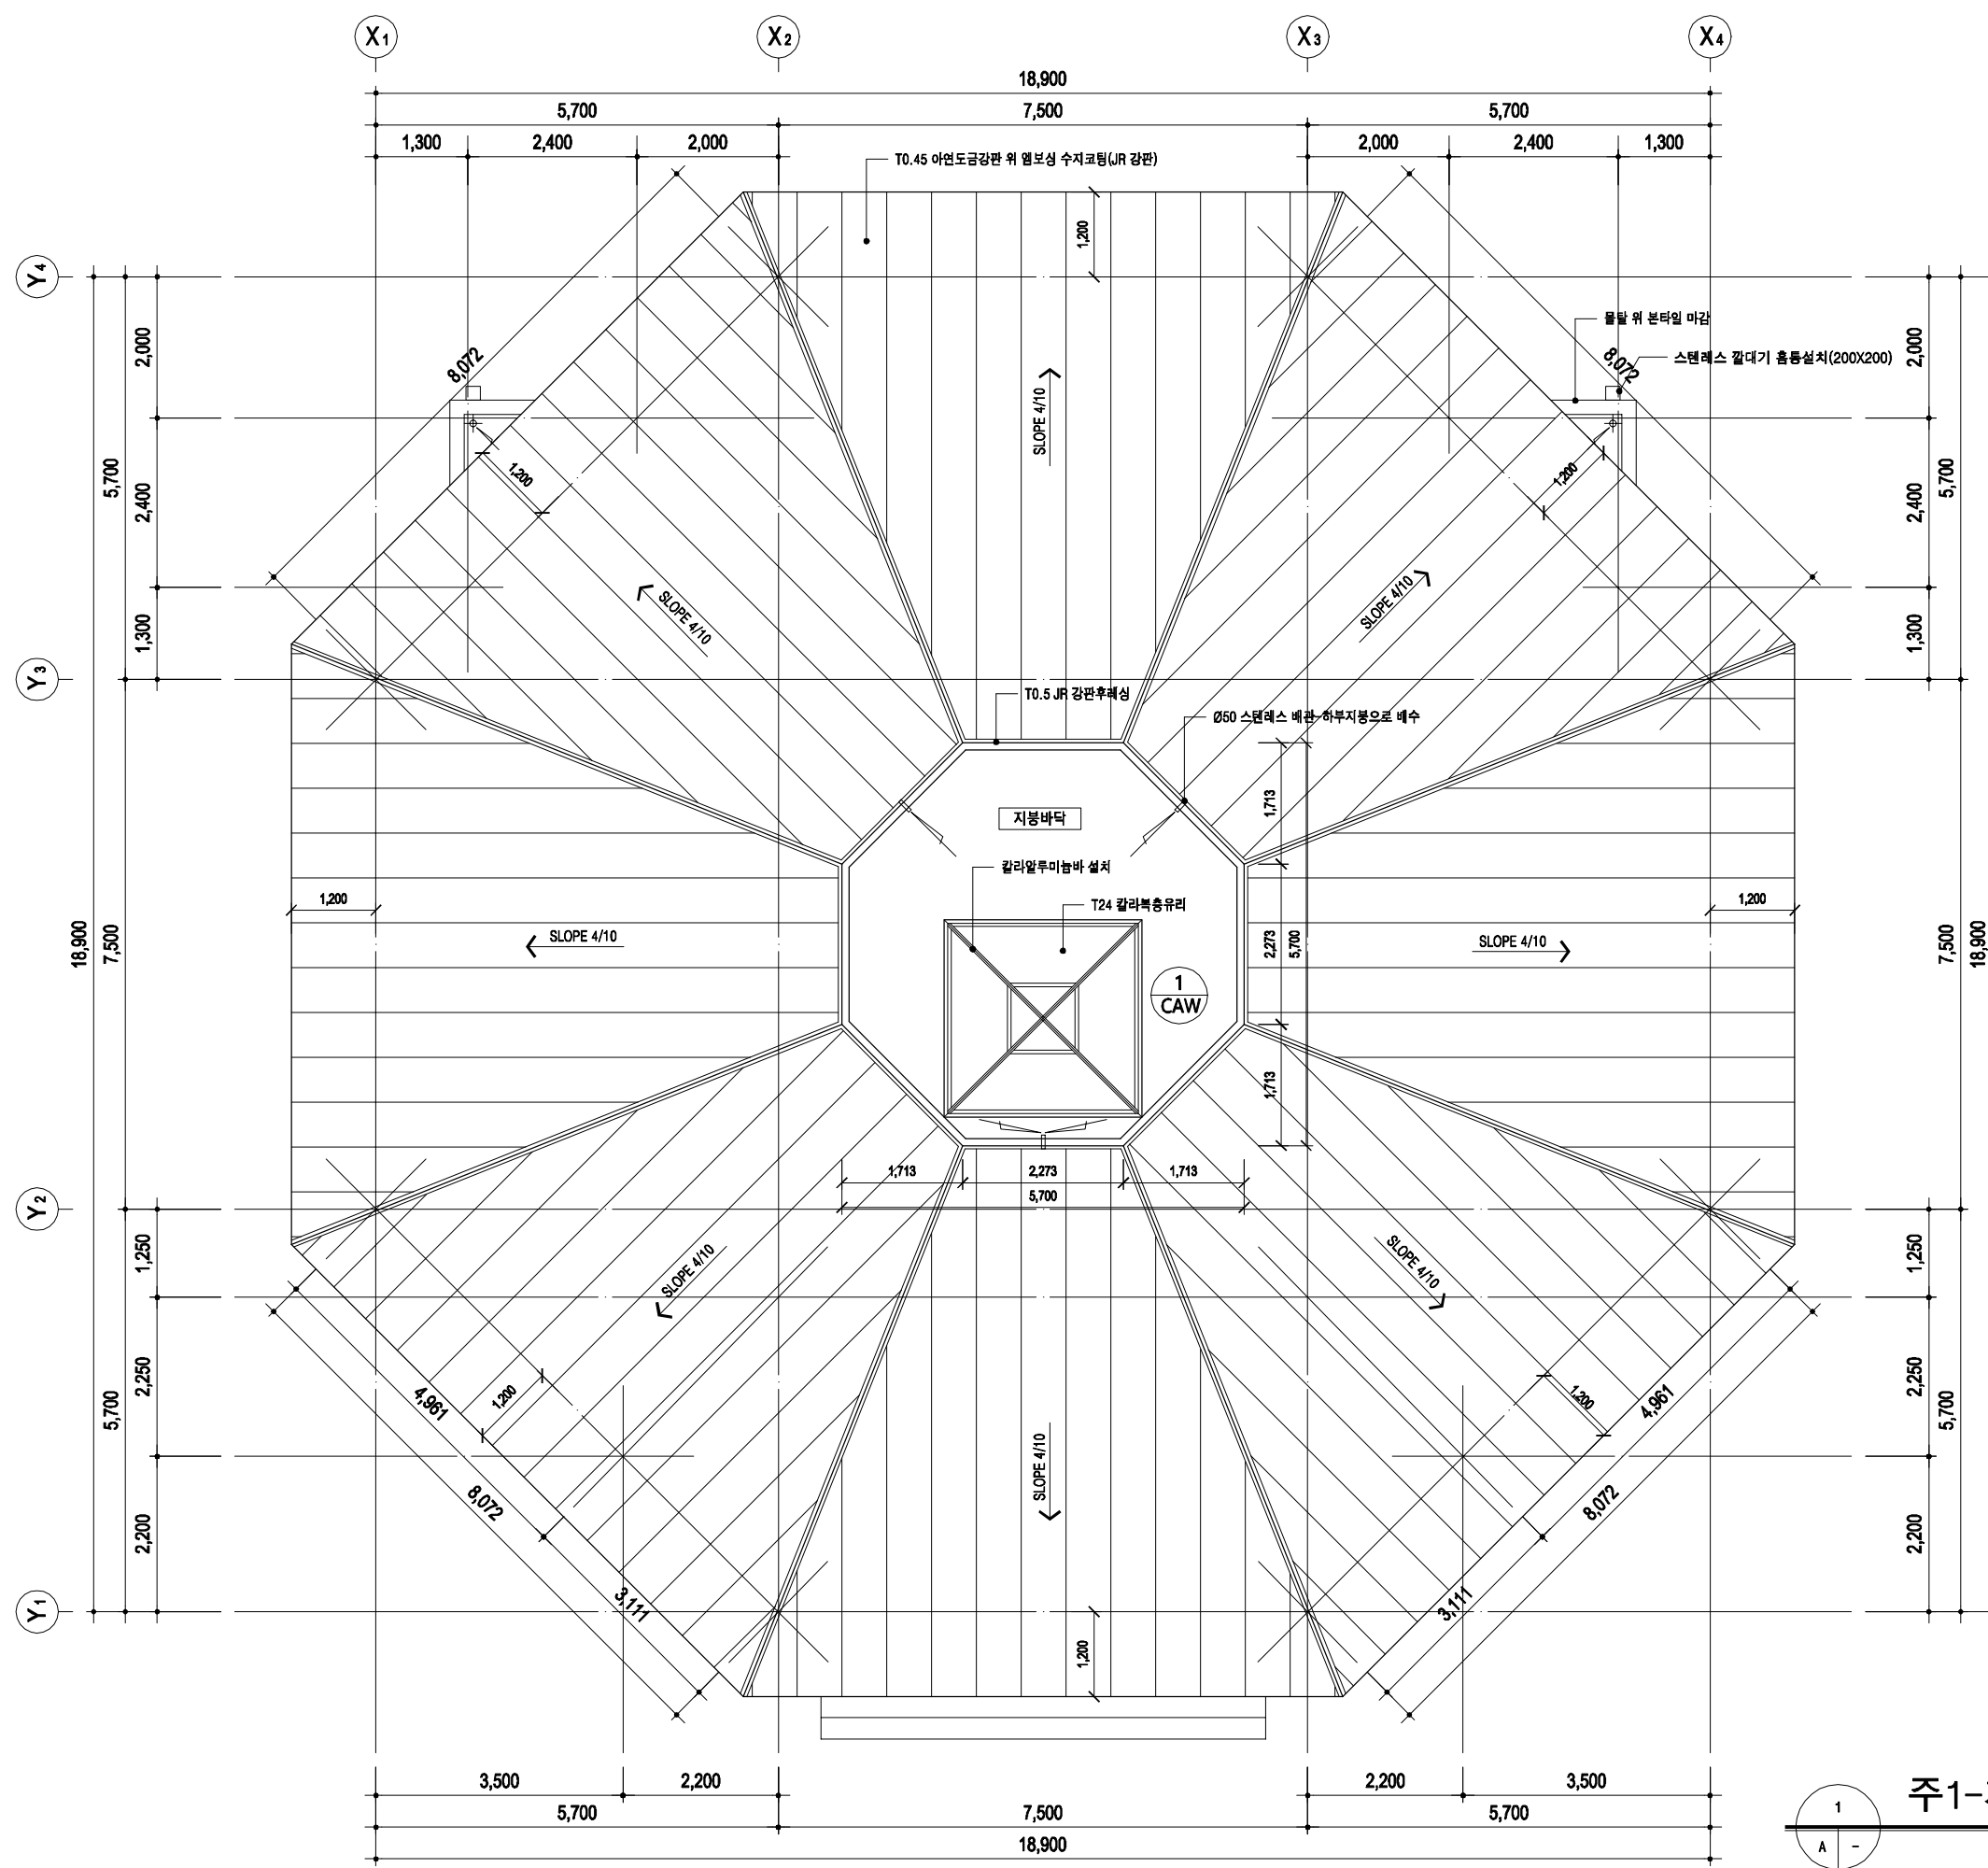

주1-지붕 평면도(변경후)

축척 A1:1/50, A3:1/100

|               |   |
|---------------|---|
| PROJECT TITLE | 리틀 포레스트<br>봉뜨락 조성사업   |
| PROJECT NO    |   |
| NOTE          |   |
| KEY PLAN      |   |
| DESIGN CORP.  | <b>아이음</b> (주) 아이음건축사사무소<br>ADD. 대구광역시 동구 장동로 81, 5F<br>TEL. 053.716.0776 FAX. 0505.720.0776<br>E-mail. e-ul2020@naver.com<br>Web. eul2020 / 0776 |
| APPROVED BY   | 대표이사 / 건축사 권오섭   |
| CHECKED BY    |   |
| DRAWN BY      |   |
| DATE          | 2023. 04.   |
| DRAWING TITLE | 주1-지붕 평면도<br>(변경후)   |
| SCALE         | A3 : 1/ 100   |
| DRAWING NO.   | A01-103   |

PROJECT TITLE

리틀 포레스트  
봉뜨락 조성사업

PROJECT NO

NOTE

KEY PLAN

DESIGN CORP.

**OHM** (주)아름건축사사무소

ADD. 대구광역시 동구 장동로 81, 5F  
TEL. 053.716.0776 FAX. 0505.720.0776  
E-mail. e-ul2020@naver.com  
Web. eul2020 / 0776

APPROVED BY  
대표이사 / 건축사 권오섭

CHECKED BY



DRAWN BY

DATE  
2023. 04.

DRAWING TITLE  
주1-정면도  
(변경후)

SCALE  
A3 : 1/ 100

DRAWING NO.  
A01-201

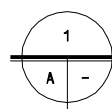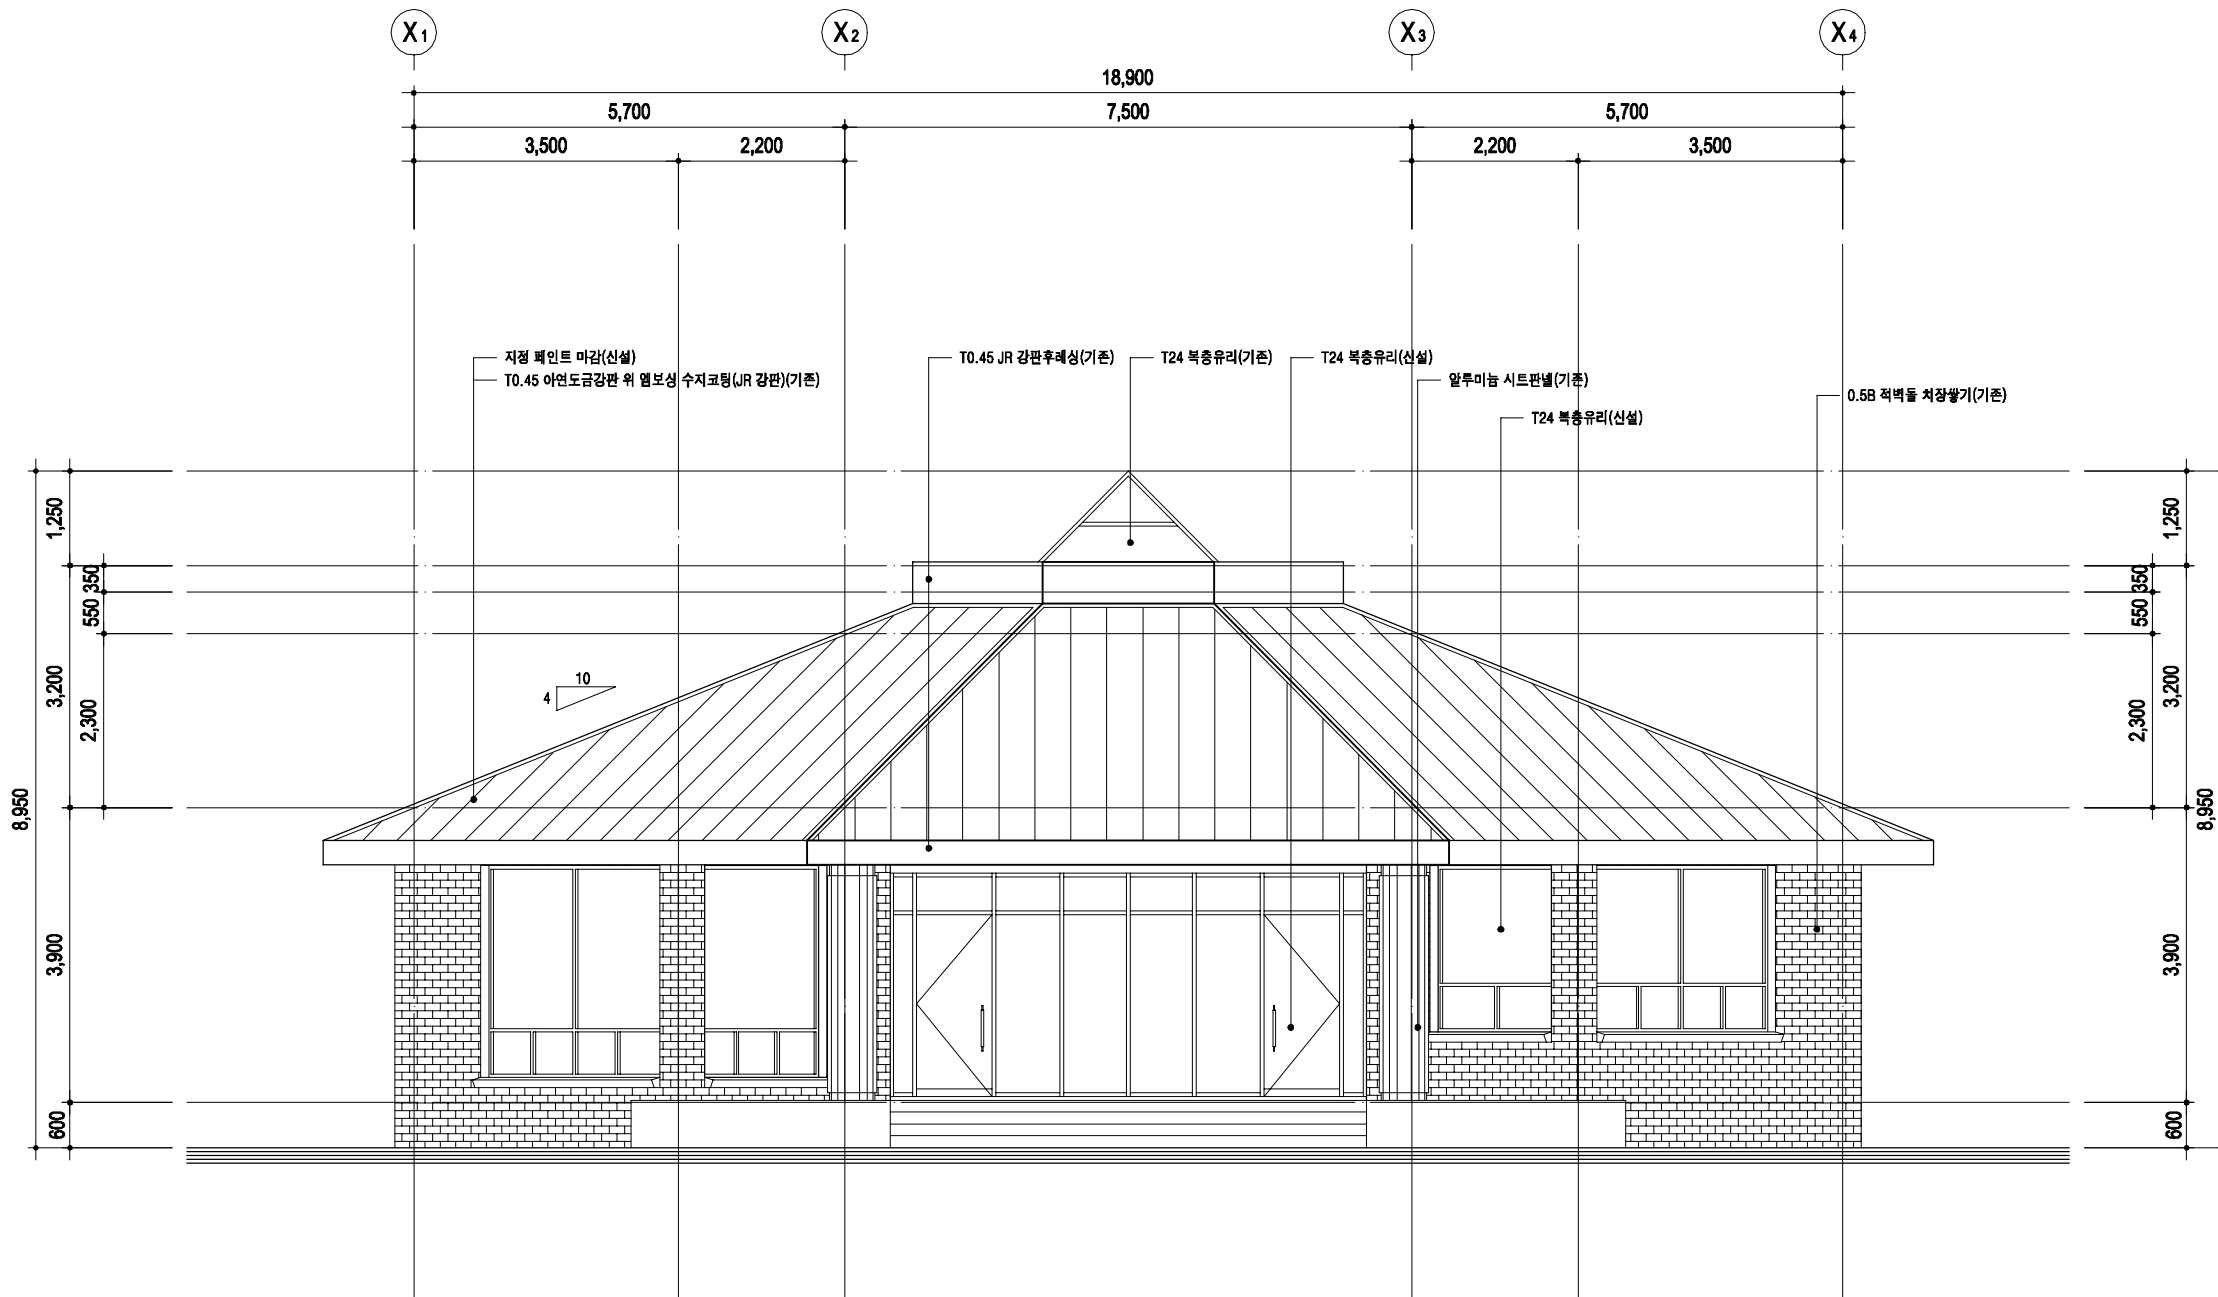

주1-정면도(변경후)

축척 A1:1/50, A3:1/100

PROJECT TITLE

리틀 포레스트  
봉뜨락 조성사업

PROJECT NO

NOTE

KEY PLAN

DESIGN CORP.

**OHM** (주)아름건축사사무소

ADD. 대구광역시 동구 장동로 81, 5F  
TEL. 053.716.0776 FAX. 0505.720.0776  
E-mail. e-ul2020@naver.com  
Web. eul2020 / 0776

APPROVED BY  
대표이사 / 건축사 권오섭

CHECKED BY


DRAWN BY

DATE  
2023. 04.

DRAWING TITLE  
주1-배면도  
(변경후)

SCALE  
A3 : 1/ 100

DRAWING NO.  
A01-202

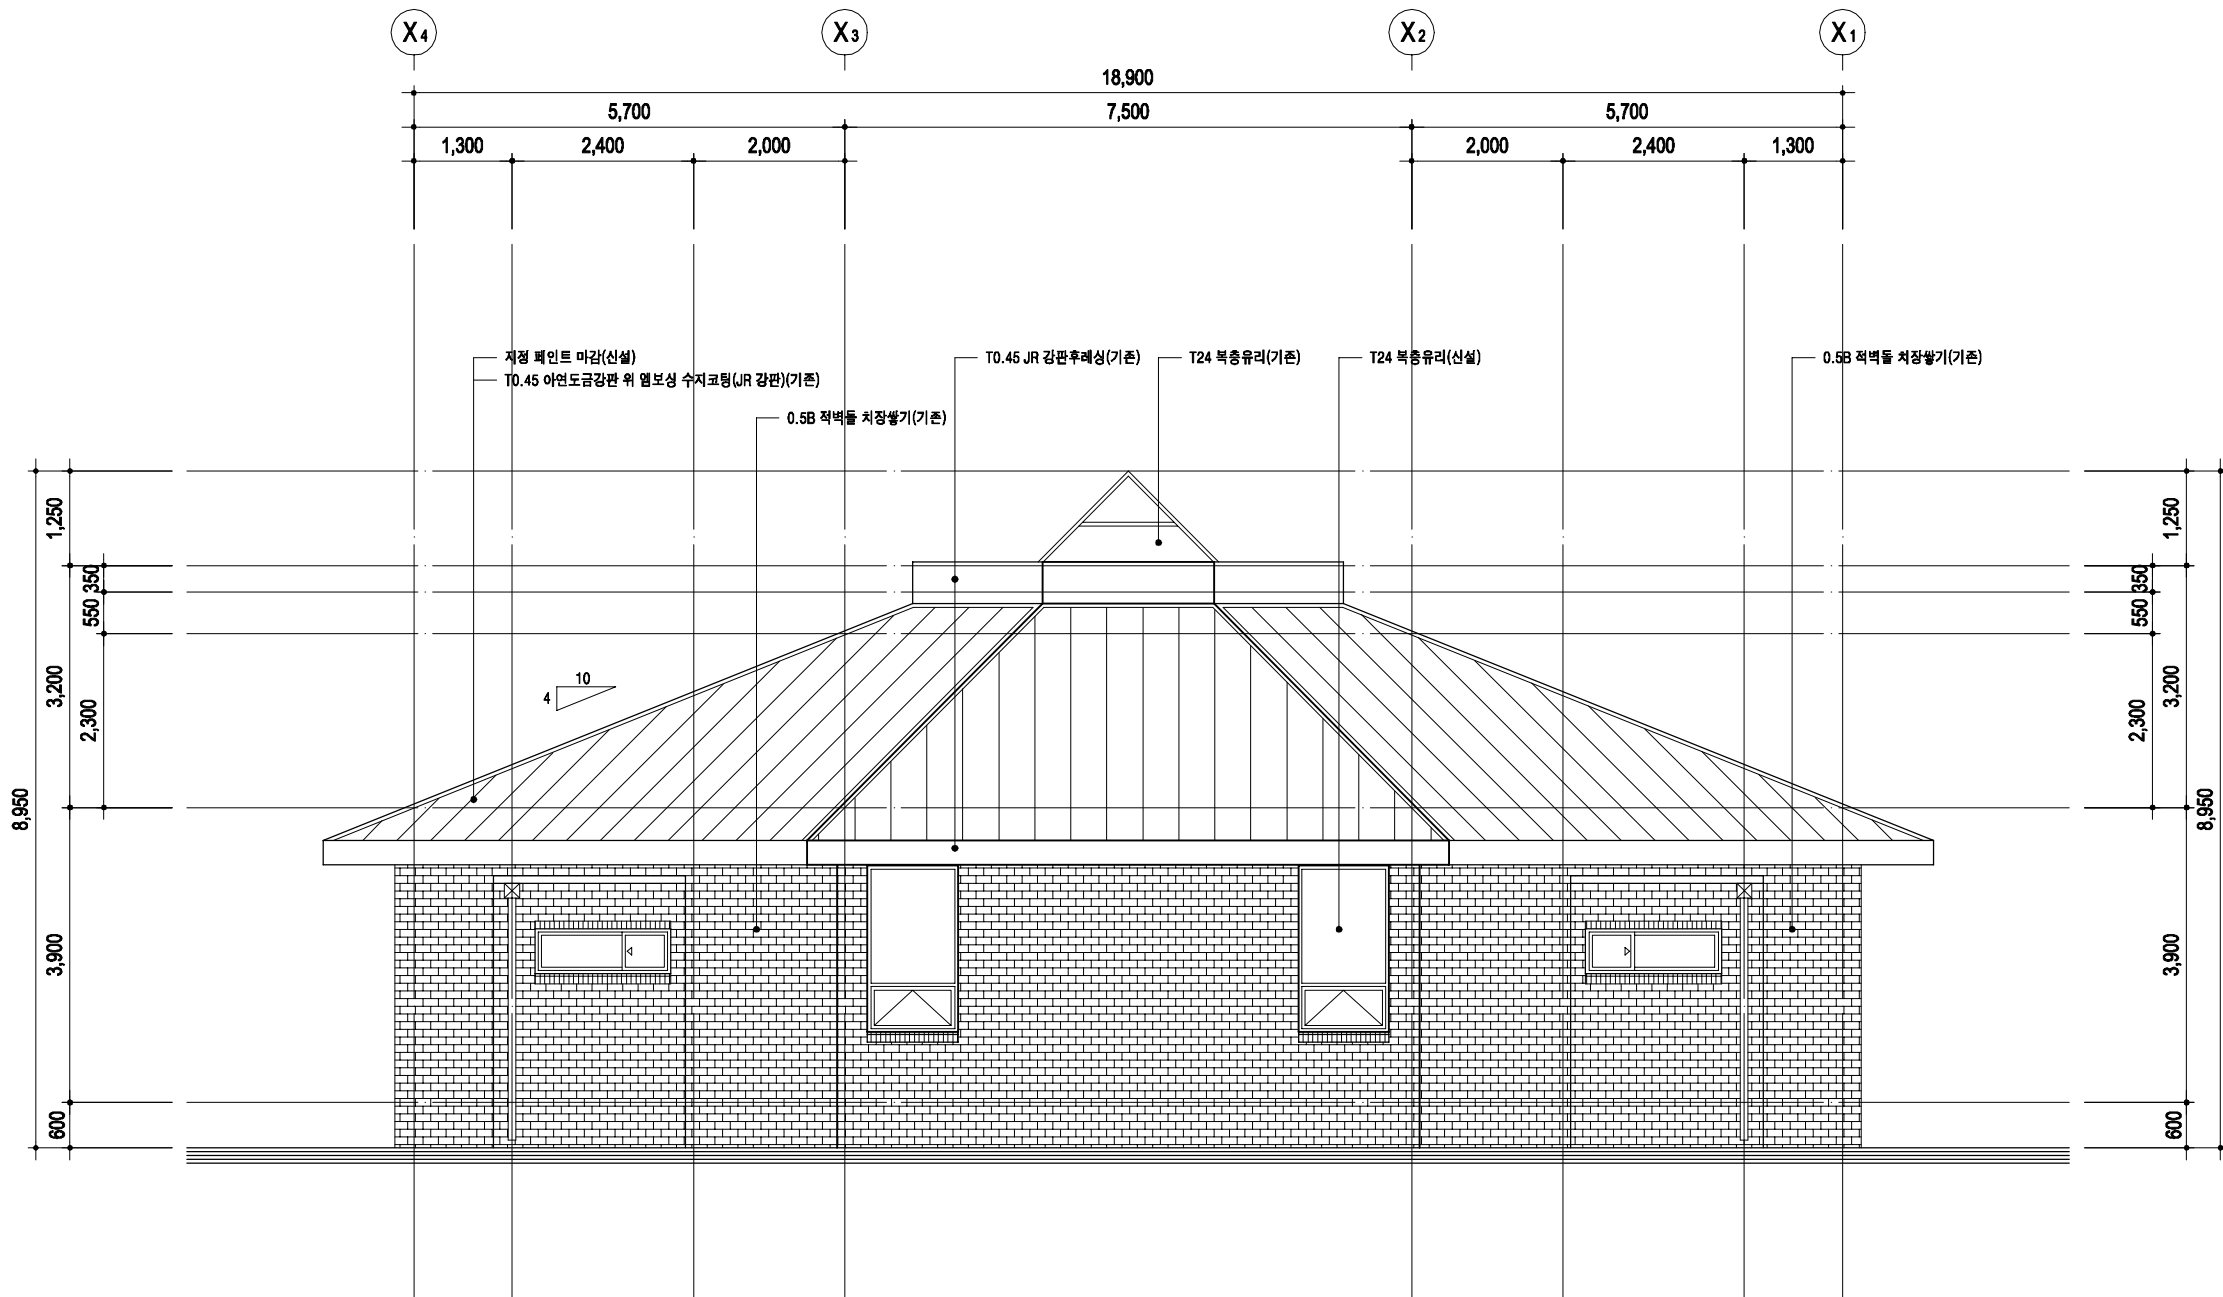

주1-배 면 도(변경후)

축척 A1:1/50, A3:1/100

PROJECT TITLE

리틀 포레스트  
봉뜨락 조성사업

PROJECT NO

NOTE

KEY PLAN

DESIGN CORP.

**아이음** (주) 아이음건축사사무소

ADD. 대구광역시 동구 장동로 81, 5F  
TEL. 053.716.0776 FAX. 0505.720.0776  
E-mail. e-ul2020@naver.com  
Web. eul2020 / 0776

APPROVED BY  
대표이사 / 건축사 권오섭

CHECKED BY



DRAWN BY

DATE  
2023. 04.

DRAWING TITLE  
주1-우측면도 (변경후)

SCALE  
A3 : 1/ 100

DRAWING NO.  
A01-203

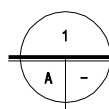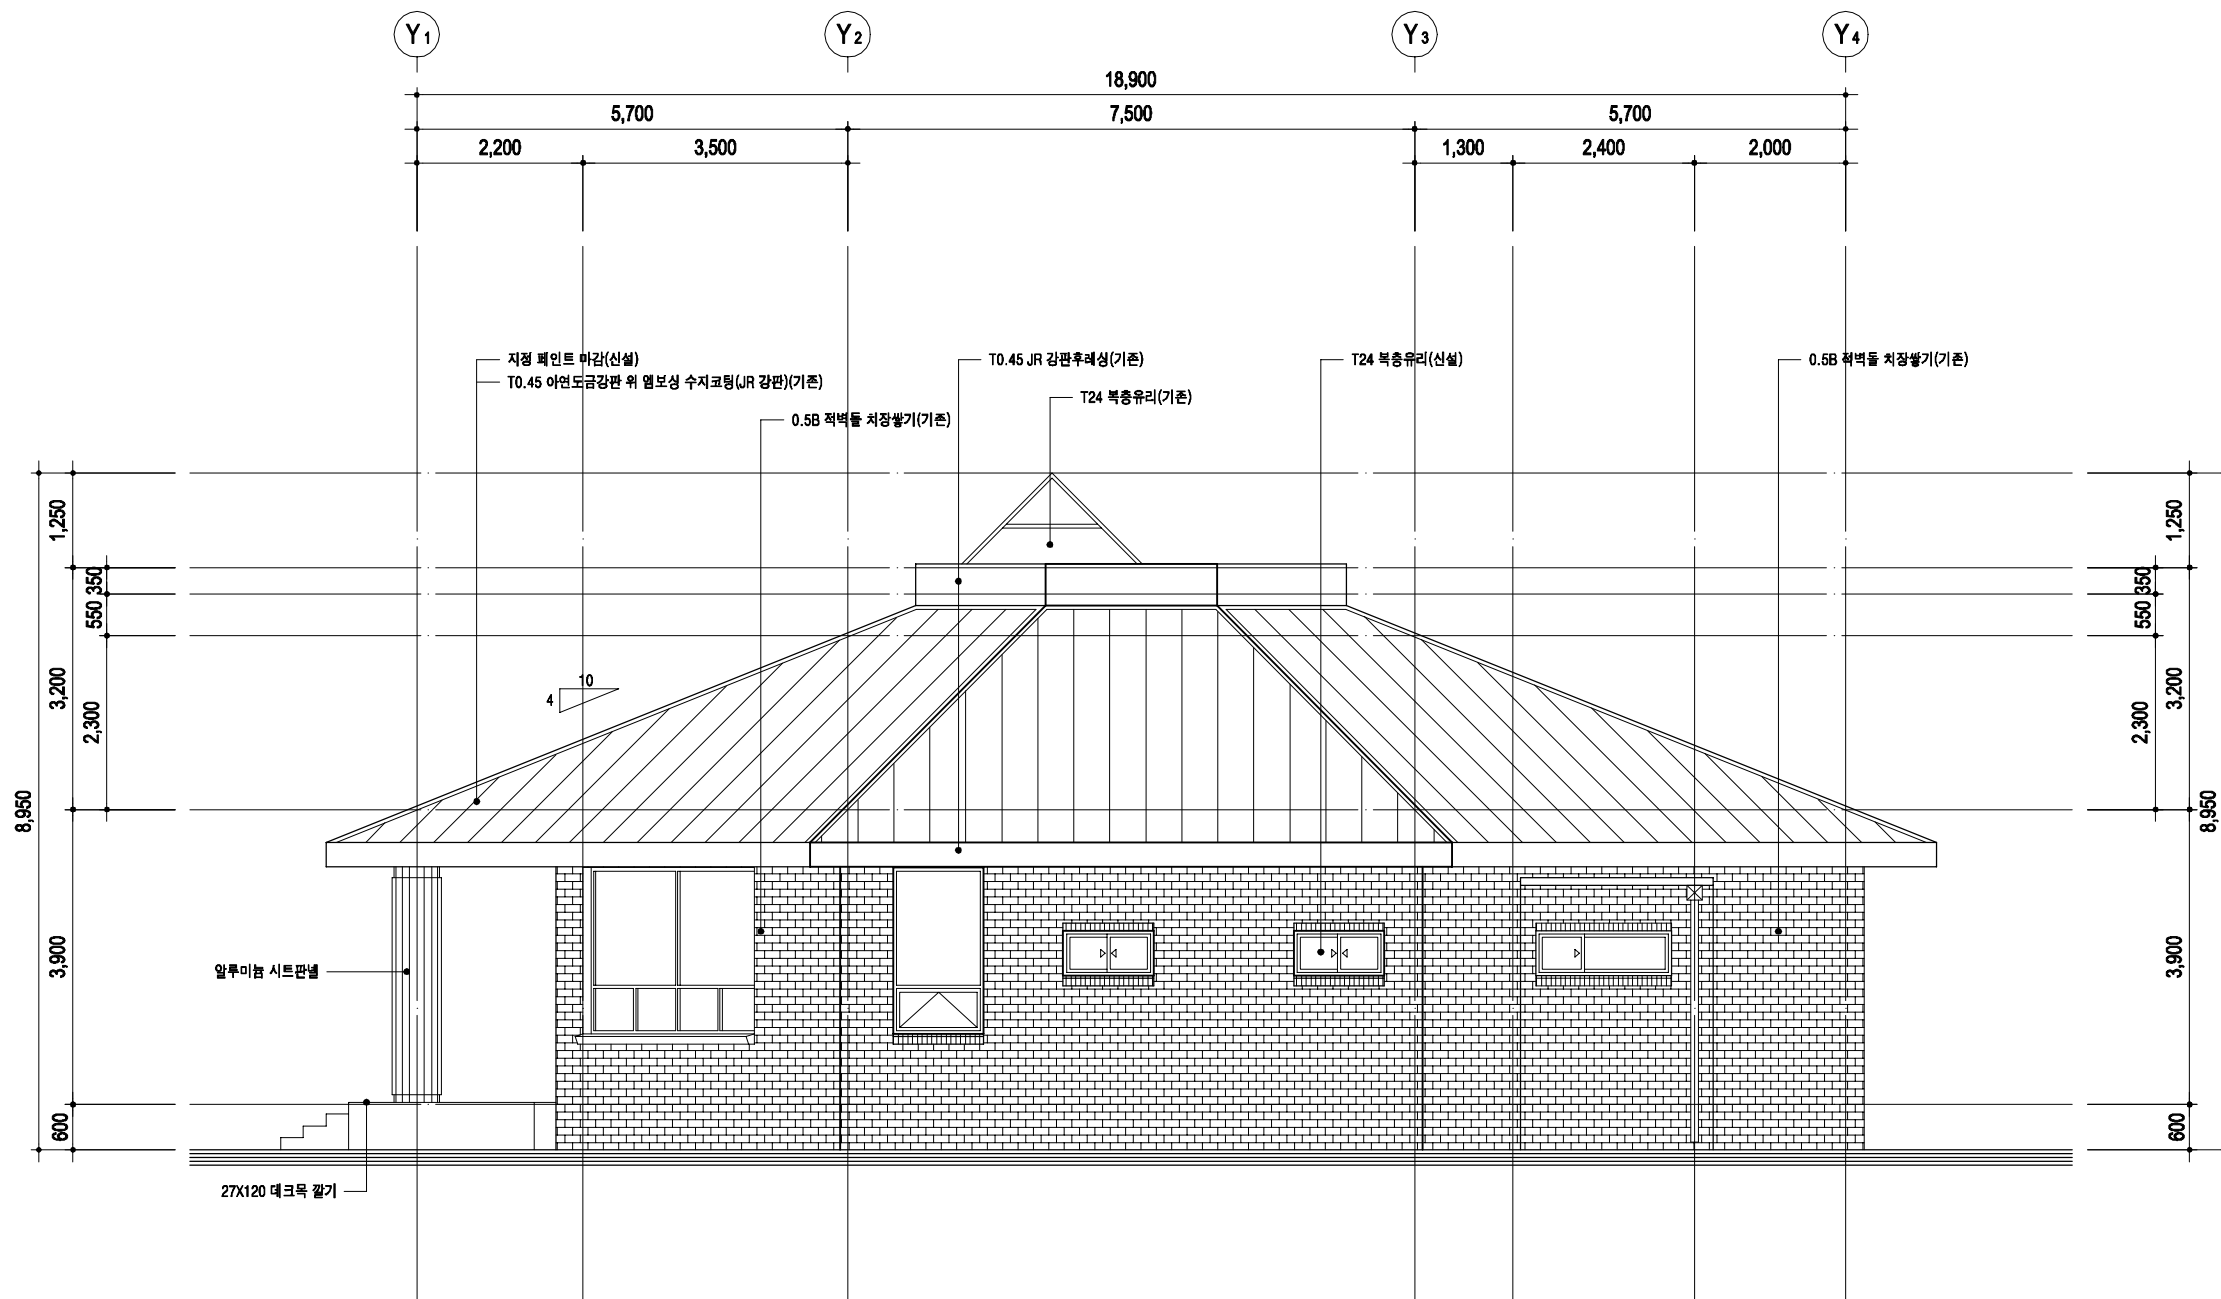

주1-우측면도(변경후)

축척 A1:1/50, A3:1/100

PROJECT TITLE

리틀 포레스트  
봉뜨락 조성사업

PROJECT NO

NOTE

KEY PLAN

DESIGN CORP.

**에이엘** (주)아을건축사사무소

ADD. 대구광역시 동구 장동로 81, 5F  
TEL. 053.716.0776 FAX. 0505.720.0776  
E-mail. e-ul2020@naver.com  
Web. eul2020 / 0776

APPROVED BY  
대표이사 / 건축사 권오섭

CHECKED BY



DRAWN BY

DATE  
2023. 04.

DRAWING TITLE  
주1-좌측면도  
(변경후)

SCALE  
A3 : 1/ 100


DRAWING NO.  
A01-204

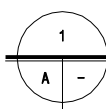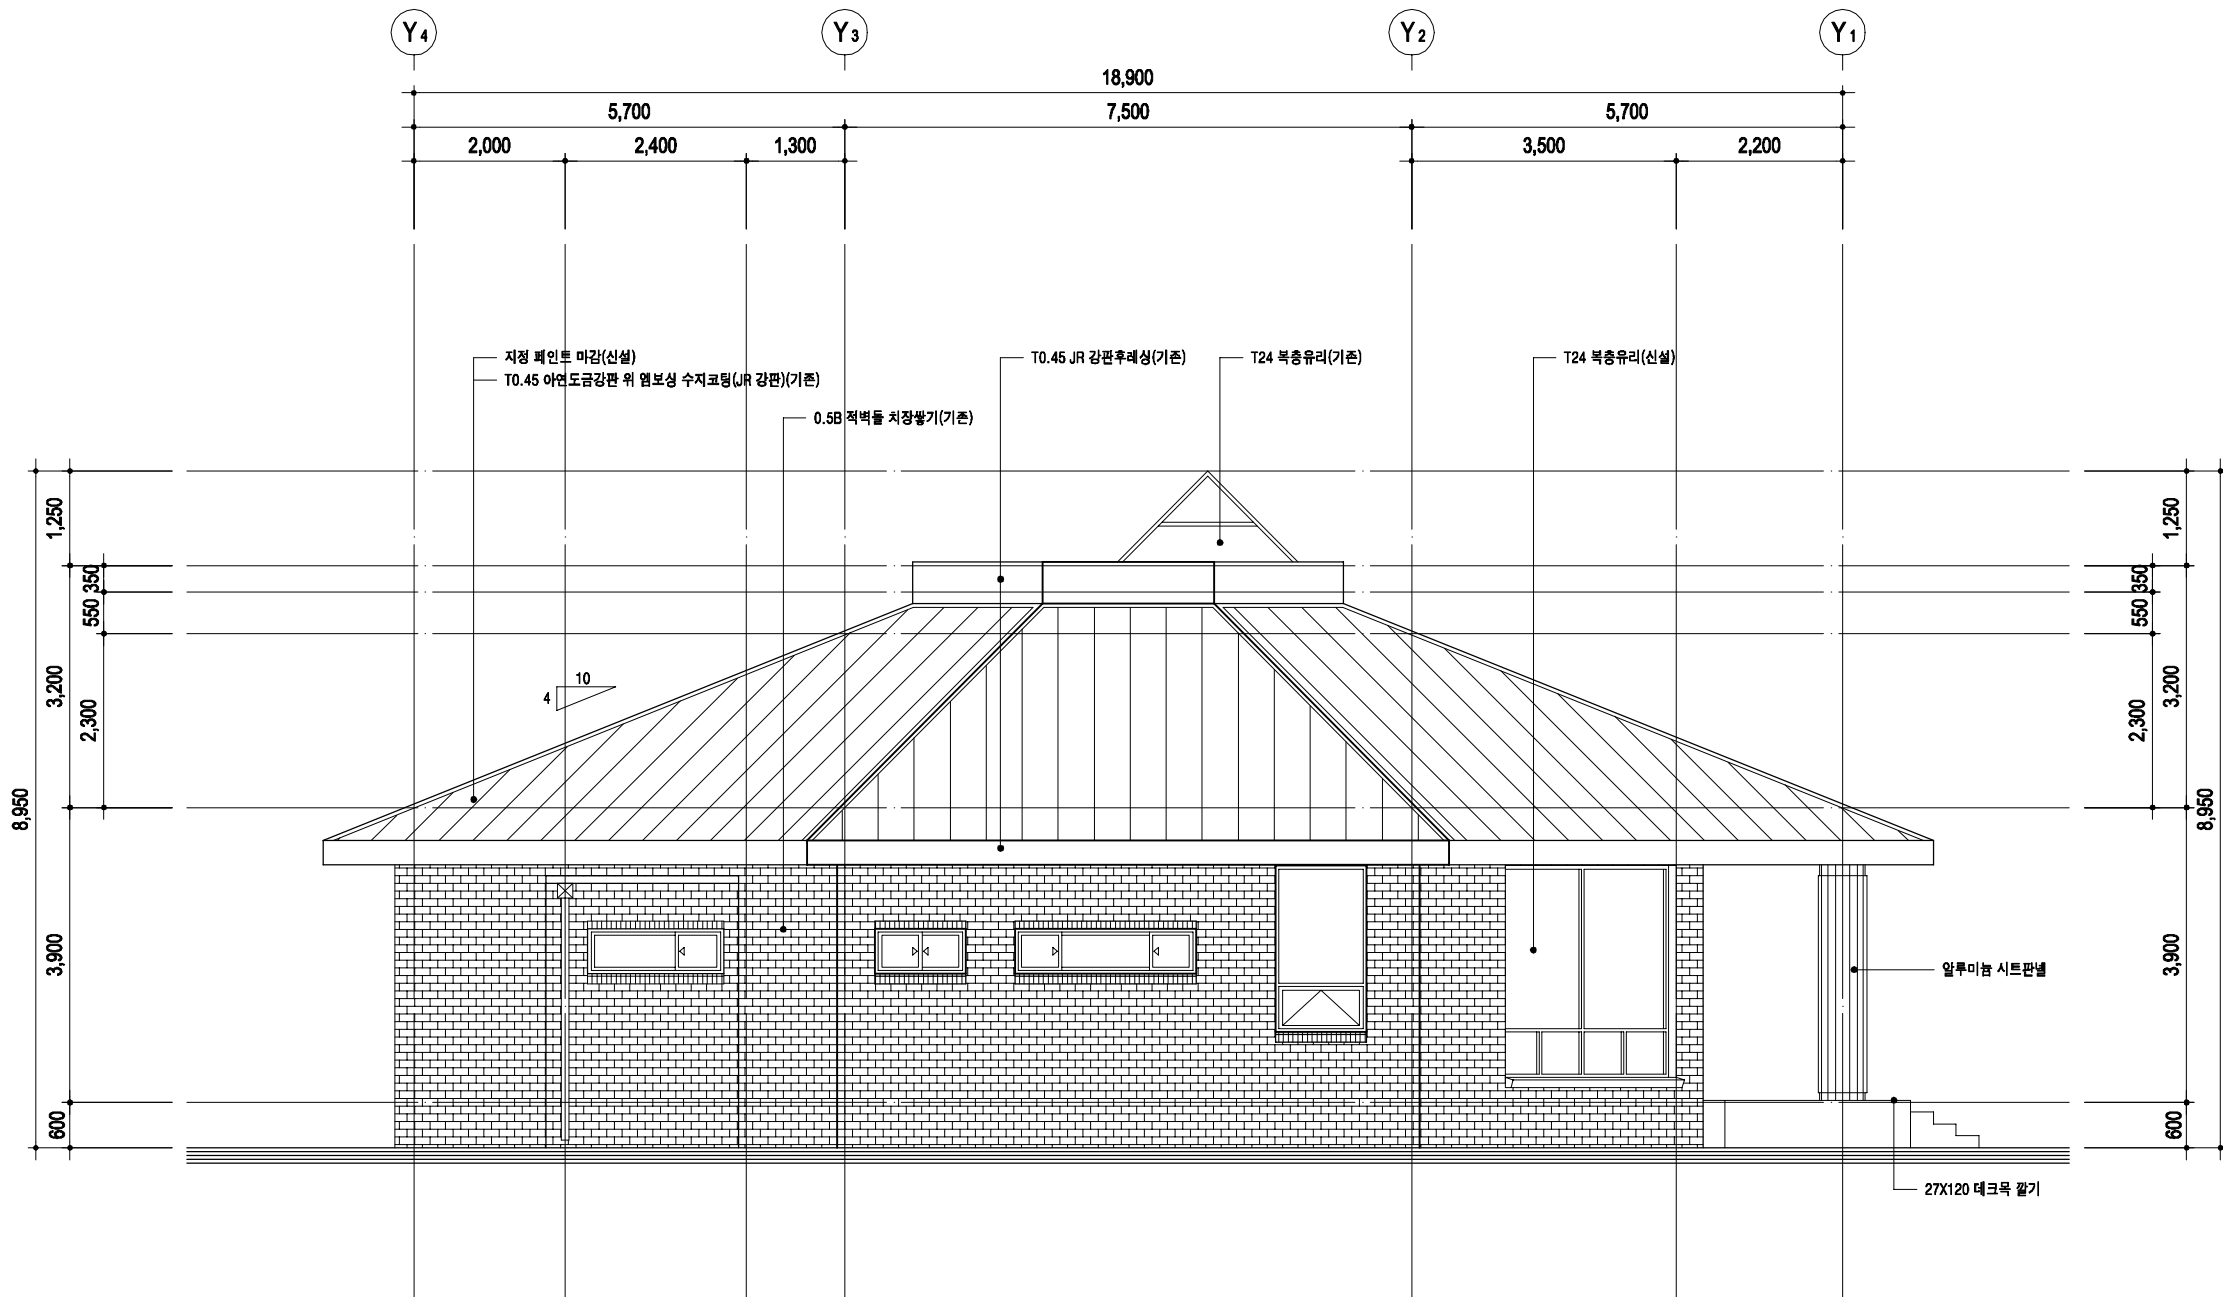

주1-좌 측 면 도(변경후)

축척 A1:1/50, A3:1/100

1. 단열기준(중부1지역) 이하로 할 것.  
- 바닥: 0.240(W/㎡.K)이하 (외기단열)  
- 벽 : 0.170(W/㎡.K)이하 (외기단열)  
- 지붕: 0.150(W/㎡.K)이하 (외기단열)  
\* 형질성능 내역 참고 할 것.


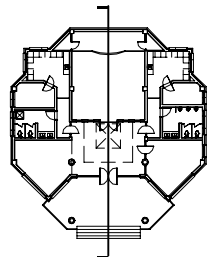


2023. 04.

주1-종단면도  
(변경후)

A3 : 1/ 80


A01-301

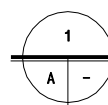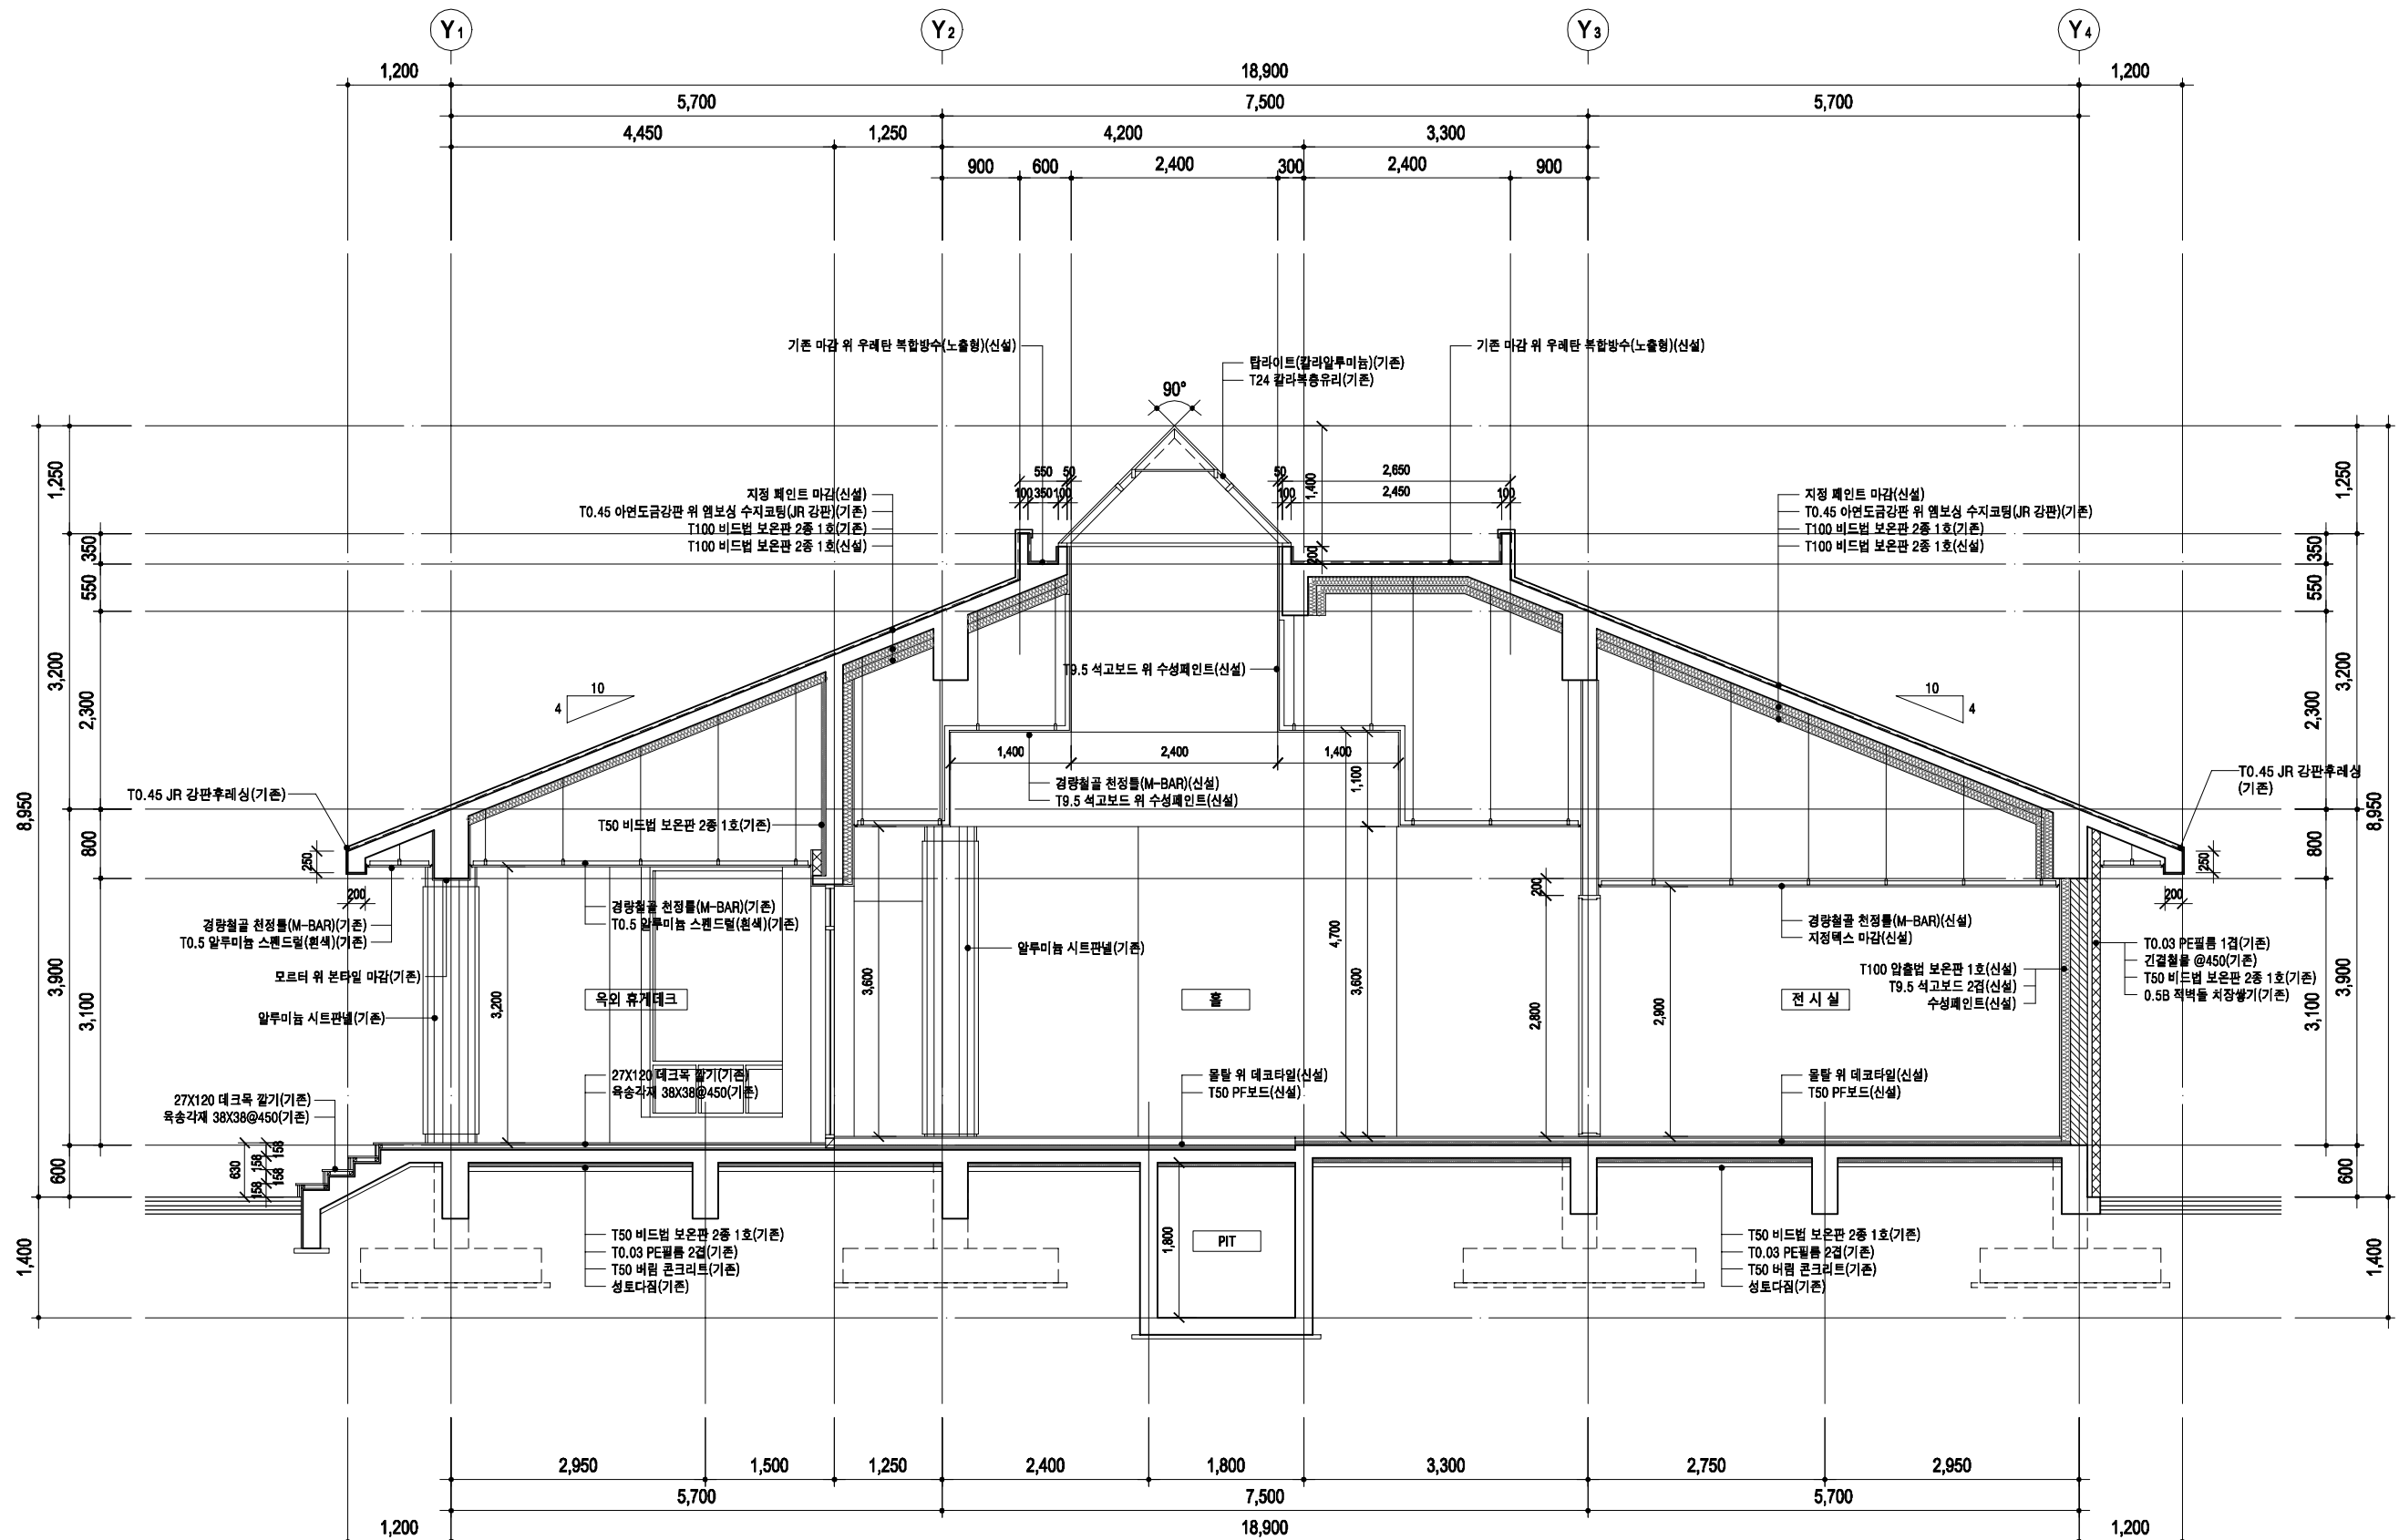

주1-종 단 면 도(변경후)

축척 A1:1/40, A3:1/80

1. 단열기준(중부1지역) 이하로 할 것.  
- 바닥: 0.240(W/㎡.K)이하 (외기단열)  
- 벽 : 0.170(W/㎡.K)이하 (외기단열)  
- 지붕: 0.150(W/㎡.K)이하 (외기단열)  
\* 형질성능 내역 참고 할 것.


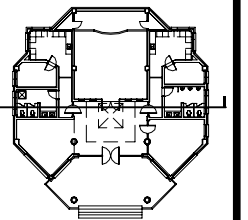


2023. 04.

주1-횡단면도(변경후)




A3 : 1/ 80

A01- 302

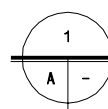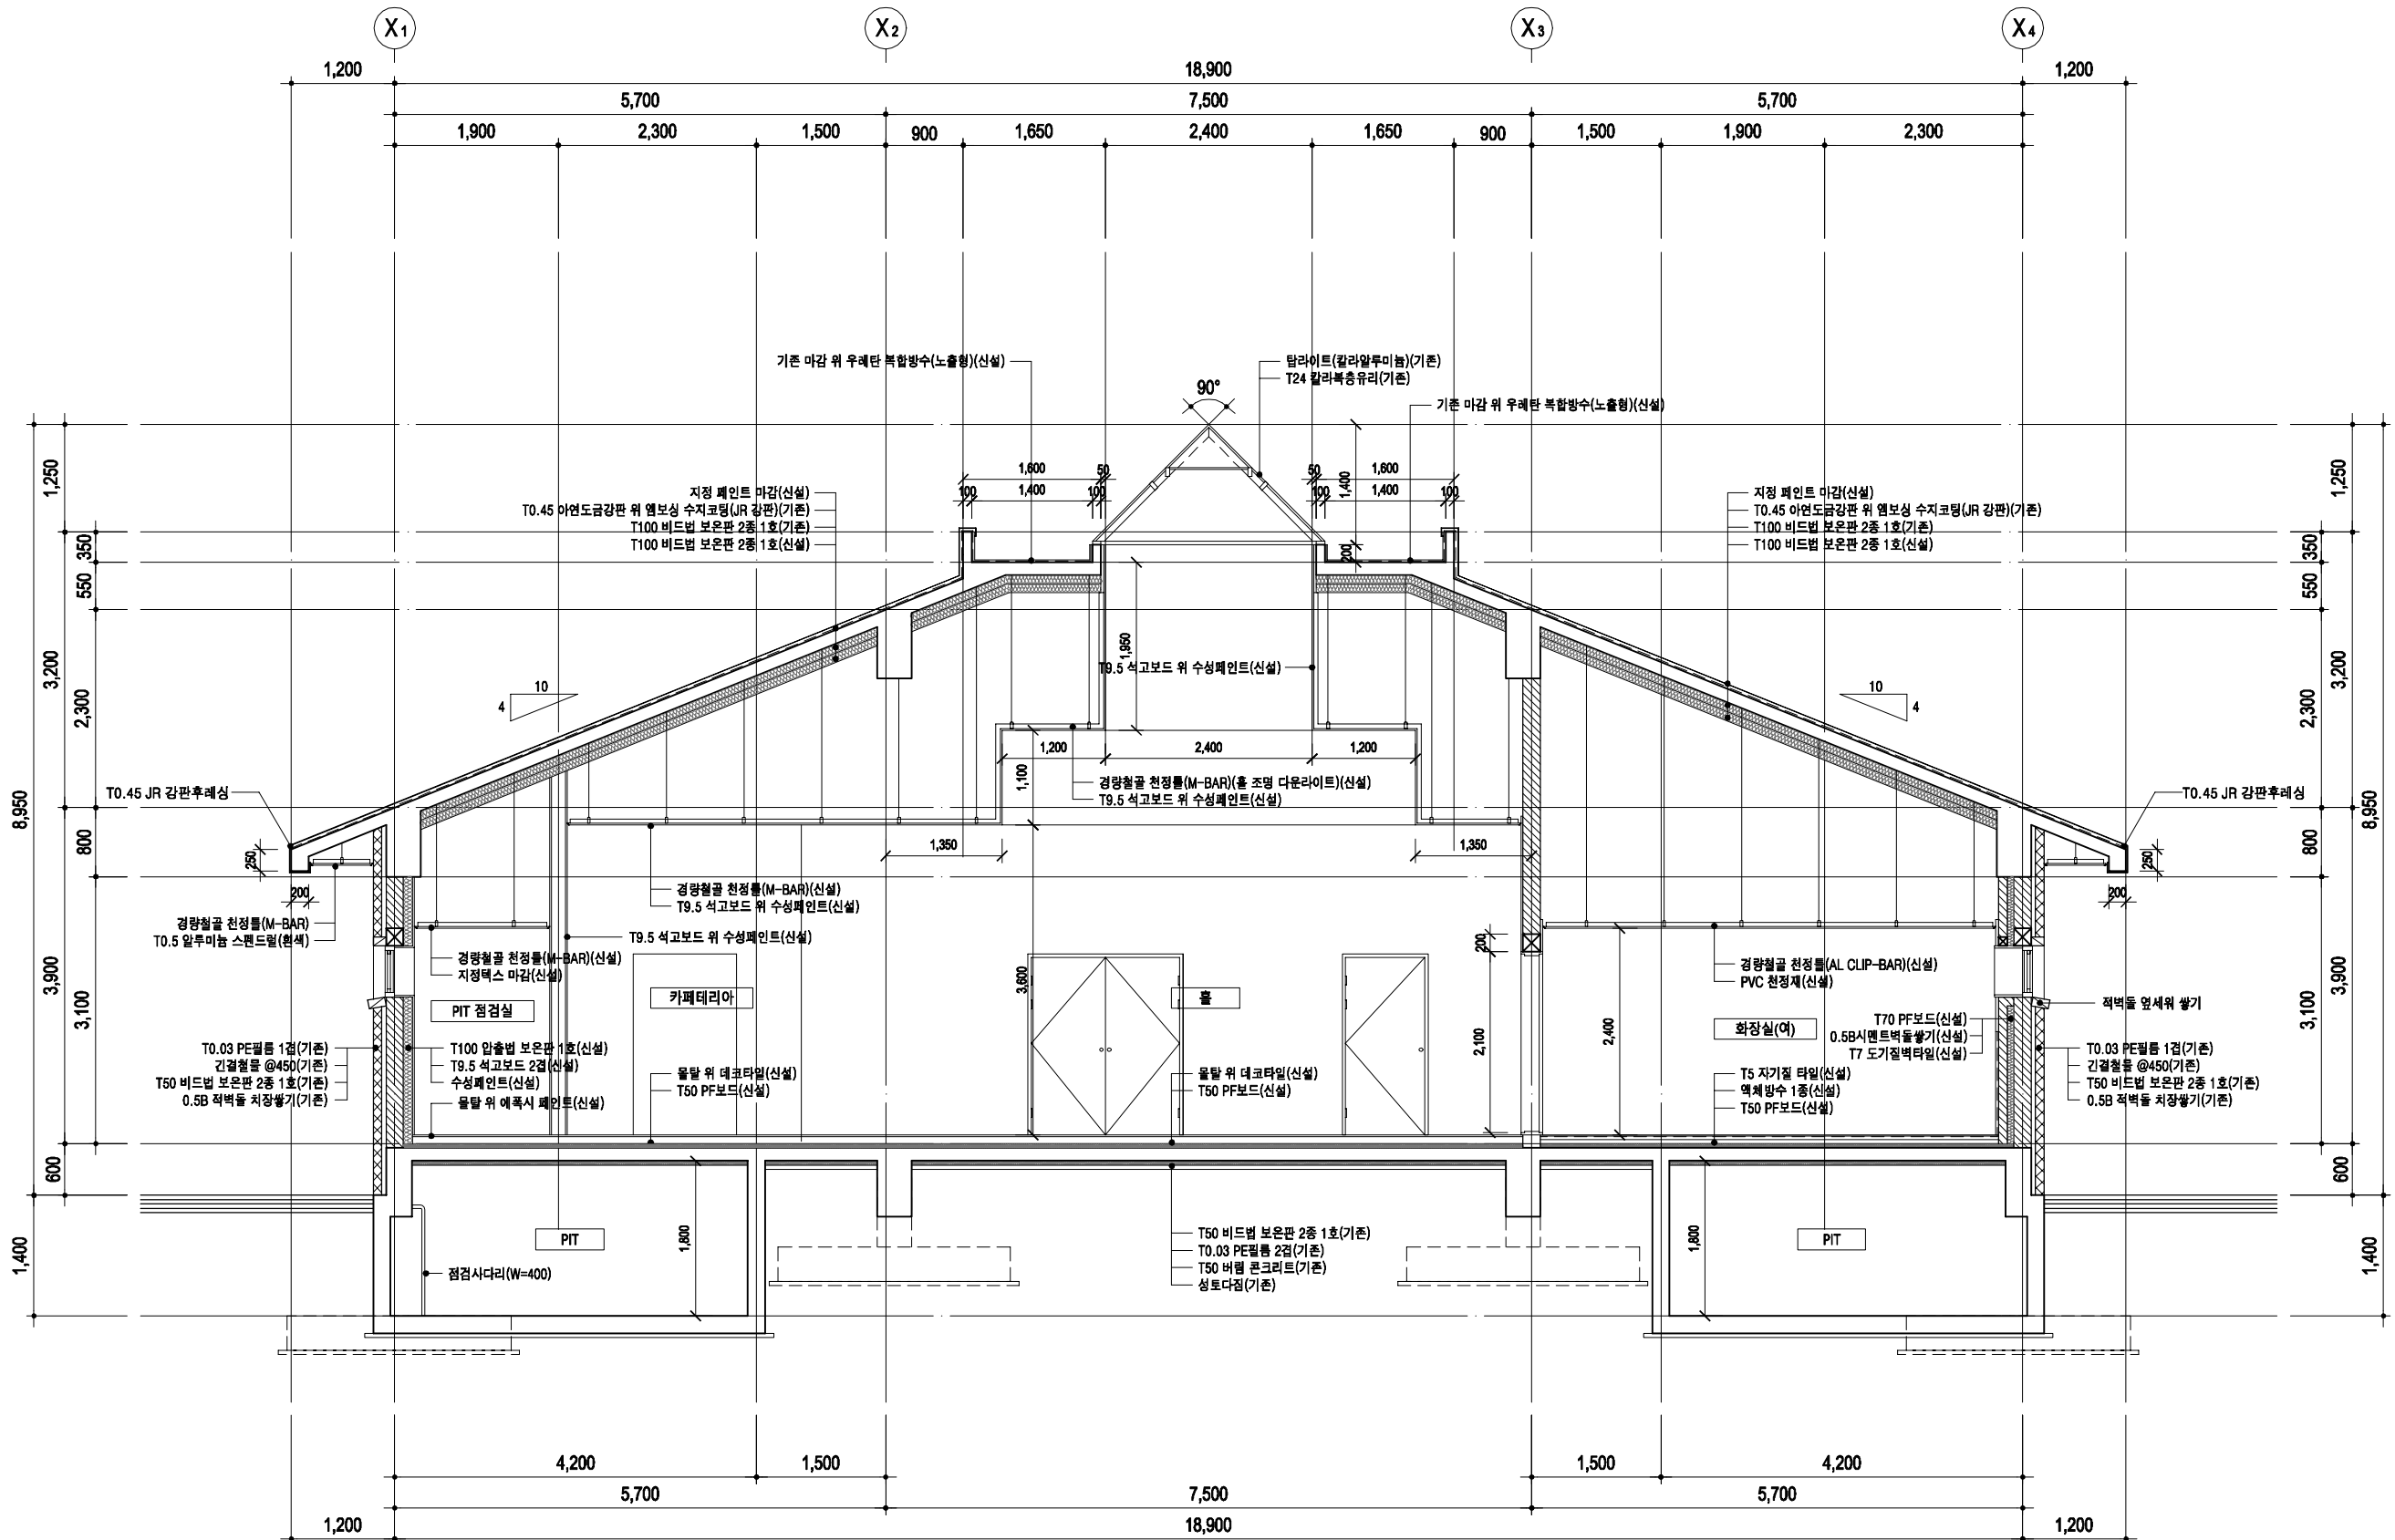

주1-횡 단 면 도(변경후)

축척 A1:1/40, A3:1/80

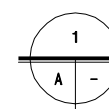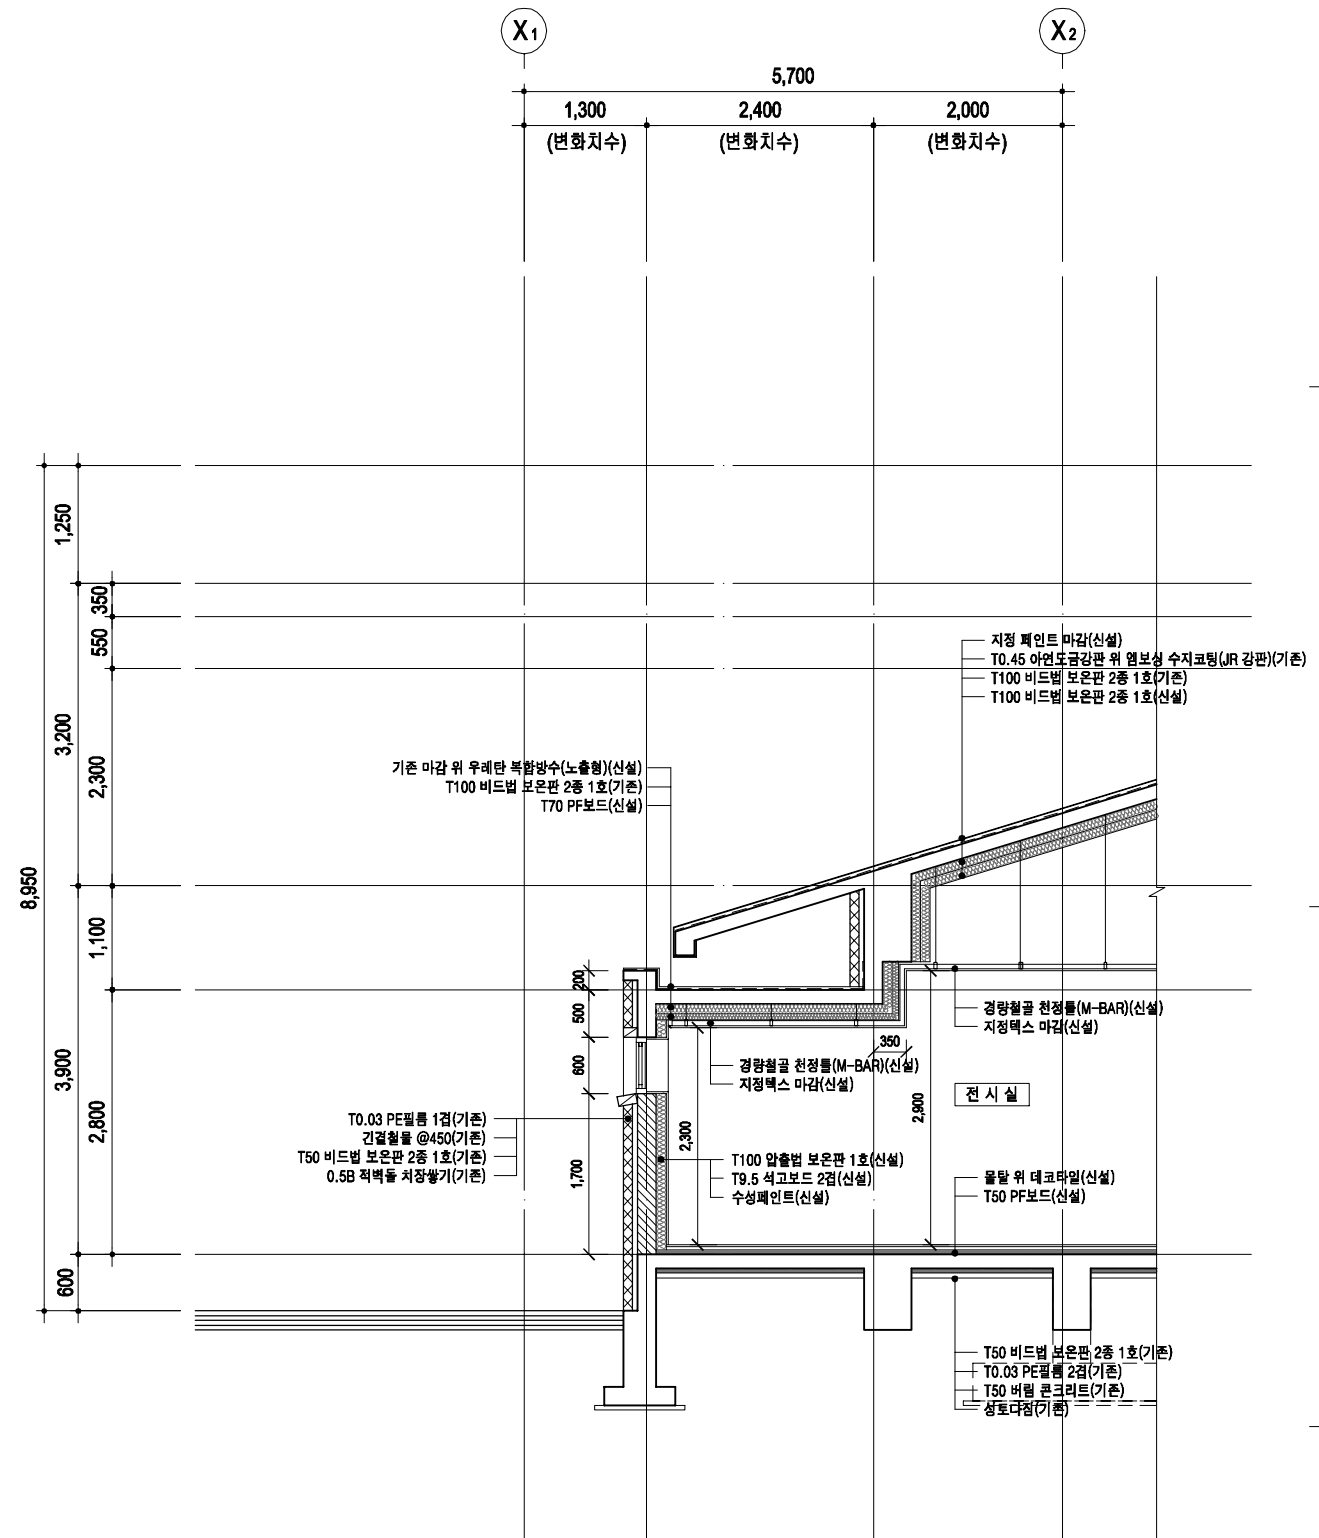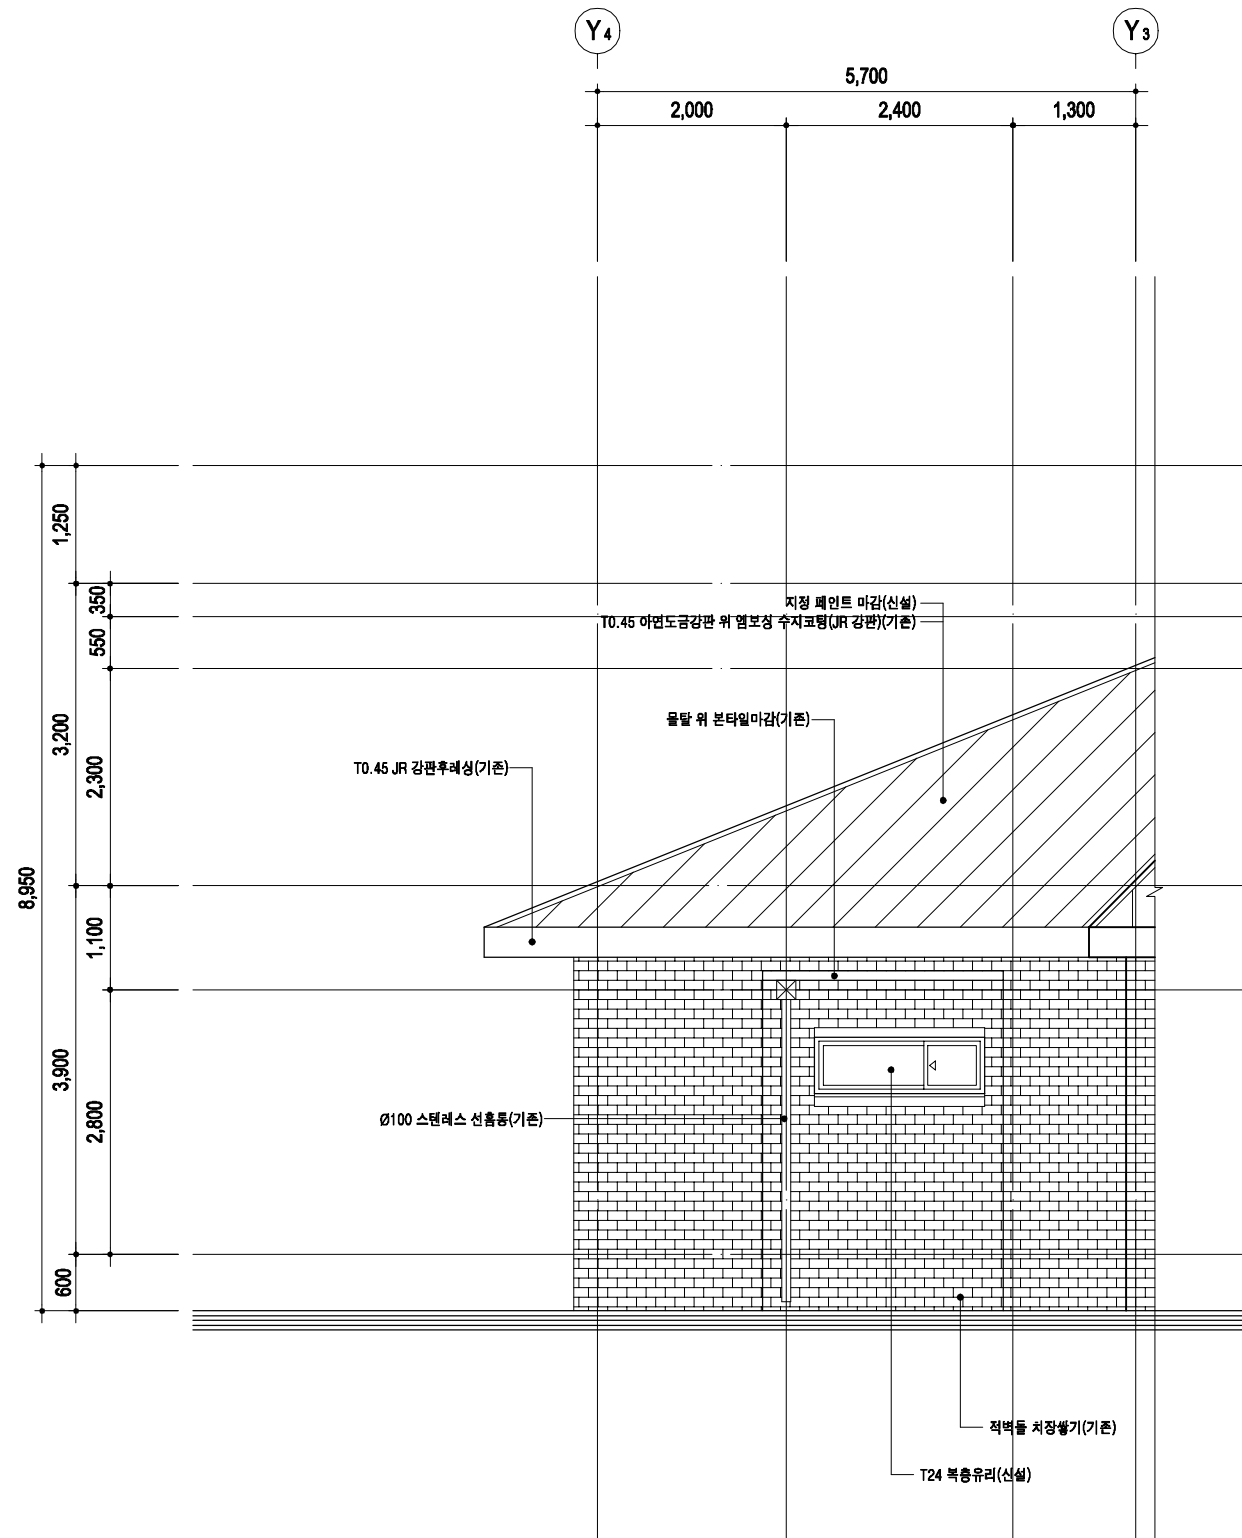

## 주1-부분 입단면 상세도(변경후)

축척 A1:1/40, A3:1/80

PROJECT TITLE


리틀 포레스트  
봉뜨락 조성사업

PROJECT NO

NOTE

- 단열기준(중부1지역) 이하로 할 것.
- 바닥: 0.240(W/㎡.K)이하 (외기단열)
- 벽 : 0.170(W/㎡.K)이하 (외기단열)
- 지붕: 0.150(W/㎡.K)이하 (외기단열)
- \* 형질성능 내역 참고 할 것.

KEY PLAN

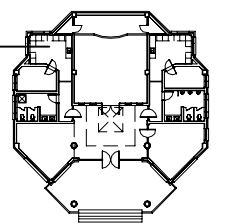

DESIGN CORP.

**이음** (주)이음건축사사무소

ADD. 대구광역시 중구 장동로 81, 5F  
TEL. 053.716.0776 FAX. 0505.720.0776  
E-mail. e-ul2020@naver.com  
Web. eul2020 / 0776

APPROVED BY  
대표이사/건축사 권오섭

CHECKED BY


DRAWN BY

DATE 2023. 04.

DRAWING TITLE  
주1-부분 입단면상세도  
(변경후)

SCALE A3 : 1/ 80

DRAWING NO. A01- 303

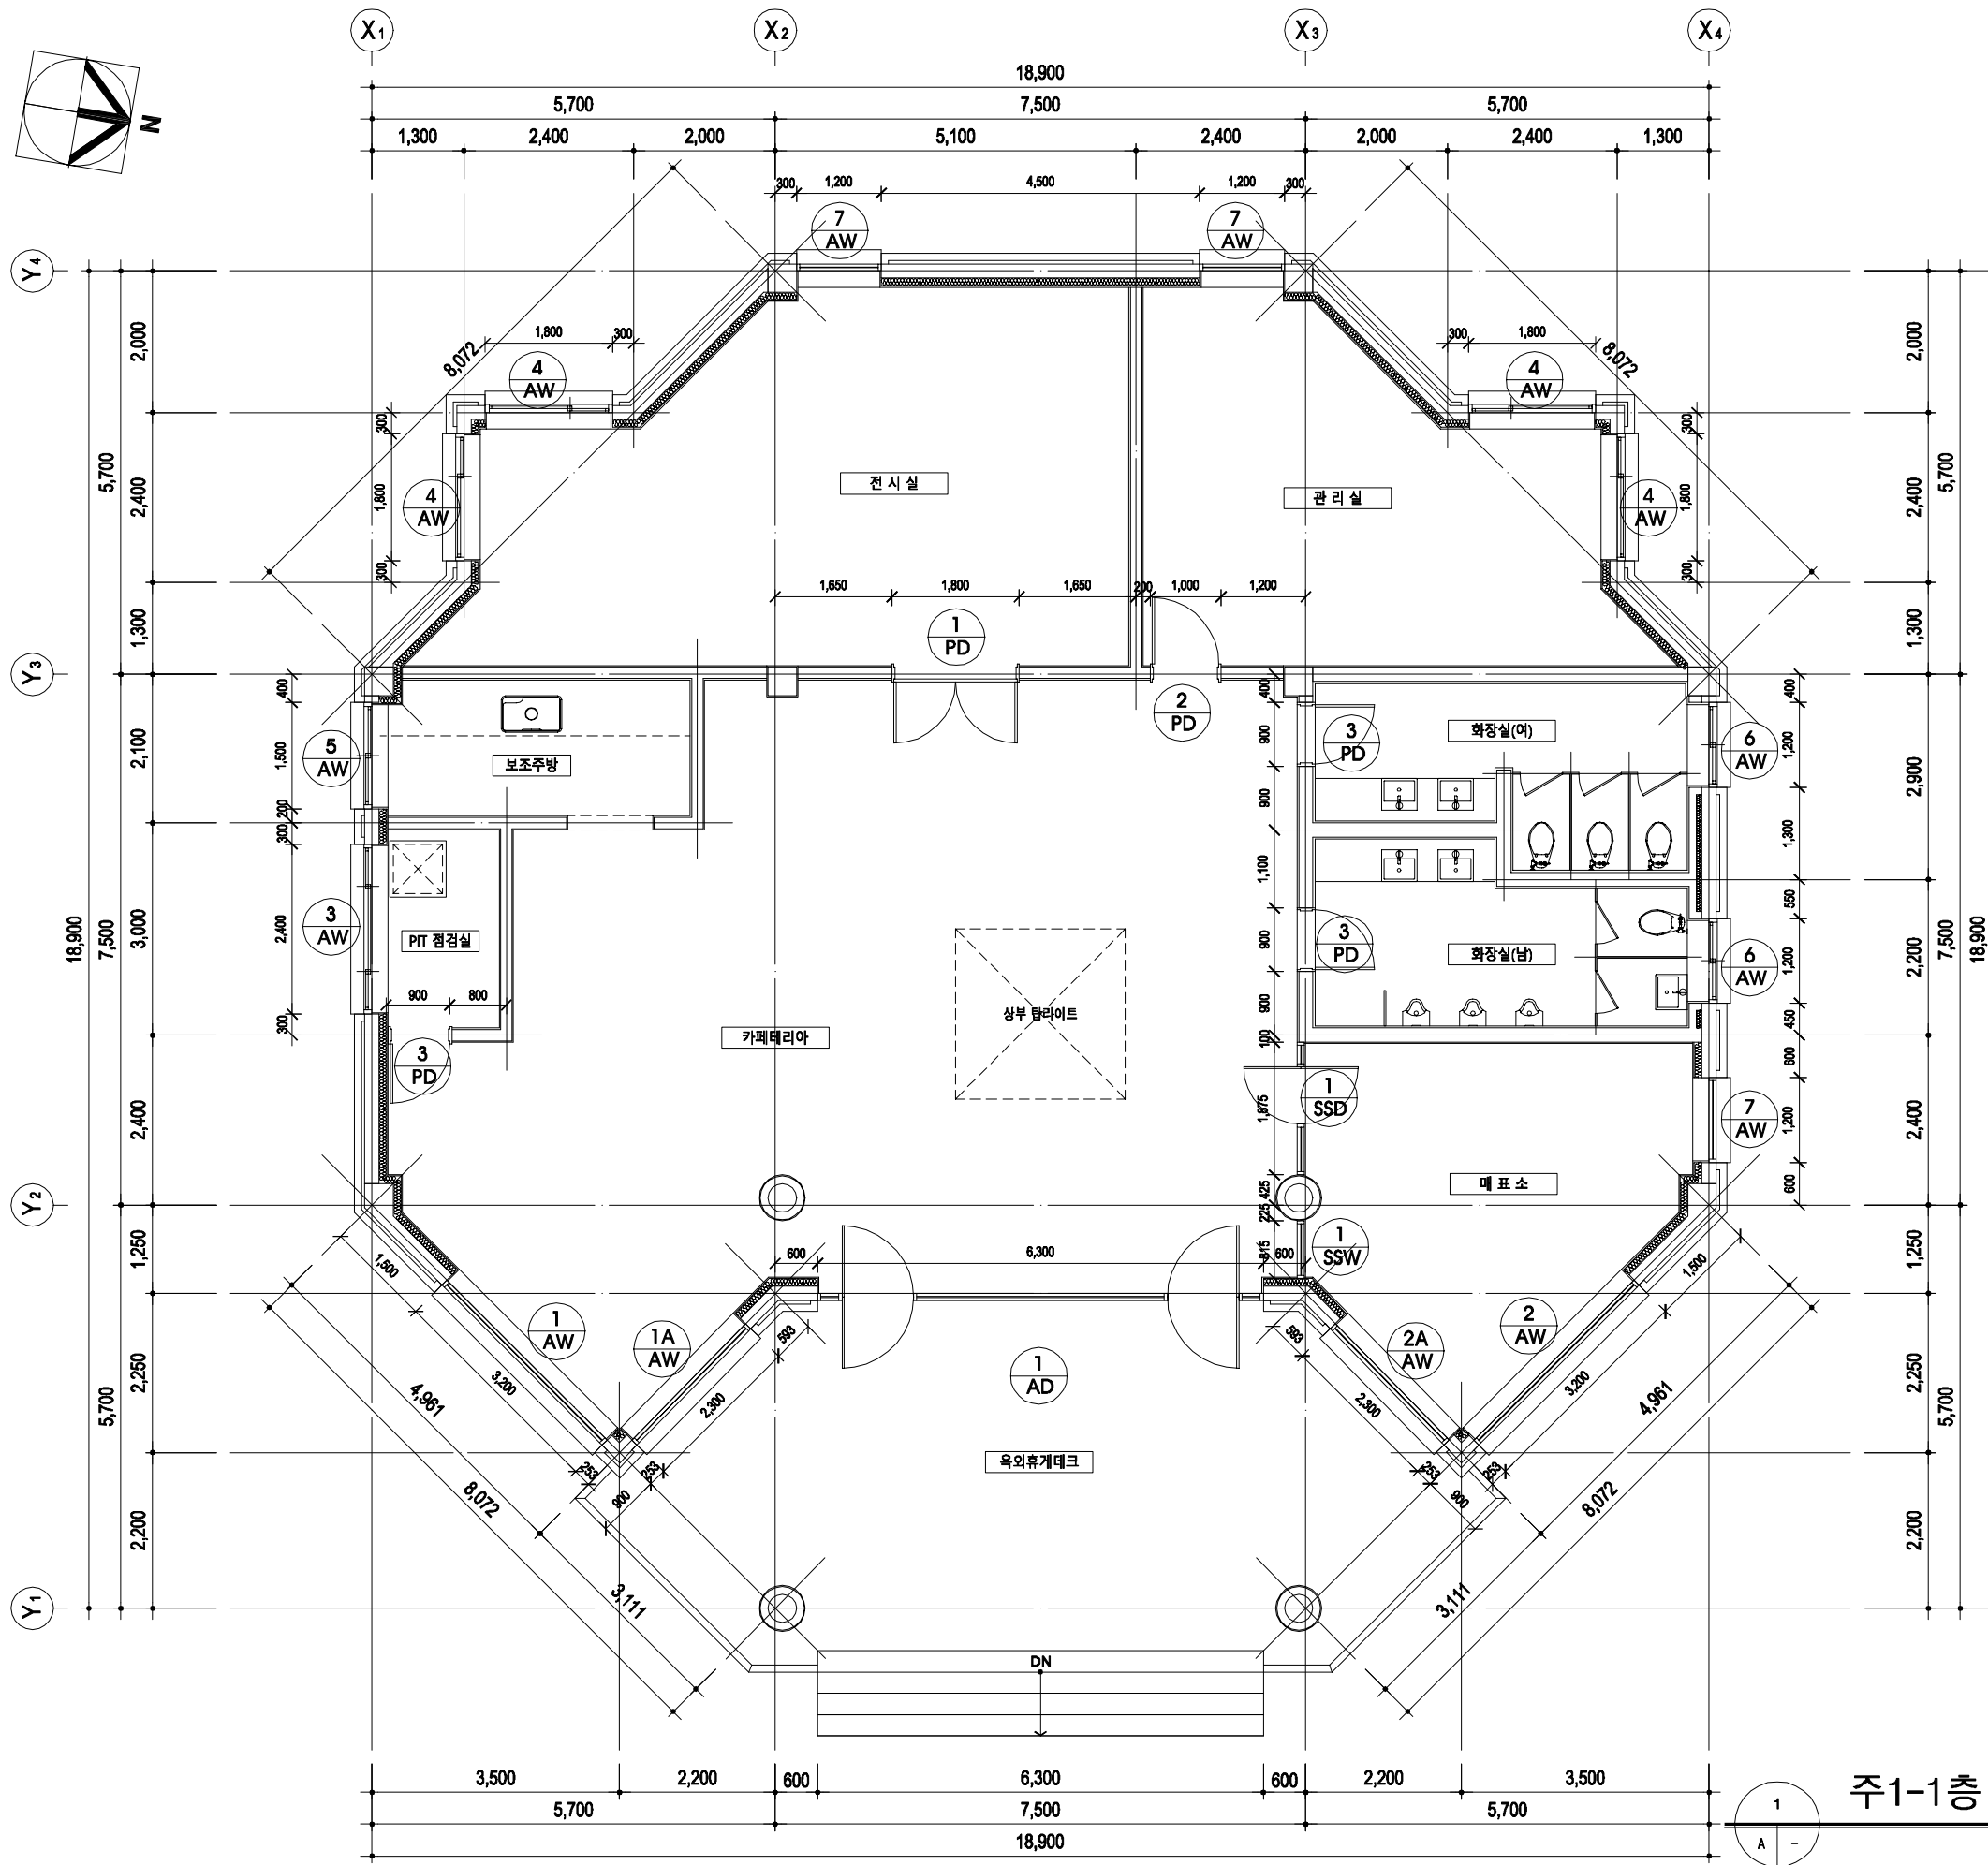

주1-1층 창호평면도(변경후)

축척 A1:1/50, A3:1/100

|               |   |
|---------------|---|
| PROJECT TITLE | 리틀 포레스트<br>봉뜨락 조성사업   |
| PROJECT NO    |   |
| NOTE          |   |
| KEY PLAN      |   |
| DESIGN CORP.  | <b>이음</b> (주)이음건축사사무소<br>ADD. 대구광역시 중구 장동로 81, 5F<br>TEL. 053.716.0776 FAX. 0505.720.0776<br>E-mail. e-ul2020@naver.com<br>Web. eul2020 / 0776 |
| APPROVED BY   | 대표이사/건축사 권오섭   |
| CHECKED BY    |   |
| DRAWN BY      |   |
| DATE          | 2023. 04.   |
| DRAWING TITLE | 1층 창호평면도<br>(변경후)   |
| SCALE         | A3 : 1/ 100   |
| DRAWING NO.   | A01-401   |

# 주1-창호일람표-1(변경후)

축척 A1:1/40, A3:1/80

PROJECT TITLE

리를 포레스트  
봉뜨락 조성사업

PROJECT NO

NOTE

KEY PLAN

DESIGN CORP.

**이음** (주)이음건축사사무소

ADD. 대구광역시 중구 장동로 81, 5F  
TEL. 053.716.0776 FAX. 0505.720.0776  
E-mail. e-ul2020@naver.com  
Web. eul2020 / 0776

APPROVED BY  
대표이사 / 건축사 권오섭

CHECKED BY

DRAWN BY

DATE 2023. 04.


DRAWING TITLE  
주1-창호일람표-1  
(변경후)

SCALE A3 : 1/ 80

DRAWING NO. A01-402

|     |                                                           |       |    |    |   |   |       |    |    |   |                                                                                       |       |    |    |   |
|-----|-----------------------------------------------------------|-------|----|----|---|---|-------|----|----|---|---------------------------------------------------------------------------------------|-------|----|----|---|
| 부 호 | 1                                                         | [기 준] | 1F | RF | 계 | 1   | [기 준] | 1F | RF | 계 | 1                                                                                     | [신 규] | 1F | RF | 계 |
| 개 소 | SSD                                                       |       | 1  | -  | 1 | SSW   |       | 1  | -  | 1 | AD                                                                                    |       | 1  | -  | 1 |
| 부   |                                                           |       |    |    |   |   |       |    |    |   |                                                                                       |       |    |    |   |
| 다   |                                                           |       |    |    |   |   |       |    |    |   |                                                                                       |       |    |    |   |
| 위   | 대표소                                                       |       |    |    |   | 대표소   |       |    |    |   | 홀                                                                                     |       |    |    |   |
| 재   | 문틀: 45x100x1.2t 스테레스 각접기(내부:1.6t 절판보강)                    |       |    |    |   | 115mm 플라스틱 BAR   |       |    |    |   | 151mm AL 단열커튼월 + 100mm AL 단열세이프도어                                                     |       |    |    |   |
| 철   | 기타부속철물 일체                                                 |       |    |    |   | 기타부속철물 일체   |       |    |    |   | 기타부속철물 일체                                                                             |       |    |    |   |
| 유   | 12mm 강화유리문 / FIX: 8mm 강화유리                                |       |    |    |   | 16mm 복층유리   |       |    |    |   | FIX : 24mm 로이복층유리 5LE(소프트,XTN145II(H/S))+14AR+5CL / DOOR : 5CL+14AR(SWS)+5LE(PLA ONE) |       |    |    |   |
| 마   | 창틀주위 우레탄충진, 창틀주위 10x10 수밀코킹                               |       |    |    |   | 창틀주위 우레탄충진, 창틀주위 10x10 수밀코킹                                                                                          |       |    |    |   | 창틀주위 우레탄충진, 창틀주위 10x10 수밀코킹                                                           |       |    |    |   |
| 부   | 1                                                         | [신 규] | 1F | RF | 계 | 2   | [신 규] | 1F | RF | 계 | 3                                                                                     | [신 규] | 1F | RF | 계 |
| 개   | PD                                                        |       | 1  | -  | 1 | PD   |       | 1  | -  | 1 | PD                                                                                    |       | 3  | -  | 3 |
| 부   |                                                           |       |    |    |   |   |       |    |    |   |                                                                                       |       |    |    |   |
| 다   |                                                           |       |    |    |   |   |       |    |    |   |                                                                                       |       |    |    |   |
| 위   | 전시실                                                       |       |    |    |   | 관리실   |       |    |    |   | 화장실 (남), 화장실 (여), PIT 점검실                                                             |       |    |    |   |
| 재   | 문틀: 플라스틱 문틀                                               |       |    |    |   | 문틀: 플라스틱 문틀   |       |    |    |   | 문틀: 플라스틱 문틀                                                                           |       |    |    |   |
| 철   | 기타부속철물 일체                                                 |       |    |    |   | 기타부속철물 일체   |       |    |    |   | 기타부속철물 일체                                                                             |       |    |    |   |
| 유   | FIX: THK5 투명유리                                            |       |    |    |   | -   |       |    |    |   | -                                                                                     |       |    |    |   |
| 마   | 창틀주위 우레탄충진, 창틀주위 10x10 수밀코킹                               |       |    |    |   | 창틀주위 우레탄충진, 창틀주위 10x10 수밀코킹                                                                                          |       |    |    |   | 창틀주위 우레탄충진, 창틀주위 10x10 수밀코킹                                                           |       |    |    |   |
| 부   | 2                                                         | [신 규] | 1F | RF | 계 | 2A   | [신 규] | 1F | RF | 계 | 3                                                                                     | [신 규] | 1F | RF | 계 |
| 개   | AW                                                        |       | 1  | -  | 1 | AW   |       | 1  | -  | 1 | AW                                                                                    |       | 2  | -  | 2 |
| 부   |                                                           |       |    |    |   |   |       |    |    |   |                                                                                       |       |    |    |   |
| 다   |                                                           |       |    |    |   |   |       |    |    |   |                                                                                       |       |    |    |   |
| 위   | 대표소                                                       |       |    |    |   | 대표소   |       |    |    |   | PIT 점검실                                                                               |       |    |    |   |
| 재   | 151mm AL 단열커튼월 + 83mm AL 단열프로젝트창                          |       |    |    |   | 151mm AL 단열커튼월 + 150mm AL 단열미서기단창                                                                                    |       |    |    |   | 150mm AL 단열미서기단창                                                                      |       |    |    |   |
| 철   | 기타부속철물 일체 / 방충망(내부)                                       |       |    |    |   | 기타부속철물 일체 / 방충망(내부)                                                                                                  |       |    |    |   | 기타부속철물 일체 / 방충망(내부)                                                                   |       |    |    |   |
| 유   | FIX,PJ : 24mm 로이복층유리 5LE(소프트,XTN145II(H/S))+14AR+5CL      |       |    |    |   | FIX : 24mm 로이복층유리 5LE(소프트,XTN145II(H/S))+14AR+5CL<br>미서기창: 43mm 로이삼중유리 5LE(SKN145II(H/S))+14AR+5CL+14AR+5LE(PLA ONE) |       |    |    |   | 43mm 로이삼중유리 5LE(SKN145II(H/S))+14AR+5CL+14AR+5LE(PLA ONE)                             |       |    |    |   |
| 마   | 창틀주위 우레탄충진, 창틀주위 10x10 수밀코킹                               |       |    |    |   | 창틀주위 우레탄충진, 창틀주위 10x10 수밀코킹                                                                                          |       |    |    |   | 창틀주위 우레탄충진, 창틀주위 10x10 수밀코킹                                                           |       |    |    |   |
| 부   | 4                                                         | [신 규] | 1F | RF | 계 | 5   | [신 규] | 1F | RF | 계 |                                                                                       |       |    |    |   |
| 개   | AW                                                        |       | 4  | -  | 4 | AW   |       | 1  | -  | 1 |                                                                                       |       |    |    |   |
| 부   |                                                           |       |    |    |   |   |       |    |    |   |                                                                                       |       |    |    |   |
| 다   |                                                           |       |    |    |   |   |       |    |    |   |                                                                                       |       |    |    |   |
| 위   | 전시실, 관리실                                                  |       |    |    |   | 보조주방   |       |    |    |   |                                                                                       |       |    |    |   |
| 재   | 150mm AL 단열미서기단창                                          |       |    |    |   | 150mm AL 단열미서기단창   |       |    |    |   |                                                                                       |       |    |    |   |
| 철   | 기타부속철물 일체 / 방충망(내부)                                       |       |    |    |   | 기타부속철물 일체 / 방충망(내부)                                                                                                  |       |    |    |   |                                                                                       |       |    |    |   |
| 유   | 43mm 로이삼중유리 5LE(SKN145II(H/S))+14AR+5CL+14AR+5LE(PLA ONE) |       |    |    |   | 43mm 로이삼중유리 5LE(SKN145II(H/S))+14AR+5CL+14AR+5LE(PLA ONE)                                                            |       |    |    |   |                                                                                       |       |    |    |   |
| 마   | 창틀주위 우레탄충진, 창틀주위 10x10 수밀코킹                               |       |    |    |   | 창틀주위 우레탄충진, 창틀주위 10x10 수밀코킹                                                                                          |       |    |    |   |                                                                                       |       |    |    |   |

주1-창호일람표-2(변경후)

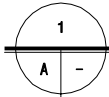

축척 A1:1/40, A3:1/80

|                |                                                           |       |    |    |   |                                                      |       |    |    |   |  |  |  |
|----------------|-----------------------------------------------------------|-------|----|----|---|------------------------------------------------------|-------|----|----|---|--|--|--|
| 부 호<br>개 소     | 6                                                         | [신 규] | 1F | RF | 계 | 7                                                    | [신 규] | 1F | RF | 계 |  |  |  |
|                | AW                                                        |       | 2  | -  | 2 | AW                                                   |       | 3  | -  | 3 |  |  |  |
| 벽면 마감 기준선<br>▼ |                                                           |       |    |    |   |                                                      |       |    |    |   |  |  |  |
|                |                                                           |       |    |    |   |                                                      |       |    |    |   |  |  |  |
|                | 위 치                                                       |       |    |    |   | 매표소, 관리실, 전시실                                        |       |    |    |   |  |  |  |
|                | 재 료                                                       |       |    |    |   | 151mm AL 단열커튼월 + 83mm AL 단열프로젝트창                     |       |    |    |   |  |  |  |
|                | 철 물                                                       |       |    |    |   | 기타부속철물 일체 / 방충망(내부)                                  |       |    |    |   |  |  |  |
| 유 리            | 43mm 로이삼중유리 5LE(SKN145I)(H/S))+14AR+5CL+14AR+5LE(PLA ONE) |       |    |    |   | FIX,PJ : 24mm 로이복중유리 5LE(소프트,XTN145I)(H/S))+14AR+5CL |       |    |    |   |  |  |  |
| 마 감            | 창틀주위 우레탄충진, 창틀주위 10x10 수밀코킹                               |       |    |    |   | 창틀주위 우레탄충진, 창틀주위 10x10 수밀코킹                          |       |    |    |   |  |  |  |
| 부 호            | 1                                                         | [기 존] | 1F | RF | 계 |                                                      |       |    |    |   |  |  |  |
| 개 소            | CAW                                                       |       | -  |    | 1 | 1                                                    |       |    |    |   |  |  |  |
| 벽면 마감 기준선<br>▼ |                                                           |       |    |    |   |                                                      |       |    |    |   |  |  |  |
|                |                                                           |       |    |    |   |                                                      |       |    |    |   |  |  |  |
|                | 위 치                                                       |       |    |    |   | 카페테리아 상부                                             |       |    |    |   |  |  |  |
|                | 재 료                                                       |       |    |    |   | 100mm 플라스틱 BAR                                       |       |    |    |   |  |  |  |
|                | 철 물                                                       |       |    |    |   | 기타부속철물일체                                             |       |    |    |   |  |  |  |
| 유 리            | 24mm 투명복중유리                                               |       |    |    |   |                                                      |       |    |    |   |  |  |  |
| 마 감            | 창틀주위 우레탄충진, 창틀주위 10x10 수밀코킹, 지정색 불소수지코팅                   |       |    |    |   |                                                      |       |    |    |   |  |  |  |

PROJECT TITLE

리틀 포레스트  
봉뜨락 조성사업

PROJECT NO

NOTE

KEY PLAN

DESIGN CORP.



ADD. 대구광역시 동구 장동로 81, 5F  
TEL. 053.716.0776 FAX. 0505.720.0776  
E-mail. e-ul2020@naver.com  
Web. eul2020 / 0776

APPROVED BY  
대표이사/건축사 권오섭

CHECKED BY


DRAWN BY

DATE  
2023. 04.

DRAWING TITLE  
주1-창호일람표-2  
(변경후)

SCALE  
A3 : 1/ 80


DRAWING NO.  
A01-403

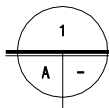


# 주1-화장실 전개도

축척 A1:1/30, A3:1/60


화장실 확대 평면도

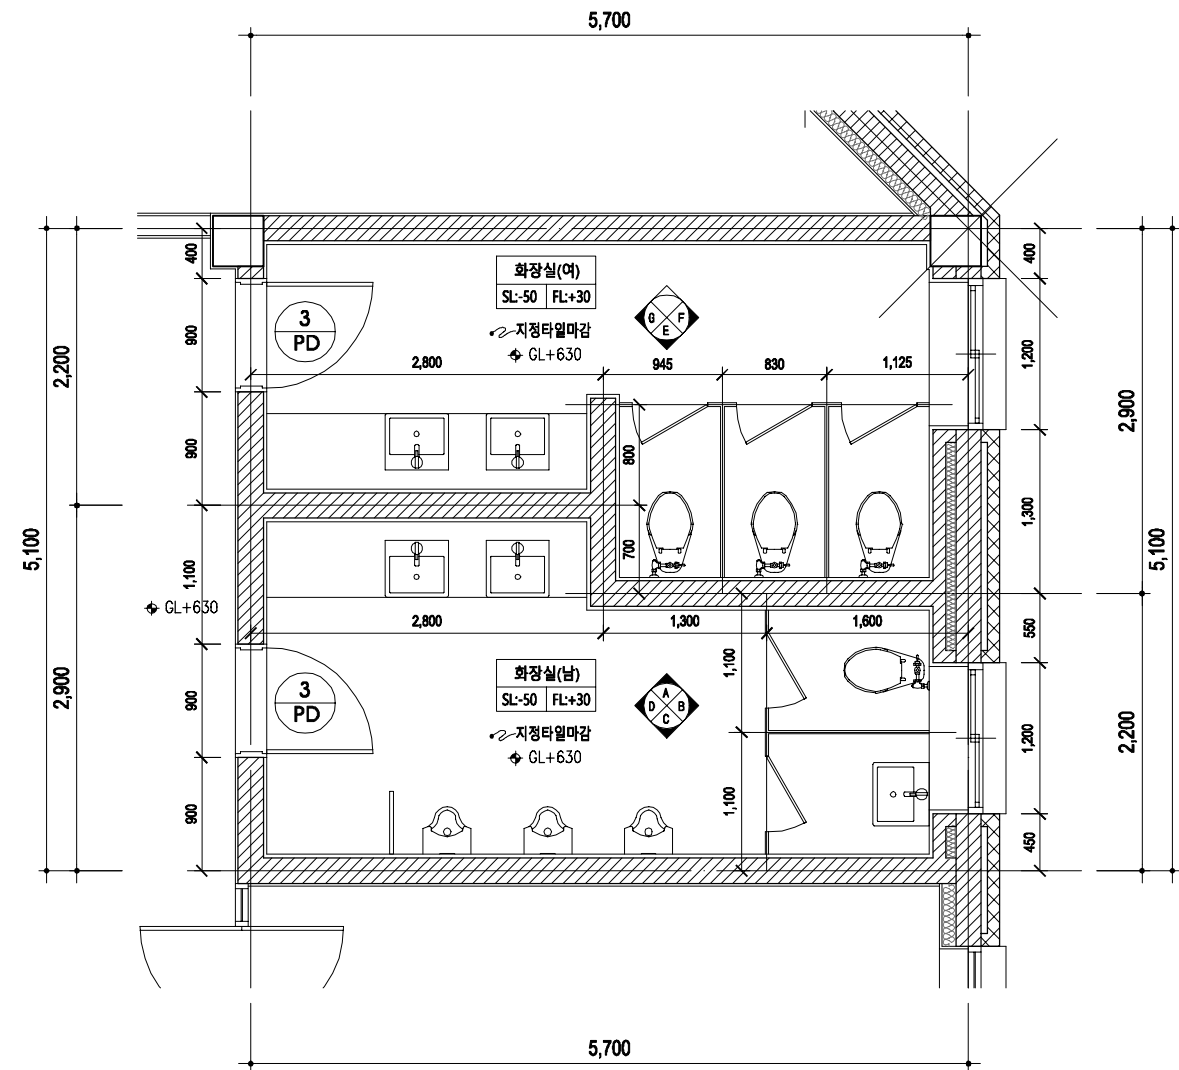


화장실(남) "A"전개도

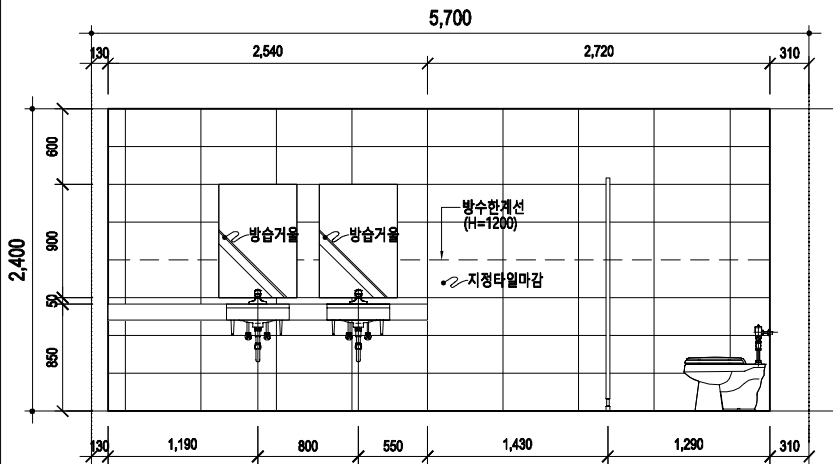


화장실(남) "B"전개도

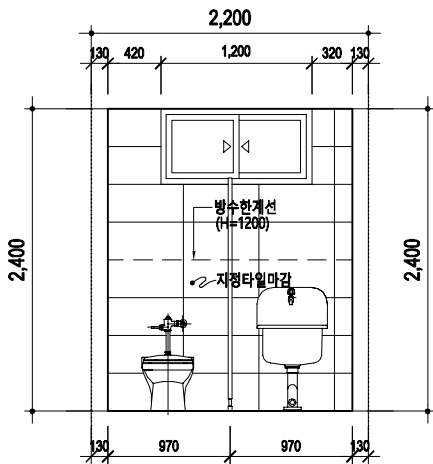


화장실(남) "C"전개도

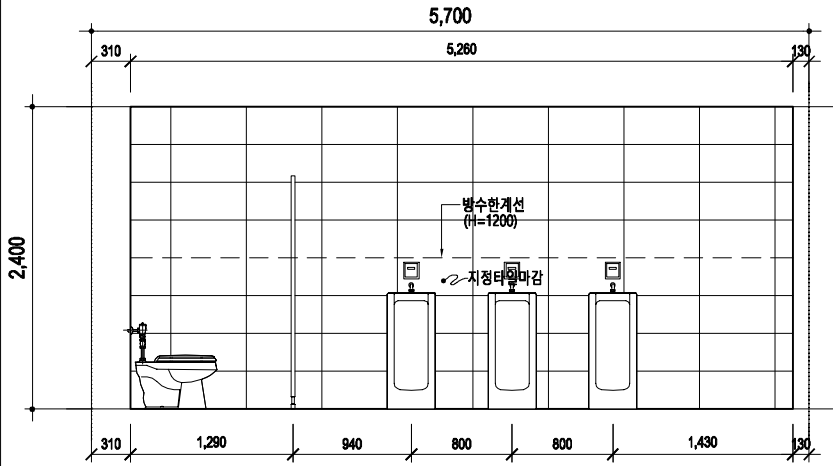


화장실(남) "D"전개도

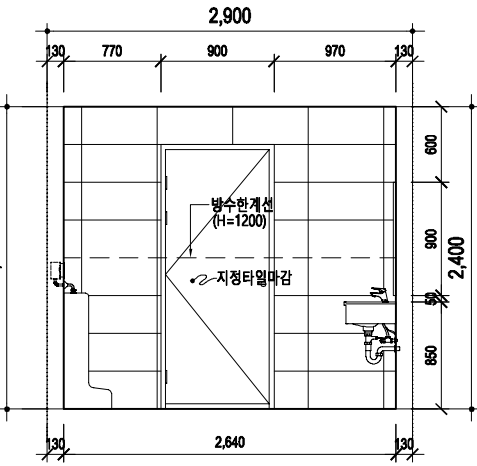


화장실(여) "E"전개도

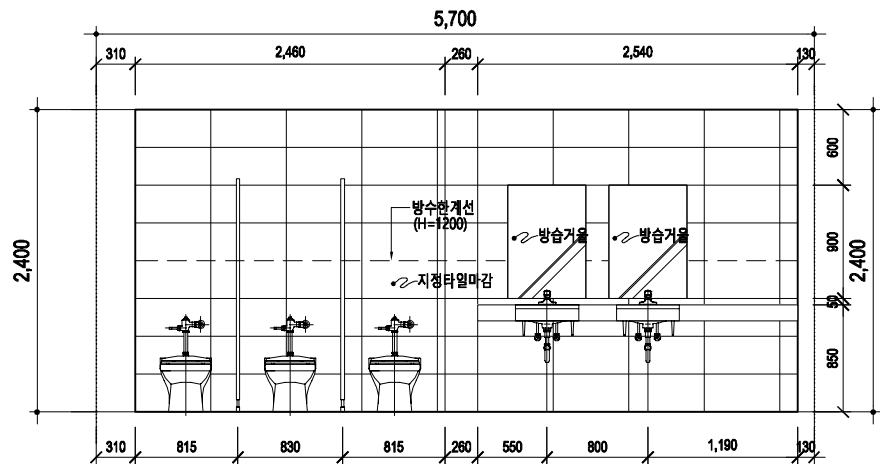

화장실(여) "F"전개도

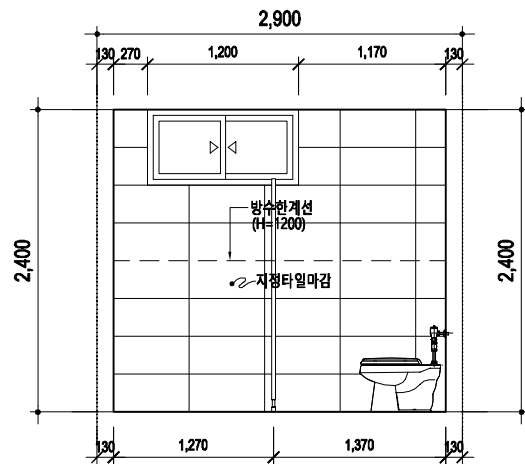

화장실(여) "G"전개도

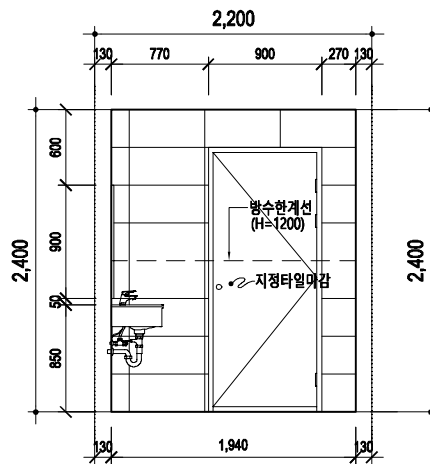

PROJECT TITLE

리틀 포레스트  
봉뜨락 조성사업

PROJECT NO

NOTE

KEY PLAN

DESIGN CORP.

**이음** (주)이음건축사사무소

ADD. 대구광역시 중구 장동로 81, 5F  
TEL. 053.716.0776 FAX. 0505.720.0776  
E-mail. e-ul2020@naver.com  
Web. eul2020 / 0776

APPROVED BY  
대표이사/건축사 권오섭

CHECKED BY

DRAWN BY

DATE 2023. 04.

DRAWING TITLE

주1-화장실 전개도

SCALE A3 : 1/ 60

DRAWING NO. A01-501

### # 지역별 형별 성능 관계 내역 - 1 (중부1지역)

구분

단면구조

열관류율계산결과

W1

외벽 (외기직접)

외부

내부

469

905020011019

외: 0.58 적벽돌 쌓기  
T50 비드법2중 1호  
T200 콘크리트  
T110 압출법 1호  
내: 19.5 석고보드 2겹

| 번호            | 재료명               | 두께:D<br>(m) | 열전도율:λ<br>(W/m.K) | 열전도저항:r<br>(㎡.K/W) | 열관류율:K<br>(W/㎡.K) |     |
|---------------|-------------------|-------------|-------------------|--------------------|-------------------|-----|
| 1             | 실외표면열전달저항Ro       | -           | -                 | 0.043              | 0.164             |     |
| 2             | 적벽돌(치장쌓기) (기준)    | 0.090       | 0.600             | 0.150              |                   |     |
| 3             | 비드법보온판 2중 1호 (기준) | 0.050       | 0.031             | 1.613              |                   |     |
| 4             | 콘크리트(124) (기준)    | 0.200       | 1.600             | 0.125              |                   |     |
| 5             | 압출법보온판 1호 (신설)    | 0.110       | 0.028             | 3.929              |                   |     |
| 6             | 석고보드 (신설)         | 0.019       | 0.180             | 0.106              |                   |     |
| 7             | 실내표면열전달저항Ri       | -           | -                 | 0.110              |                   |     |
| 합계            |                   |             |                   |                    | 6.075             |     |
| 기준열관류율(W/㎡.K) |                   |             |                   |                    | 0.170 이하          | 중부1 |

W2

외벽 (외기직접)

외부

내부

459

905019011019

외: 0.58 적벽돌 쌓기  
T50 비드법2중 1호  
1.08 시멘트벽돌 쌓기  
T110 압출법 1호  
내: 19.5 석고보드 2겹

| 번호            | 재료명               | 두께:D<br>(m) | 열전도율:λ<br>(W/m.K) | 열전도저항:r<br>(㎡.K/W) | 열관류율:K<br>(W/㎡.K) |     |
|---------------|-------------------|-------------|-------------------|--------------------|-------------------|-----|
| 1             | 실외표면열전달저항Ro       | -           | -                 | 0.043              | 0.159             |     |
| 2             | 적벽돌(치장쌓기) (기준)    | 0.090       | 0.600             | 0.150              |                   |     |
| 3             | 비드법보온판 2중 1호 (기준) | 0.050       | 0.031             | 1.613              |                   |     |
| 4             | 시멘트벽돌 (기준)        | 0.190       | 0.600             | 0.317              |                   |     |
| 5             | 압출법보온판 1호 (신설)    | 0.110       | 0.028             | 3.929              |                   |     |
| 6             | 석고보드 (신설)         | 0.019       | 0.180             | 0.106              |                   |     |
| 7             | 실내표면열전달저항Ri       | -           | -                 | 0.110              |                   |     |
| 합계            |                   |             |                   |                    | 6.267             |     |
| 기준열관류율(W/㎡.K) |                   |             |                   |                    | 0.170 이하          | 중부1 |

W3

외벽 (외기직접)

외부

내부

459

905019011019

외: 0.58 적벽돌 쌓기  
T50 비드법2중 1호  
1.08 시멘트벽돌 쌓기  
T110 압출법 1호  
내: 0.58 시멘트벽돌 쌓기

| 번호            | 재료명               | 두께:D<br>(m) | 열전도율:λ<br>(W/m.K) | 열전도저항:r<br>(㎡.K/W) | 열관류율:K<br>(W/㎡.K) |     |
|---------------|-------------------|-------------|-------------------|--------------------|-------------------|-----|
| 1             | 실외표면열전달저항Ro       | -           | -                 | 0.043              | 0.169             |     |
| 2             | 적벽돌(치장쌓기) (기준)    | 0.090       | 0.600             | 0.150              |                   |     |
| 3             | 비드법보온판 2중 1호 (기준) | 0.050       | 0.031             | 1.613              |                   |     |
| 4             | 시멘트벽돌 (기준)        | 0.190       | 0.600             | 0.317              |                   |     |
| 5             | PF보드 (신설)         | 0.070       | 0.020             | 3.500              |                   |     |
| 6             | 시멘트벽돌 (신설)        | 0.090       | 0.600             | 0.150              |                   |     |
| 7             | 실내표면열전달저항Ri       | -           | -                 | 0.110              |                   |     |
| 합계            |                   |             |                   |                    | 5.883             |     |
| 기준열관류율(W/㎡.K) |                   |             |                   |                    | 0.170 이하          | 중부1 |

구분

단면구조

열관류율계산결과

번호

재료명

두께:D  
(m)

열전도율:λ  
(W/m.K)

열전도저항:r  
(㎡.K/W)

열관류율:K  
(W/㎡.K)

합계

기준열관류율(W/㎡.K)

번호

재료명

두께:D  
(m)

열전도율:λ  
(W/m.K)

열전도저항:r  
(㎡.K/W)

열관류율:K  
(W/㎡.K)

합계

기준열관류율(W/㎡.K)

번호

재료명

두께:D  
(m)

열전도율:λ  
(W/m.K)

열전도저항:r  
(㎡.K/W)

열관류율:K  
(W/㎡.K)

합계

기준열관류율(W/㎡.K)

# 단열재의 등급

"가" 등급: 열전도율이 0.034 W/mK(0.029 kcal/mh°C)이하인 경우

"나" 등급: 열전도율이 0.035 ~ 0.040 W/mK(0.030~0.034 kcal/mh°C) 이하인 경우

"다" 등급: 열전도율이 0.041 ~ 0.046 W/mK(0.035~0.039 kcal/mh°C) 이하인 경우

"라" 등급: 열전도율이 0.047 ~ 0.051 W/mK(0.040~0.044 kcal/mh°C) 이하인 경우

# 방습층 (투습도가 24시간당 30g/m<sup>2</sup> 이하 또는 투습계수 0.28g/m<sup>2</sup>.h.mmHg 이하의 투습저항을 가진층)으로 인정될 수 있는 재료 또는 구조일것.

# 바닥난방에서 단열재의 설치

가. 바닥난방 부위에 설치되는 단열재는 바닥난방의 열이 슬래브 하부 및 측벽으로 손실되는 것을 막을 수 있도록 온수배관 (전기난방인 경우는 발열선) 하부와 슬래브 사이에 설치하고, 온수배관 (전기난방인 경우는 발열선) 하부와 슬래브 사이에 설치되는 구성 재료의 열저항의 합계는 층간 바닥의 경우에는 해당 바닥에 요구되는 총열관류저항(별표1에서 제시되는 열관류저항의 역수)의 60% 이상 최하층 바닥인 경우에는 70% 이상이 되어야 한다. 다만, 바닥난방을 하는 욕실 및 현관부위와 슬래브의 측벽을 직접 이용하는 심야전기이용 온돌 등 (한국전력의 심야전력이용기기 승인을 받은 것에 한한다)의 경우에는 단열재의 위치가 그러하지 않을 수 있다.

# 기밀 및 결로방지 등을 위한 조치  
가. 벽체 내표면 및 내부에서의 결로를 방지하고 단열재의 성능저하를 방지하기 위하여 규칙 제21조 규정에 의하여 단열조치를 하여야 하는 하는 부위(외벽 및 공동주택 층간바닥제외)에는 방습층을 단열재의 실내측에 설치 하여야 한다.

나. 방습층 및 단열재가 이어지는 부위 및 단부는 이음 및 단부를 통한 투습을 방지할수 있도록 다음과 같이 조치하여야 한다.

- 1) 단열재의 이음부는 최대한 밀착하여 시공하거나 2장을 엇갈리게 시공하여 이음부를 통한 단열성은 저하가 최소화될 수 있도록 조치할것.
- 2) 방습층으로 알루미늄박 또는 플라스틱 필름 등을 사용할 경우의 이음부는 100mm 이상 중첩하고 내습성 테이프, 접착제 등으로 기밀하게 마감할것.
- 3) 단열부위가 만나는 모서리 부위는 방습층 및 단열재가 이어짐이 없이 시공하거나 이어질경우 이음부를 통한 단열성은 저하가 최소화 되도록 하며, 알루미늄박 또는 플라스틱계 필름 등을 사용할 경우의 모서리 이음부는 150mm이상 중첩되게 시공하고 내습성 테이프, 접착제 등으로 기밀하게 마감할것.
- 4) 방습층의 단부는 단부를 통한 루핑이 발생하지 않도록 내습성 테이프, 접착제 등으로 기밀하게 마감할것.

다. 건축물 외피 단열부위의 접합부, 틈 등은 밀폐될수 있도록 코킹과 가스켓등을 사용하여 기밀하게 처리하여야 한다.

라. 외기에 직접 면하고 1층 또는 지상으로 연결된 출입문은 제5조제9호  
아목에 따른 방풍구조로 하여야 한다. 다만, 다음 각 호에 해당하는  
경우에는 그러하지 않을 수 있다.

- 1) 바닥면적 3백 제곱미터 이하의 개별 점포의 출입문
- 2) 주택의 출입문(단, 기숙사는 제외)
- 3) 사람의 통행을 주목적으로 하지 않는 출입문
- 4) 너비 1.2미터 이하의 출입문

다. 방풍구조를 설치하여야 하는 출입문에서 회전문과 일반문이 같이 설치되었던 경우, 일반문 부위는 방풍실 구조의 이중문을 설치하여야 한다.

바. 건축물의 거실의 창호가 외기에 직접 면하는 부위인 경우에는 제5조 제9호 자목에 따른 기밀성 창호를 설치하여야 한다.

\_\_\_\_\_

PROJECT TITLE

리틀 포레스트  
봉뜨락 조성사업

PROJECT NO. \_\_\_\_\_

#### NOTE

## KEY PLAN

DESIGN CORP.

**이을** (주)이을건축사사무소  
ADD. 대구광역시 동구 장동로 81, 5F  
TEL. 053.716.0776 FAX. 0505.720.0776  
E-mail. e-ul2020@naver.com  
Web. eul2020 / 0776

APPROVED BY  
대표이사/건축사 권 오 섭

CHECKED BY \_\_\_\_\_

DRAWN BY

|      |           |
|------|-----------|
| DATE | 2023. 04. |
|------|-----------|



|                      |
|----------------------|
| <b>DRAWING TITLE</b> |
|----------------------|

### 형별성능관계내역-1

SCALE A3 : 1/ 10

DRAWING NO. **A01-901**

## # 지역별 형별 성능 관계 내역 - 2 (중부1지역)
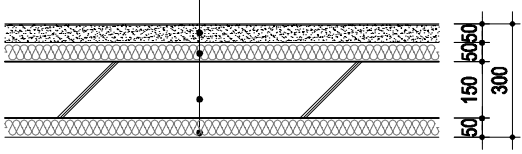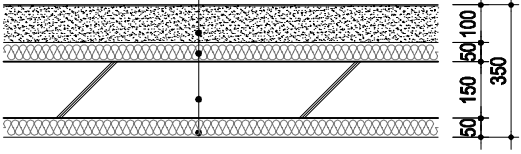
| 구분 |   | F1 | 최 하 층 바 닥 (외 기 간 접) |                                                                                                  |   |   | F2 | 최 하 층 바 닥 (외 기 간 접)                                                                               |                   |             |                   | F3                 |                   |                   |       |             |                   |                    |                   |    |       |             |                   |                    |                   |  |  |  |  |  |
|----|---|----|---------------------|--------------------------------------------------------------------------------------------------|---|---|----|---------------------------------------------------------------------------------------------------|-------------------|-------------|-------------------|--------------------|-------------------|-------------------|-------|-------------|-------------------|--------------------|-------------------|----|-------|-------------|-------------------|--------------------|-------------------|--|--|--|--|--|
| 단  | 면 | 구  | 조                   | <div>실 내</div>  |   |   |    | <div>실 내</div>  |                   |             
|    |   |    |                     | <div>G.L</div>                                                                                   |   |   |    | <div>G.L</div>                                                                                    |                   |             
| 열  | 관 | 류  | 을                   | 계                                                                                                | 산 | 결 | 과  | 번호                                                                                                | 재 료 명             | 두께:D<br>(m) | 열전도율:λ<br>(W/m.K) | 열전도저항:r<br>(㎡.K/W) | 열관류율:K<br>(W/㎡.K) | 번호                | 재 료 명 | 두께:D<br>(m) | 열전도율:λ<br>(W/m.K) | 열전도저항:r<br>(㎡.K/W) | 열관류율:K<br>(W/㎡.K) | 번호 | 재 료 명 | 두께:D<br>(m) | 열전도율:λ<br>(W/m.K) | 열전도저항:r<br>(㎡.K/W) | 열관류율:K<br>(W/㎡.K) |  |  |  |  |  |
|    |   |    |                     |                                                                                                  |   |   |    | 1                                                                                                 | 실내표면열전달저항Ri       | -           | -                 | 0.086              | 1                 | 실내표면열전달저항Ri       | -     | -           | 0.086             |                    |                   |    |       |             |                   |                    |                   |  |  |  |  |  |
|    |   |    |                     |                                                                                                  |   |   |    | 2                                                                                                 | 시멘트물말(1:3) (산설)   | 0.047       | 1.400             | 0.034              | 2                 | 시멘트물말(1:3) (산설)   | 0.097 | 1.400       | 0.069             |                    |                   |    |       |             |                   |                    |                   |  |  |  |  |  |
|    |   |    |                     |                                                                                                  |   |   |    | 3                                                                                                 | PF보드 (산설)         | 0.050       | 0.020             | 2.500              | 3                 | PF보드 (산설)         | 0.050 | 0.020       | 2.500             |                    |                   |    |       |             |                   |                    |                   |  |  |  |  |  |
|    |   |    |                     |                                                                                                  |   |   |    | 4                                                                                                 | 콘크리트(1:2:4) (기준)  | 0.150       | 1.600             | 0.094              | 4                 | 콘크리트(1:2:4) (기준)  | 0.150 | 1.600       | 0.094             |                    |                   |    |       |             |                   |                    |                   |  |  |  |  |  |
|    |   |    |                     |                                                                                                  |   |   |    | 5                                                                                                 | 비드넵보온판 2중 1호 (기준) | 0.050       | 0.031             | 1.613              | 5                 | 비드넵보온판 2중 1호 (기준) | 0.050 | 0.031       | 1.613             |                    |                   |    |       |             |                   |                    |                   |  |  |  |  |  |
|    |   |    |                     |                                                                                                  |   |   |    | 6                                                                                                 | 실외표면열전달저항Ro       | -           | -                 | 0.150              | 6                 | 실외표면열전달저항Ro       | -     | -           | 0.150             |                    |                   |    |       |             |                   |                    |                   |  |  |  |  |  |
|    |   
# 단열재의 등급  
 "가" 등급 : 열전도율이 0.034 W/mK(0.029 kcal/mh°C)이하인 경우  
 "나" 등급 : 열전도율이 0.035 ~ 0.040 W/mK(0.030~0.034 kcal/mh°C) 이하인 경우  
 "다" 등급 : 열전도율이 0.041 ~ 0.046 W/mK(0.035~0.039 kcal/mh°C) 이하인 경우  
 "라" 등급 : 열전도율이 0.047 ~ 0.051 W/mK(0.040~0.044 kcal/mh°C) 이하인 경우

# 방습층 (투습도가 24시간당 30g/m2 이하 또는 투습계수 0.28g/m2.h.mmHg 이하의 투습저항을 가진층) 으로 인정될 수 있는 재료 또는 구조일것.

# 바닥난방에서 단열재의 설치  
 가. 바닥난방 부위에 설치되는 단열재는 바닥난방의 열이 슬래브 하부 및 측벽으로 손실되는 것을 막을 수 있도록 온수배관 (전기난방인 경우는 발열선) 하부와 슬래브 사이에 설치하고, 온수배관 (전기난방인 경우는 발열선) 하부와 슬래브 사이에 설치되는 구성 재료의 열저항의 합계는 층간 바닥인 경우에는 해당 바닥에 요구되는 총열관류저항(별표1에서 제시되는 열관류율의 역수)의 60% 이상 최하층 바닥인 경우에는 70% 이상이 되어야 한다. 다만, 바닥난방을 하는 욕실 및 현관부위와 슬래브의 측벽을 직접 이용하는 심야전기이용 온돌 등 (한국전력의 심야전력이용기기 승인을 받은 것에 한한다)의 경우에는 단열재의 위치가 그러하지 않을 수 있다.

# 기밀 및 결로방지 등을 위한 조치  
 가. 벽체 내표면및 내부에서의 결로를 방지하고 단열재의 성능저하를 방지하기 위하여 규칙 제21조 규정에 의하여 단열조치를 하여야 하는 하는 부위(창호 및 공동주택 층간바닥제외)에는 방습층을 단열재의 실내측에 설치 하여야 한다.

나. 방습층 및 단열재가 이어지는 부위 및 단부는 이음 및 단부를 통한 투습을 방지할수 있도록 다음과 같이 조치하여야 한다.  
 1) 단열재의 이음부는 최대한 밀착하여 시공하거나 2장을 엇갈리게 시공하여 이음부를 통한 단열성능 저하가 최소화될 수 있도록 조치할것.  
 2) 방습층으로 알루미늄박 또는 플라스틱 필름 등을 사용할 경우의 이음부는 100mm 이상 중첩하고 내습성 테이프, 접착제 등으로 기밀하게 마감할것.  
 3) 단열부위가 만나는 모서리 부위는 방습층 및 단열재가 이어짐이 없이 시공하거나 이어질경우 이음부를 통한 단열성능 저하가 최소화 되도록 하며, 알루미늄박 또는 플라스틱계 필름 등을 사용할 경우의 모서리 이음부는 150mm이상 중첩되게 시공하고 내습성 테이프, 접착제 등으로 기밀하게 마감할것.  
 4) 방습층의 단부는 단부를 통한 투습이 발생하지 않도록 내습성 테이프, 접착제 등으로 기밀하게 마감할것.  
 다. 건축물 외피 단열부위의 접합부, 틈 등은 밀폐될수 있도록 코킹과 가스켓등을 사용하여 기밀하게 처리하여야 한다.  
 라. 외기에 직접 면하고 1층 또는 지상으로 연결된 출입문은 제5조제9호 아목에 따른 방풍구조로 하여야 한다. 다만, 다음 각 호에 해당하는 경우에는 그러하지 않을 수 있다.  
 1) 바닥면적 3백 제곱미터 이하의 개별 점포의 출입문  
 2) 주택의 출입문(단, 기숙사는 제외)  
 3) 사람의 통행을 주 목적으로 하지 않는 출입문  
 4) 너비 1.2미터 이하의 출입문  
 마. 방풍구조를 설치하여야 하는 출입문에서 회전문과 일반문이 같이 설치되어진 경우, 일반문 부위는 방풍실 구조의 이중문을 설치하여야 한다.  
 바. 건축물의 거실의 창호가 외기에 직접 면하는 부위인 경우에는 제5조 제9호 자목에 따른 기밀성 창호를 설치하여야 한다.

PROJECT TITLE

리를 포레스트  
봉뜨락 조성사업

PROJECT NO

NOTE

KEY PLAN

DESIGN CORP.

**이음** (주)이음건축사사무소

ADD. 대구광역시 중구 장동로 81, 5F  
TEL. 053.716.0776 FAX. 0505.720.0776  
E-mail. e-ul2020@naver.com  
Web. eul2020 / 0776

APPROVED BY  
대표이사/건축사 권오섭

CHECKED BY

DRAWN BY





DATE  
2023. 04.


DRAWING TITLE  
형별성능관계내역-2

SCALE  
A3 : 1/ 20

DRAWING NO.  
A01-902


## # 지역별 형별 성능 관계 내역 - 3 (중부1지역)
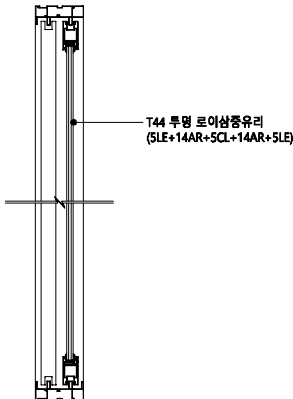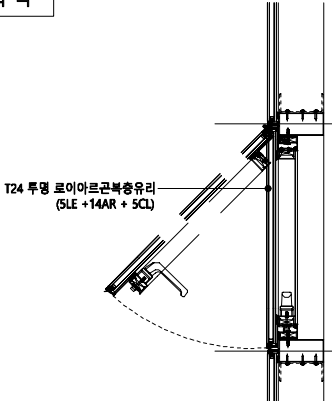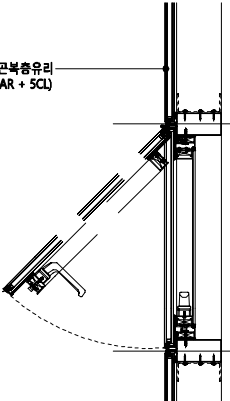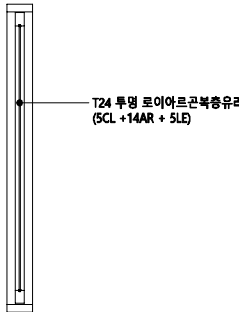
| 구분                                   | AW1            | 창 (외 기 직 접 / 창 틀 포 함) |                                                                                     |                                                                      | AW2        | 창 (외 기 직 접 / 창 틀 포 함) |                                                                                    |       | AW3                                          | 창 (외 기 직 접 / 창 틀 포 함) |                                                                                     |                   |                |   |          |  |     |
|--------------------------------------|----------------|-----------------------|-------------------------------------------------------------------------------------|----------------------------------------------------------------------|------------|-----------------------|------------------------------------------------------------------------------------|-------|----------------------------------------------|-----------------------|-------------------------------------------------------------------------------------|-------------------|----------------|---|----------|--|-----|
| 단<br>면<br>구<br>조                     |                | 외 측                   |                                                                                     | 내 측                                                                  |            | 외 측                   |                                                                                    | 내 측   |                                              | 외 측                   |                                                                                     | 내 측               |                | # 단열재의 등급<br>"가" 등급 : 열전도율이 0.034 W/mK(0.029 kcal/mh℃)이하인 경우<br>"나" 등급 : 열전도율이 0.035 ~ 0.040 W/mK(0.030~0.034 kcal/mh℃) 이하인 경우<br>"다" 등급 : 열전도율이 0.041 ~ 0.046 W/mK(0.035~0.039 kcal/mh℃) 이하인 경우<br>"라" 등급 : 열전도율이 0.047 ~ 0.051 W/mK(0.040~0.044 kcal/mh℃) 이하인 경우<br><br># 방습층 (투습도가 24시간당 30g/m2 이하 또는 투습계수 0.28g/m2.h.mmHg 이하의 투습저항을 가진층) 으로 인정될 수 있는 재료 또는 구조일것.<br><br># 바닥난방에서 단열재의 설치<br>가. 바닥난방 부위에 설치되는 단열재는 바닥난방의 열이 슬래브 하부 및 측벽으로 손실되는 것을 막을 수 있도록 온수배관 (전기난방인 경우는 발열선) 하부와 슬래브 사이에 설치하고, 온수배관 (전기난방인 경우는 발열선) 하부와 슬래브 사이에 설치되는 구성 재료의 열저항의 합계는 층간 바닥인 경우에는 해당 바닥에 요구되는 총열관류저항(별표1에서 제시되는 열관류율의 역수)의 60% 이상 최하층 바닥인 경우에는 70% 이상이 되어야 한다. 다만, 바닥난방을 하는 욕실 및 현관부위와 슬래브의 측벽을 직접 이용하는 심야전기이용 온돌 등 (한국전력의 심야전력이용기기 승인을 받은 것에 한한다)의 경우에는 단열재의 위치가 그러하지 않을 수 있다.<br><br># 기밀 및 결로방지 등을 위한 조치<br>가. 벽체 내표면및 내부에서의 결로를 방지하고 단열재의 성능저하를 방지하기 위하여 규칙 제21조 규정에 의하여 단열조치를 하여야 하는 하는 부위(창호 및 공동주택 층간바닥제외)에는 방습층을 단열재의 실내측에 설치 하여야 한다.<br>나. 방습층 및 단열재가 이어지는 부위 및 단부는 이음 및 단부를 통한 투습을 방지할수 있도록 다음과 같이 조치하여야 한다.<br>1) 단열재의 이음부는 최대한 밀착하여 시공하거나 2장을 잇갈리게 시공하여 이음부를 통한 단열성능 저하가 최소화될 수 있도록 조치할것.<br>2) 방습층으로 알루미늄박 또는 플라스틱 필름 등을 사용할 경우의 이음부는 100mm 이상 중첩하고 내습성 테이프, 접착제 등으로 기밀하게 마감할것.<br>3) 단열부위가 만나는 모서리 부위는 방습층 및 단열재가 이어짐이 없이 시공하거나 이어질경우 이음부를 통한 단열성능 저하가 최소화 되도록 하며, 알루미늄박 또는 플라스틱계 필름 등을 사용할 경우의 모서리 이음부는 150mm이상 중첩되게 시공하고 내습성 테이프, 접착제 등으로 기밀하게 마감할것.<br>4) 방습층의 단부는 단부를 통한 투습이 발생하지 않도록 내습성 테이프, 접착제 등으로 기밀하게 마감할것.<br>다. 건축물 외피 단열부위의 접합부, 틈 등은 밀폐될수 있도록 코킹과 가스켓등을 사용하여 기밀하게 처리하여야 한다.<br>라. 외기에 직접 면하고 1층 또는 지상으로 연결된 출입문은 제5조제9호 아목에 따른 방풍구조로 하여야 한다. 다만, 다음 각 호에 해당하는 경우에는 그러하지 않을 수 있다.<br>1) 바닥면적 3백 제곱미터 이하의 개별 점포의 출입문<br>2) 주택의 출입문(단, 기숙사는 제외)<br>3) 사람의 통행을 주목적으로 하지 않는 출입문<br>4) 너비 1.2미터 이하의 출입문<br>마. 방풍구조를 설치하여야 하는 출입문에서 회전문과 일반문이 같이 설치되어진 경우, 일반문 부위는 방풍실 구조의 이중문을 설치하여야 한다.<br>바. 건축물의 거실의 창호가 외기에 직접 면하는 부위인 경우에는 제5조 제9호 자목에 따른 기밀성 창호를 설치하여야 한다. |          |  |     |
|                                      | * 시험성적서 참조     |                       |    |                                                                      | * 시험성적서 참조 |                       |  |       | * 시험성적서 참조                                   |                       |  |                   |                |   |          |  |     |
| 열<br>관<br>류<br>을<br>계<br>산<br>결<br>과 | 번호             | 구 분                   |                                                                                     | 내 용                                                                  |            | 번호                    | 구 분                                                                                |       | 내 용                                          |                       | 번호                                                                                  | 구 분               |                | 내 용   |          |  |     |
|                                      | 1              | 두 겹                   |                                                                                     | 로이 5mm(SKN145II(H/S)) + 아르곤 14mm + 일반 5mm 아르곤 14mm + 로이 5mm(PLA ONE) |            | 1                     | 두 겹                                                                                |       | 로이 5mm(소프트XTN145II(H/S)) + 아르곤 14mm + 일반 5mm |                       | 1                                                                                   | 두 겹               |                | 로이 5mm(소프트XTN145II(H/S)) + 아르곤 14mm + 일반 5mm   |          |  |     |
|                                      | 2              | 종 류                   |                                                                                     | 미서기창, 아르곤 주입+로이유리(소프트코팅)                                             |            | 2                     | 종 류                                                                                |       | 프로젝트창, 아르곤 주입+로이유리(소프트코팅)                    |                       | 2                                                                                   | 종 류               |                | FIX창, 아르곤 주입+로이유리(소프트코팅)   |          |  |     |
|                                      | 3              | 프 레 임                 |                                                                                     | 금속재(열교차단재 적용)                                                        |            | 3                     | 프 레 임                                                                              |       | 금속재(열교차단재 적용)                                |                       | 3                                                                                   | 프 레 임             |                | 금속재(열교차단재 적용)   |          |  |     |
|                                      | 4              | 기밀성 등급(KS F 2292)     |                                                                                     | 1 등급 (1 m³/hm²미만)                                                    |            | 4                     | 기밀성 등급(KS F 2292)                                                                  |       | 1 등급 (1 m³/hm²미만)                            |                       | 4                                                                                   | 기밀성 등급(KS F 2292) |                | 1 등급 (1 m³/hm²미만)   |          |  |     |
|                                      |                |                       |                                                                                     |                                                                      |            |                       |                                                                                    |       |                                              |                       |                                                                                     |                   |                |   |          |  |     |
|                                      | 적용열관류율(W/m².K) |                       | 0.979                                                                               |                                                                      |            | 적용열관류율(W/m².K)        |                                                                                    | 1.174 |                                              |                       | 적용열관류율(W/m².K)                                                                      |                   | 1.133          |   |          |  |     |
|                                      | 기준열관류율(W/m².K) |                       | 1.300 이하                                                                            |                                                                      | 중부1        |                       | 기준열관류율(W/m².K)                                                                     |       | 1.300 이하                                     |                       | 중부1                                                                                 |                   | 기준열관류율(W/m².K) |   | 1.300 이하 |  | 중부1 |
| 구분                                   | AD1            | 문 (외 기 직 접 / 문 틀 포 함) |                                                                                     |                                                                      |            |                       |                                                                                    |       |                                              |                       |                                                                                     |                   |                |   |          |  |     |
| 단<br>면<br>구<br>조                     |                | 외 측                   |                                                                                     | 내 측                                                                  |            |                       |                                                                                    |       |                                              |                       |                                                                                     |                   |                |   |          |  |     |
|                                      | * 시험성적서 참조     |                       |  |                                                                      |            |                       |                                                                                    |       |                                              |                       |                                                                                     |                   |                |   |          |  |     |
| 열<br>관<br>류<br>을<br>계<br>산<br>결<br>과 | 번호             | 구 분                   |                                                                                     | 내 용                                                                  |            | 번호                    | 구 분                                                                                |       | 내 용                                          |                       | 번호                                                                                  | 구 분               |                | 내 용   |          |  |     |
|                                      | 1              | 두 겹                   |                                                                                     | 일반 5mm + 아르곤 14mm (SWS) + 로이 5mm (PLA ONE)                           |            |                       |                                                                                    |       |                                              |                       |                                                                                     |                   |                |   |          |  |     |
|                                      | 2              | 종 류                   |                                                                                     | 여닫이문, 아르곤 주입+로이유리(소프트코팅)                                             |            |                       |                                                                                    |       |                                              |                       |                                                                                     |                   |                |   |          |  |     |
|                                      | 3              | 프 레 임                 |                                                                                     | 금속재(열교차단재 적용)                                                        |            |                       |                                                                                    |       |                                              |                       |                                                                                     |                   |                |   |          |  |     |
|                                      | 4              | 기밀성 등급(KS F 2292)     |                                                                                     | 1 등급 (1 m³/hm²미만)                                                    |            |                       |                                                                                    |       |                                              |                       |                                                                                     |                   |                |   |          |  |     |
|                                      |                |                       |                                                                                     |                                                                      |            |                       |                                                                                    |       |                                              |                       |                                                                                     |                   |                |   |          |  |     |
|                                      | 적용열관류율(W/m².K) |                       | 1.277                                                                               |                                                                      |            | 적용열관류율(W/m².K)        |                                                                                    |       |                                              |                       | 적용열관류율(W/m².K)                                                                      |                   |                |   |          |  |     |
|                                      | 기준열관류율(W/m².K) |                       | 1.500 이하                                                                            |                                                                      | 중부1        |                       | 기준열관류율(W/m².K)                                                                     |       |                                              |                       |                                                                                     | 기준열관류율(W/m².K)    |                |   |          |  |     |

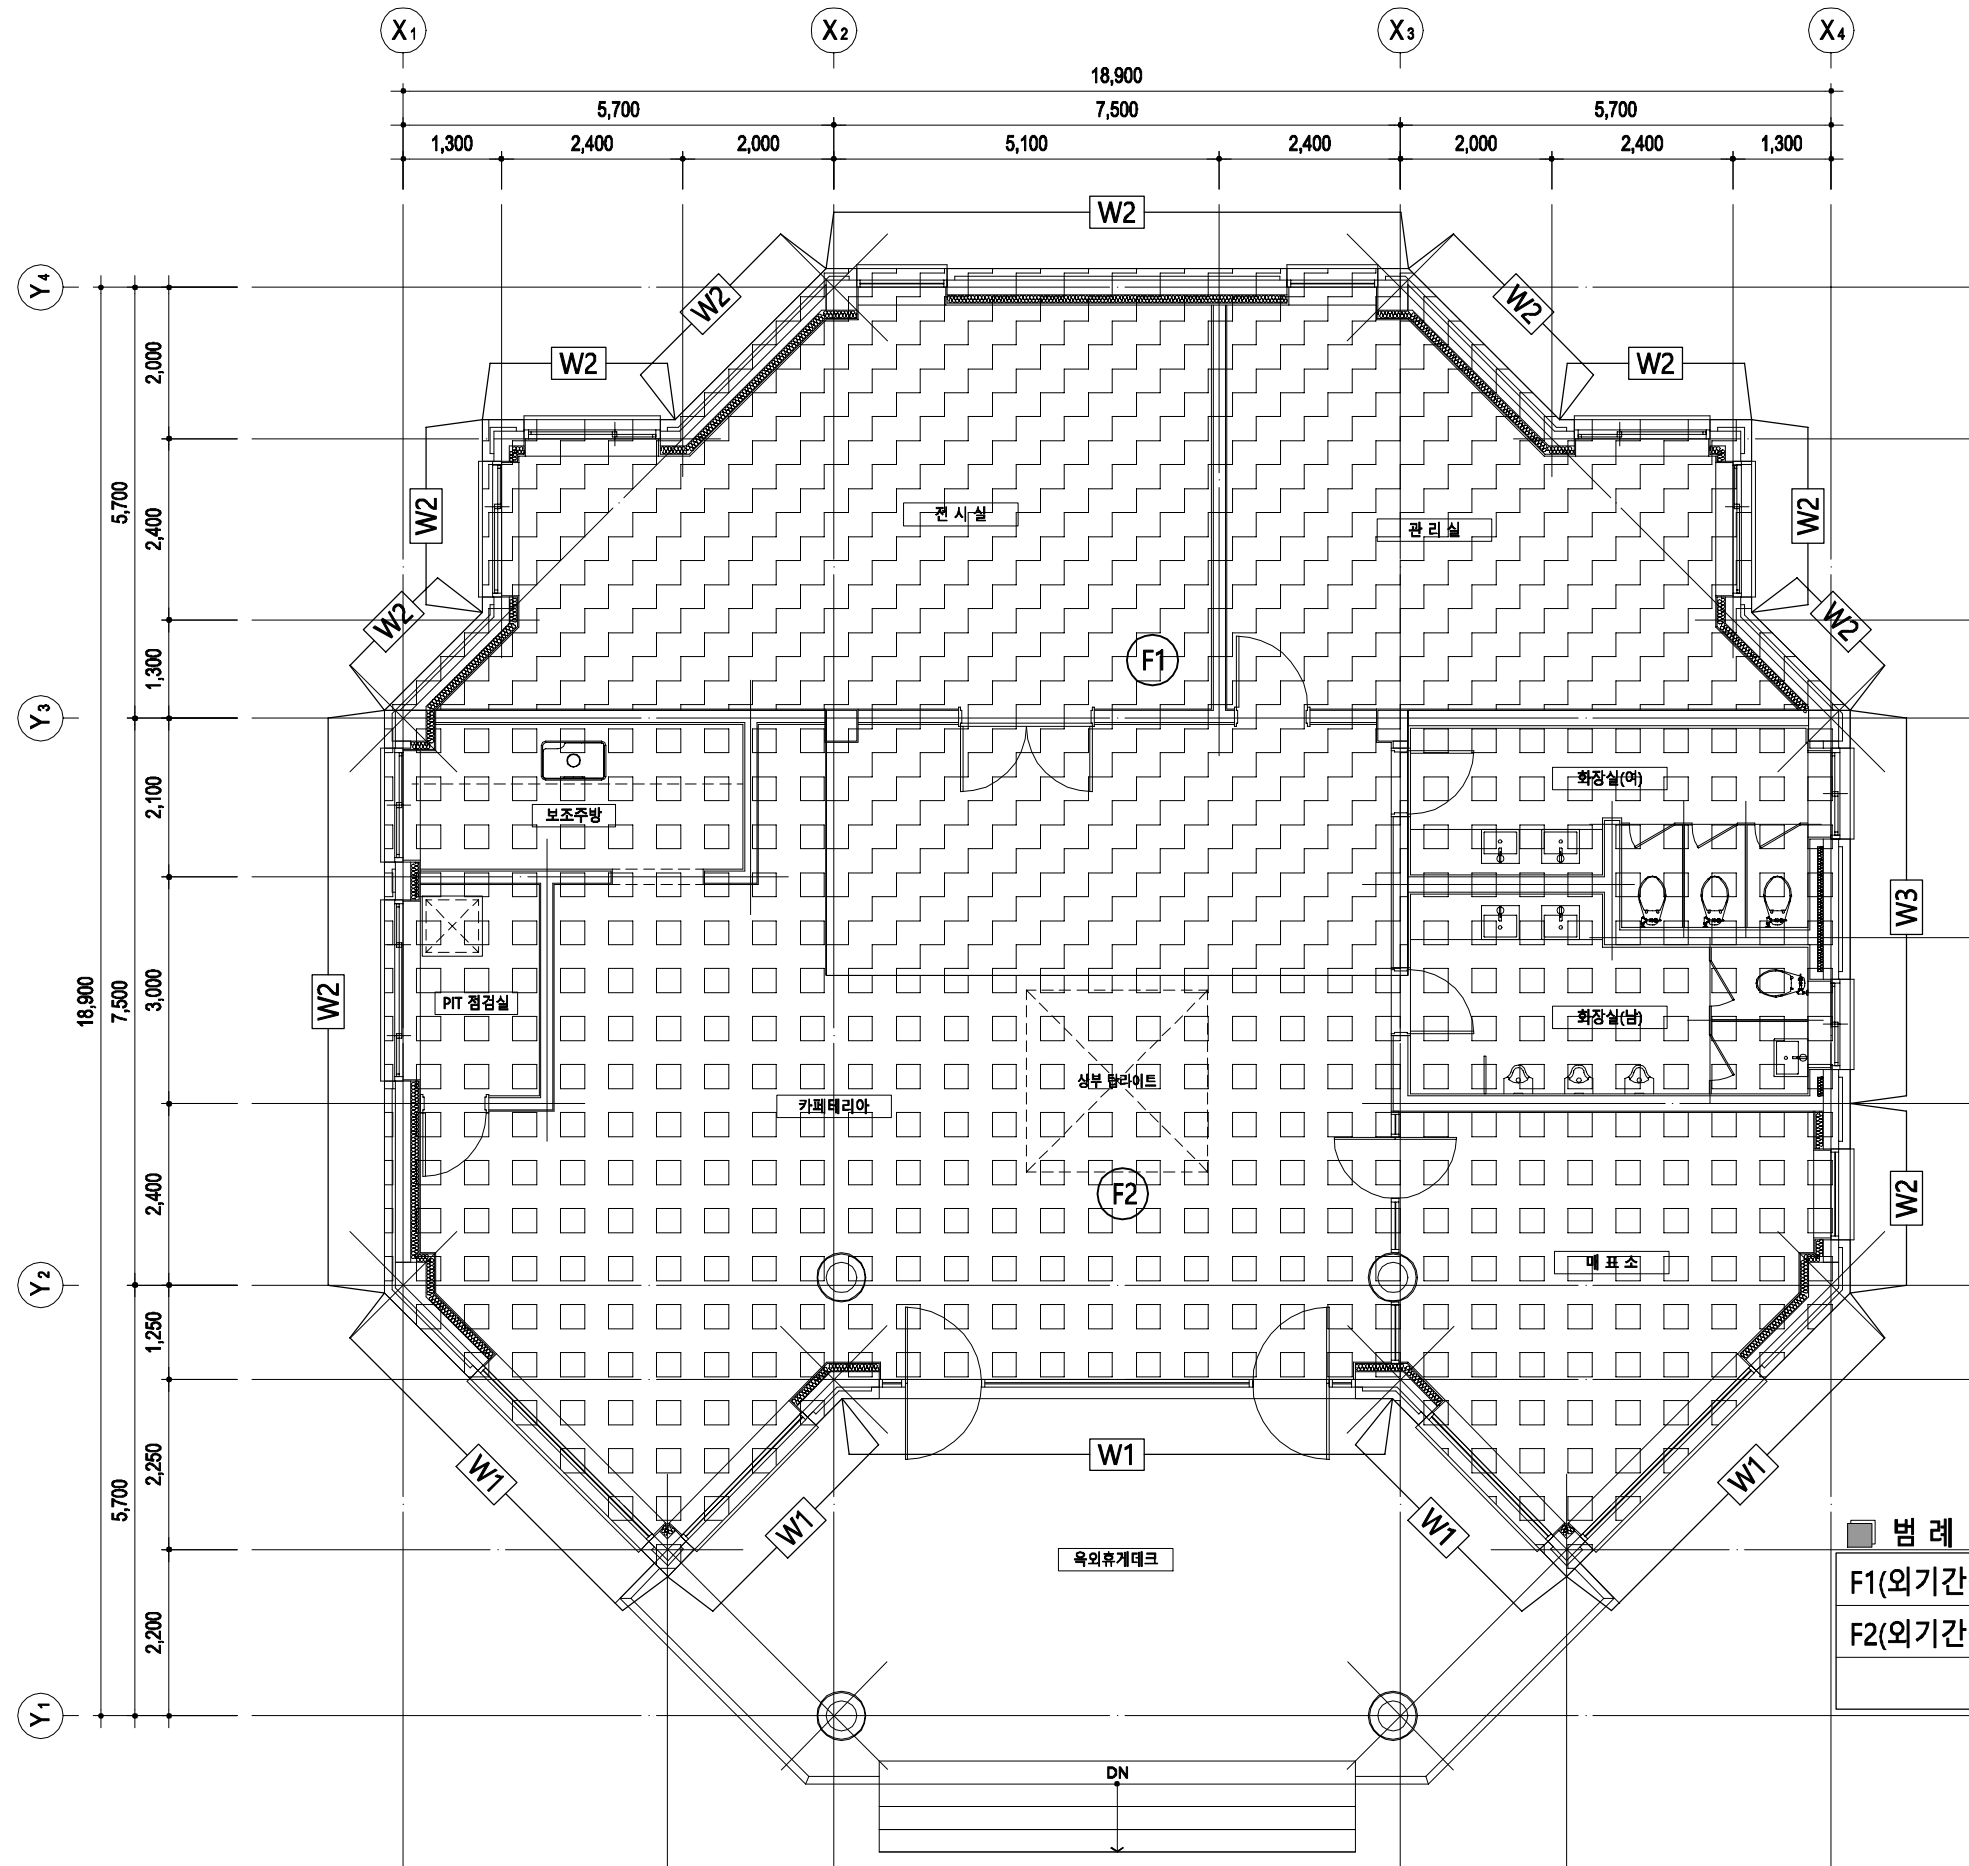

| 범례       |                                  |           |               |  |
|----------|----------------------------------|-----------|---------------|--|
| F1(외기간접) | T50 PF보드(신설)<br>T50 비드벌 2종1호(기존) | 외기에 간접 노출 | 면적: 112.74 m2 |  |
| F2(외기간접) | T50 PF보드(신설)<br>T50 비드벌 2종1호(기존) | 외기에 간접 노출 | 면적: 158.61 m2 |  |

지상1층 바닥 및 외벽 단열 위치도

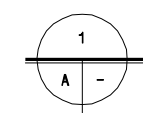

축척 A1:1/50, A3:1/100

PROJECT TITLE  
리틀 포레스트  
봉뜨락 조성사업

PROJECT NO

NOTE

KEY PLAN

DESIGN CORP.  
**이원** (주)이원건축사사무소  
ADD. 대구광역시 중구 장동로 81, 5F  
TEL. 053.716.0776 FAX. 0505.720.0776  
E-mail. e-ul2020@naver.com  
Web. eul2020 / 0776

APPROVED BY  
대표이사/건축사 권오섭

CHECKED BY


DRAWN BY

DATE  
2023. 04.

DRAWING TITLE  
지상1층 바닥 및  
외벽 단열 위치도

SCALE  
A3 : 1/ 100

DRAWING NO.  
A01-904

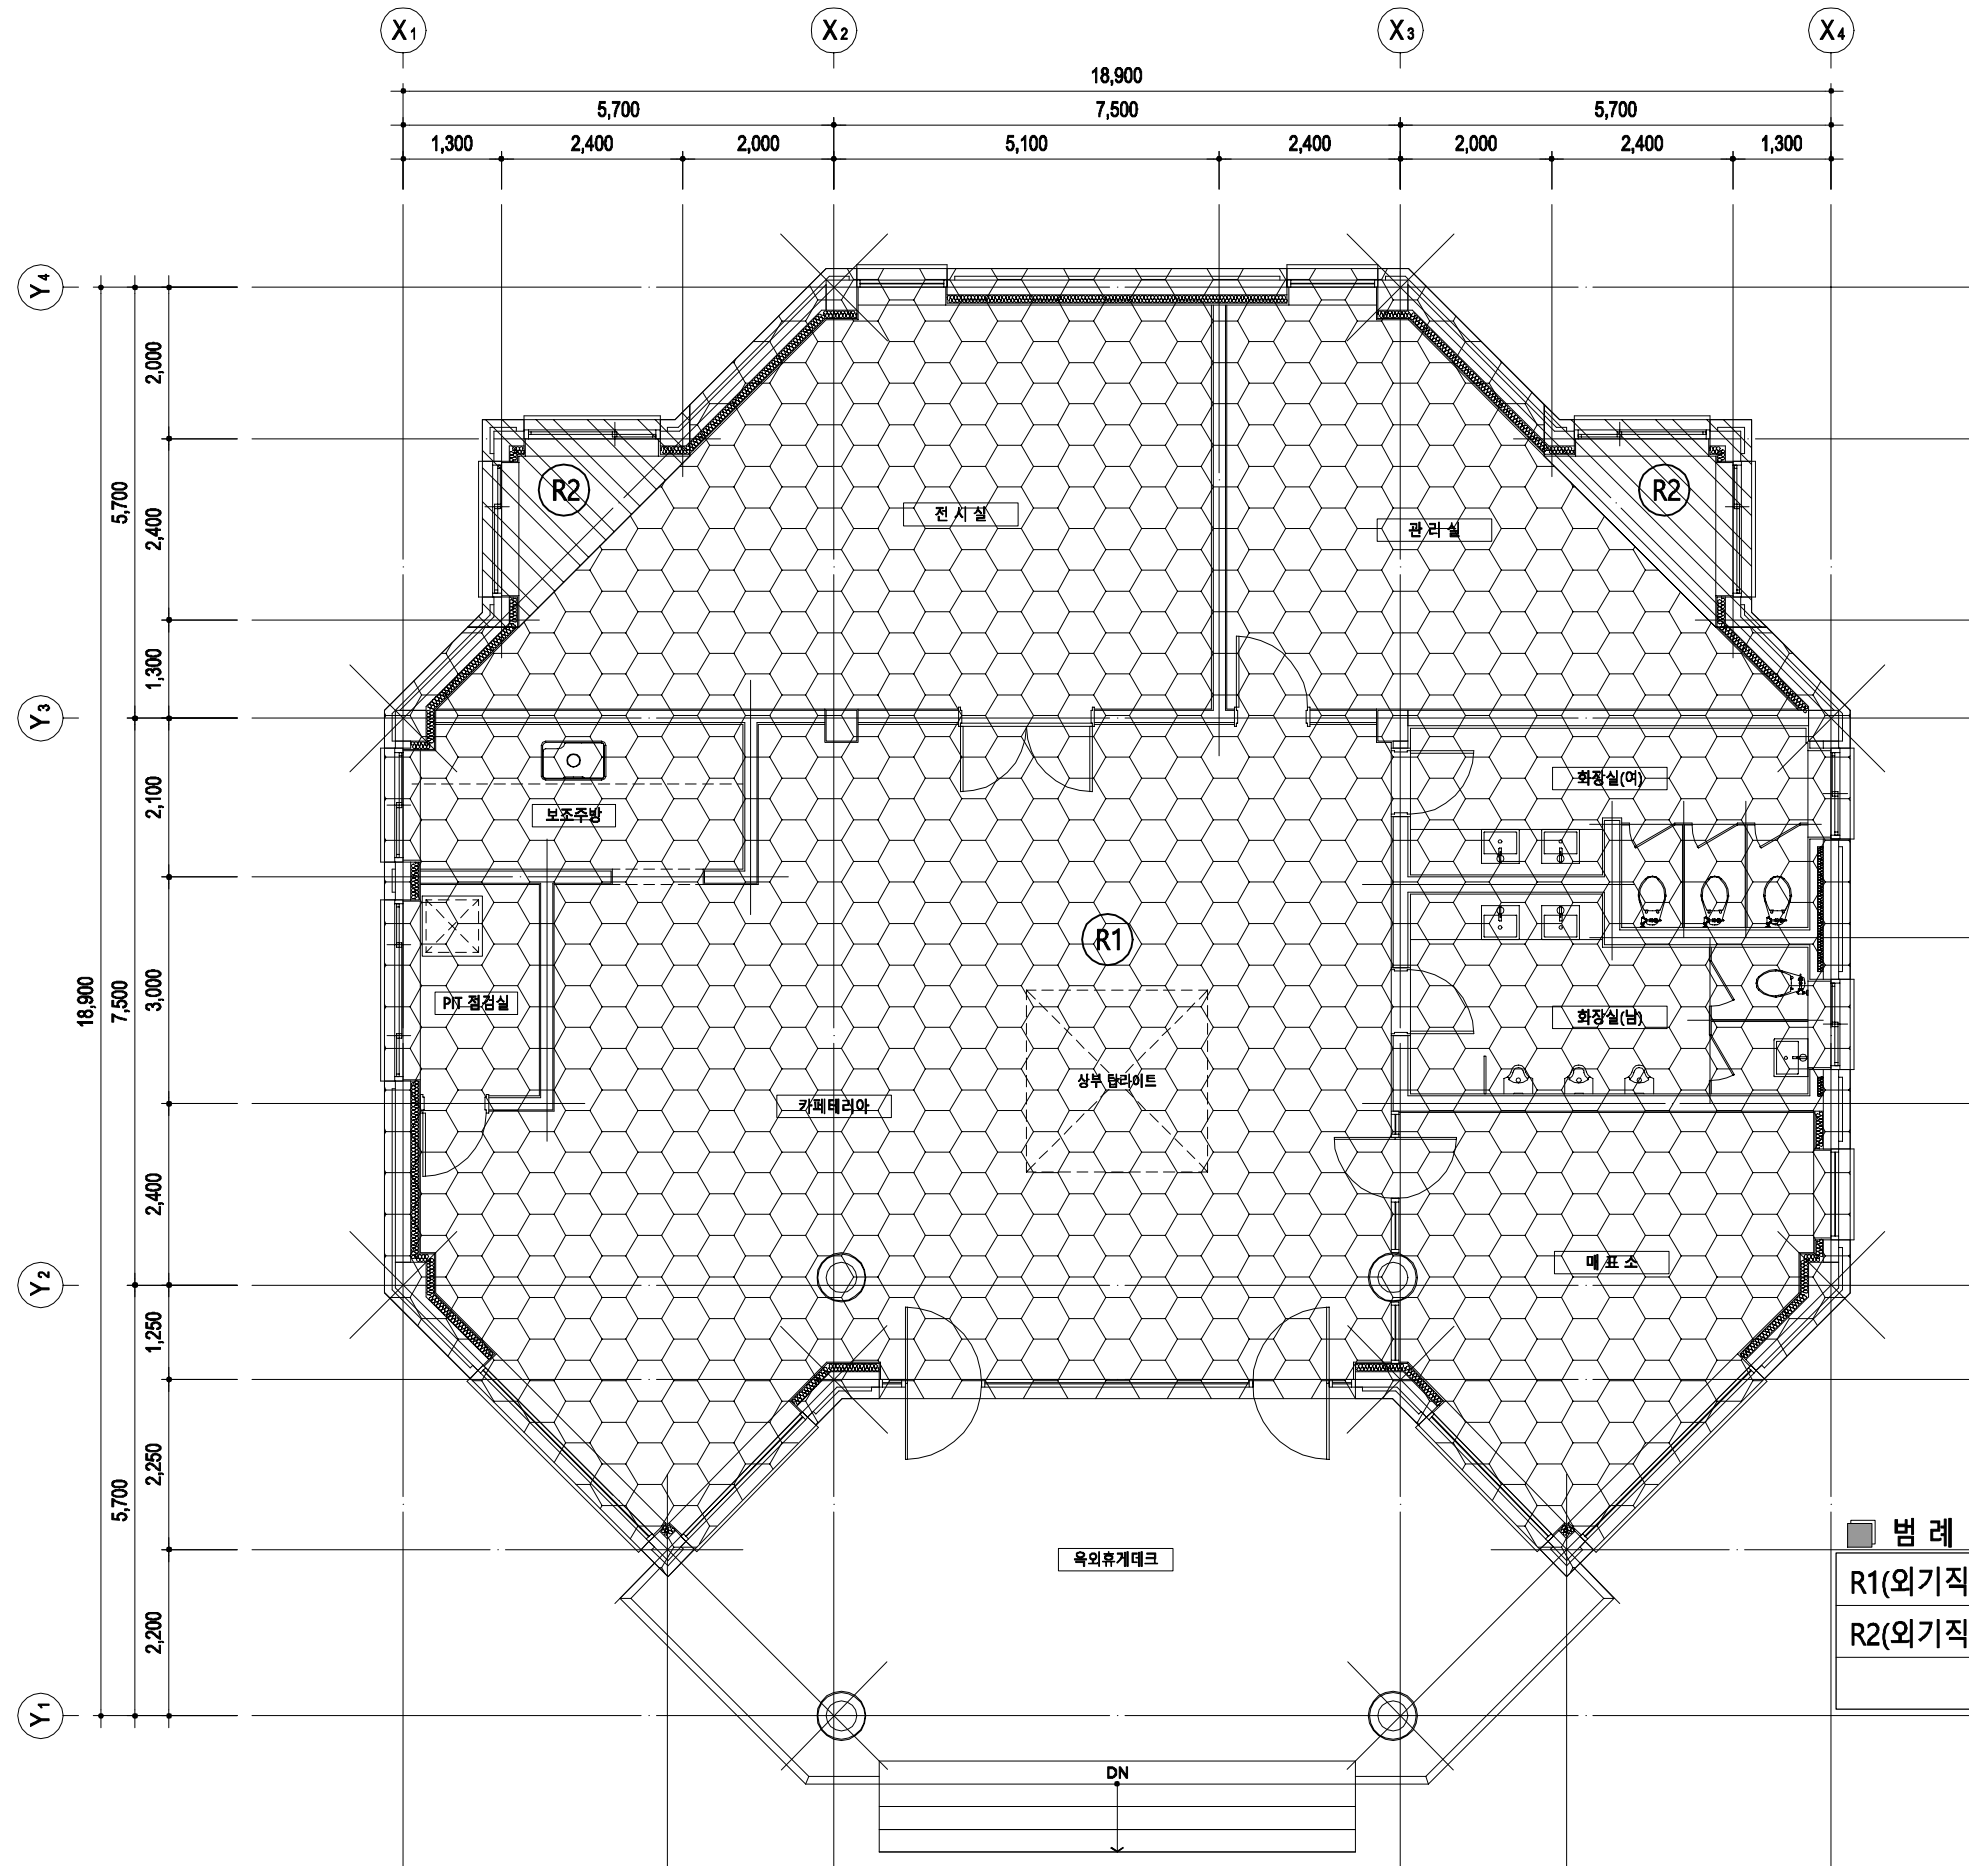

|          |                                        |           |               |  |
|----------|----------------------------------------|-----------|---------------|--|
| 범례       |                                        |           |               |  |
| R1(외기직접) | T100 비드법 2종1호(기준)<br>T100 비드법 2종1호(신설) | 외기에 직접 노출 | 면적: 261.31 m2 |  |
| R2(외기직접) | T100 비드법 2종1호(기준)<br>T70 PF보드(신설)      | 외기에 직접 노출 | 면적: 10.04 m2  |  |
|          |                                        |           |               |  |

지붕 단열 위치도

축척 A1:1/50, A3:1/100

PROJECT TITLE

리틀 포레스트  
봉뜨락 조성사업

PROJECT NO

NOTE

KEY PLAN

DESIGN CORP.

(주)이울건축사사무소

ADD. 대구광역시 중구 장동로 81, 5F  
TEL. 053.716.0776 FAX. 0505.720.0776  
E-mail. e-ul2020@naver.com  
Web. eul2020 / 0776

APPROVED BY

대표이사 / 건축사 권오섭

CHECKED BY

DRAWN BY

DATE

2023. 04.

DRAWING TITLE



지붕 단열 위치도

SCALE

A3 : 1/ 100

DRAWING NO.

A01-905

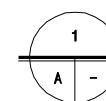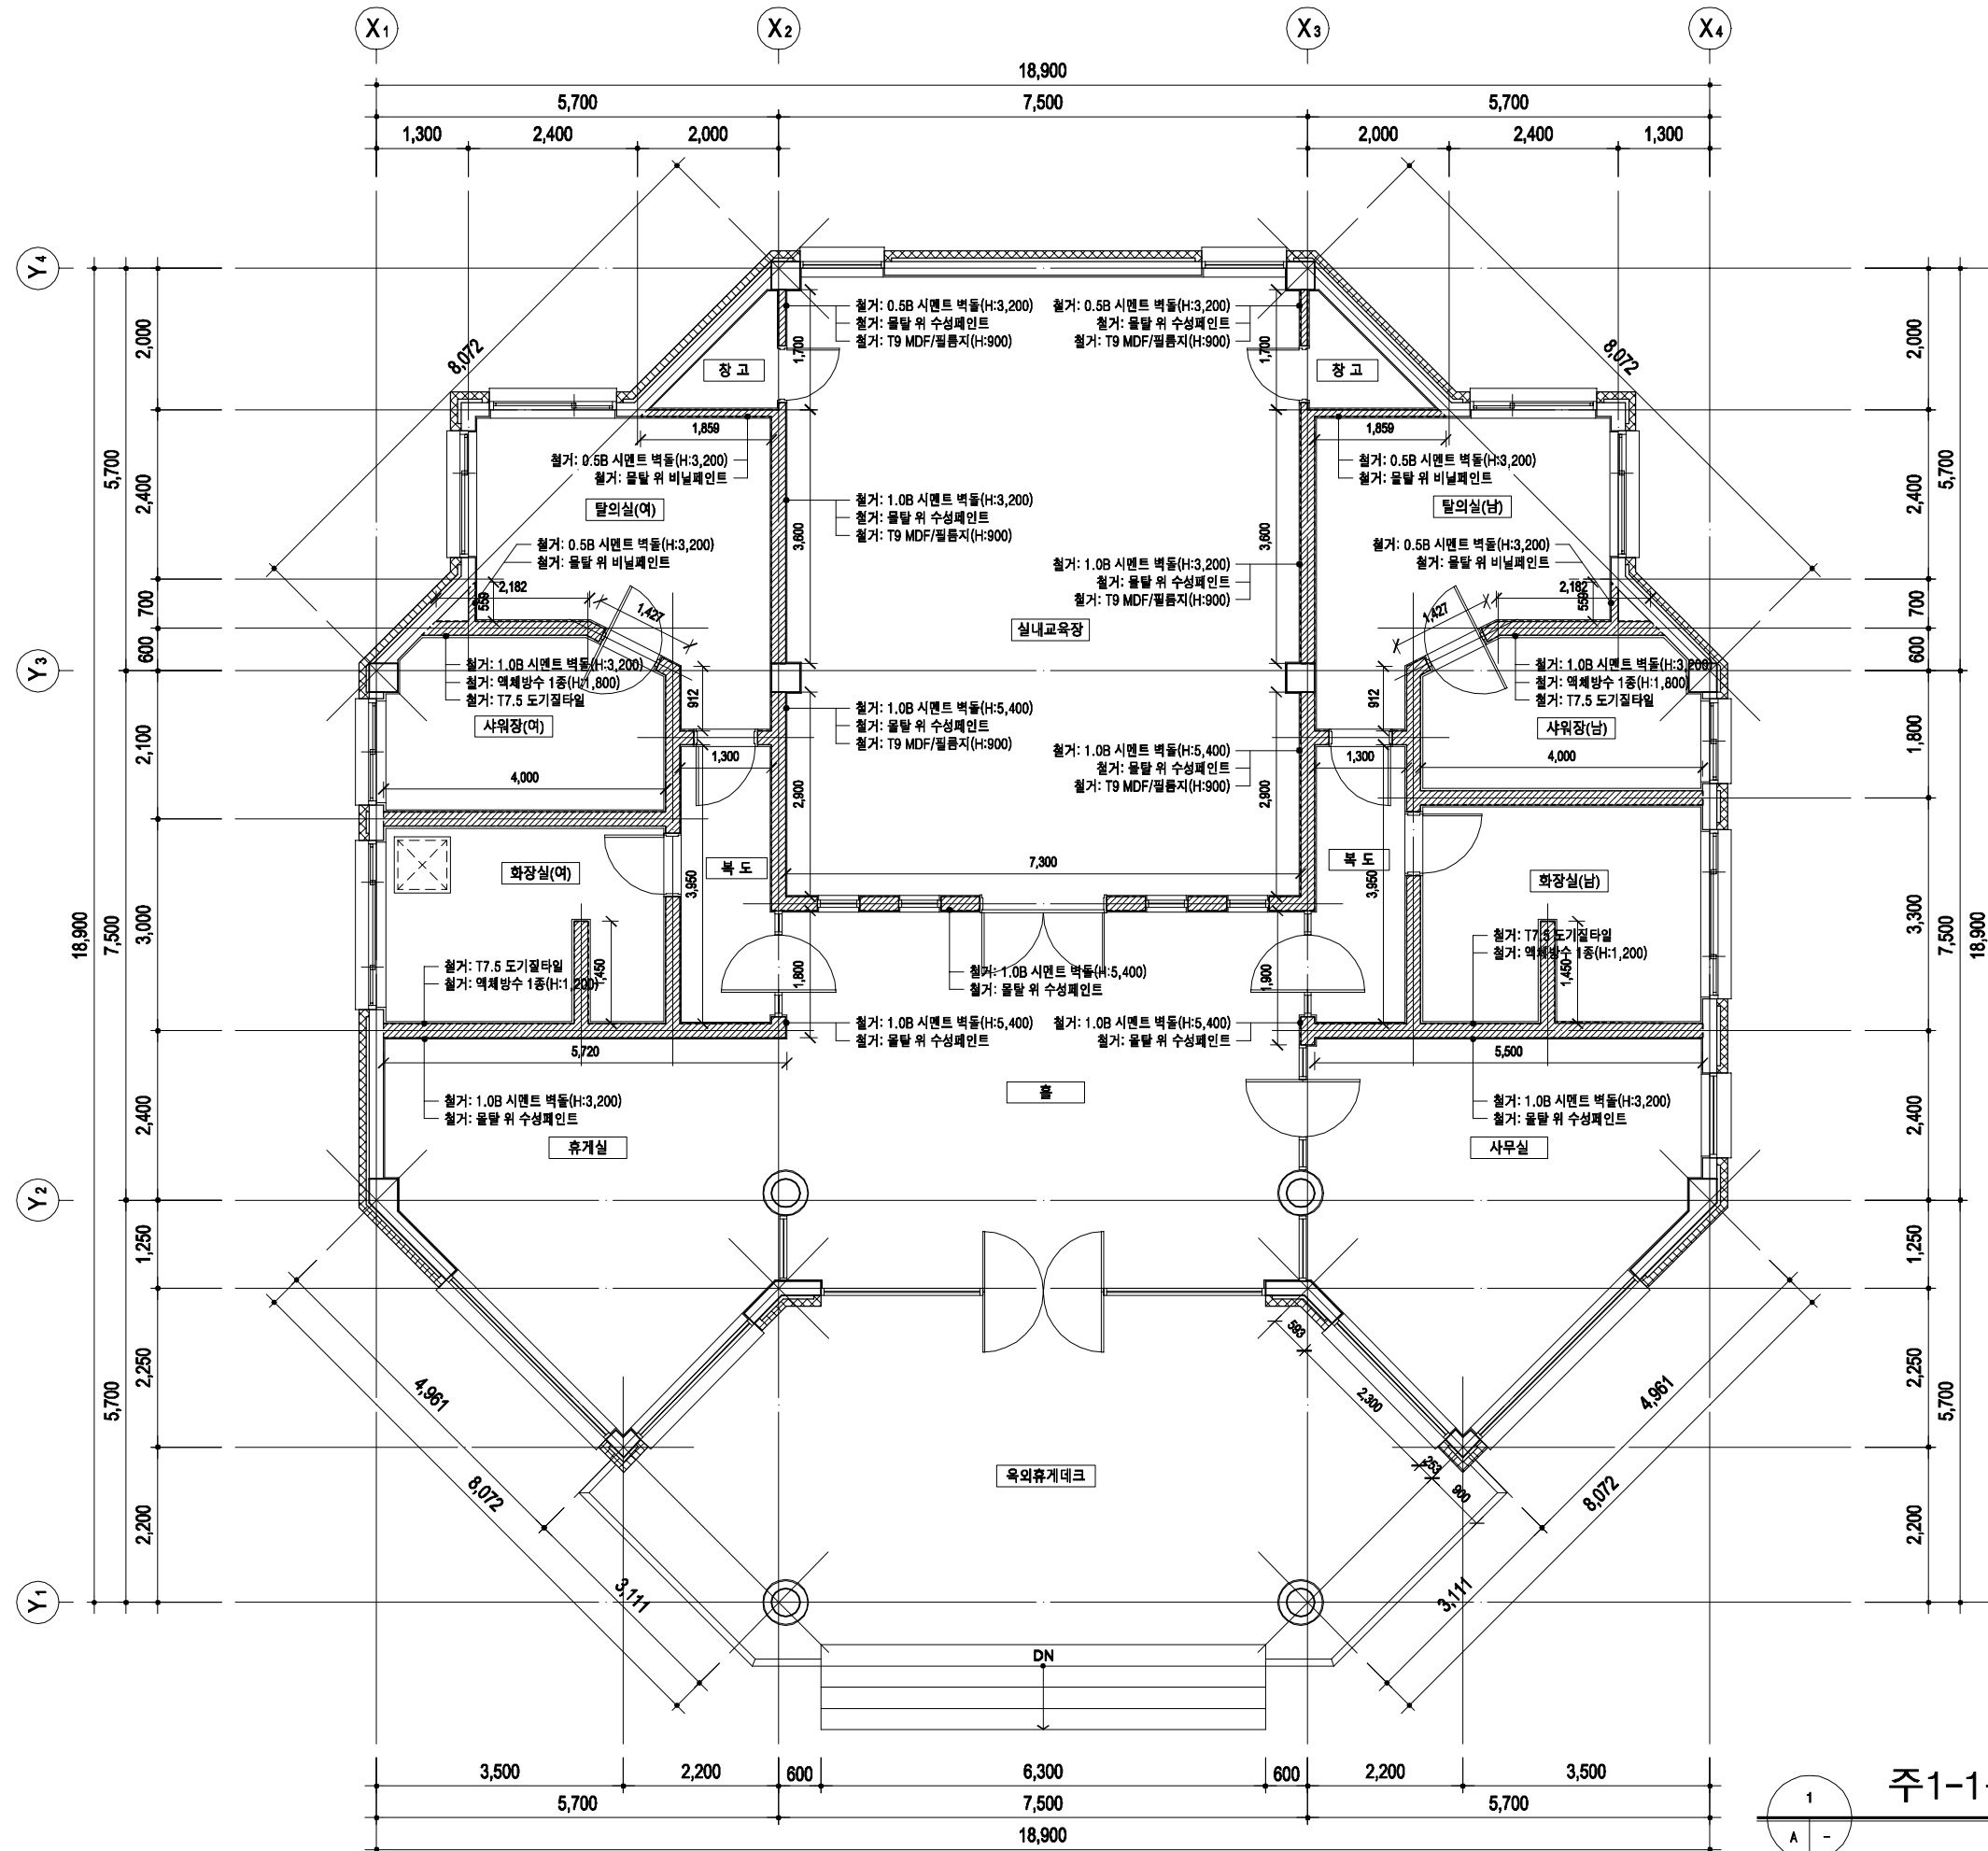

주1-1층 벽체평면도(철거)

축척 A1:1/50, A3:1/100

PROJECT TITLE

리틀 포레스트  
봉뜨락 조성사업

PROJECT NO

NOTE

KEY PLAN

DESIGN CORP.

**이음** (주)이음건축사사무소

ADD. 대구광역시 중구 장동로 81, 5F  
TEL. 053.716.0776 FAX. 0505.720.0776  
E-mail. e-ul2020@naver.com  
Web. eul2020 / 0776

APPROVED BY  
대표이사/건축사 권오섭

CHECKED BY



DRAWN BY

DATE 2023. 04.

DRAWING TITLE  
주1-1층 벽체평면도  
(철거)

SCALE A3 : 1/ 100



DRAWING NO. A01- 1001

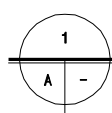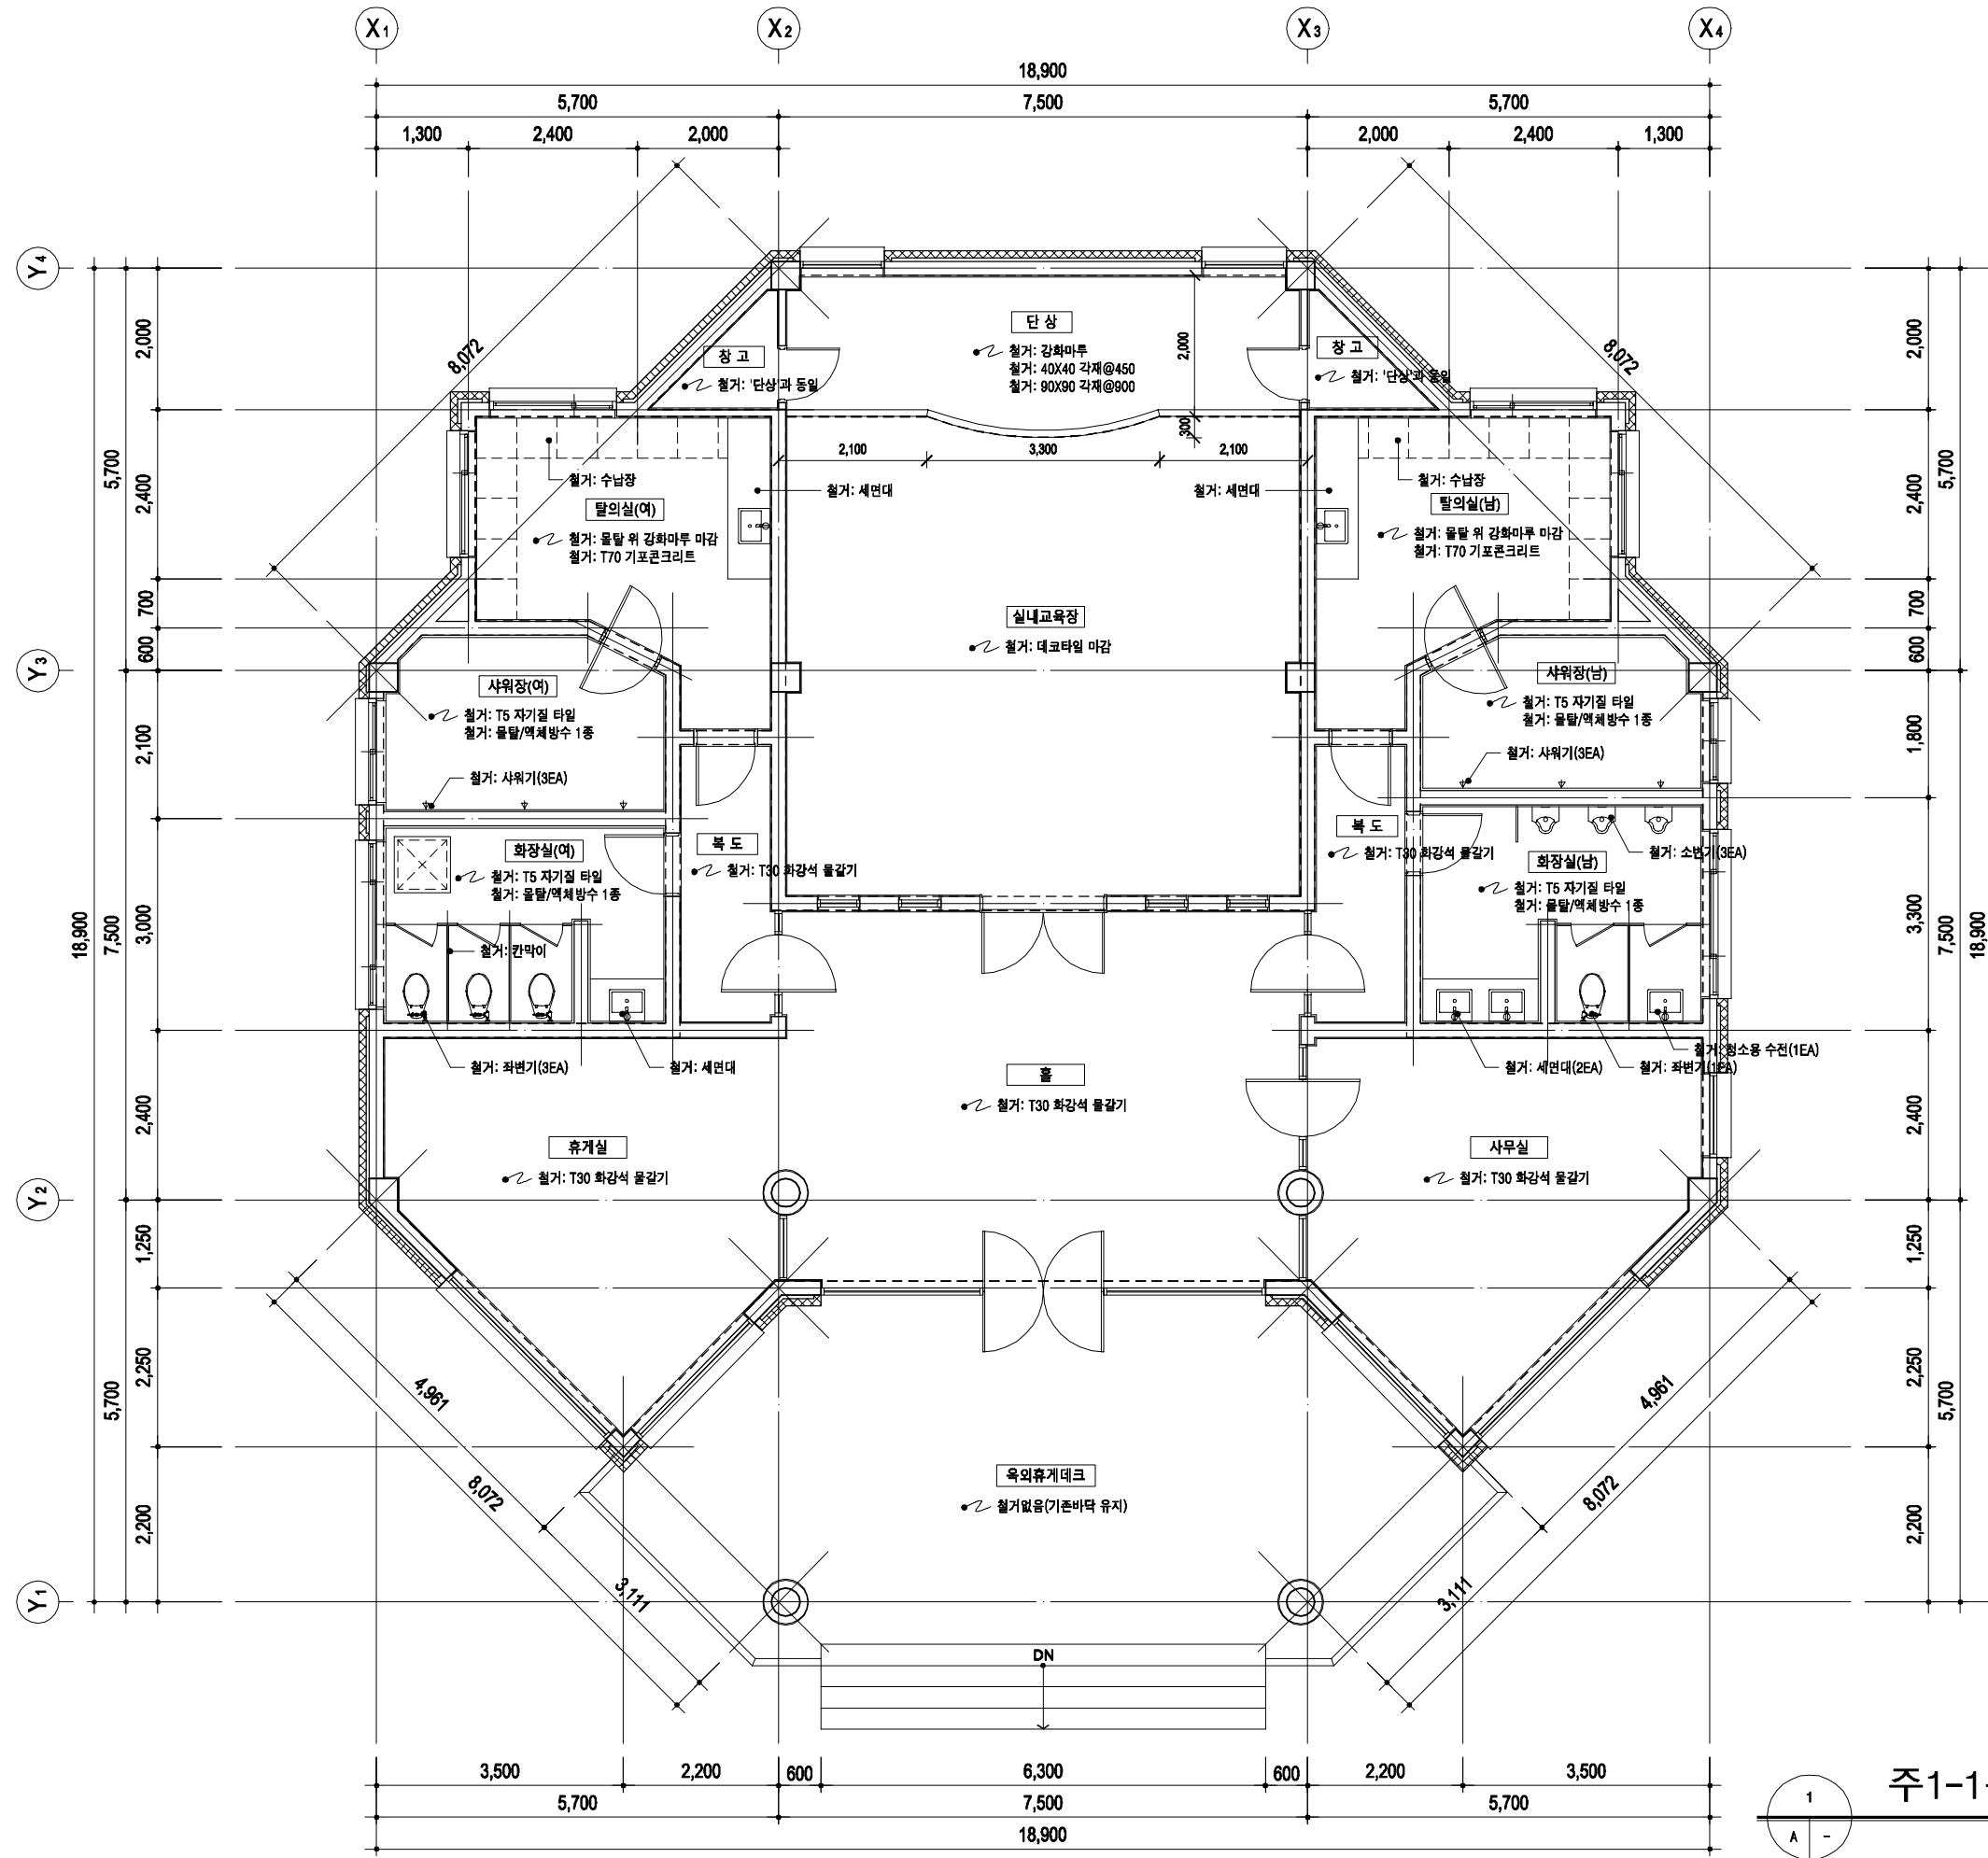

주1-1층 바닥평면도(철거)

축척 A1:1/50, A3:1/100

|               |   |
|---------------|---|
| PROJECT TITLE | 리틀 포레스트<br>봉뜨락 조성사업   |
| PROJECT NO    |   |
| NOTE          |   |
| KEY PLAN      |   |
| DESIGN CORP.  | <b>이음</b> (주)이음건축사사무소<br>ADD. 대구광역시 중구 장동로 81, 5F<br>TEL. 053.716.0776 FAX. 0505.720.0776<br>E-mail. e-ul2020@naver.com<br>Web. eul2020 / 0776 |
| APPROVED BY   | 대표이사/건축사 권오섭   |
| CHECKED BY    |   |
| DRAWN BY      |   |
| DATE          | 2023. 04.   |
| DRAWING TITLE | 주1-1층 바닥평면도<br>(철거)   |
| SCALE         | A3 : 1/ 100   |
| DRAWING NO.   | A01- 1002   |

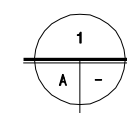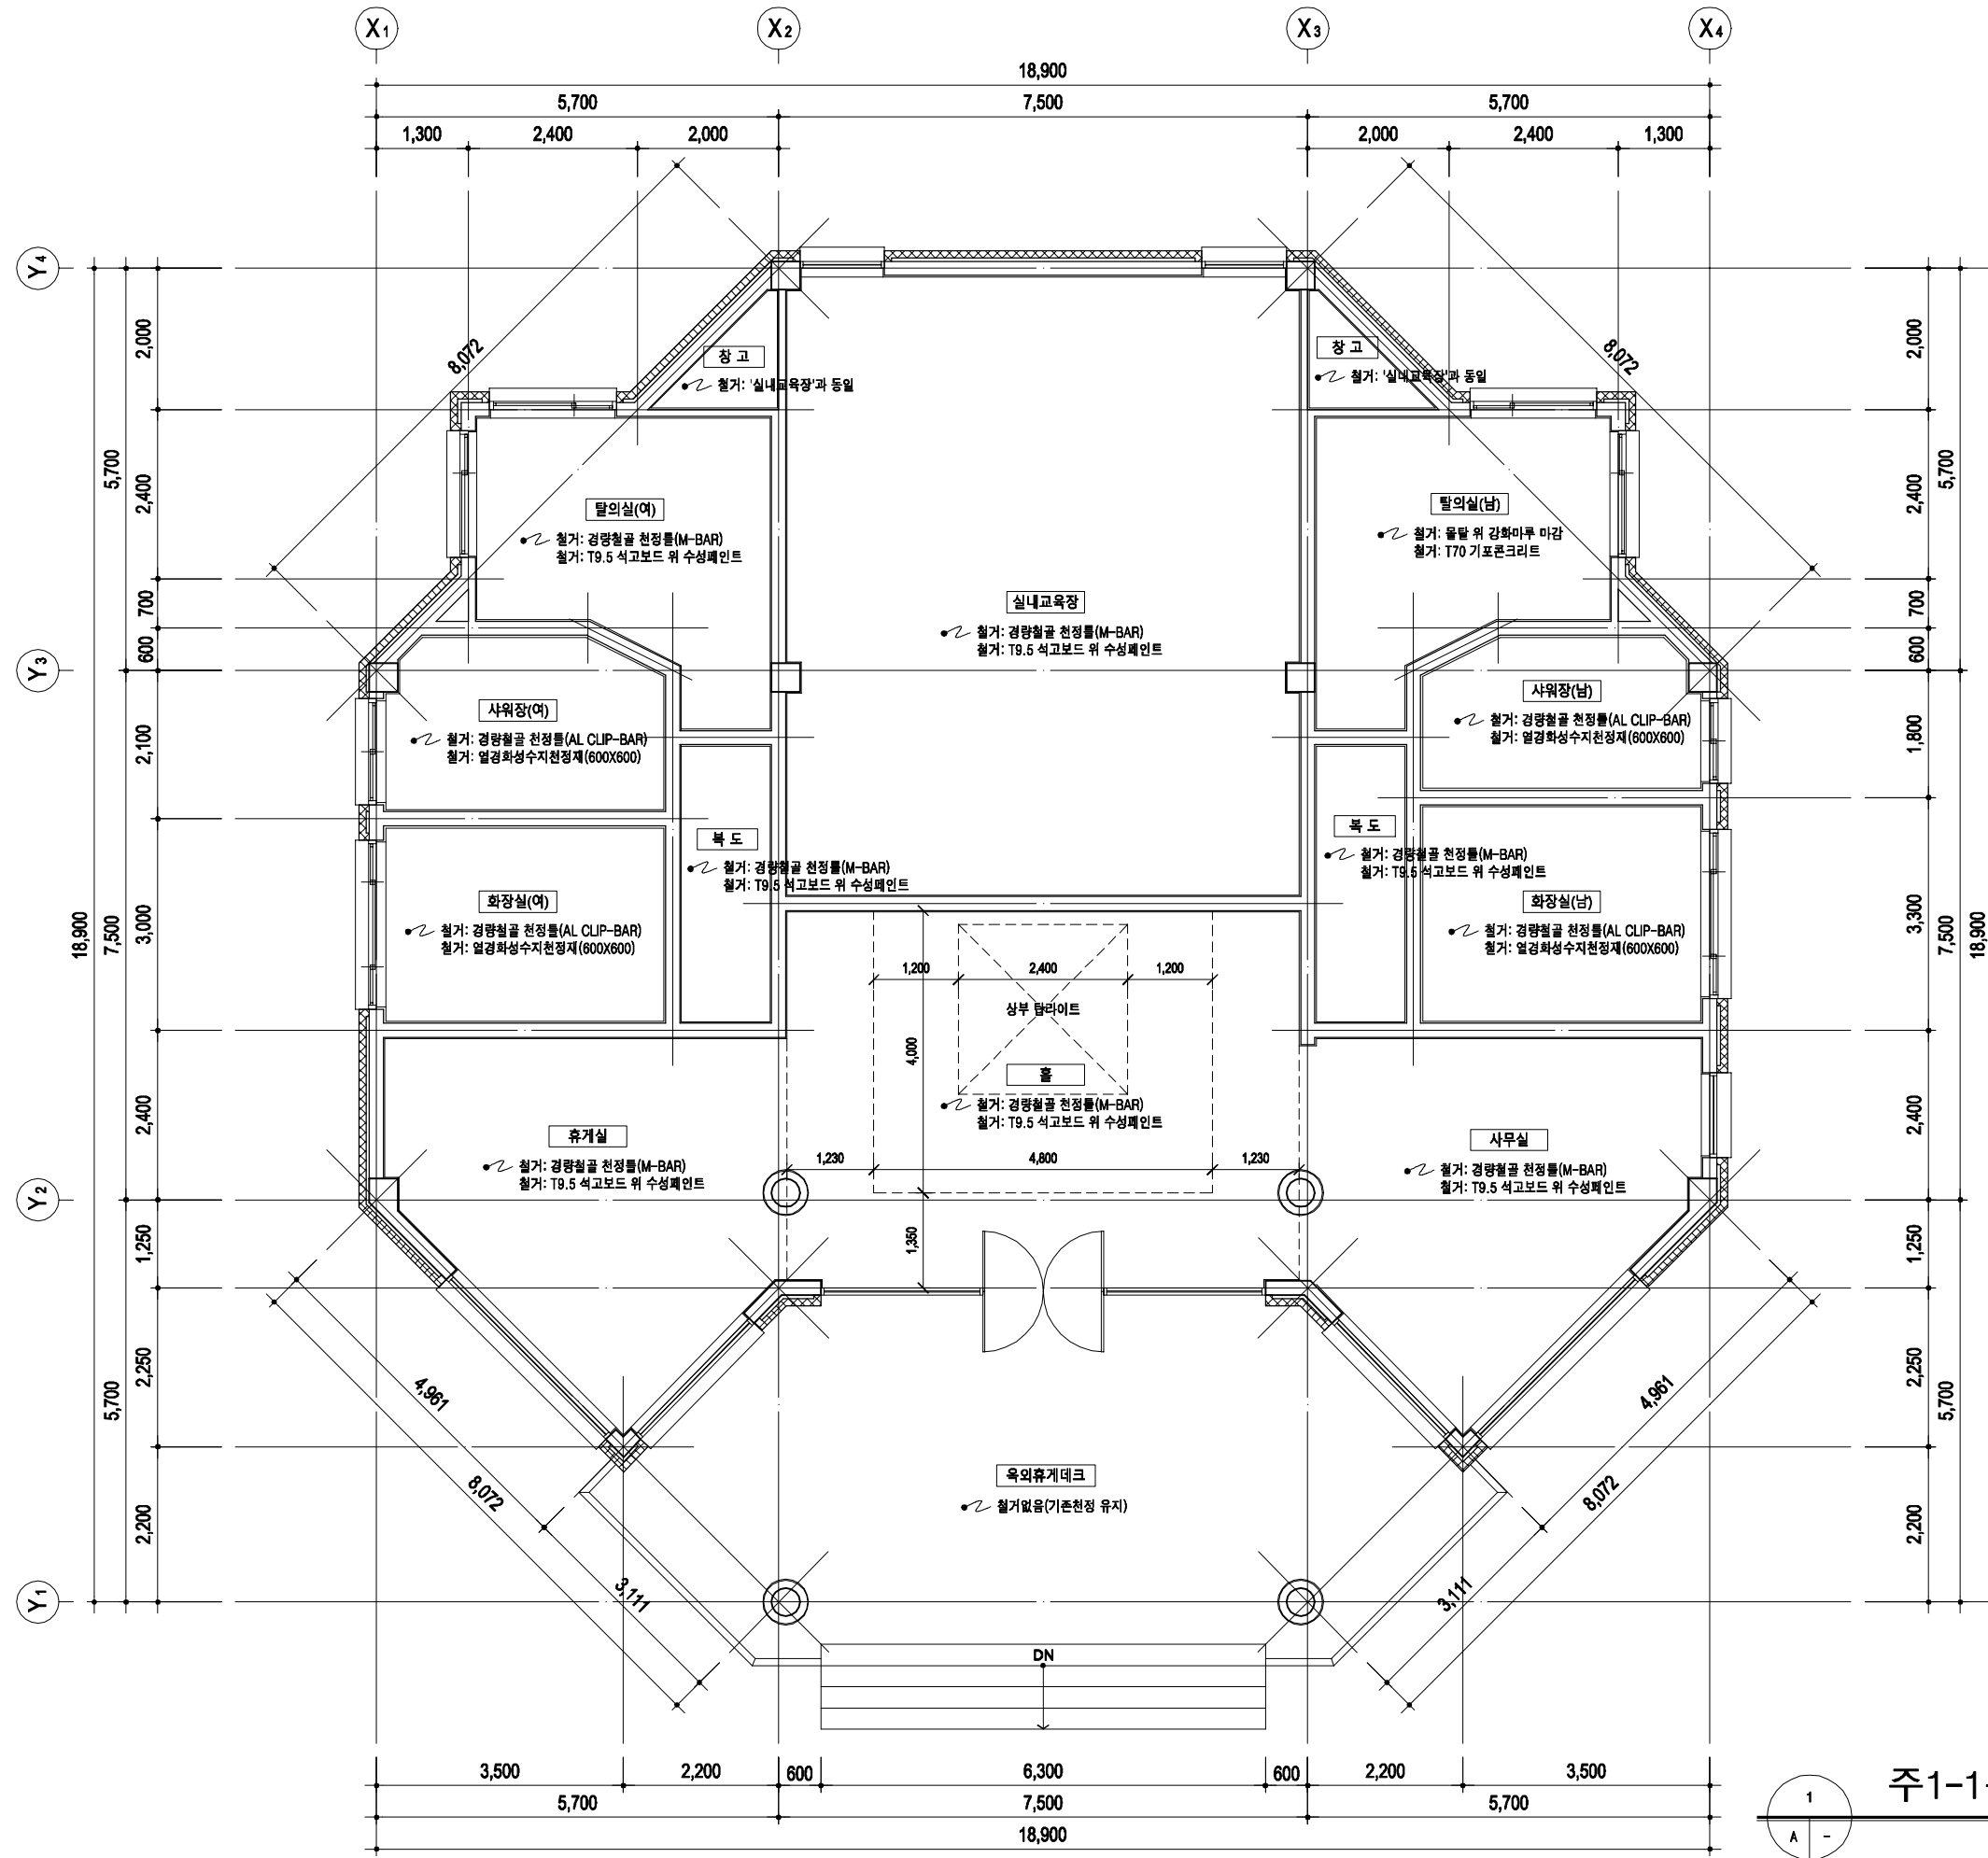

주1-1층 천정평면도(철거)

축척 A1:1/50, A3:1/100

|               |                                 |
|---------------|---------------------------------|
| PROJECT TITLE | 리틀 포레스트<br>봉뜨락 조성사업             |
| PROJECT NO    |                                 |
| NOTE          |                                 |
| KEY PLAN      |                                 |
| DESIGN CORP.  | 이음건축사사무소                        |
| ADD.          | 대구광역시 중구 장동로 81, 5F             |
| TEL.          | 053.716.0776 FAX. 0505.720.0776 |
| E-mail.       | e-ul2020@naver.com              |
| Web.          | eul2020 / 0776                  |
| APPROVED BY   | 대표이사/건축사 권오섭                    |
| CHECKED BY    |                                 |
| DRAWN BY      |                                 |
| DATE          | 2023. 04.                       |
| DRAWING TITLE | 주1-1층 천정평면도<br>(철거)             |
| SCALE         | A3 : 1/ 100                     |
| DRAWING NO.   | A01- 1003                       |

PROJECT TITLE

리틀 포레스트  
봉뜨락 조성사업

PROJECT NO

NOTE

KEY PLAN

DESIGN CORP.

**이음** (주)이음건축사사무소

ADD. 대구광역시 동구 장동로 81, 5F  
TEL. 053.716.0776 FAX. 0505.720.0776  
E-mail. e-ul2020@naver.com  
Web. eul2020 / 0776

APPROVED BY  
대표이사/건축사 권오섭

CHECKED BY



DRAWN BY

DATE  
2023. 04.

DRAWING TITLE  
주1-정면도  
(철거)

SCALE  
A3 : 1/ 100

DRAWING NO.  
A01- 1004

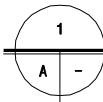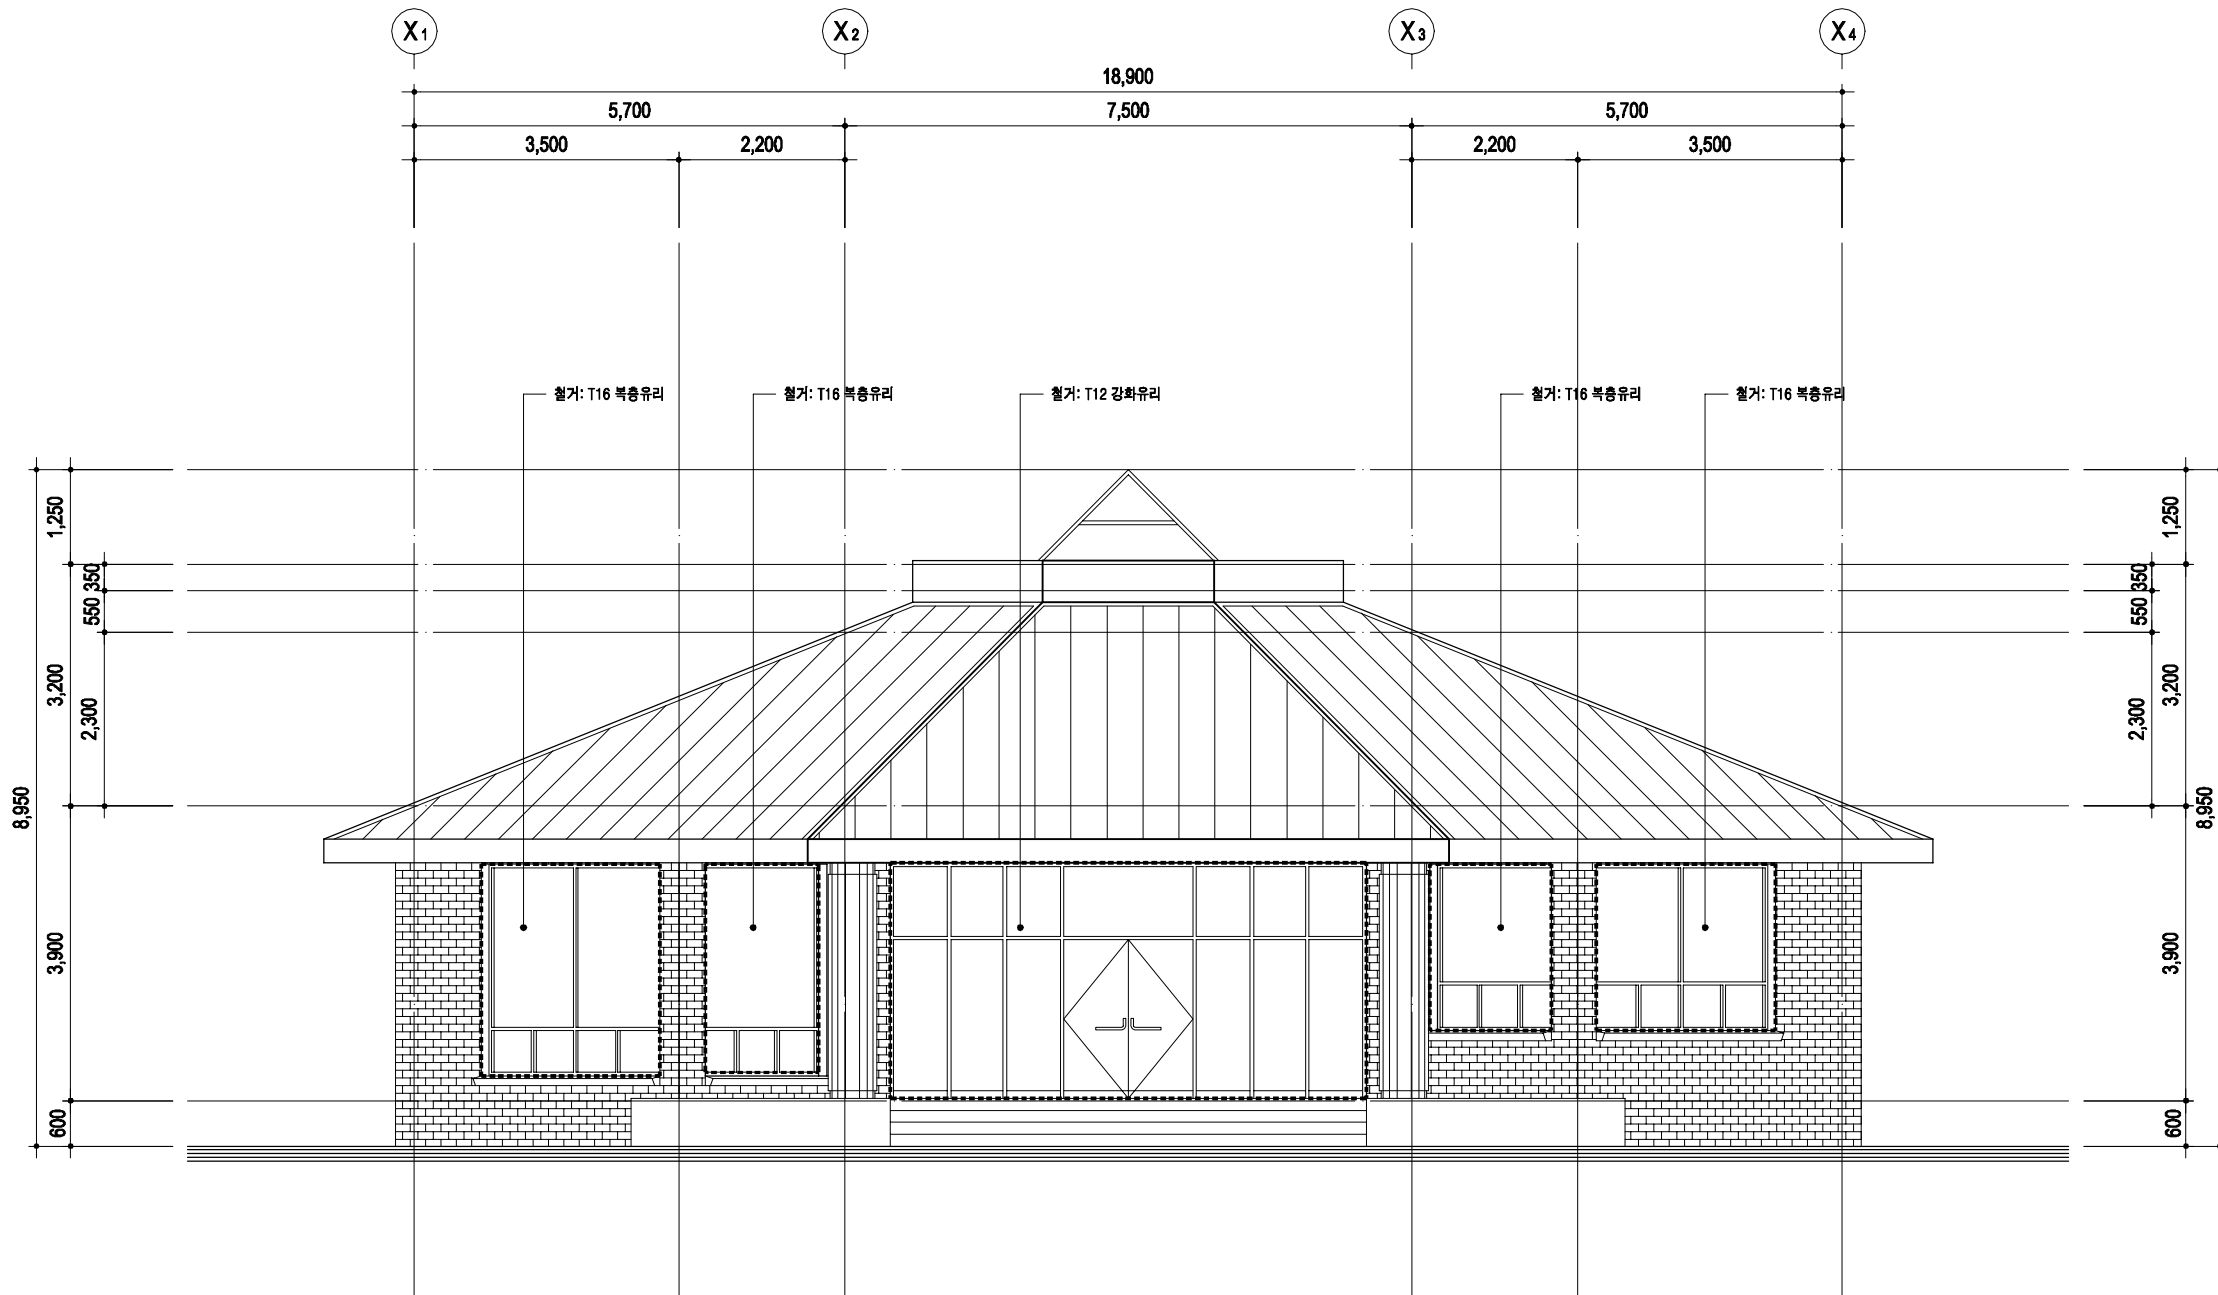

주1-정면도(철거)

축척 A1:1/50, A3:1/100

PROJECT TITLE

리틀 포레스트  
봉뜨락 조성사업

PROJECT NO

NOTE

KEY PLAN

DESIGN CORP.

**이음** (주)이음건축사사무소

ADD. 대구광역시 동구 장동로 81, 5F  
TEL. 053.716.0776 FAX. 0505.720.0776  
E-mail. e-ul2020@naver.com  
Web. eul2020 / 0776

APPROVED BY  
대표이사/건축사 권오섭

CHECKED BY



DRAWN BY

DATE  
2023. 04.

DRAWING TITLE  
주1-배면도  
(철거)

SCALE  
A3 : 1/ 100

DRAWING NO.  
A01- 1005

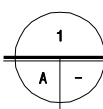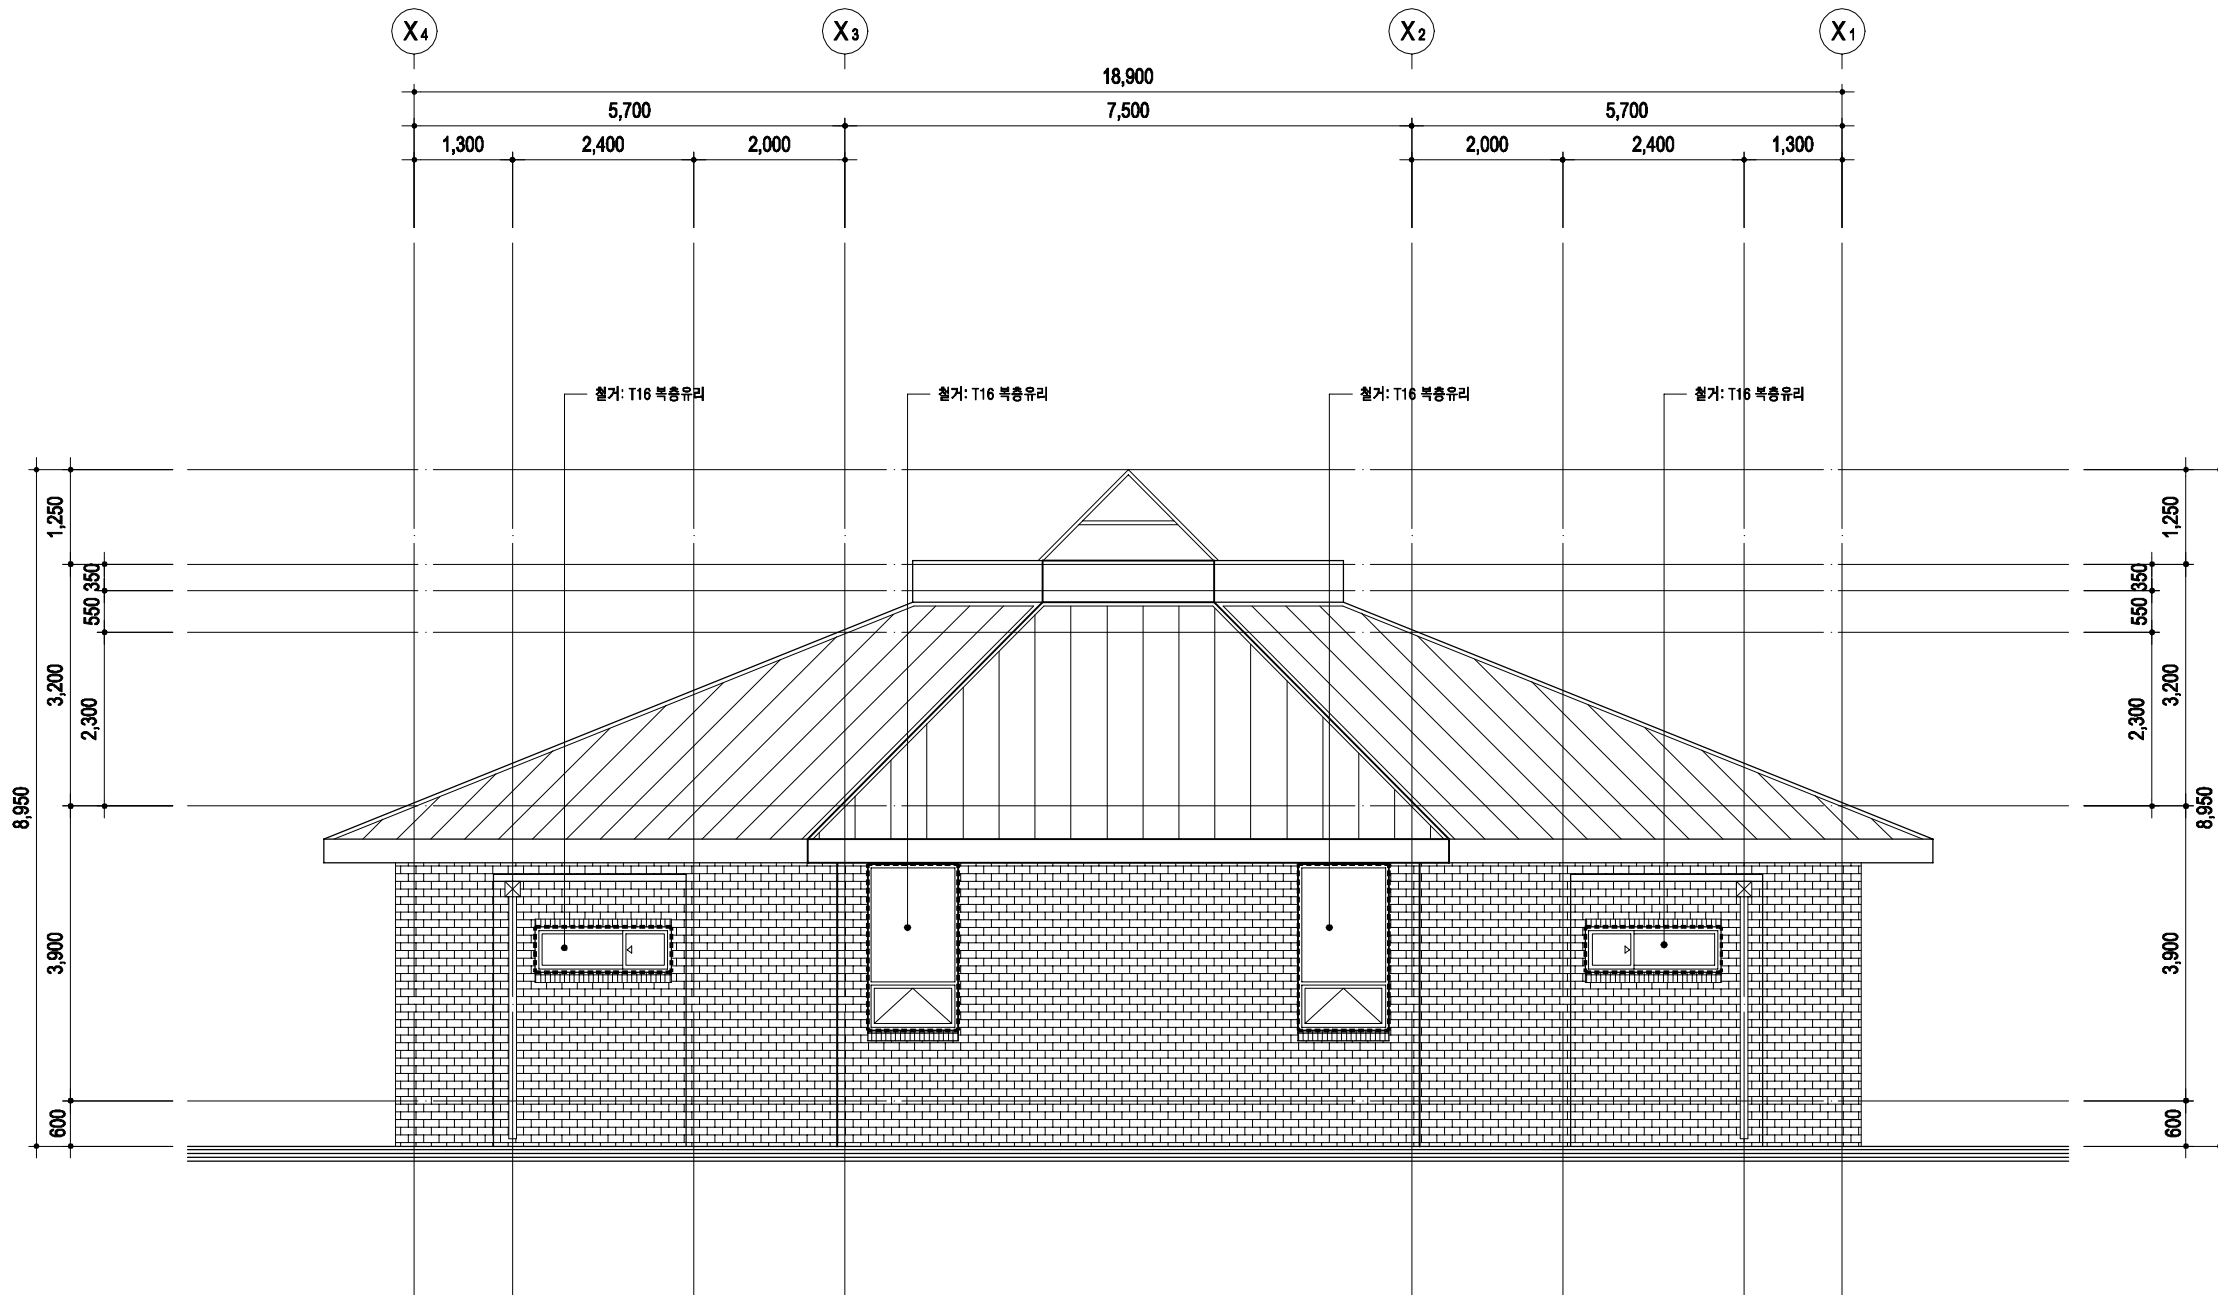

주1-배면도(철거)

축척 A1:1/50, A3:1/100

PROJECT TITLE

리틀 포레스트  
봉뜨락 조성사업

PROJECT NO

NOTE

KEY PLAN

DESIGN CORP.

**이음** (주)이음건축사사무소

ADD. 대구광역시 동구 장동로 81, 5F  
TEL. 053.716.0776 FAX. 0505.720.0776  
E-mail. e-ul2020@naver.com  
Web. eul2020 / 0776

APPROVED BY  
대표이사/건축사 권오섭

CHECKED BY


DRAWN BY

DATE  
2023. 04.

DRAWING TITLE  
주1-우측면도  
(철거)

SCALE  
A3 : 1/ 100

DRAWING NO.  
A01- 1006

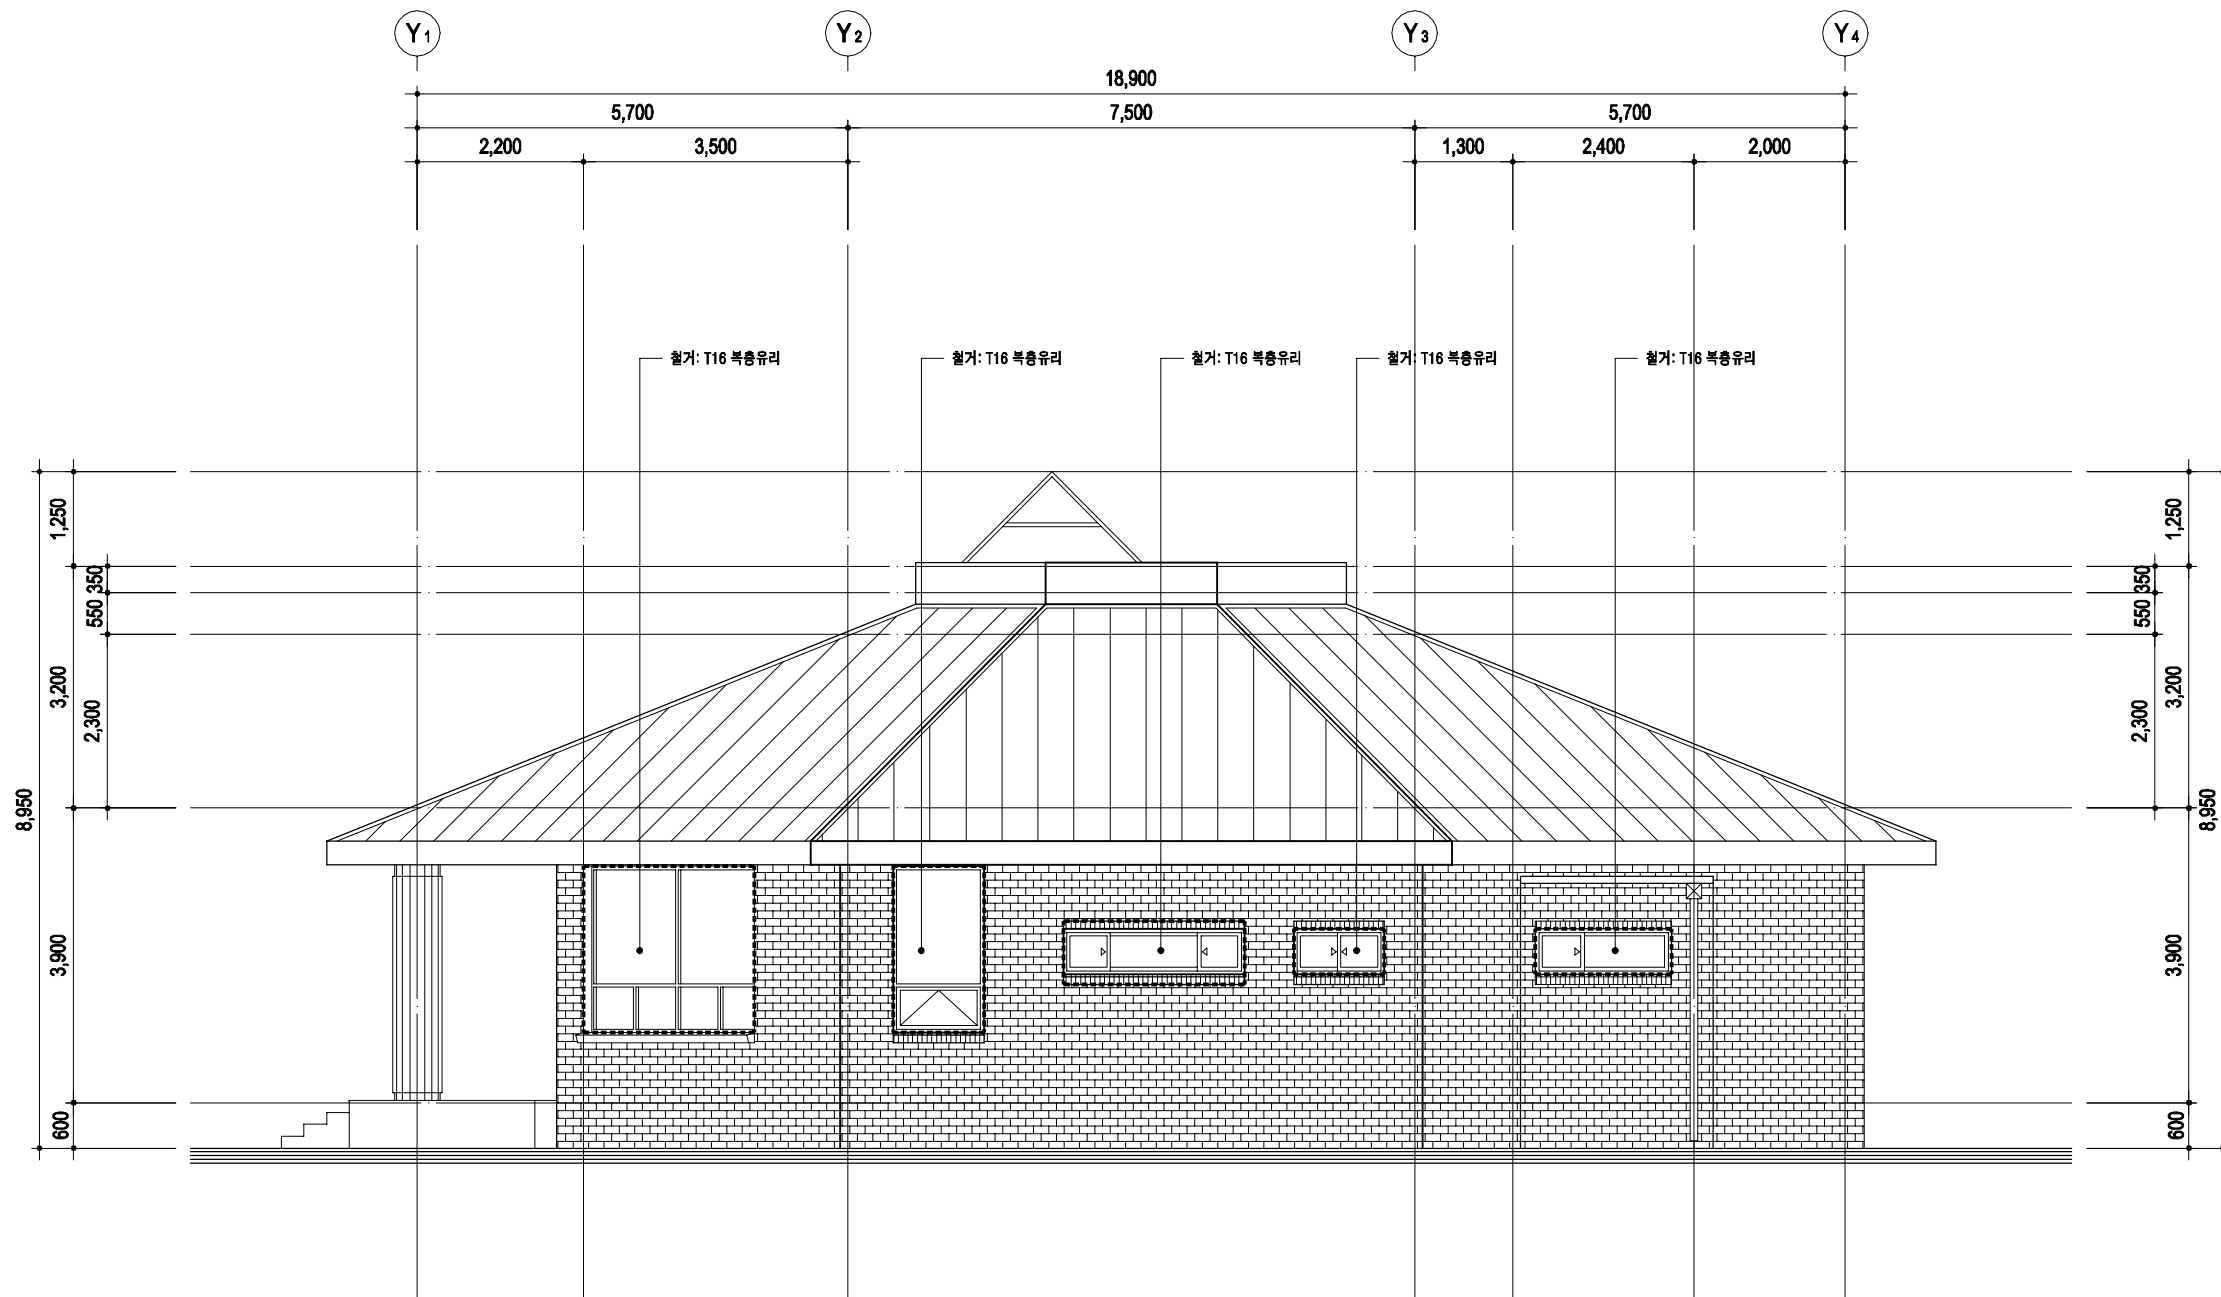

주1-우측면도(철거)

축척 A1:1/50, A3:1/100

PROJECT TITLE

리틀 포레스트  
봉뜨락 조성사업

PROJECT NO

NOTE

KEY PLAN

DESIGN CORP.

**이음** (주)이음건축사사무소

ADD. 대구광역시 동구 장동로 81, 5F  
TEL. 053.716.0776 FAX. 0505.720.0776  
E-mail. e-ul2020@naver.com  
Web. eul2020 / 0776

APPROVED BY  
대표이사/건축사 권오섭

CHECKED BY



DRAWN BY

DATE  
2023. 04.

DRAWING TITLE  
주1-좌측면도  
(철거)

SCALE  
A3 : 1/ 100

DRAWING NO.  
A01- 1007

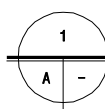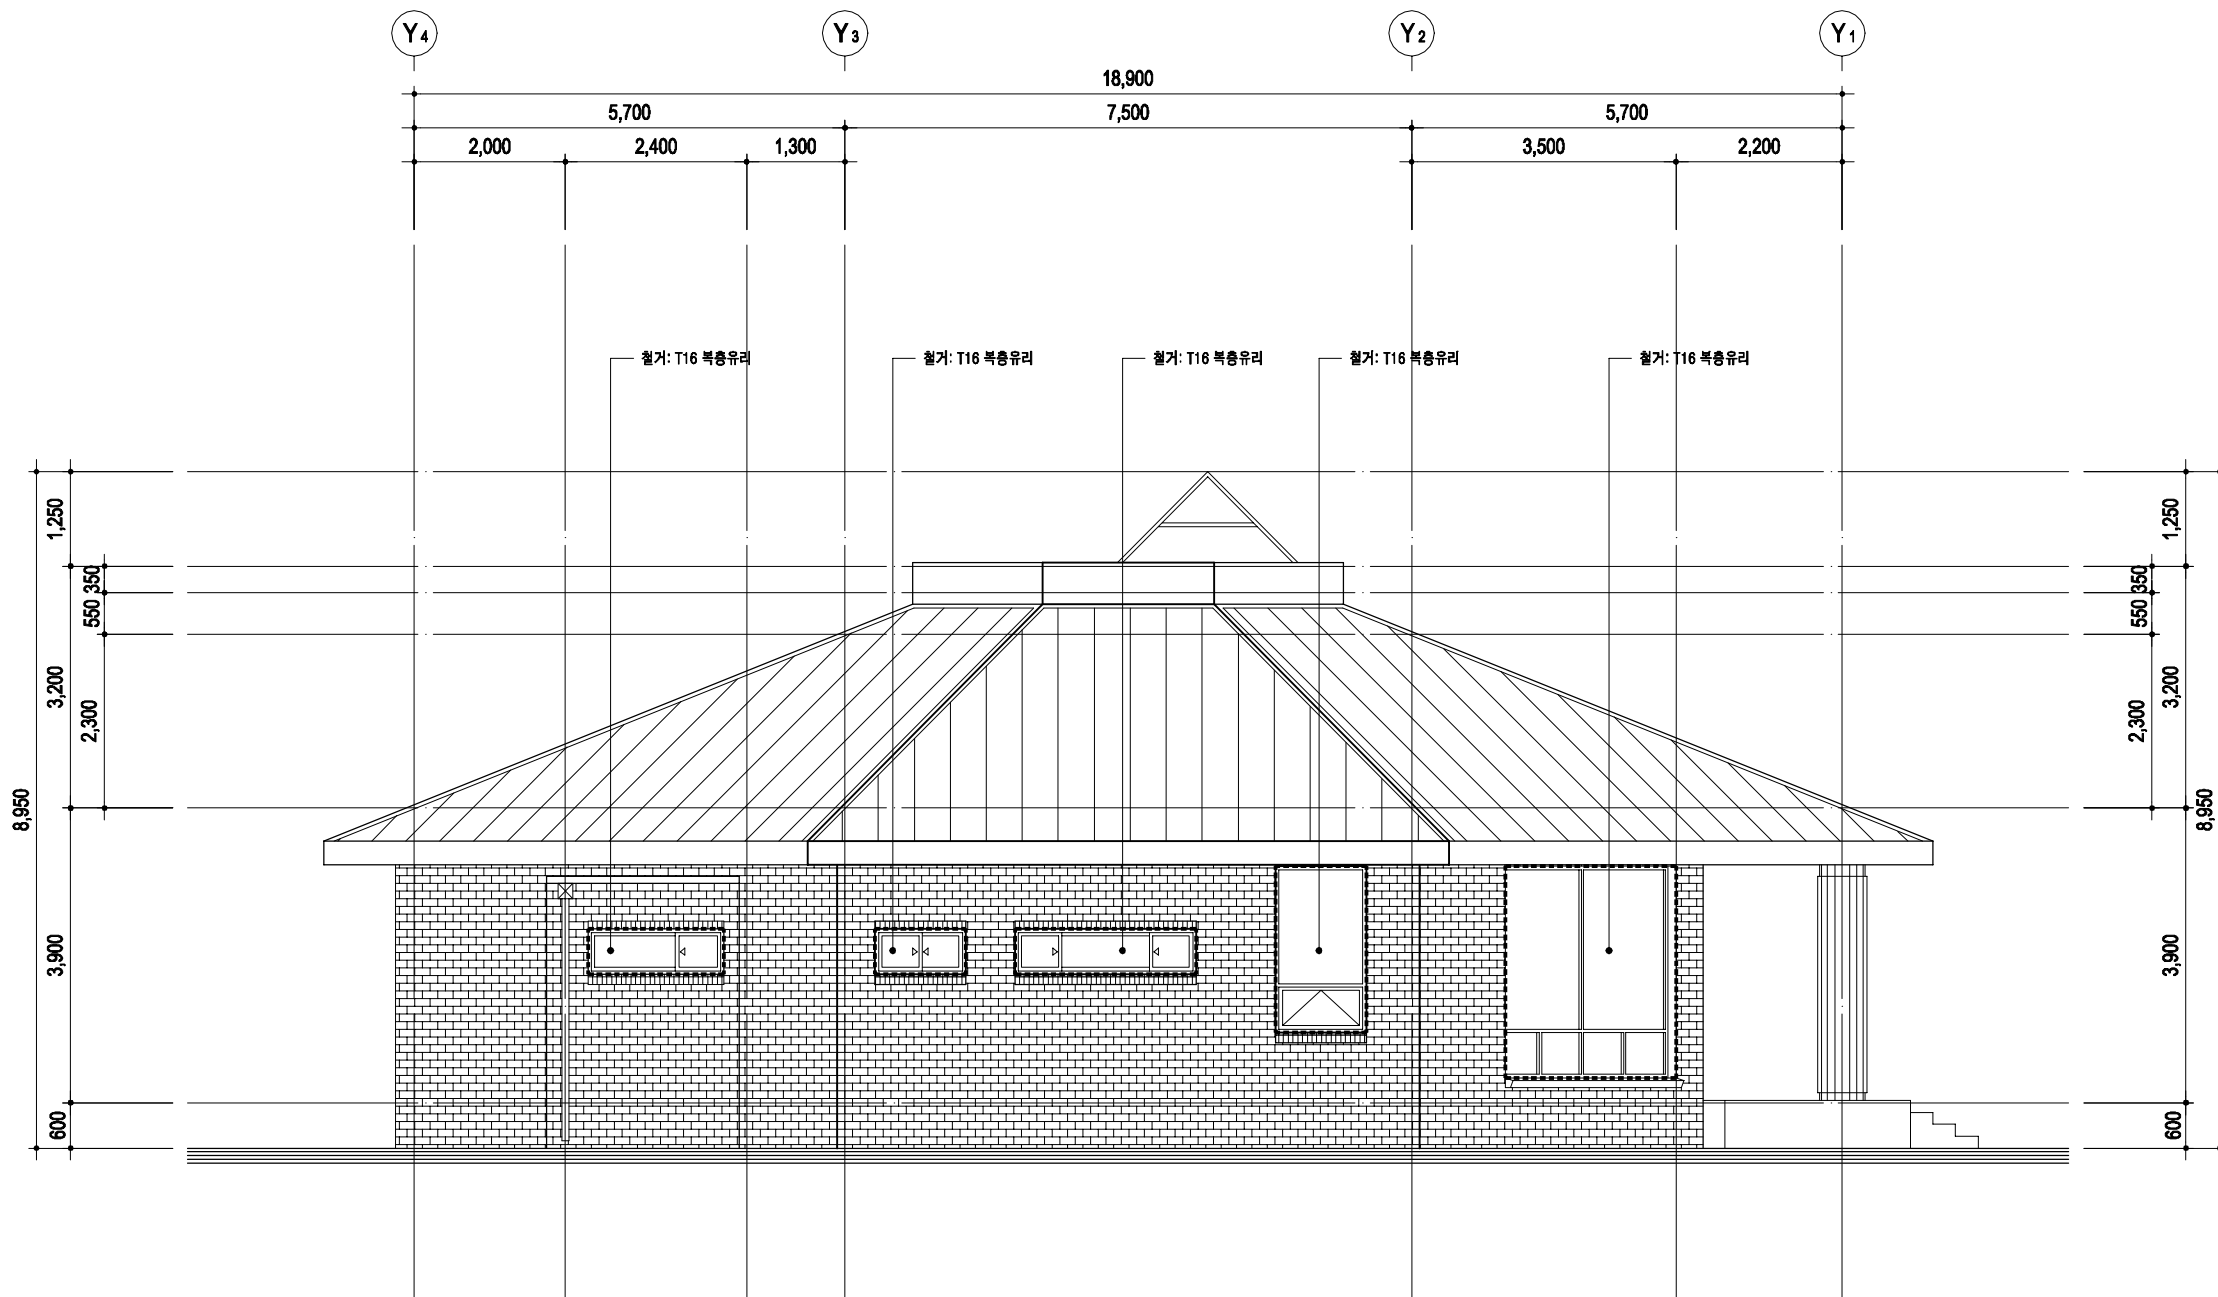

주1-좌측면도(철거)

축척 A1:1/50, A3:1/100


PROJECT TITLE

리틀 포레스트  
봉뜨락 조성사업

PROJECT NO

NOTE

KEY PLAN

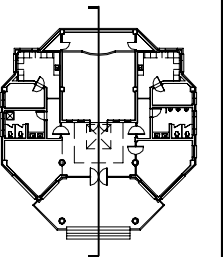

DESIGN CORP.

**이음** (주)이음건축사사무소

ADD. 대구광역시 중구 장동로 81, 5F  
TEL. 053.716.0776 FAX. 0505.720.0776  
E-mail. e-ul2020@naver.com  
Web. eul2020 / 0776

APPROVED BY  
대표이사 / 건축사 권오섭

CHECKED BY


DRAWN BY

DATE  
2023. 04.

DRAWING TITLE  
주1-종단면도  
(철거)

SCALE  
A3 : 1/ 80

DRAWING NO.  
A01- 1008

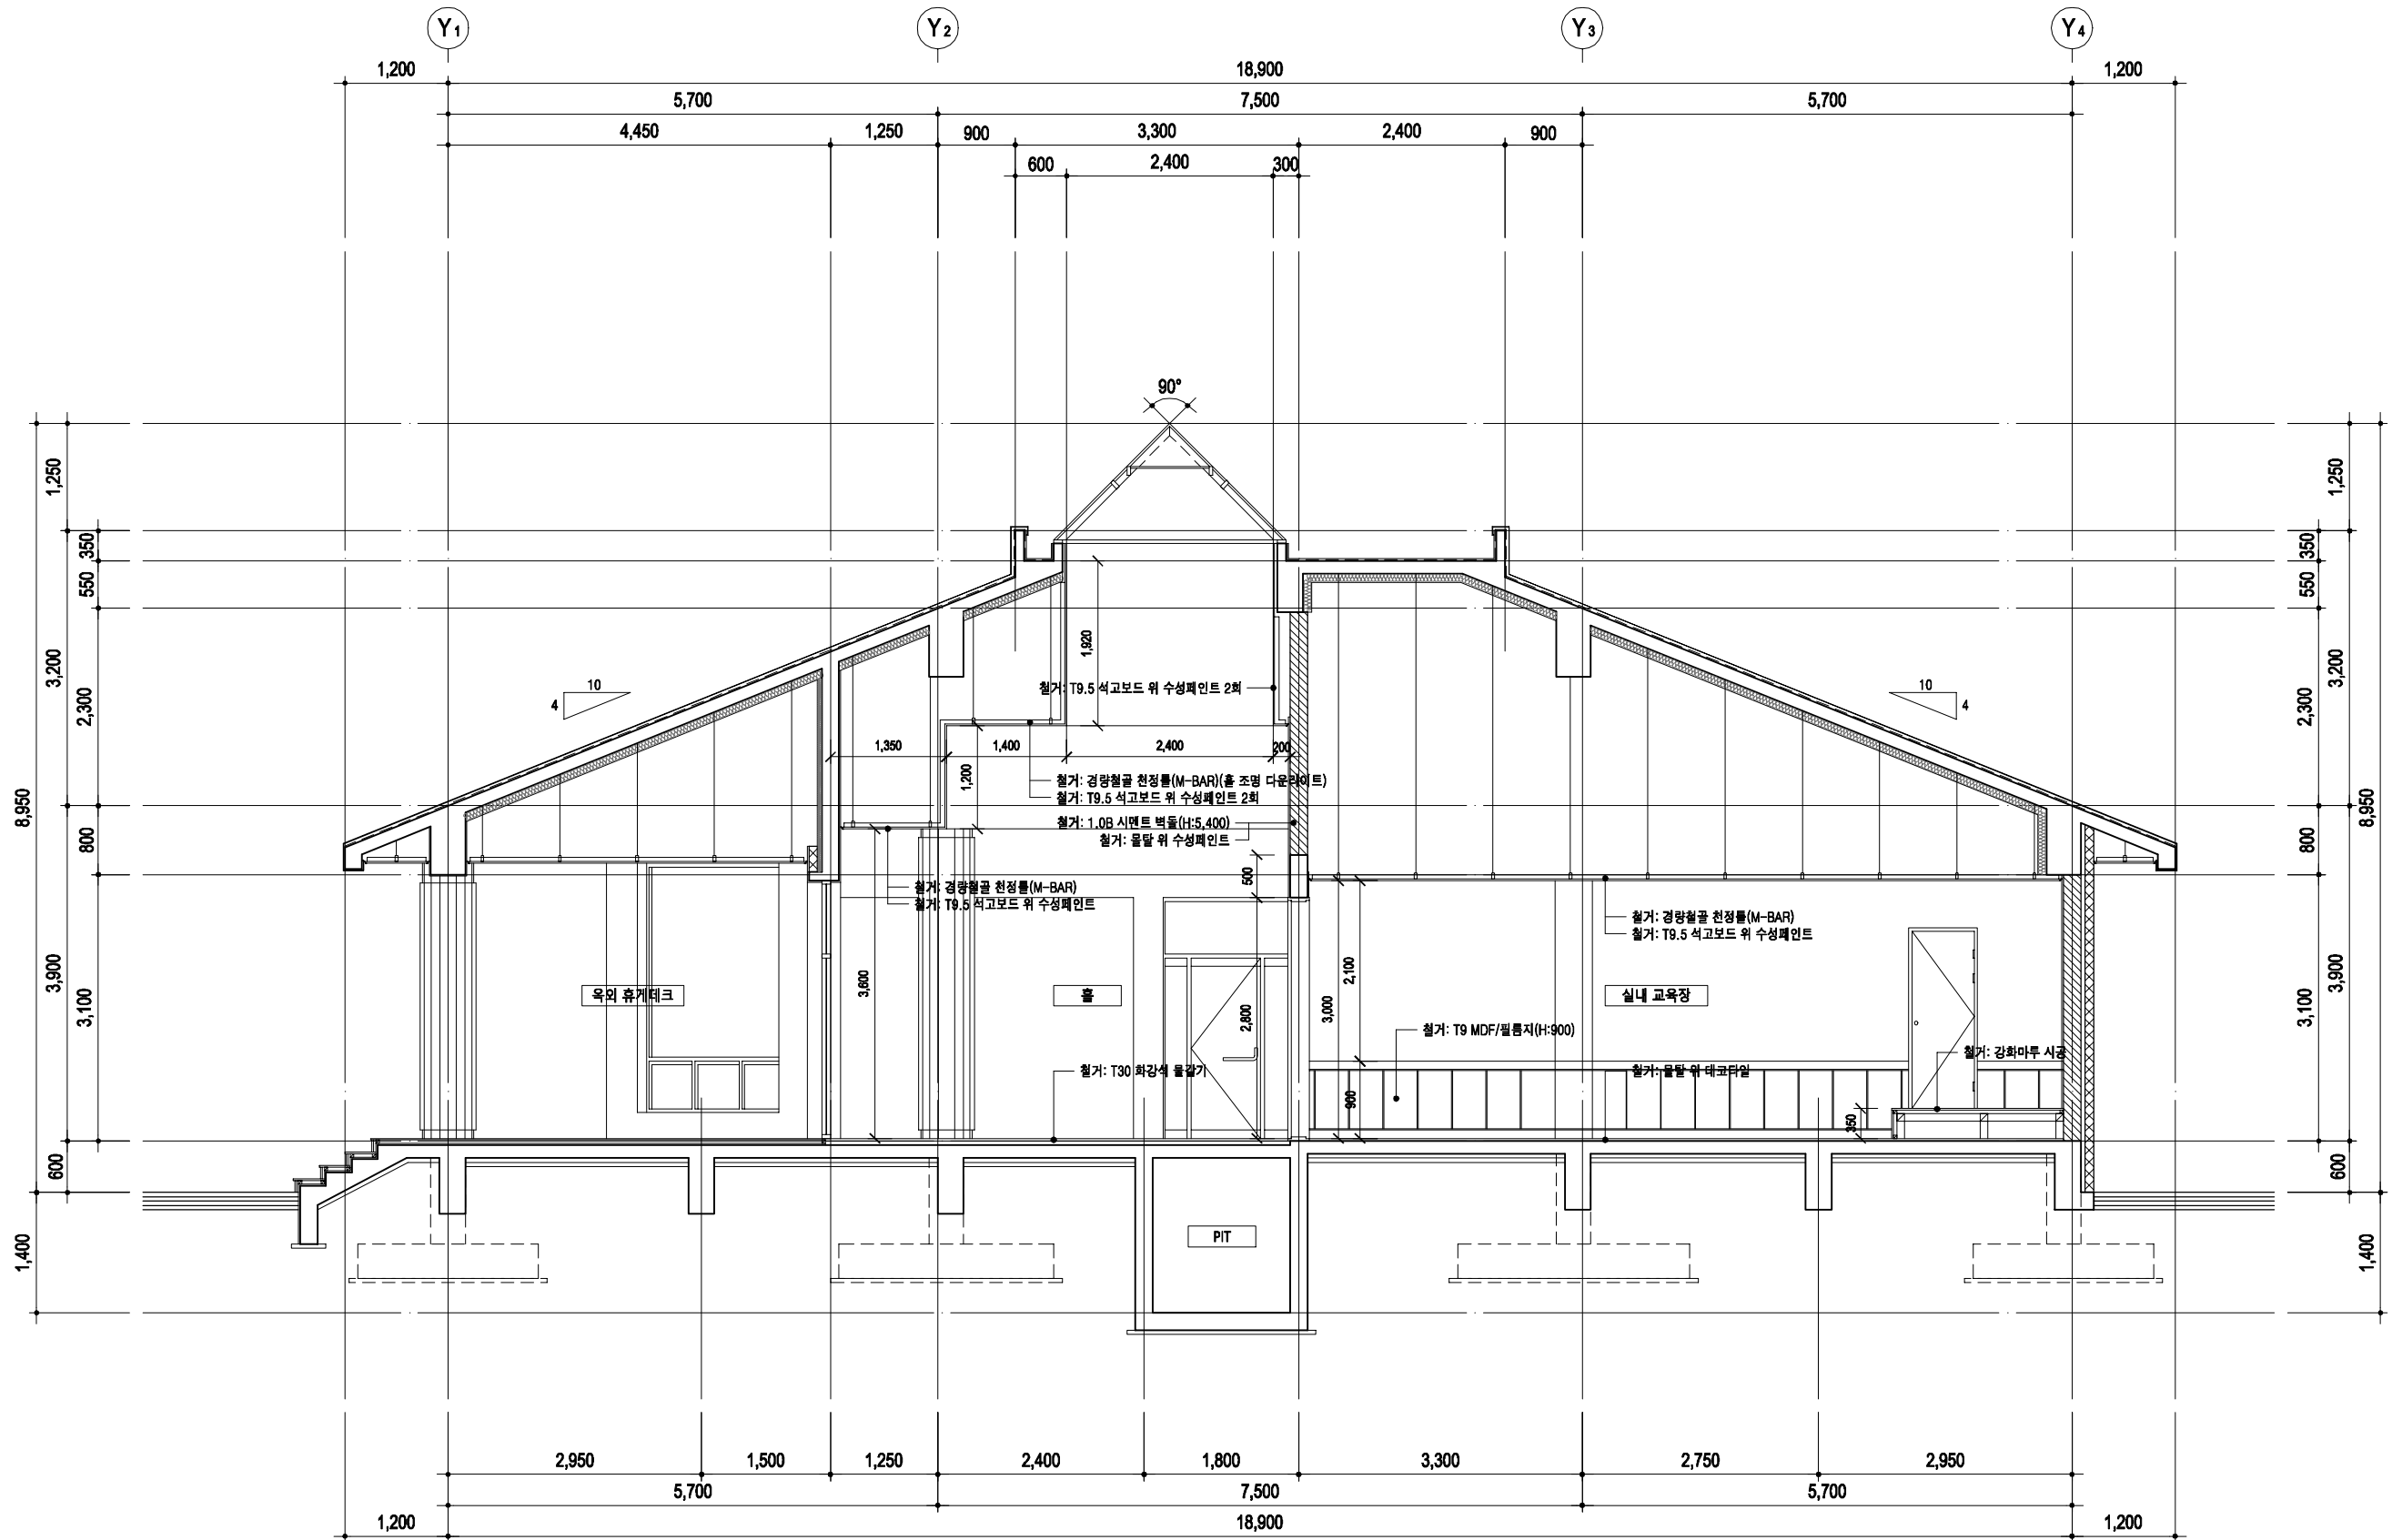

주1-종단면도(철거)

축척 A1:1/40, A3:1/80


PROJECT TITLE

리틀 포레스트  
봉뜨락 조성사업

PROJECT NO

NOTE

KEY PLAN

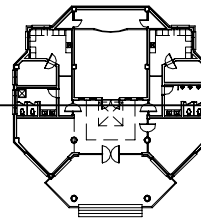

DESIGN CORP.

이음건축사사무소

ADD. 대구광역시 중구 장동로 81, 5F  
TEL. 053.716.0776 FAX. 0505.720.0776  
E-mail. e-ul2020@naver.com  
Web. eul2020 / 0776

APPROVED BY

대표이사/건축사 권오섭

CHECKED BY

DRAWN BY

DATE

2023. 04.

DRAWING TITLE


주1-횡단면도(철거)

SCALE


A3 : 1/ 80

DRAWING NO.

A01- 1009

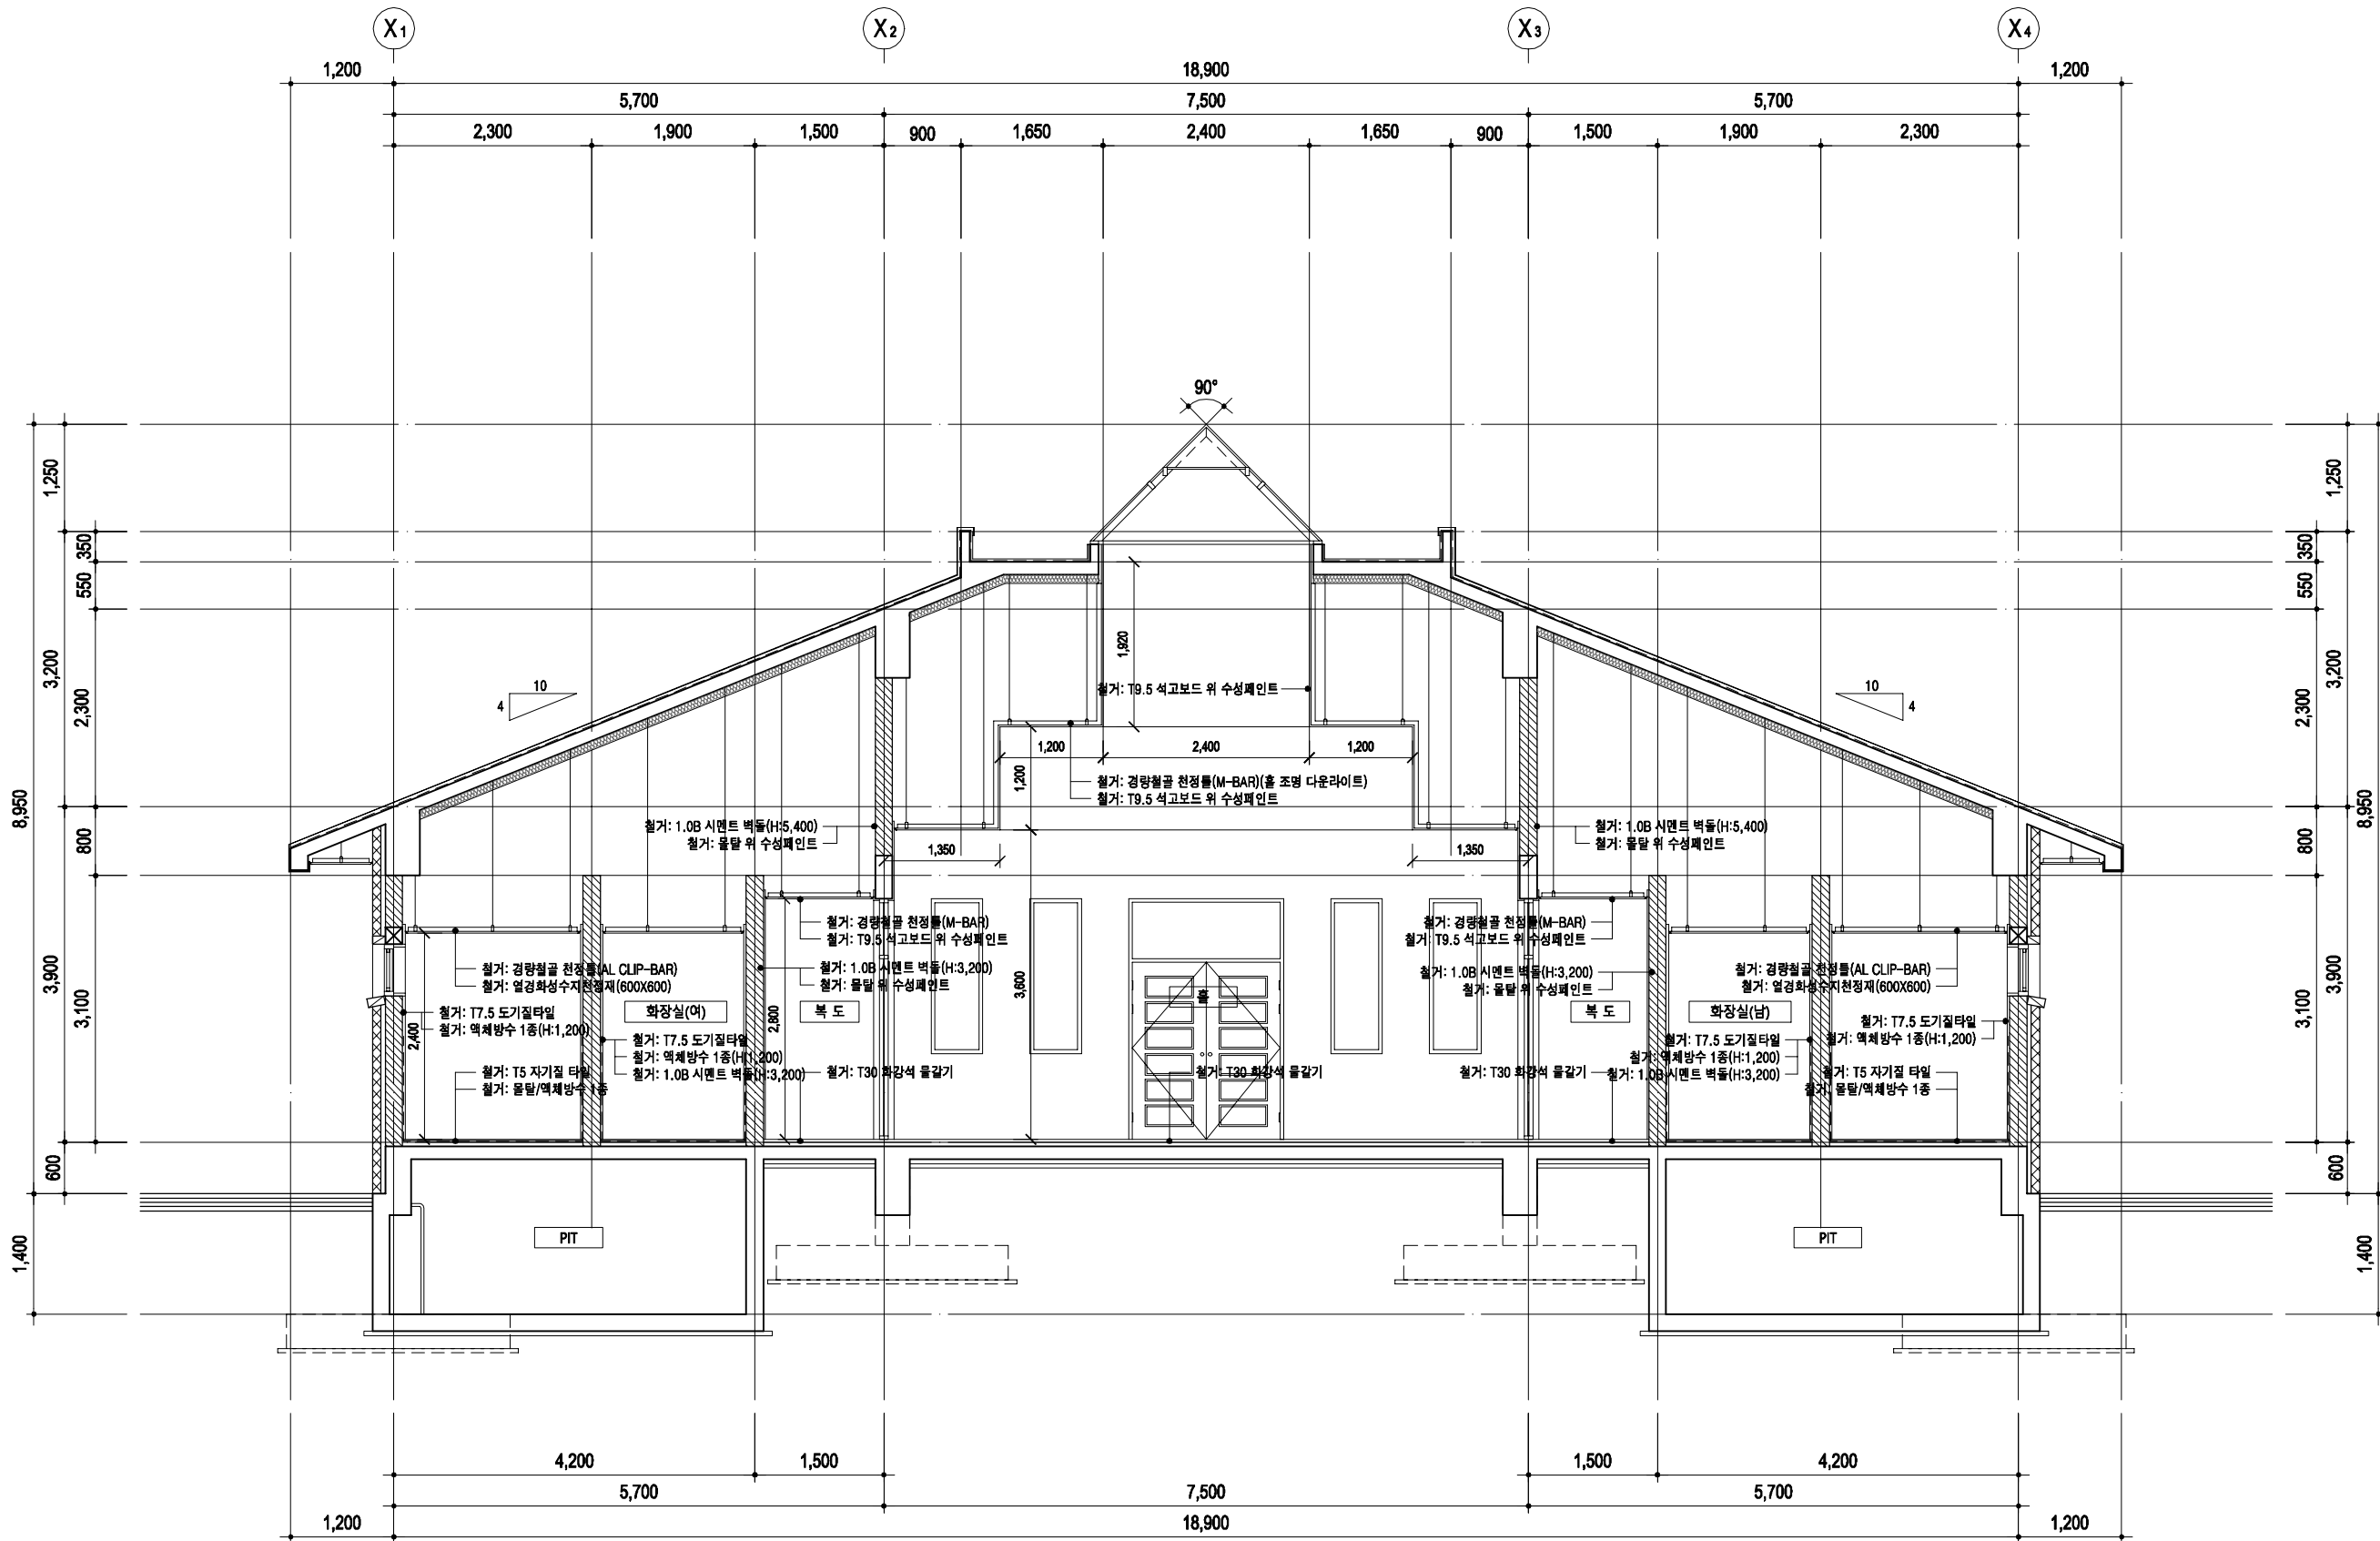

주1-횡단면도(철거)

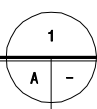

축척 A1:1/40, A3:1/80


PROJECT TITLE

리틀 포레스트  
봉뜨락 조성사업

PROJECT NO

NOTE

KEY PLAN

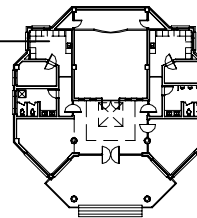

DESIGN CORP.

**이음** (주)이음건축사사무소

ADD. 대구광역시 중구 장동로 81, 5F  
TEL. 053.716.0776 FAX. 0505.720.0776  
E-mail. e-ul2020@naver.com  
Web. eul2020 / 0776

APPROVED BY

대표이사/건축사 권오섭

CHECKED BY

DRAWN BY

DATE

2023. 04.

DRAWING TITLE




주1-부분 단면 상세도(철거)

SCALE

A3 : 1/ 80



DRAWING NO.

A01- 1010

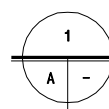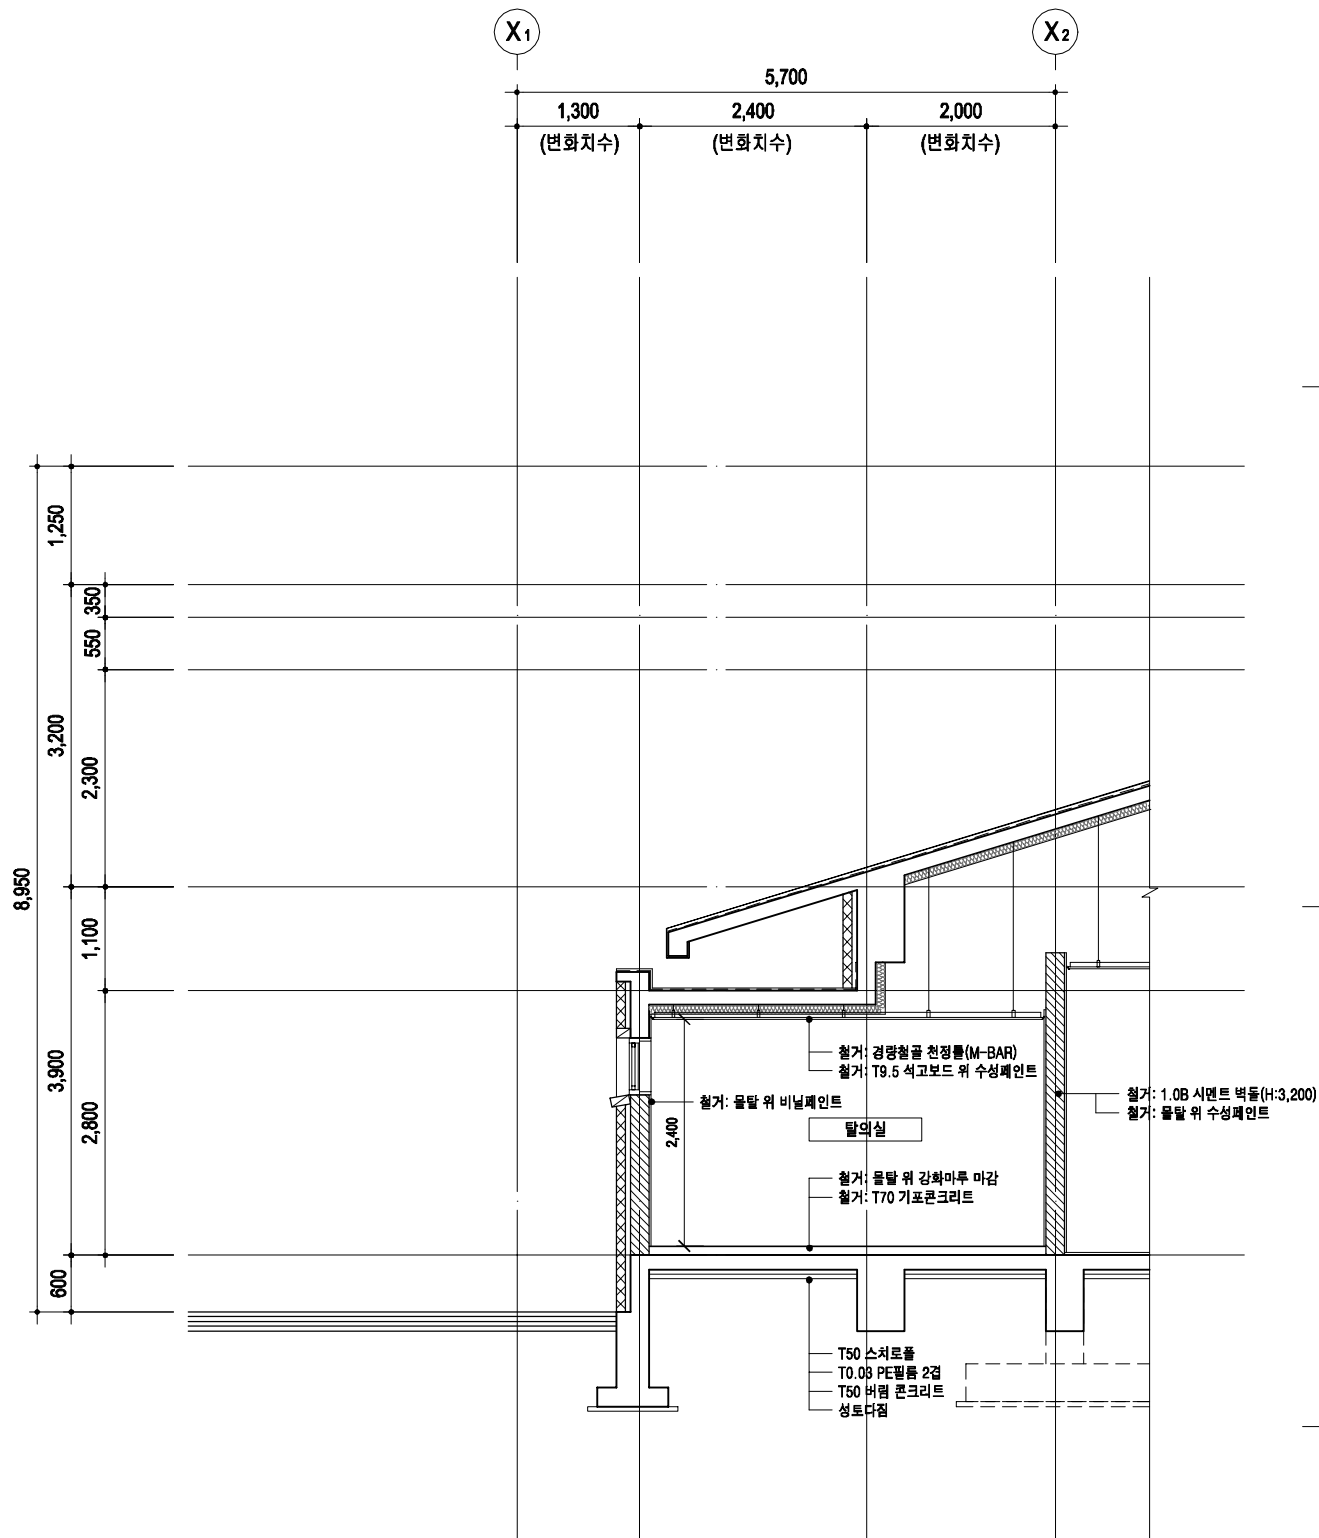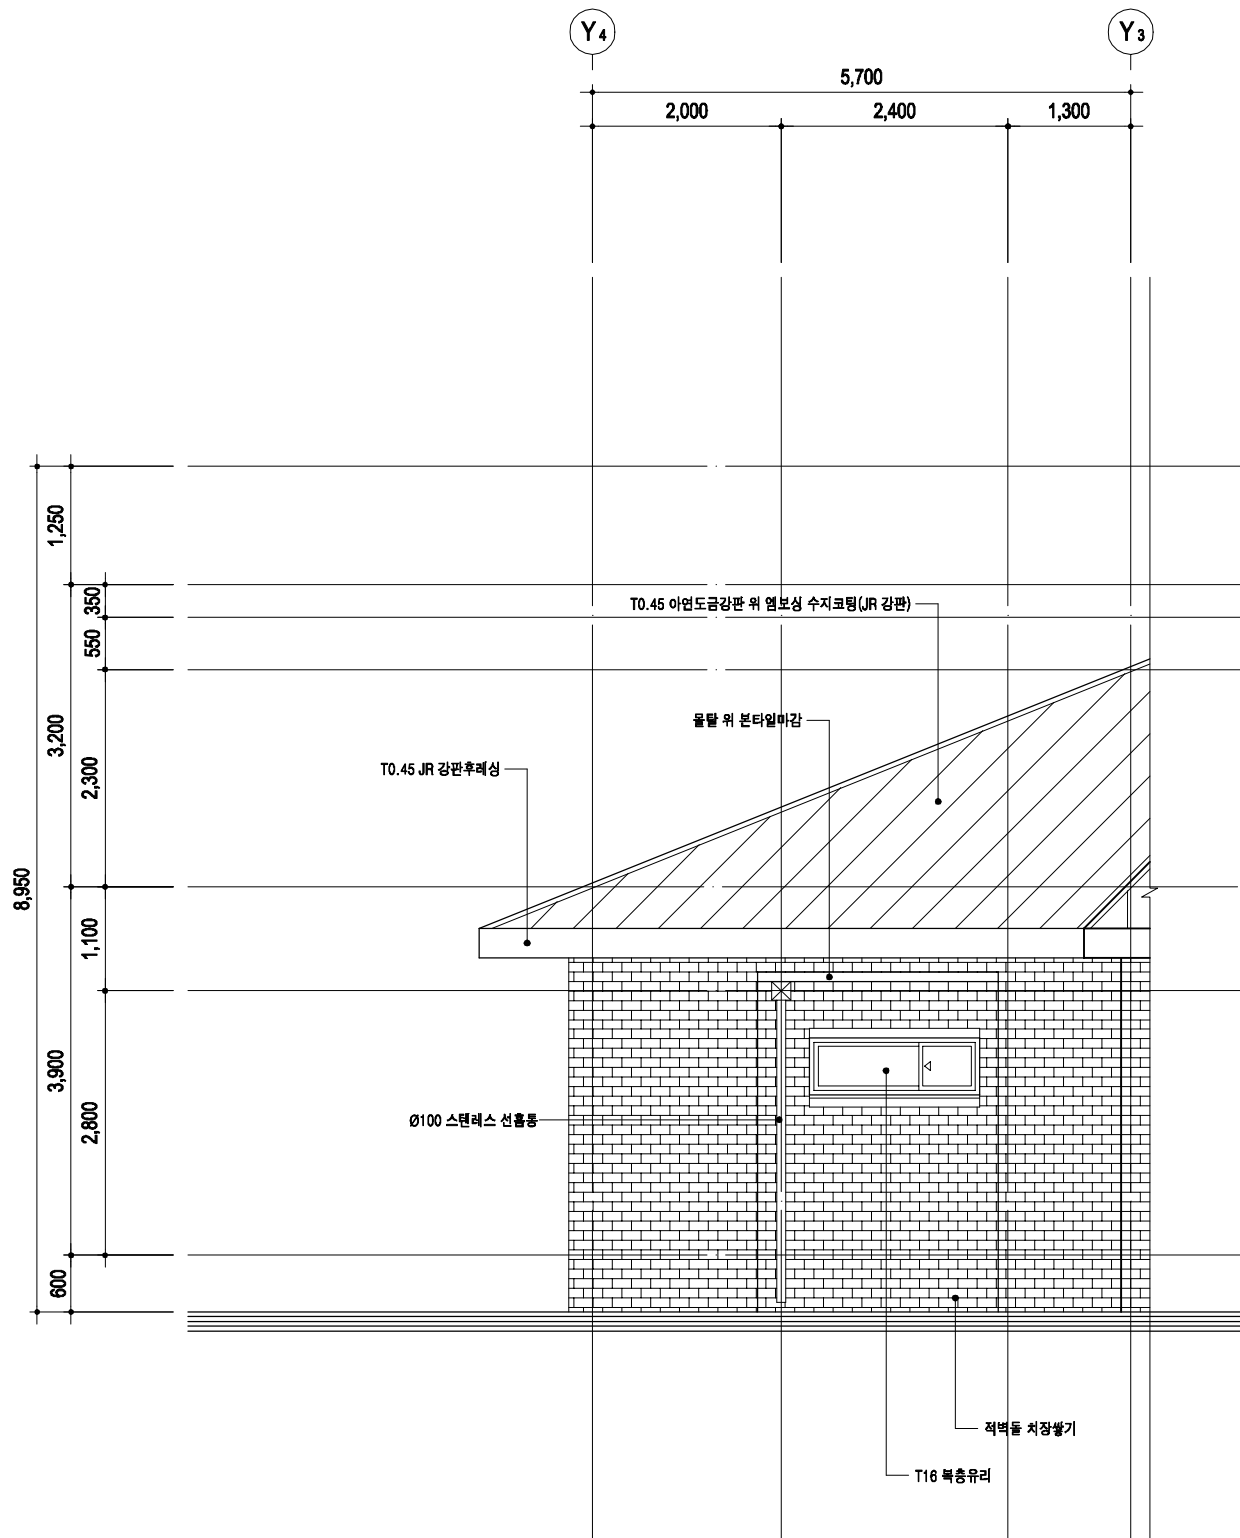

주1-부분 단면 상세도(철거)

축척 A1:1/40, A3:1/80

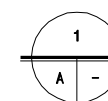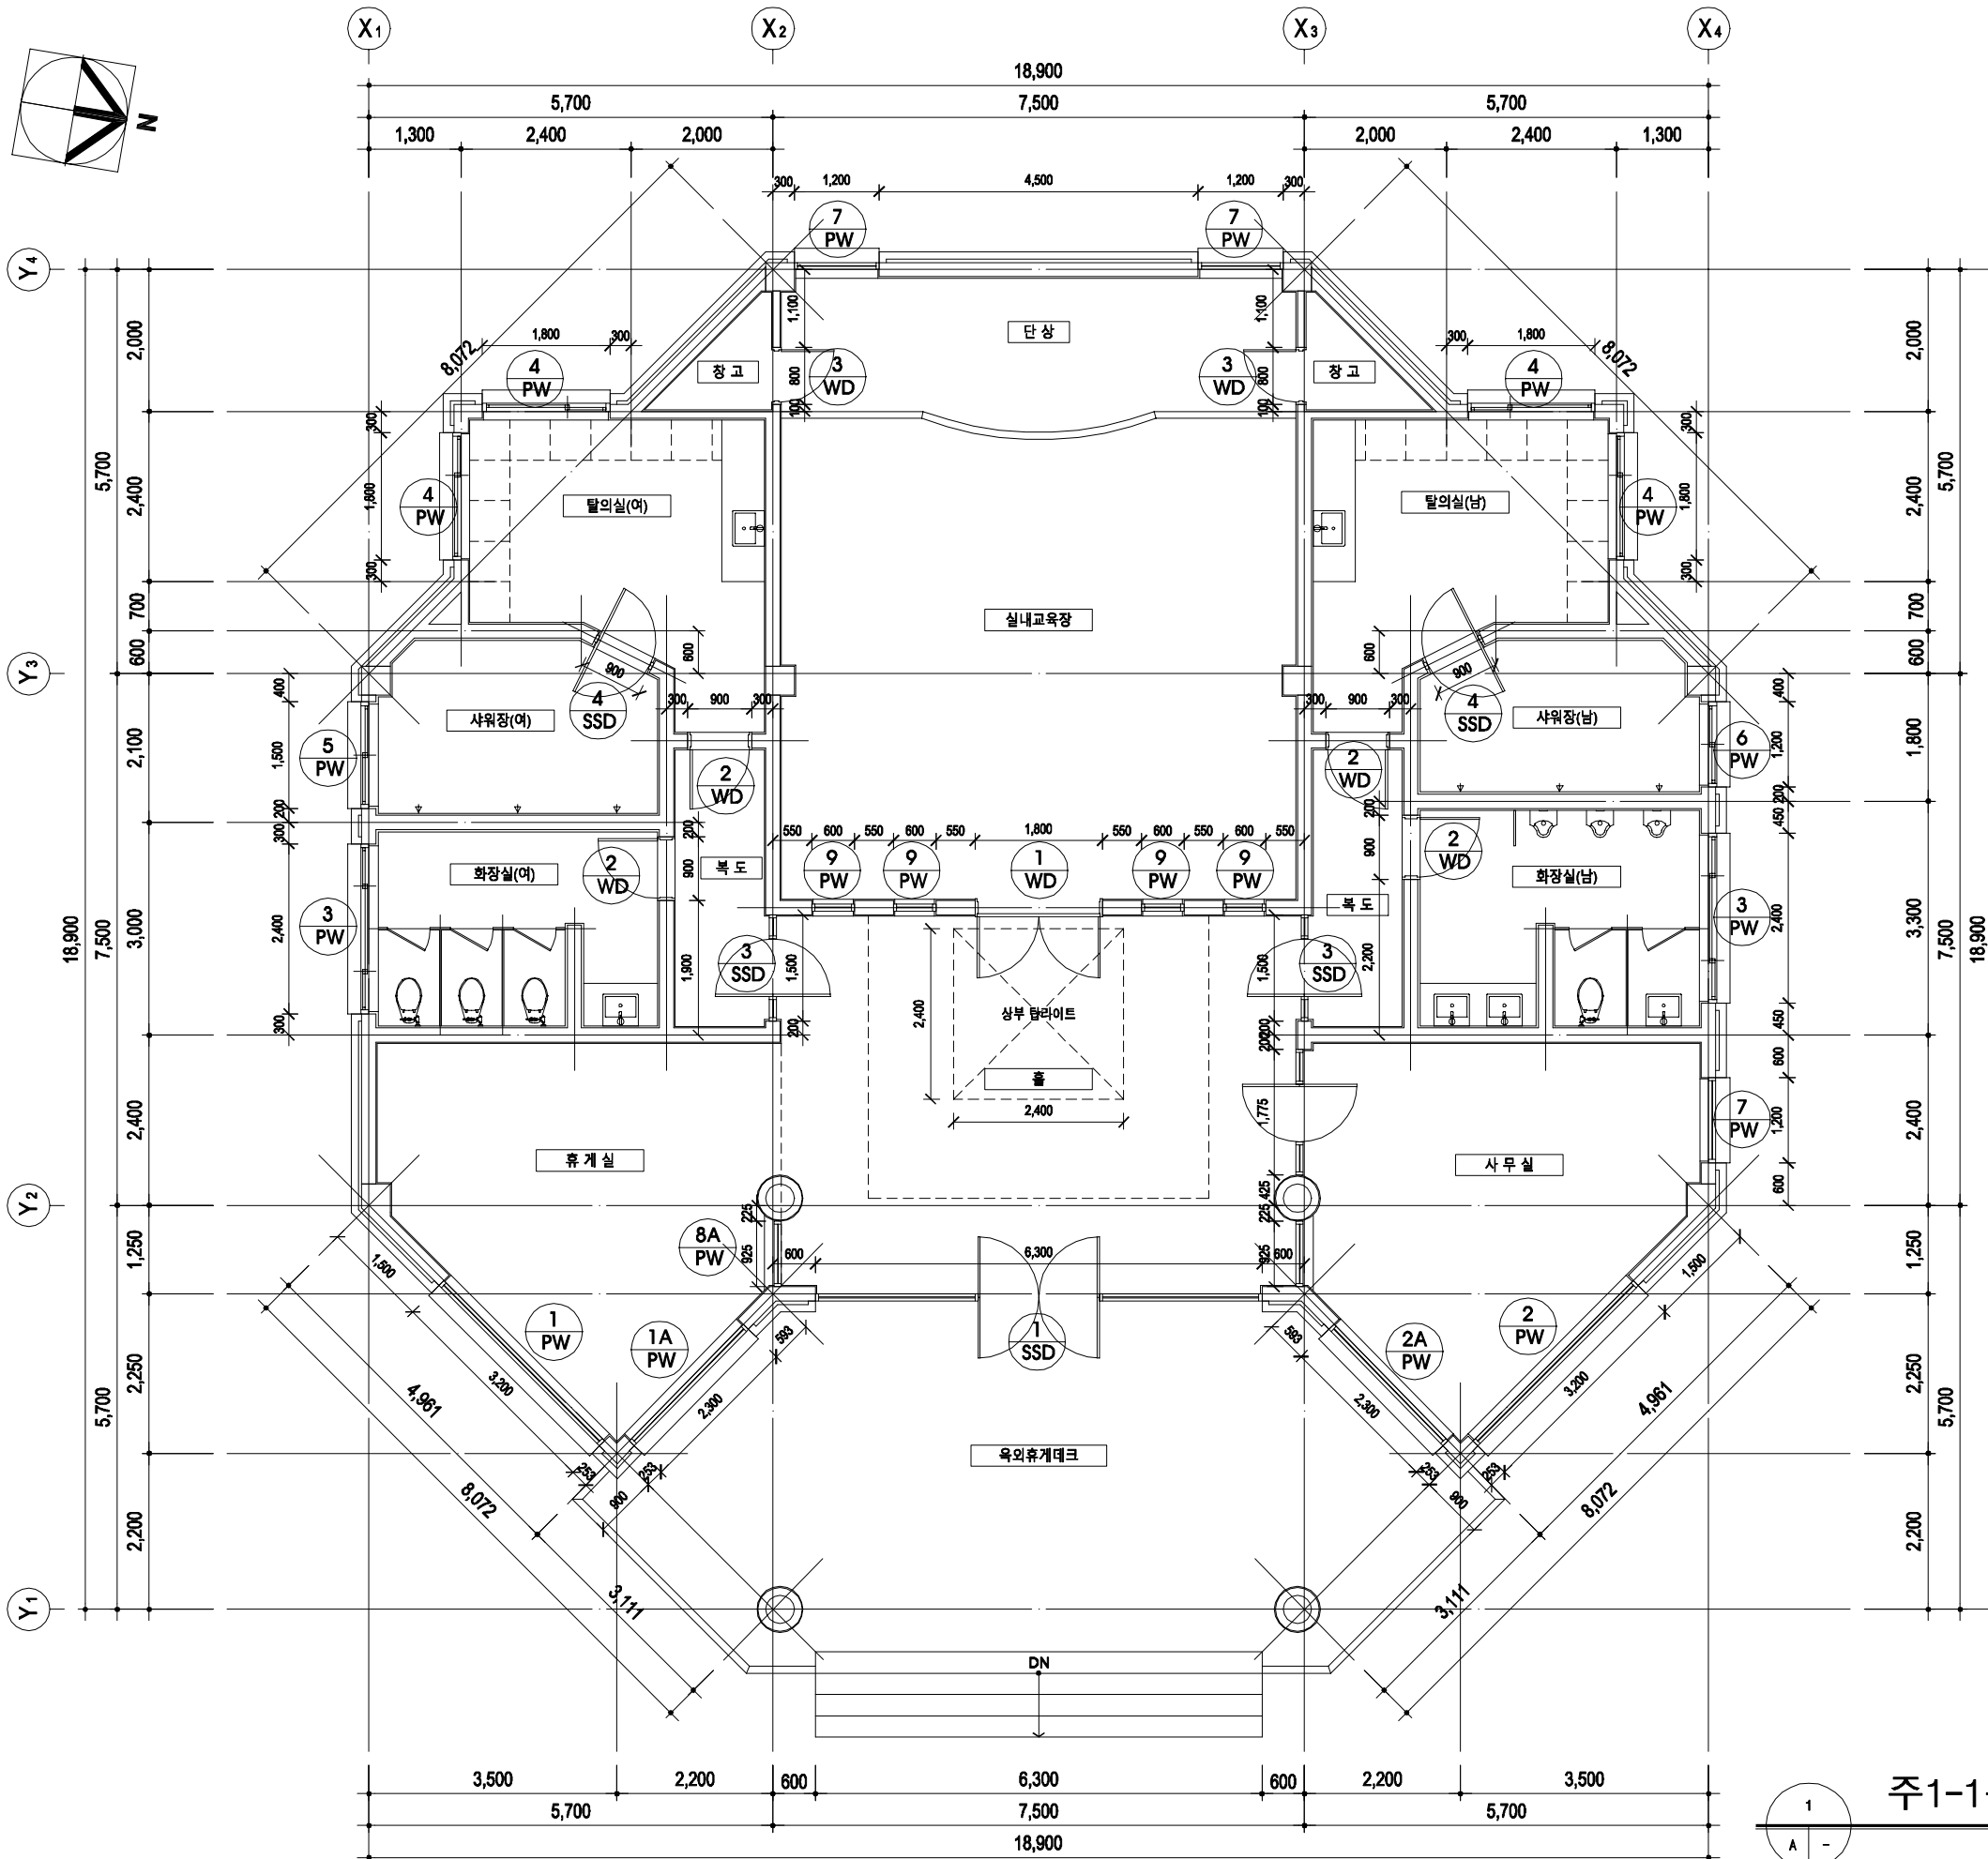

주1-1층 창호평면도(철거)

축척 A1:1/50, A3:1/100

PROJECT TITLE

리틀 포레스트  
봉뜨락 조성사업

PROJECT NO

NOTE

KEY PLAN

DESIGN CORP.

**이음** (주)이음건축사사무소

ADD. 대구광역시 중구 장동로 81, 5F  
TEL. 053.716.0776 FAX. 0505.720.0776  
E-mail. e-ul2020@naver.com  
Web. eul2020 / 0776

APPROVED BY

대표이사/건축사 권오섭

CHECKED BY

DRAWN BY

DATE

2023. 04.

DRAWING TITLE

주1-1층 창호평면도  
(철거)

SCALE

A3 : 1/ 100

DRAWING NO.

A01- 1011

1  
A -

주1-창호 일람표-1(철거)

축척 A1:1/40, A3:1/80

|           |                                        
|-----------|----------------------------------------|--|--|--|----|----|---|----|-----|--|--|----|----|----|----|--|-----|--|----|----|----|----|---|--|--|----|----|---|----|--|--|--|----|----|---|
| 부 호       | 1                                      |  |  |  | 1F | RF | 계 |    | 3   |  |  |    | 1F | RF | 계  |  | 4   |  |    |    | 1F | RF | 계 |  |  |    |    |   |    |  |  |  |    |    |   |
| 개 소       | SSD                                    |  |  |  | 1  | -  | 1 |    | SSD |  |  |    | 2  | -  | 2  |  | SSD |  |    |    | 2  | -  | 2 |  |  |    |    |   |    |  |  |  |    |    |   |
| 벽면 마감 기준선 |                                        |  
| 위 치       | 홀                                      |  |  
| 재 료       | 문틀: 45x100x1.2t 스테레스 각접기(내부:1.6t 철판보강) |  |  
| 철 물       | 후로아한지(K8,400이상 80~120kg용), 보조키, 손잡이 2조 |  |  
| 유 리       | THK12 강화유리문 / FIX: THK8 강화유리           |  |  
| 마 감       | 창틀주위 우레탄충진, 창틀주위 10x10 수밀코킹            |  |  
| 부 호       | 1                                      |  |  |  | 1F | RF | 계 | 2  |     |  |  | 1F | RF | 계  | 1  |  |     |  | 1F | RF | 계  | 1A |   |  |  | 1F | RF | 계 |    |  |  |  |    |    |   |
| 개 소       | WD                                     |  |  |  | 1  | -  | 1 | WD |     |  |  | 4  | -  | 4  | WD |  |     |  | 2  | -  | 2  | PW |   |  |  | 1  | -  | 1 | PW |  |  |  | 1  | -  | 1 |
| 벽면 마감 기준선 |                                        |  
| 위 치       | 실내교육장                                  |  |  
| 재 료       | 문틀: 45x250 라왕                          |  |  
| 철 물       | 황동도어록 2조, 4"황동경첩 6개                    |  |  
| 유 리       | FIX: THK5 투명유리                         |  |  
| 마 감       | 창틀주위 우레탄충진, 창틀주위 10x10 수밀코킹            |  |  
| 부 호       | 2                                      |  |  |  | 1F | RF | 계 | 2A |     |  |  | 1F | RF | 계  | 3  |  |     |  | 1F | RF | 계  | 4  |   |  |  | 1F | RF | 계 | 5  |  |  |  | 1F | RF | 계 |
| 개 소       | PW                                     |  |  |  | 1  | -  | 1 | PW |     |  |  | 1  | -  | 1  | PW |  |     |  | 2  | -  | 2  | PW |   |  |  | 4  | -  | 4 | PW |  |  |  | 1  | -  | 1 |
| 벽면 마감 기준선 |                                        |  
| 위 치       | 사무실                                    |  |  
| 재 료       | 115mm 플라스틱 BAR                         |  |  
| 철 물       | 크리센트 등 부속품 일체 / 방충망(내부)                |  |  
| 유 리       | THK16 복층유리                             |  |  
| 마 감       | 창틀주위 우레탄충진, 창틀주위 10x10 수밀코킹            |  |  
| 부 호       |                                        |  
| 개 소       |                                        |  
| 벽면 마감 기준선 |                                        |  
| 위 치       | 사무실                                    |  |  
| 재 료       | 115mm 플라스틱 BAR                         |  |  
| 철 물       | 크리센트 등 부속품 일체 / 방충망(내부)                |  |  
| 유 리       | THK16 복층유리                             |  |  
| 마 감       | 창틀주위 우레탄충진, 창틀주위 10x10 수밀코킹            |  |  
| 부 호       |                                        |  
| 개 소       |                                        |  
| 벽면 마감 기준선 |                                        |  
| 위 치       | 창 고                                    |  |  
| 재 료       | 문틀: 45x250 라왕                          |  |  
| 철 물       | 황동도어록 1조, 4"황동경첩 3개                    |  |  
| 유 리       | -                                      |  |  
| 마 감       | 창틀주위 우레탄충진, 창틀주위 10x10 수밀코킹            |  |  
| 부 호       |                                        |  
| 개 소       |                                        |  
| 벽면 마감 기준선 |                                        |  
| 위 치       | 휴게실                                    |  |  
| 재 료       | 115mm 플라스틱 BAR                         |  |  
| 철 물       | 크리센트 등 부속품 일체 / 방충망(내부)                |  |  
| 유 리       | THK16 복층유리                             |  |  
| 마 감       | 창틀주위 우레탄충진, 창틀주위 10x10 수밀코킹            |  |  |  |    |    |   |    |     |  |  |    |    |    |    |  |     |  |    |    |    |    |   |  |  |    |    |   |    |  |  |  |    |    |   |
| 부 호       |                                        |  |  |  |    |    |   |    |     |  |  |    |    |    |    |  |     |  |    |    |    |    |   |  |  |    |    |   |    |  |  |  |    |    |   |
| 개 소       |                                        |  |  |  |    |    |   |    |     |  |  |    |    |    |    |  |     |  |    |    |    |    |   |  |  |    |    |   |    |  |  |  |    |    |   |
| 벽면 마감 기준선 |                                        |  |  |  |    |    |   |    |     |  |  |    |    |    |    |  |     |  |    |    |    |    |   |  |  |    |    |   |    |  |  |  |    |    |   |
| 위 치       | 휴게실                                    |  |  |  |    |    |   |    |     |  |  |    |    |    |    |  |     |  |    |    |    |    |   |  |  |    |    |   |    |  |  |  |    |    |   |
| 재 료       | 115mm 플라스틱 BAR                         |  |  |  |    |    |   |    |     |  |  |    |    |    |    |  |     |  |    |    |    |    |   |  |  |    |    |   |    |  |  |  |    |    |   |
| 철 물       | 크리센트 등 부속품 일체 / 방충망(내부)                |  |  |  |    |    |   |    |     |  |  |    |    |    |    |  |     |  |    |    |    |    |   |  |  |    |    |   |    |  |  |  |    |    |   |
| 유 리       | THK16 복층유리                             |  |  |  |    |    |   |    |     |  |  |    |    |    |    |  |     |  |    |    |    |    |   |  |  |    |    |   |    |  |  |  |    |    |   |
| 마 감       | 창틀주위 우레탄충진, 창틀주위 10x10 수밀코킹            |  |  |  |    |    |   |    |     |  |  |    |    |    |    |  |     |  |    |    |    |    |   |  |  |    |    |   |    |  |  |  |    |    |   |
| 부 호       |                                        |  |  |  |    |    |   |    |     |  |  |    |    |    |    |  |     |  |    |    |    |    |   |  |  |    |    |   |    |  |  |  |    |    |   |
| 개 소       |                                        |  |  |  |    |    |   |    |     |  |  |    |    |    |    |  |     |  |    |    |    |    |   |  |  |    |    |   |    |  |  |  |    |    |   |
| 벽면 마감 기준선 |                                        |  |  |  |    |    |   |    |     |  |  |    |    |    |    |  |     |  |    |    |    |    |   |  |  |    |    |   |    |  |  |  |    |    |   |
| 위 치       | 휴게실                                    |  |  |  |    |    |   |    |     |  |  |    |    |    |    |  |     |  |    |    |    |    |   |  |  |    |    |   |    |  |  |  |    |    |   |
| 재 료       | 115mm 플라스틱 BAR                         |  |  |  |    |    |   |    |     |  |  |    |    |    |    |  |     |  |    |    |    |    |   |  |  |    |    |   |    |  |  |  |    |    |   |
| 철 물       | 크리센트 등 부속품 일체 / 방충망(내부)                |  |  |  |    |    |   |    |     |  |  |    |    |    |    |  |     |  |    |    |    |    |   |  |  |    |    |   |    |  |  |  |    |    |   |
| 유 리       | THK16 복층유리                             |  |  |  |    |    |   |    |     |  |  |    |    |    |    |  |     |  |    |    |    |    |   |  |  |    |    |   |    |  |  |  |    |    |   |
| 마 감       | 창틀주위 우레탄충진, 창틀주위 10x10 수밀코킹            |  |  
| 부 호       |                                        |  
| 개 소       |                                        |  
| 벽면 마감 기준선 |                                        |  
| 위 치       | 창 고                                    |  |  
| 재 료       | 문틀: 45x250 라왕                          |  |  
| 철 물       | 황동도어록 1조, 4"황동경첩 3개                    |  |  
| 유 리       | -                                      |  |  
| 마 감       | 창틀주위 우레탄충진, 창틀주위 10x10 수밀코킹            |  |  
| 부 호       |                                        |  
| 개 소       |                                        |  
| 벽면 마감 기준선 |                                        |  
| 위 치       | 창 고                                    |  |  
| 재 료       | 문틀: 45x250 라왕                          |  |  
| 철 물       | 황동도어록 1조, 4"황동경첩 3개                    |  |  
| 유 리       | -                                      |  |  
| 마 감       | 창틀주위 우레탄충진, 창틀주위 10x10 수밀코킹            |  |  
| 부 호       |                                        |  
| 개 소       |                                        |  
| 벽면 마감 기준선 |                                        |  
| 위 치       | 화장실 (남,여)                              |  |  
| 재 료       | 115mm 플라스틱 BAR                         |  |  
| 철 물       | 크리센트 등 부속품 일체 / 이동식 방충망                |  |  
| 유 리       | THK16 복층유리                             |  |  
| 마 감       | 창틀주위 우레탄충진, 창틀주위 10x10 수밀코킹            |  |  
| 부 호       |                                        |  
| 개 소       |                                        |  
| 벽면 마감 기준선 |                                        |  
| 위 치       | 탈의실 (남,여)                              |  |  
| 재 료       | 115mm 플라스틱 BAR                         |  |  
| 철 물       | 크리센트 등 부속품 일체 / 이동식 방충망                |  |  
| 유 리       | THK16 복층유리                             |  |  
| 마 감       | 창틀주위 우레탄충진, 창틀주위 10x10 수밀코킹            |  |  
| 부 호       |                                        |  
| 개 소       |                                        |  
| 벽면 마감 기준선 |                                        |  
| 위 치       | 사위장 (여)                                |  |  
| 재 료       | 115mm 플라스틱 BAR                         |  |  
| 철 물       | 크리센트 등 부속품 일체 / 이동식 방충망                |  |  
| 유 리       | THK16 복층유리                             |  |  
| 마 감       | 창틀주위 우레탄충진, 창틀주위 10x10 수밀코킹            |  |  

PROJECT TITLE

리틀 포레스트  
봉뜨락 조성사업

PROJECT NO

NOTE

KEY PLAN

DESIGN CORP.

**이원** (주)이원건축사사무소

ADD. 대구광역시 중구 장동로 81, 5F  
TEL. 053.716.0776 FAX. 0505.720.0776  
E-mail. e-ul2020@naver.com  
Web. eul2020 / 0776

APPROVED BY  
대표이사 / 건축사 권오섭  
CHECKED BY

DRAWN BY


DATE 2023. 04.

DRAWING TITLE

주1-창호 일람표-1  
(철거)

SCALE A3 : 1/ 80

DRAWING NO. A01- 1012

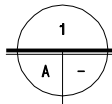

주1-창호 일람표-2(철거)

축척 A1:1/40, A3:1/80

| 부 호           | 6                           | 1F | RF | 계 | 7                           | 1F | RF | 계 | 8A                          | 1F | RF | 계 | 9                           | 1F | RF | 계 |
|---------------|-----------------------------|----|----|---|-----------------------------|----|----|---|-----------------------------|----|----|---|-----------------------------|----|----|---|
| 개 소           | PW                          | 1  | -  | 1 | PW                          | 3  | -  | 3 | PW                          | 1  | -  | 1 | PW                          | 4  | -  | 4 |
| 벽면마감 기준선<br>▼ |                             |    |    |   |                             |    |    |   |                             |    |    |   |                             |    |    |   |
|               |                             |    |    |   |                             |    |    |   |                             |    |    |   |                             |    |    |   |
|               | 사위장 (남)                     |    |    |   | 사무실, 실내교육장                  |    |    |   | 휴게실                         |    |    |   | 실내교육장                       |    |    |   |
|               | 115mm 플라스틱 BAR              |    |    |   | 115mm 플라스틱 BAR              |    |    |   | 100mm 플라스틱 BAR              |    |    |   | 100mm 플라스틱 BAR              |    |    |   |
|               | 크리센트 등 부속품 일체 / 이동식 방충망     |    |    |   | 크리센트 등 부속품 일체 / 방충망(내부)     |    |    |   | 부속품 일체                      |    |    |   | 부속품 일체                      |    |    |   |
| 유 리           | THK16 복층유리                  |    |    |   | THK16 복층유리                  |    |    |   | THK16 복층유리                  |    |    |   | THK16 복층유리                  |    |    |   |
| 마 감           | 창틀주위 우레탄충진, 창틀주위 10x10 수밀코킹 |    |    |   | 창틀주위 우레탄충진, 창틀주위 10x10 수밀코킹 |    |    |   | 창틀주위 우레탄충진, 창틀주위 10x10 수밀코킹 |    |    |   | 창틀주위 우레탄충진, 창틀주위 10x10 수밀코킹 |    |    |   |
| 부 호           |                             |    |    |   |                             |    |    |   |                             |    |    |   |                             |    |    |   |
| 개 소           |                             |    |    |   |                             |    |    |   |                             |    |    |   |                             |    |    |   |
|               |                             |    |    |   |                             |    |    |   |                             |    |    |   |                             |    |    |   |
PROJECT TITLE

리틀 포레스트  
봉뜨락 조성사업

PROJECT NO

NOTE

KEY PLAN

DESIGN CORP.



ADD. 대구광역시 중구 장동로 81, 5F  
TEL. 053.716.0776 FAX. 0505.720.0776  
E-mail. e-ul2020@naver.com  
Web. eul2020 / 0776

APPROVED BY  
대표이사 / 건축사 권오섭

CHECKED BY

DRAWN BY

DATE  
2023. 04.

DRAWING TITLE  
주1-창호 일람표-2  
(철거)

SCALE  
A3 : 1/ 80

DRAWING NO.  
A01- 1013

PROJECT TITLE

리틀 포레스트  
봉뜨락 조성사업

PROJECT NO

NOTE

KEY PLAN

DESIGN CORP.

**이음** (주)이음건축사사무소

ADD. 대구광역시 동구 장동로 81, 5F  
TEL. 053.716.0776 FAX. 0505.720.0776  
E-mail. e-ul2020@naver.com  
Web. eul2020 / 0776

APPROVED BY  
대표이사/건축사 권오섭

CHECKED BY



DRAWN BY

DATE  
2023. 04.

DRAWING TITLE  
부1-1층 및 지붕 평면도(철거)


SCALE  
A3 : 1/ 50

DRAWING NO.  
A01- 1021

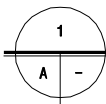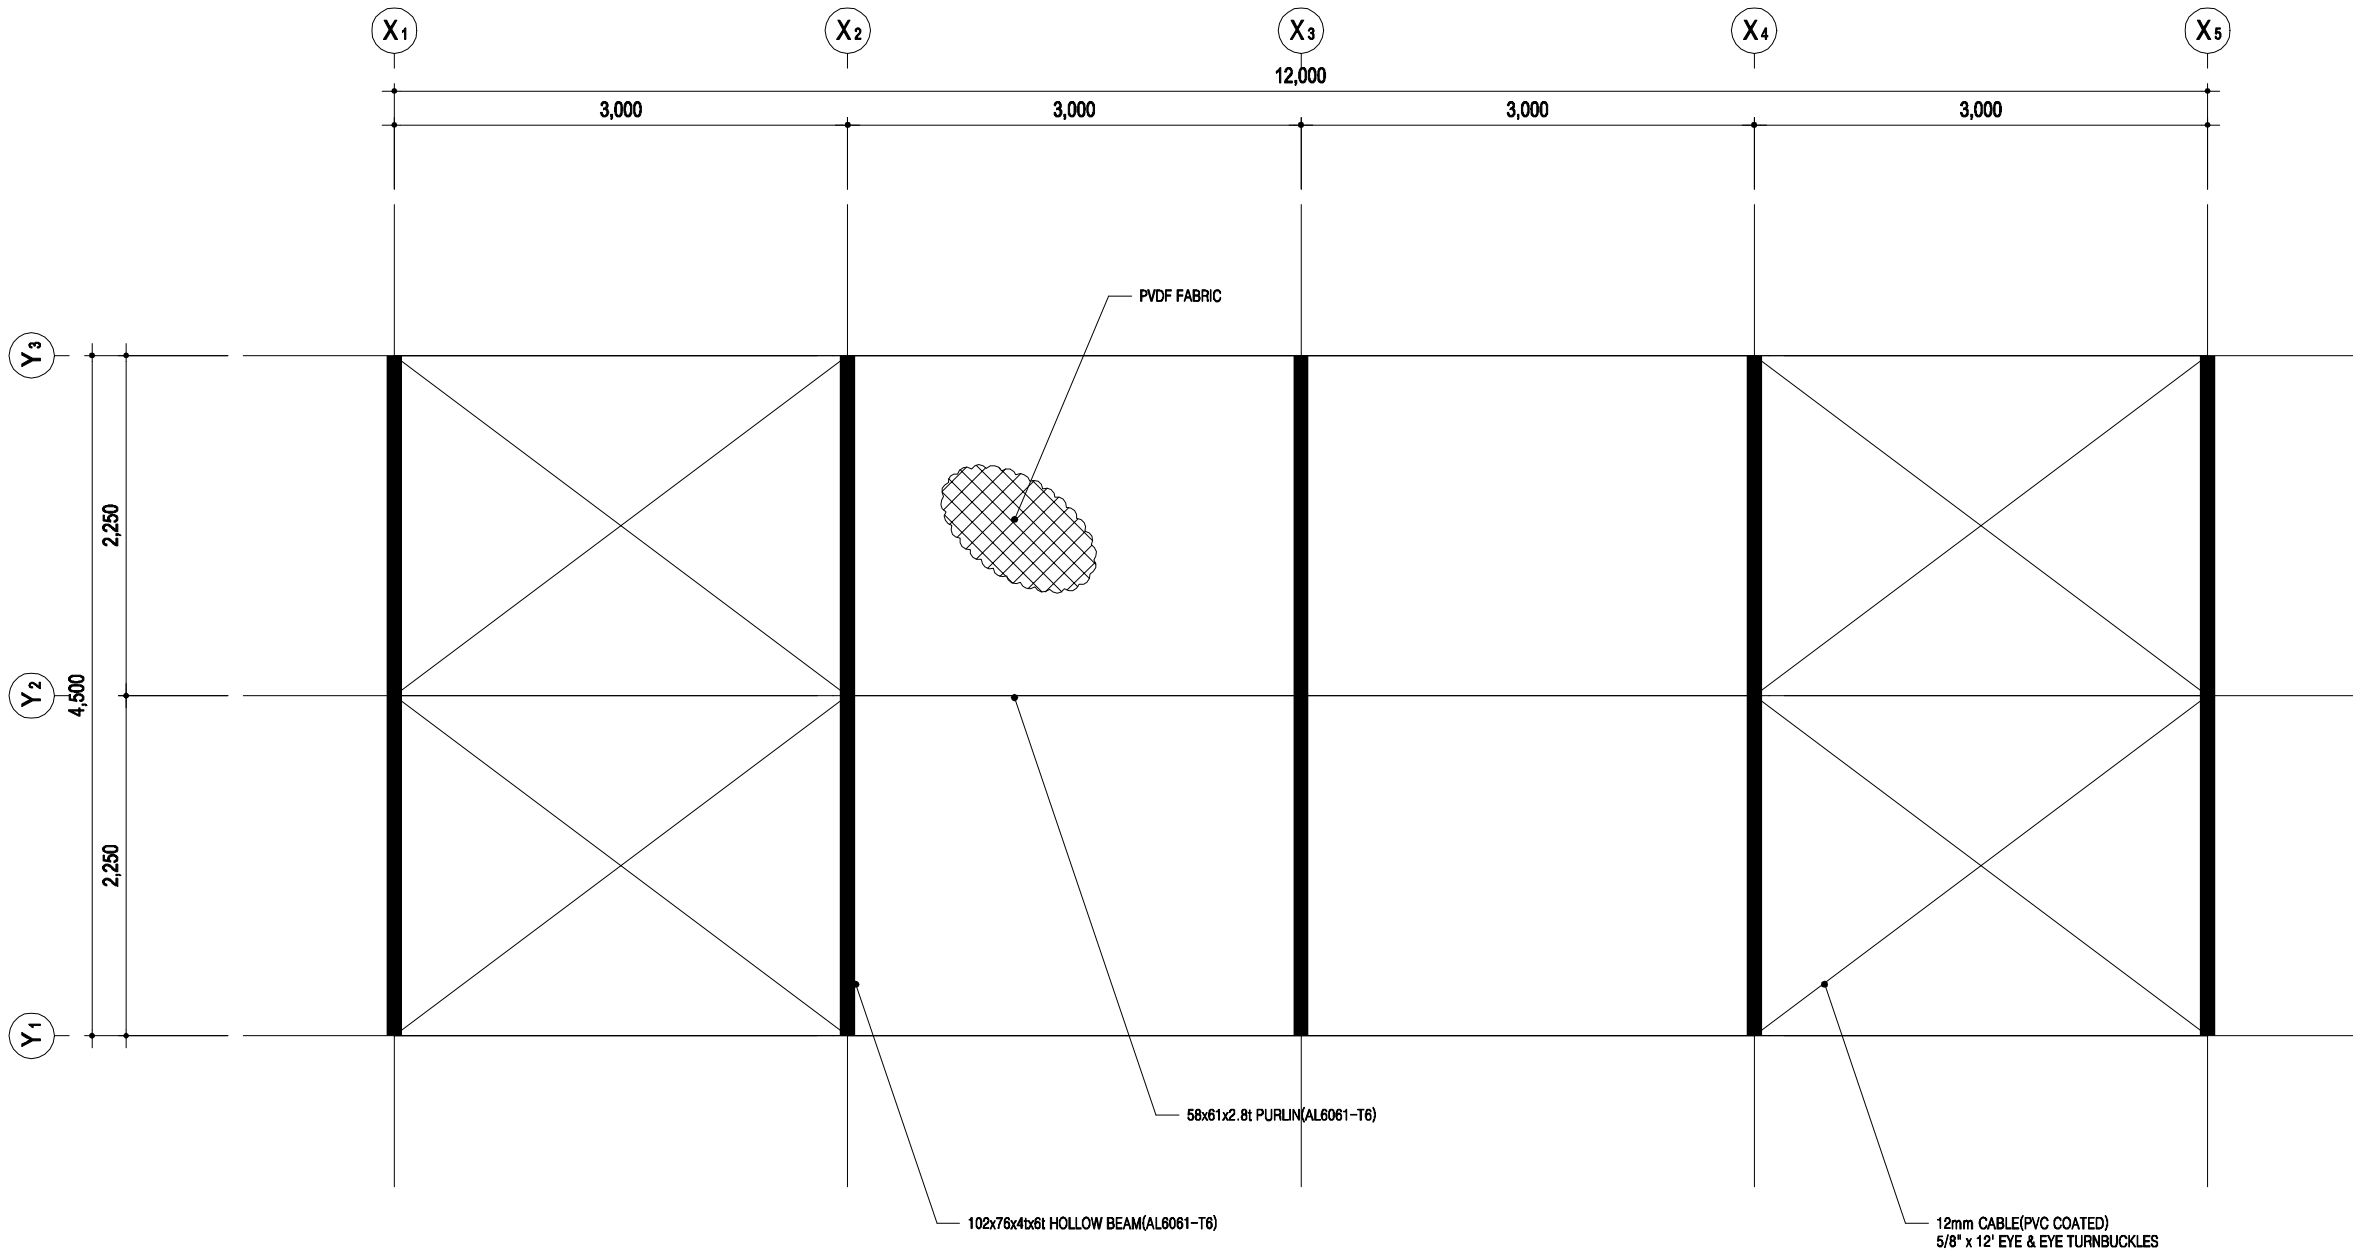


부1-1층 및 지붕 평면도(철거)

축척 A1:1/25. A3:1/50

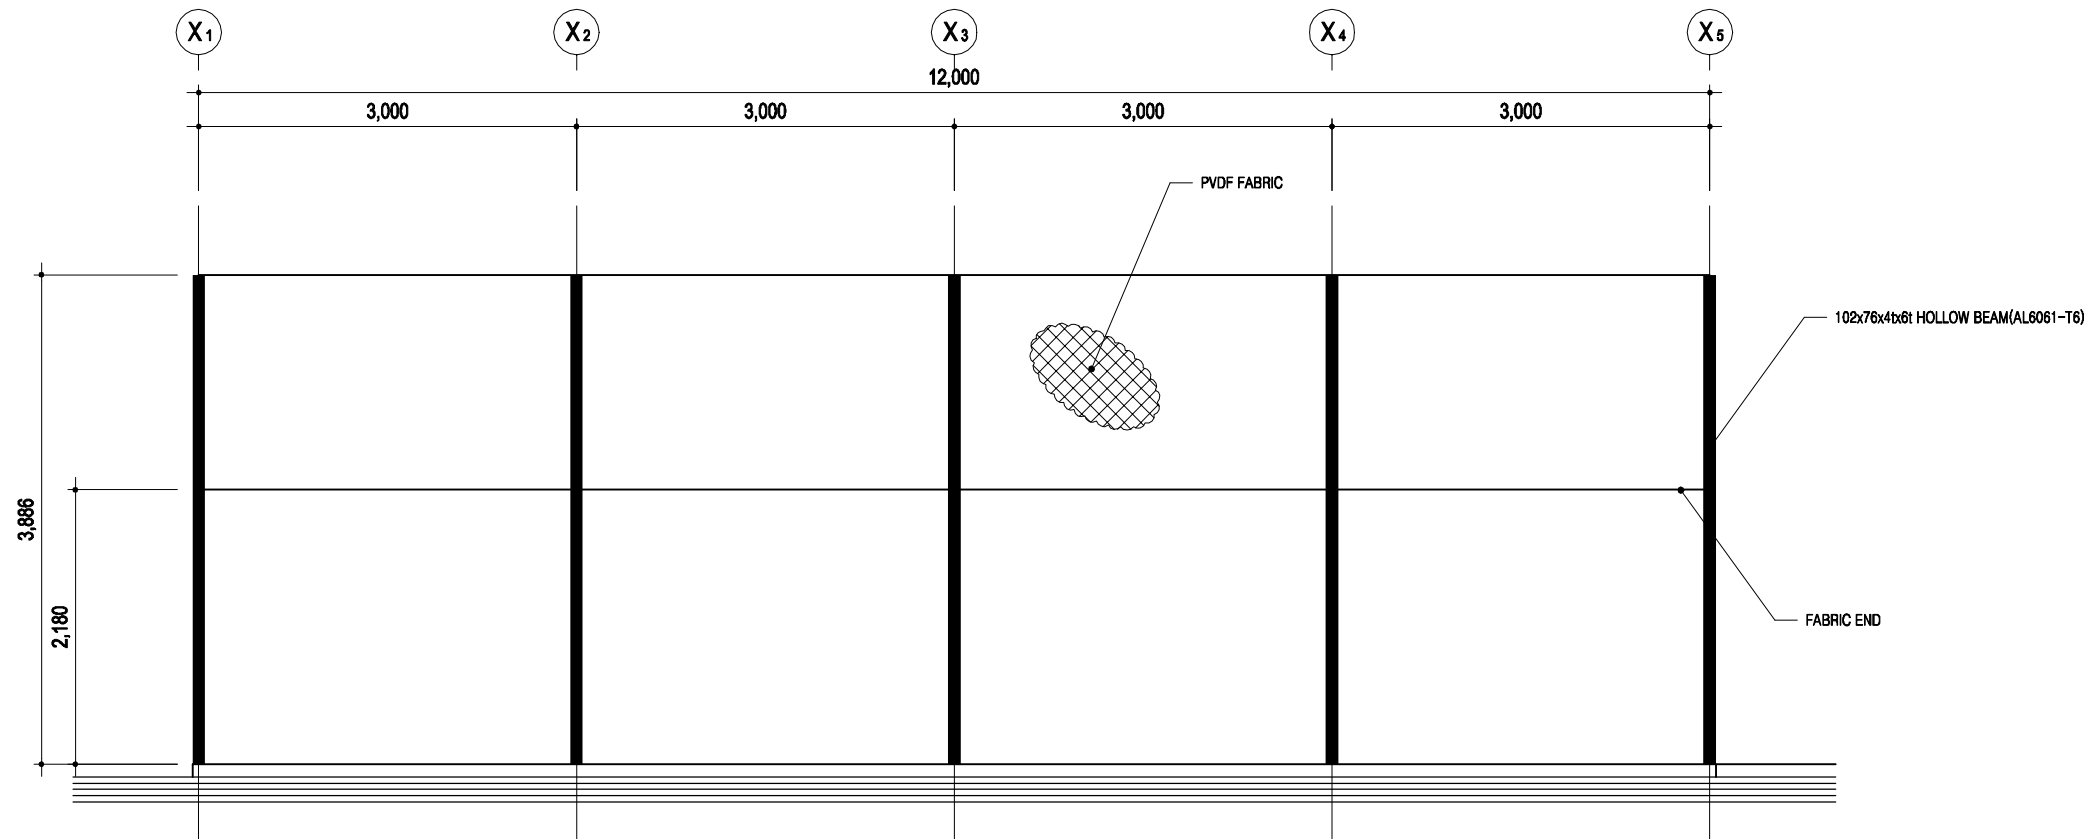

부1- 'A' 정면도(철거)

축척 A1:1/30, A3:1/60

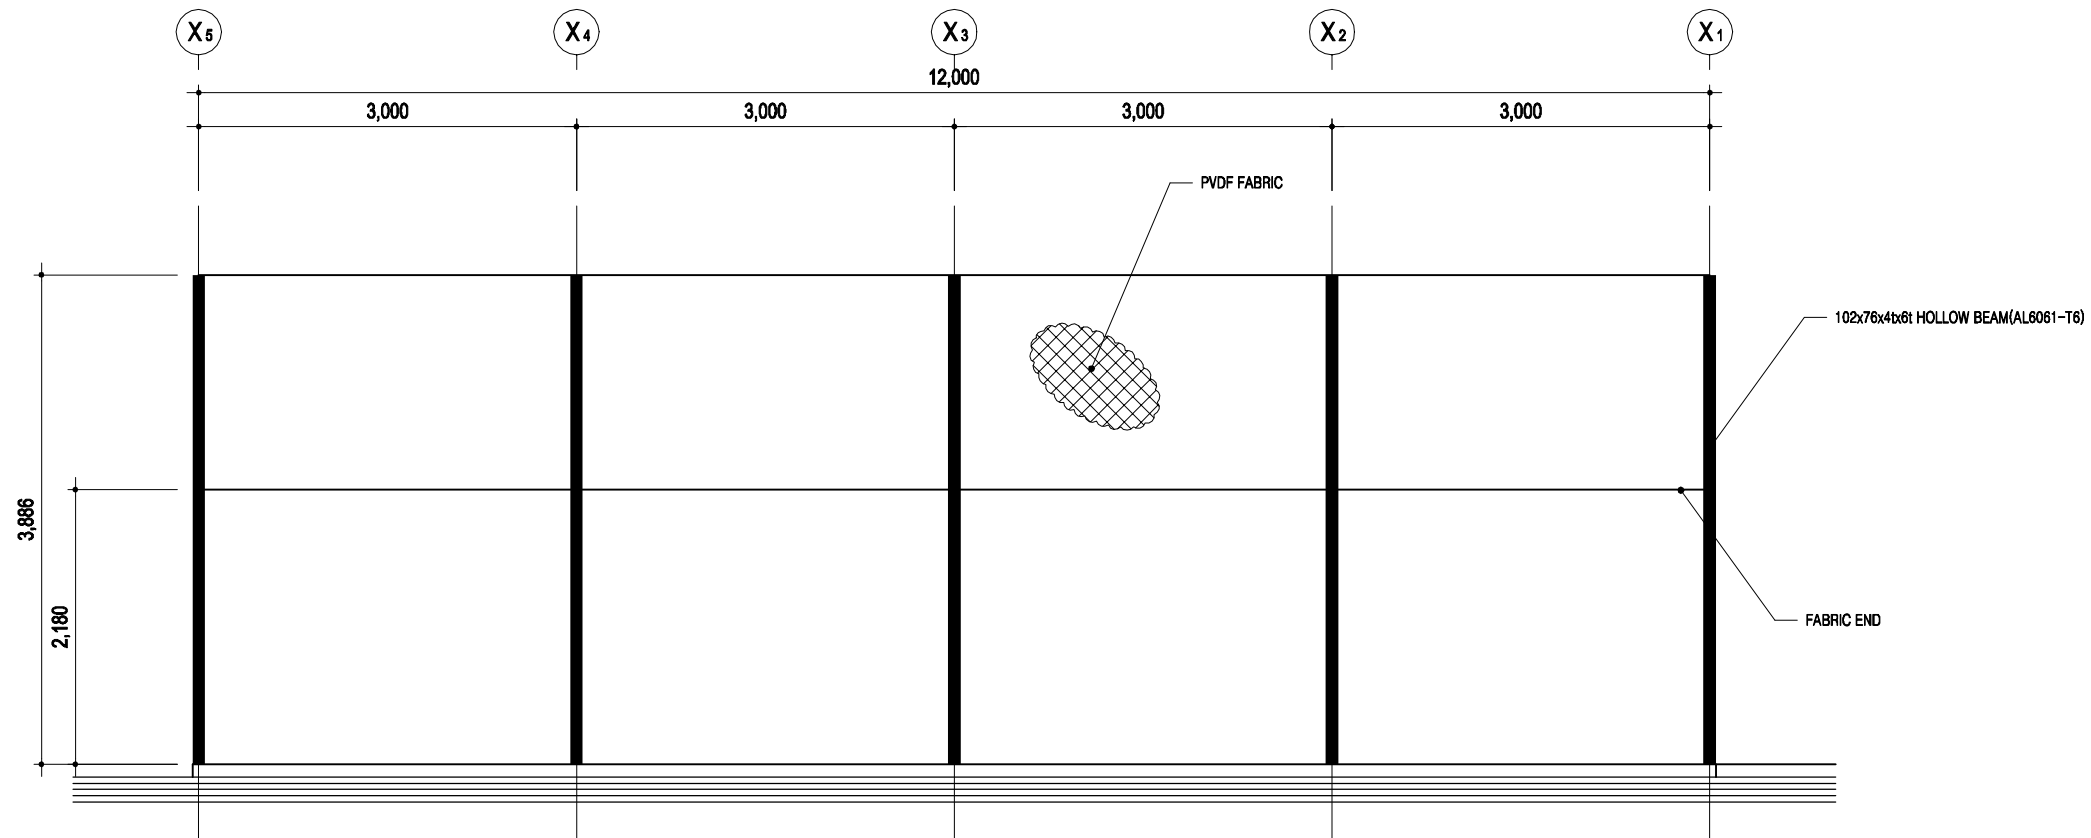

부1- 'B' 배면도(철거)

축척 A1:1/30, A3:1/60

PROJECT TITLE

리틀 포레스트  
봉뜨락 조성사업

PROJECT NO

NOTE

KEY PLAN

DESIGN CORP.

**이음** (주)이음건축사사무소

ADD. 대구광역시 중구 장동로 81, 5F  
TEL. 053.716.0776 FAX. 0505.720.0776  
E-mail. e-ul2020@naver.com  
Web. eul2020 / 0776

APPROVED BY  
대표이사/건축사 권오섭

CHECKED BY

DRAWN BY

DATE 2023. 04.

DRAWING TITLE

부1-A,B 입면도  
(기존)

SCALE A3 : 1/ 60

DRAWING NO. A01- 1022

PROJECT TITLE

리틀 포레스트  
봉뜨락 조성사업

PROJECT NO

NOTE

KEY PLAN

DESIGN CORP.

**이음** (주)이음건축사무소

ADD. 대구광역시 동구 장동로 81, 5F  
TEL. 053.716.0776 FAX. 0505.720.0776  
E-mail. e-ul2020@naver.com  
Web. eul2020 / 0776

APPROVED BY  
대표이사/건축사 권오섭

CHECKED BY



DRAWN BY

DATE  
2023. 04.

DRAWING TITLE  
부1-C,D 입면도  
(철거)



SCALE  
A3 : 1/ 50

DRAWING NO.  
A01- 1023

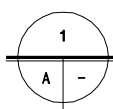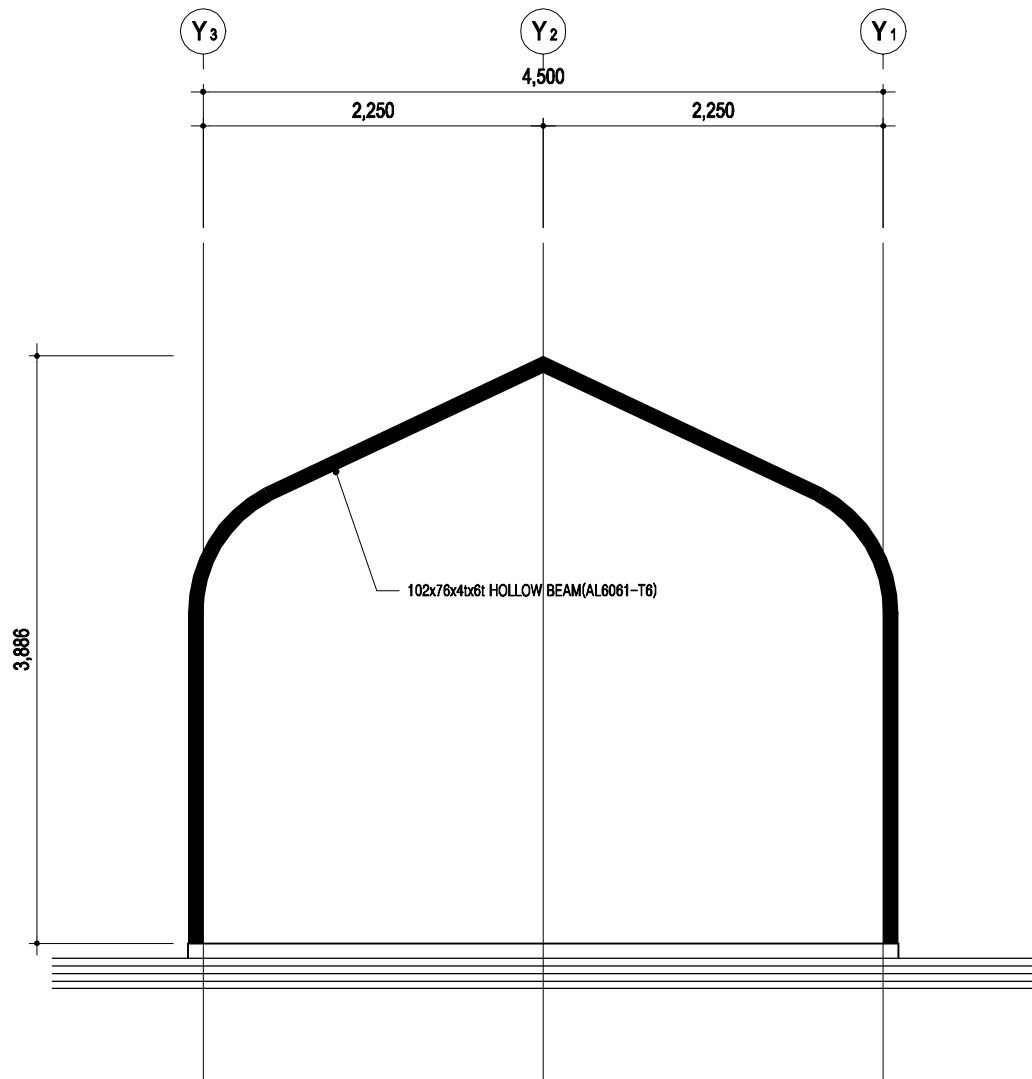

부1-\'C\' 좌측면도(철거)

축척 A1:1/25. A3:1/50

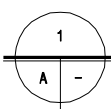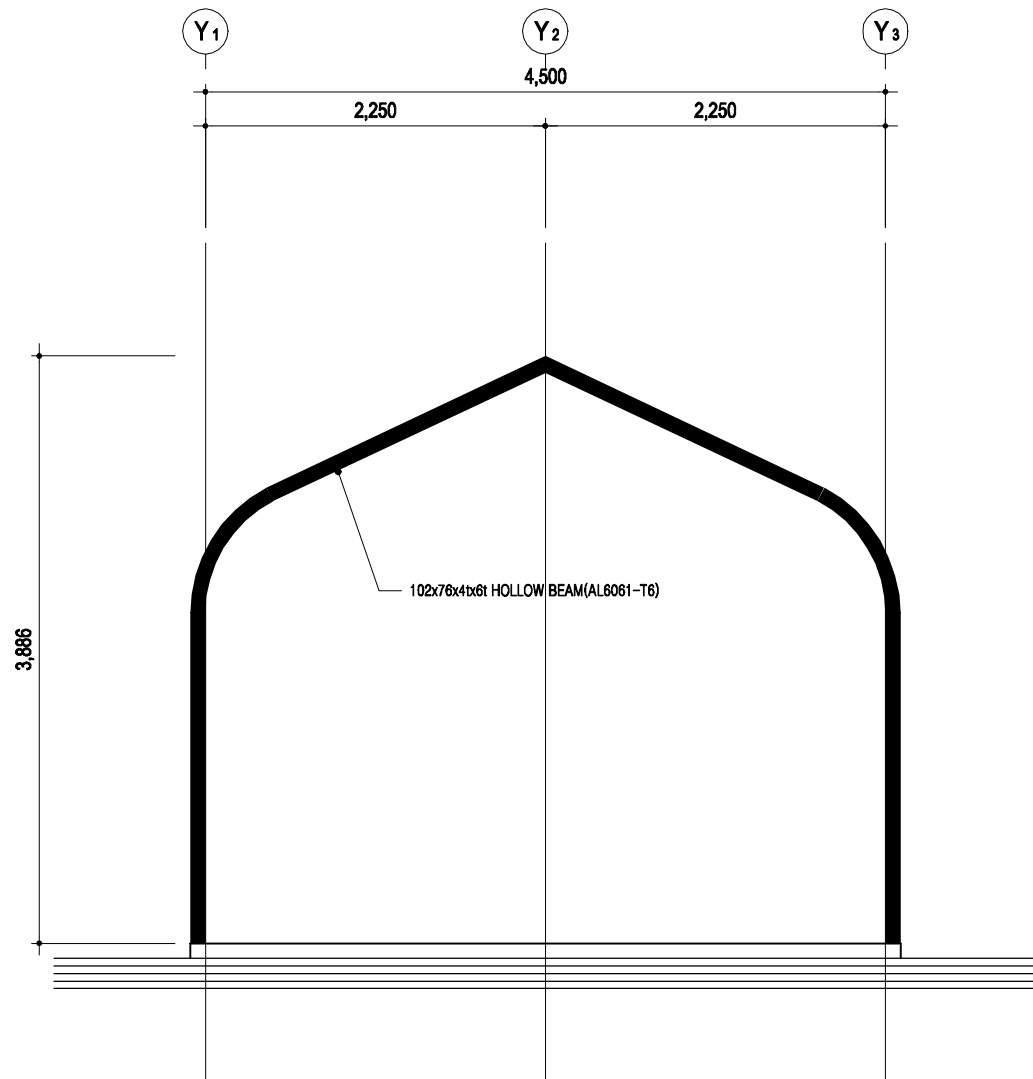

부1-\'D\' 우측면도(철거)

축척 A1:1/25. A3:1/50

PROJECT TITLE

리틀 포레스트  
봉뜨락 조성사업

PROJECT NO

NOTE

KEY PLAN

DESIGN CORP.

**이음** (주)이음건축사사무소

ADD. 대구광역시 동구 장동로 81, 5F  
TEL. 053.716.0776 FAX. 0505.720.0776  
E-mail. e-ul2020@naver.com  
Web. eul2020 / 0776

APPROVED BY  
대표이사 / 건축사 권오섭

CHECKED BY



DRAWN BY

DATE  
2023. 04.

DRAWING TITLE  
부1-주단면 상세도 (철거)


SCALE  
A3 : 1/ 20

DRAWING NO.  
A01- 1024

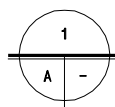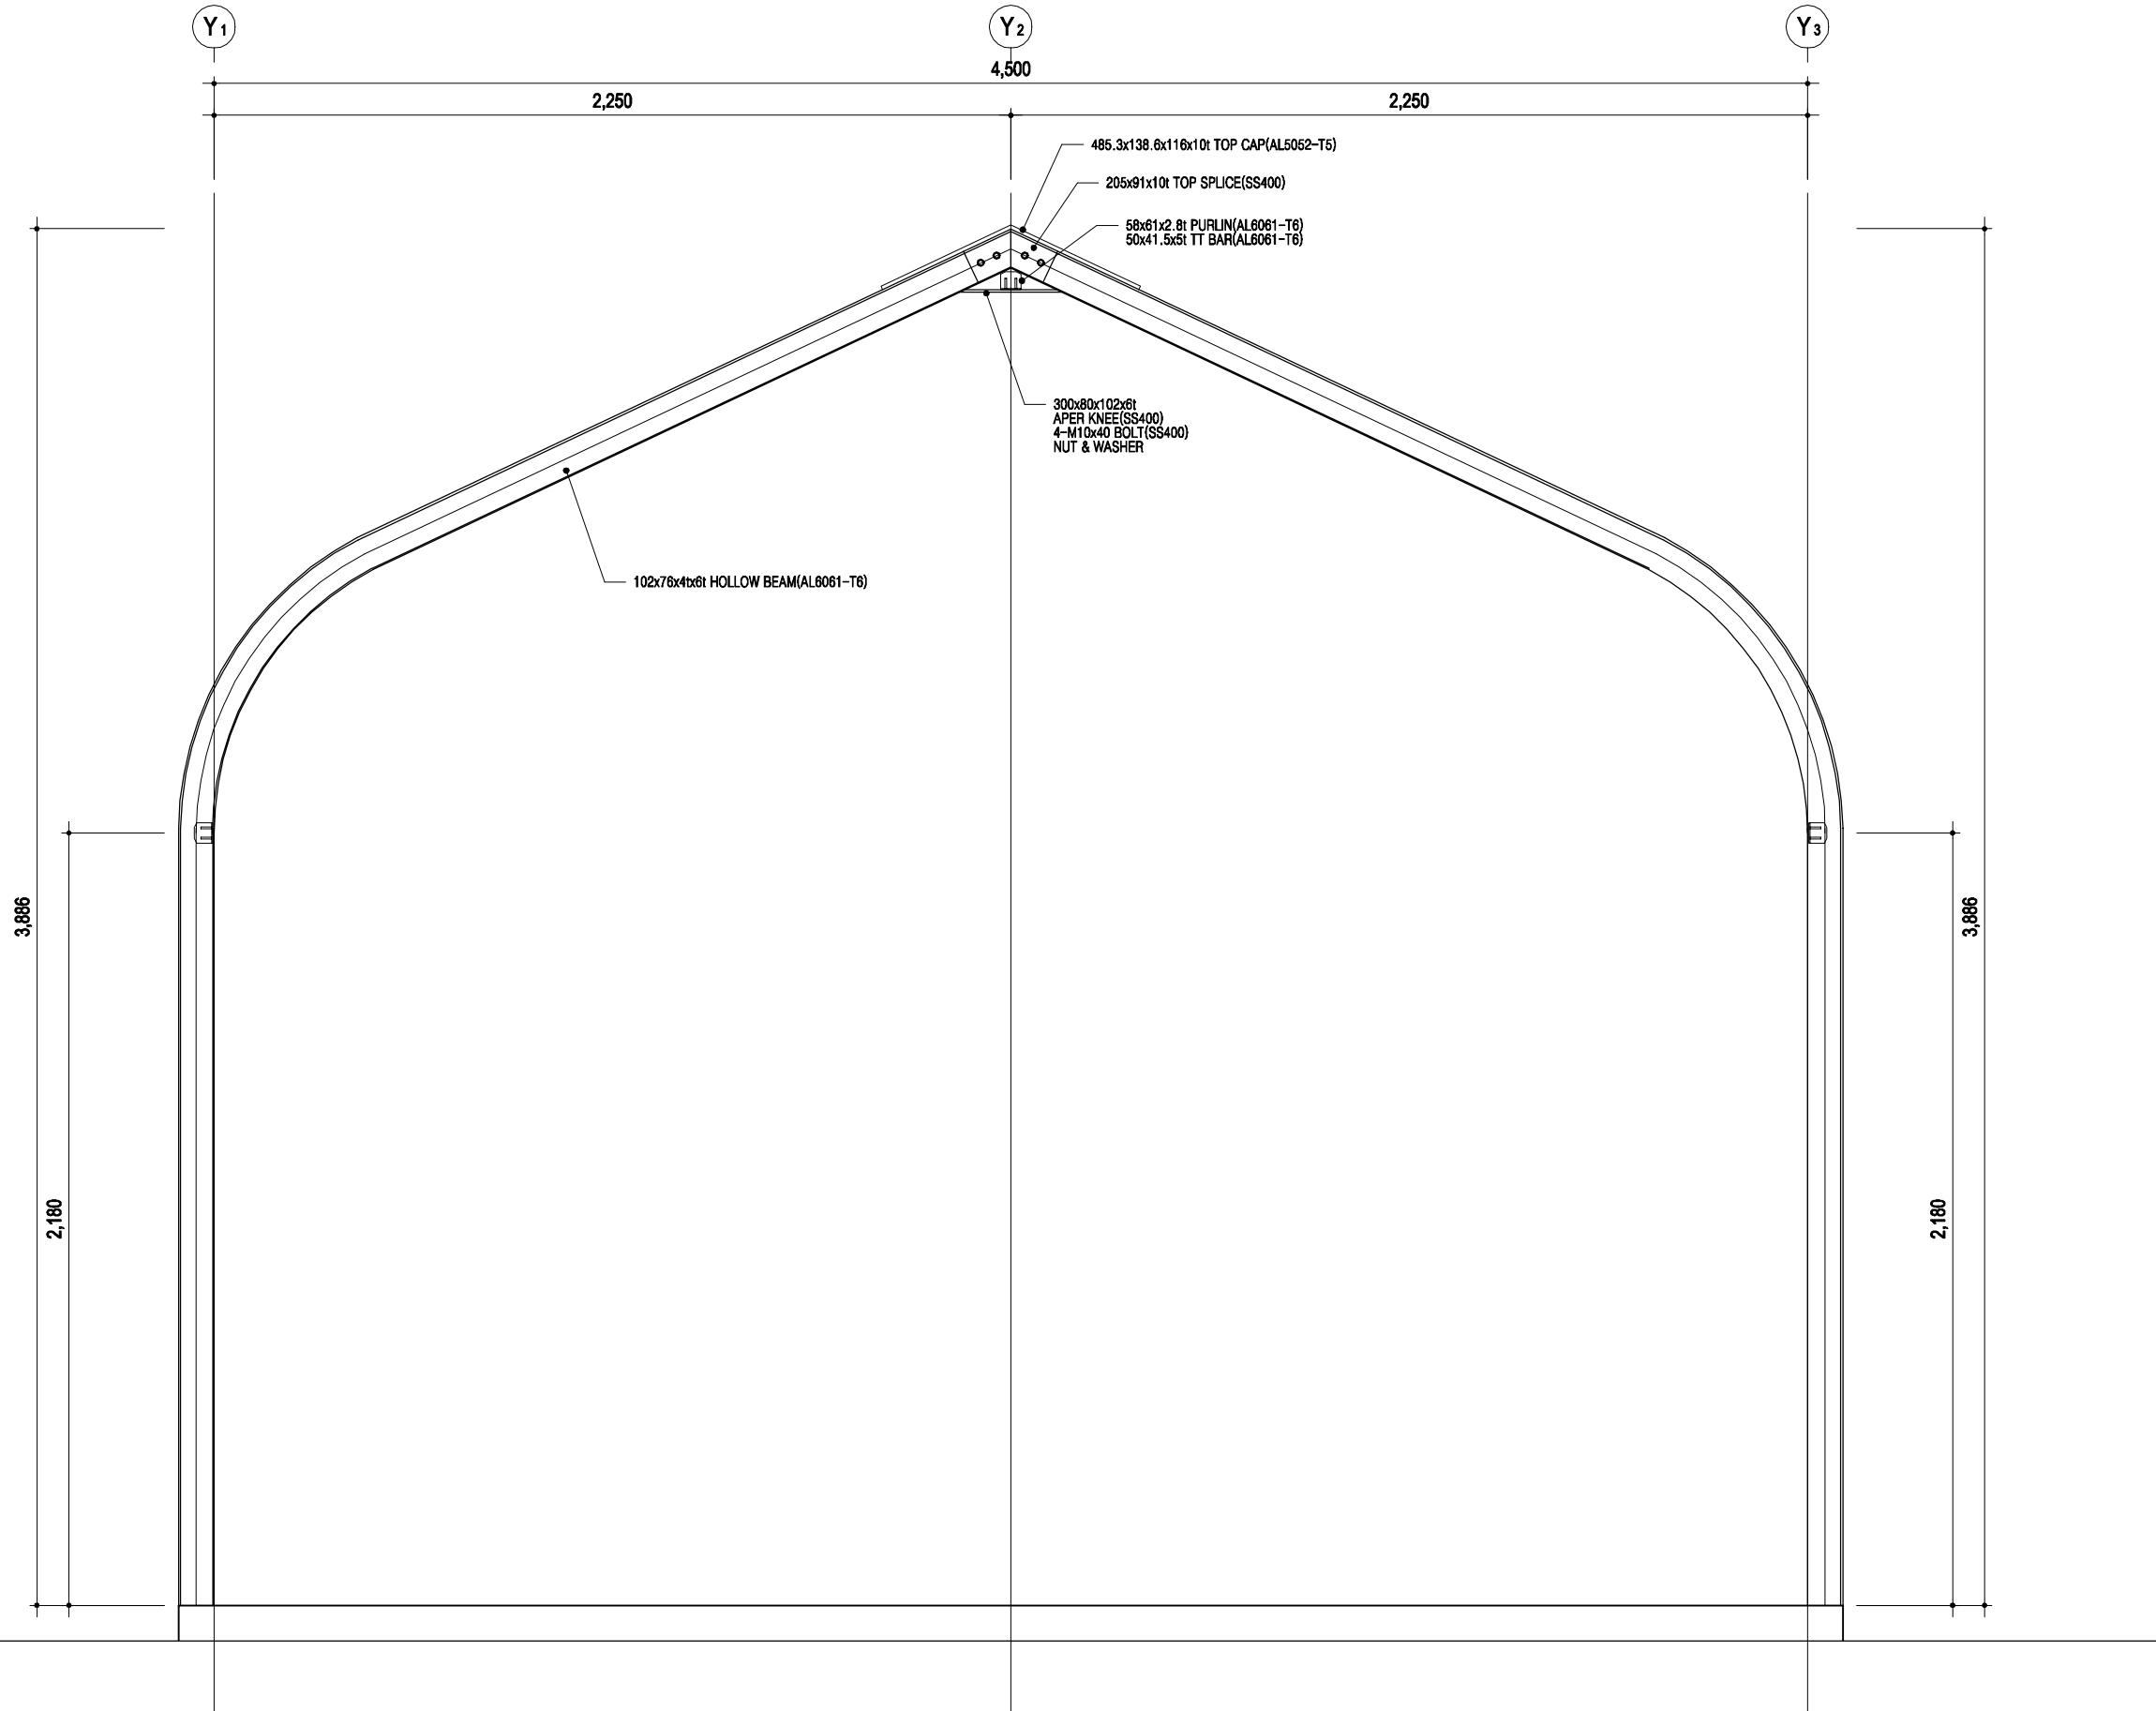

부1-주단면 상세도 (철거)

축척 A1:1/10. A3:1/20

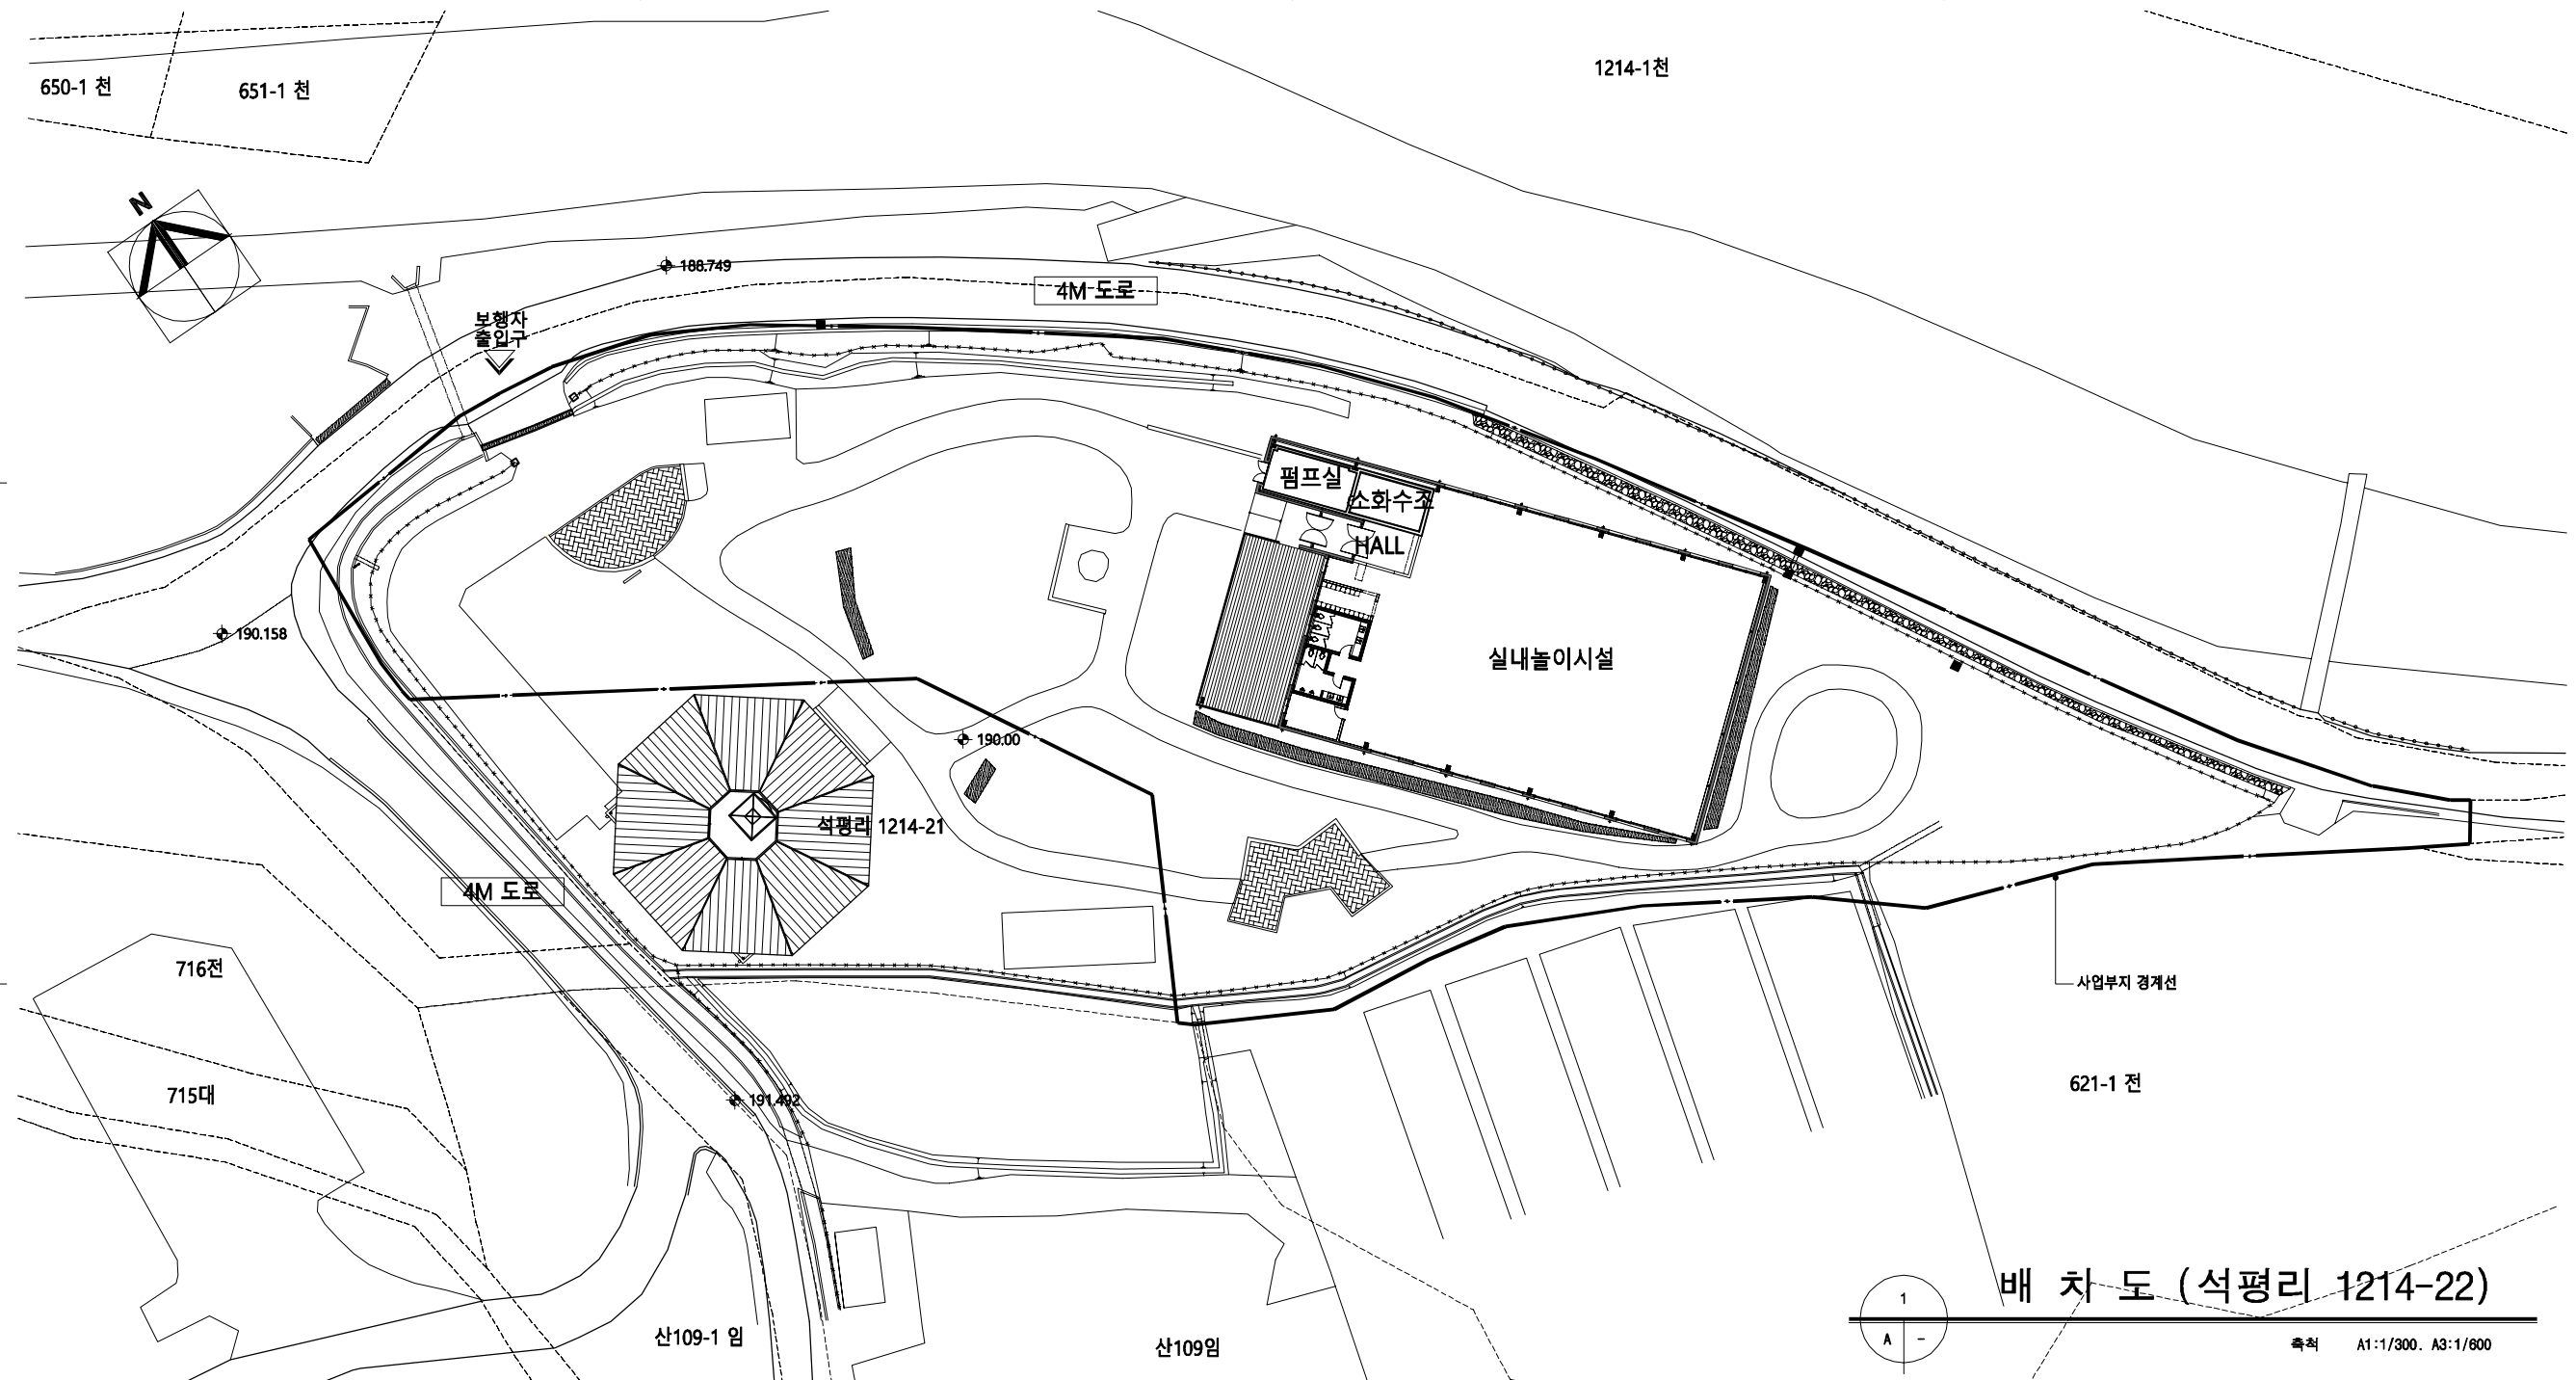

PROJECT NO.

### KEY PLAN

배 치 도 ( 석 평 리 1214-22 )

**축척** A1:1/300. A3:1/600

■ 건축 개요 (석평리 1214-22)

|         |                          |          |
|---------|--------------------------|----------|
| 대 지 위 치 | 경상북도 봉화군 봉화읍 석평리 1214-22 |          |
| 대 지 면 적 | 석평리 1214-22              | 5,009.00 |
|         |                          |          |
|         |                          |          |
|         | 계                        | 5,009.00 |
| 지 역 지 구 | 계획관리지역                   |          |
| 도 로 현 황 | 북측 : 4M도로 / 서측 : 4M도로    |          |
| 건 물 용 도 | 운동시설(놀이형 시설)             |          |
| 구 조     | 철골구조                     |          |
| 층 수     | 지상 1층                    |          |
| 건 물 높 이 | 6.55 M                   |          |

| 바 닥 면 적 | 변 경 전  |    |           |          | 변 경 후  |    |             |          |
|---------|--------|----|-----------|----------|--------|----|-------------|----------|
|         | 구분     | 층별 | 용 도       | 면 적      | 구분     | 층별 | 용 도         | 면 적      |
|         | 주1     | 1  | 운동시설(승마장) | 924.00   | 주1     | 1  | 운동시설(놀이형시설) | 924.00   |
|         |        |    |           |          |        |    |             |          |
|         | 계      |    |           | 924.00   | 계      |    |             | 924.00   |
| 건 축 면 적 | 924.00 |    |           |          | 924.00 |    |             |          |
| 연 면 적   | 924.00 |    |           |          | 924.00 |    |             |          |
| 건 폐 율   | 법 정    |    |           | 40.00 %  | 법 정    |    |             | 40.00 %  |
|         | 설 계    |    |           | 18.45 %  | 설 계    |    |             | 18.45 %  |
| 용 적 율   | 법 정    |    |           | 100.00 % | 법 정    |    |             | 100.00 % |
|         | 설 계    |    |           | 18.45 %  | 설 계    |    |             | 18.45 %  |

|        |   |                 |             |
|--------|---|-----------------|-------------|
| 주 차    | 법 정   | 해당없음.           | 0.0 대       |
|        | 설 계   | -               | 0.0 대       |
| 오수처리시설 | 법 정   | 924.00 X 15l/m³ | 13.86 (㎡/일) |
|        | 설 계   |                 | 26.00 (㎡/일) |
| 기 타    | <p>1. 건축물 표시변경사항이나 에너지절약계획대상에 해당되어 협의를 위해 용도변경신고로 진행함.</p> <p>2. 건축구조기준설계하중 (KDS 41 10 05) 기준에 따라 설계하중이 5%미만의 용도변경일 경우 구조안전확인서 제출대상에서 제외됨.</p> <p>체육시설(5.0kN/m²) → 체육시설(5.0kN/m²)로 용도변경이며 설계하중의 변경이 없으므로 구조안전확인서 제출을 제외함.</p> |                 |             |

ADD. 대구광역시 동구 장동로 81, 5F  
TEL. 053.716.0776 FAX. 0505.720.0776  
E-mail. e-ul2020@naver.com  
Web. eul2020 / 0776

APPROVED BY  
대표이사/건축사 권 오 섭

CHECKED BY

DRAWN BY


DATE 2023. 04.


DRAWING TITLE

배치도 및 건축개요  
(석평리 1214-22)

SCALE  
A3 : 1/ 600

DRAWING NO. A02-001

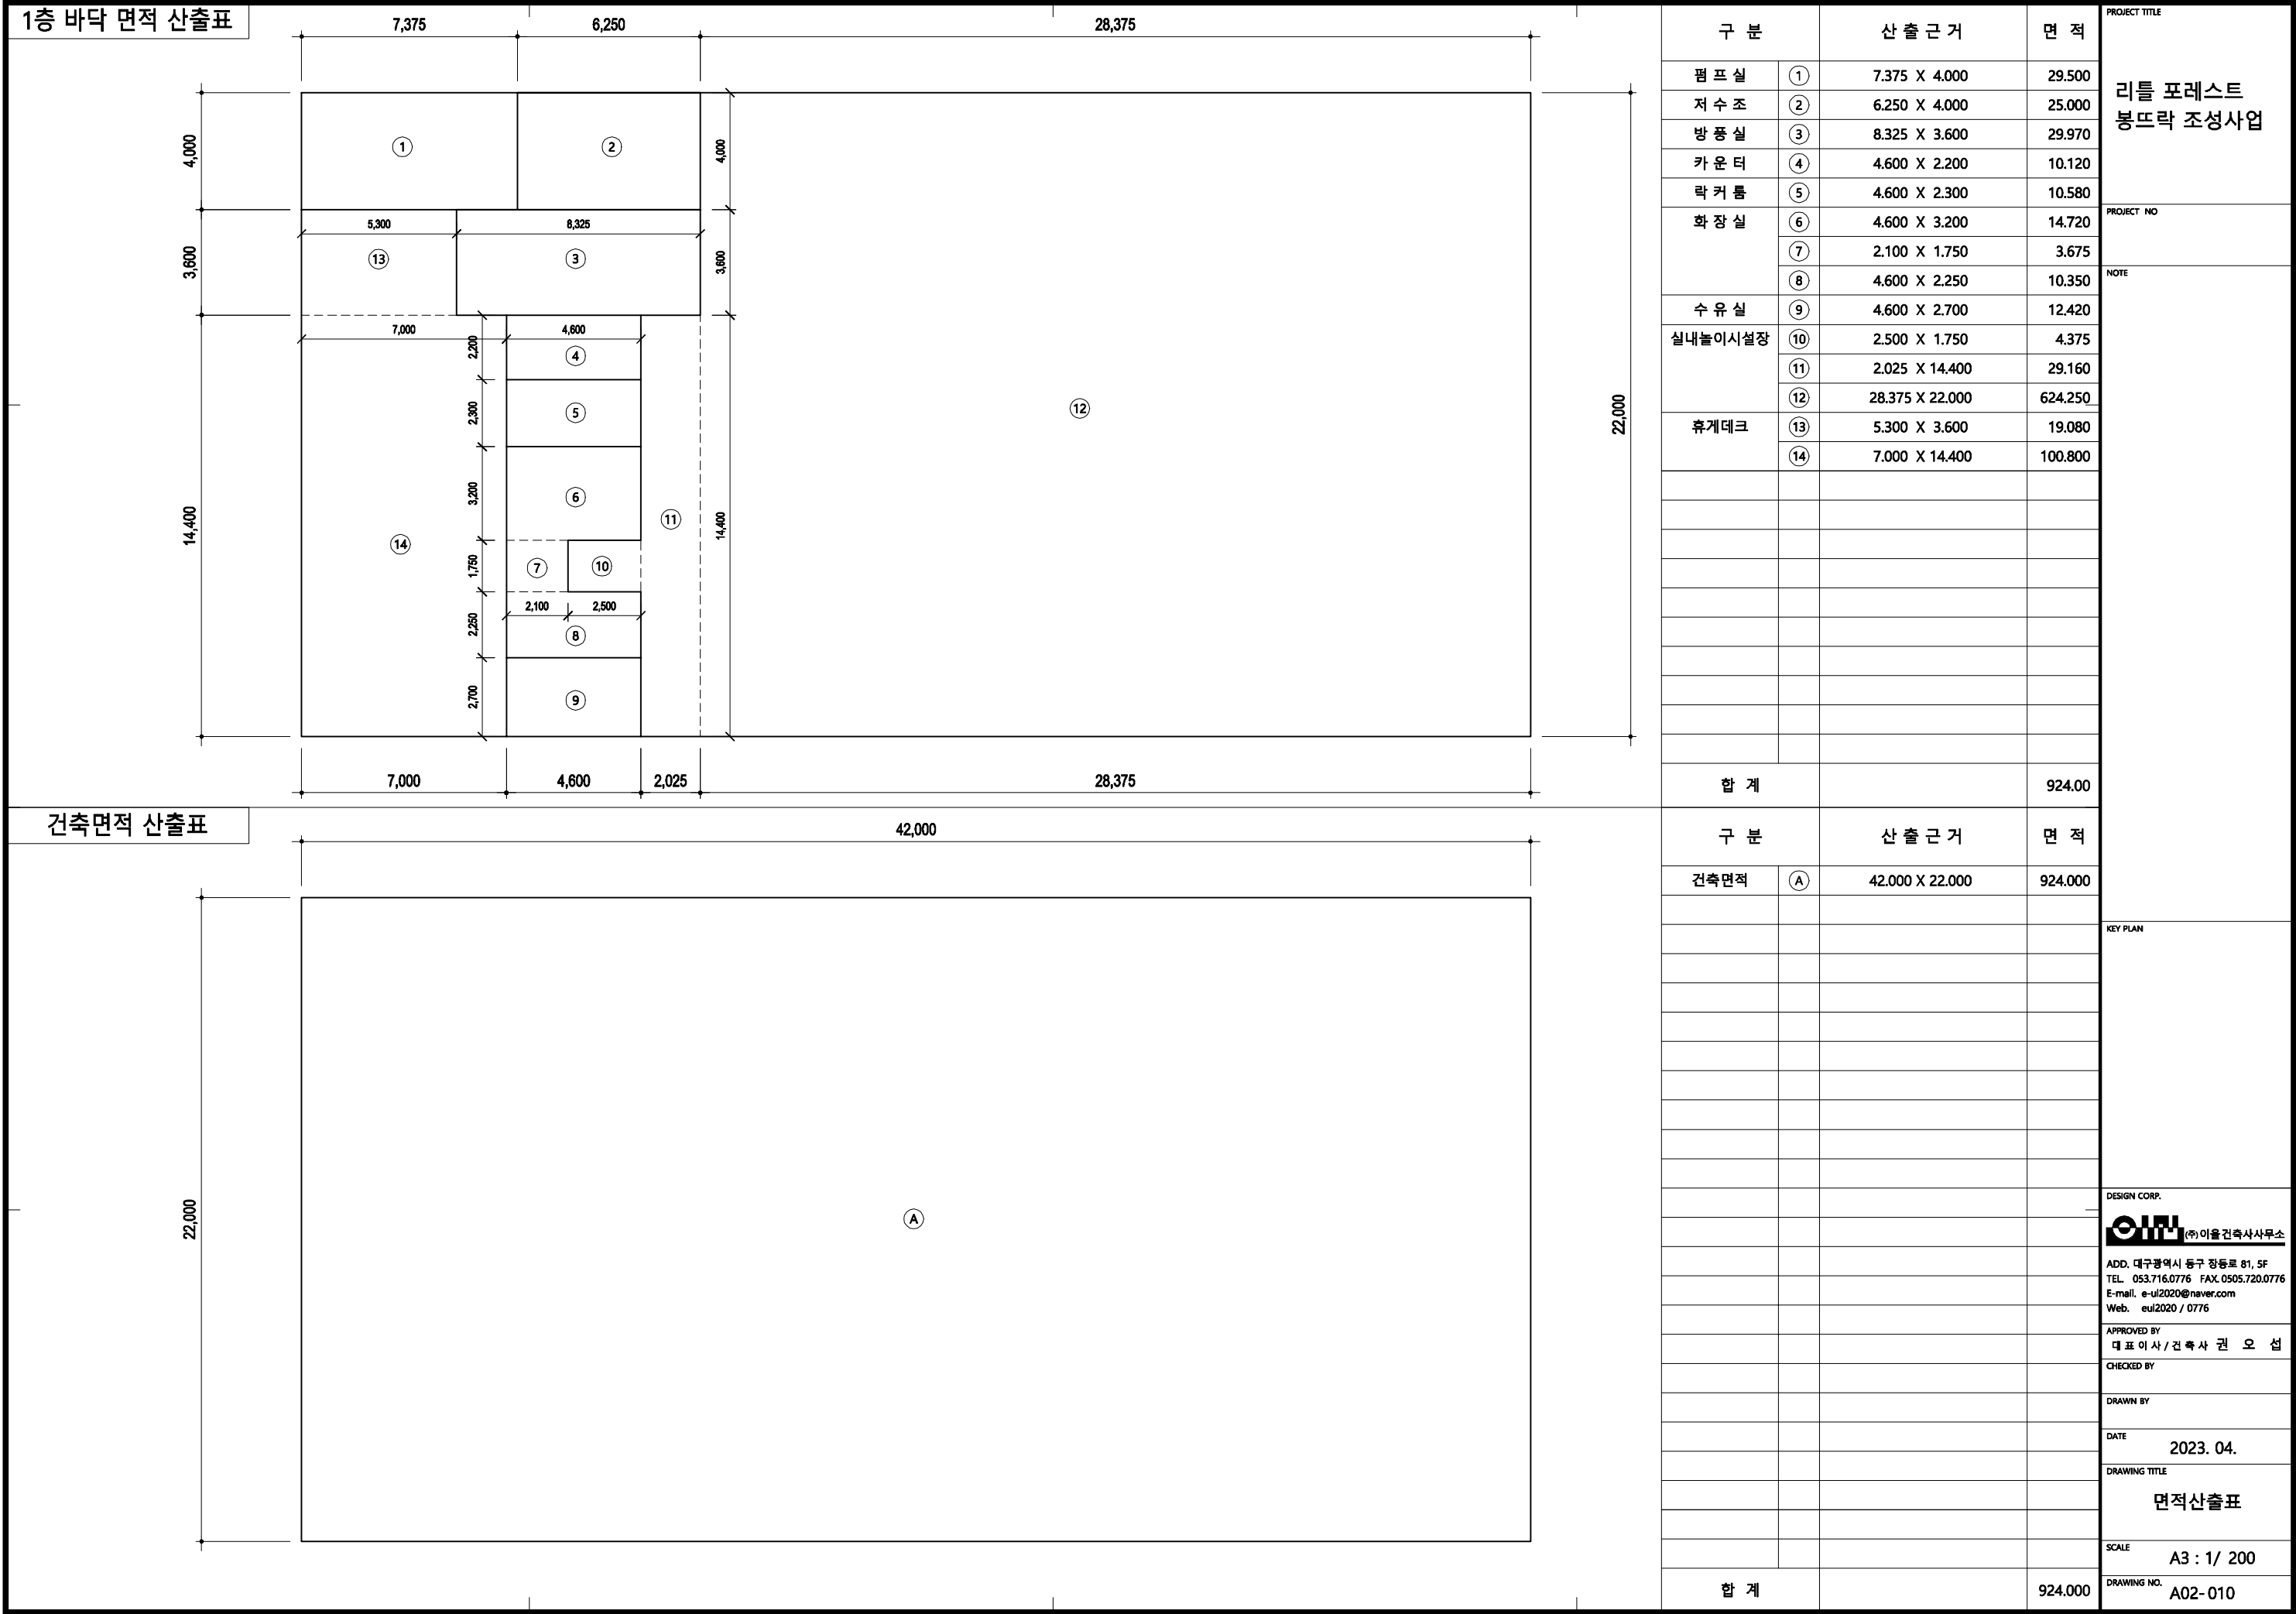

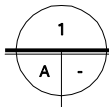

# 실내재료 마감표

축척 : 1/NONE(A1) , 1/NONE(A3)

| 구 분            | 바 닥                         |                      |     | 걸 레 받 이       |          |     | 벽                                   |                       |     | 천 장                       |                           |       | 상세번호 | 비 고 |
|----------------|-----------------------------|----------------------|-----|---------------|----------|-----|-------------------------------------|-----------------------|-----|---------------------------|---------------------------|-------|------|-----|
| 실 명            | 바 랑                         | 마 감                  | 두 께 | 바 랑           | 마 감      | 높 이 | 바 랑                                 | 마 감                   | 두 께 | 바 랑                       | 마 감                       | 천장고   |      |     |
| 방풍실            | THK70 무근콘크리트 / THK27 시멘트몰탈  | THK3 데코타일            | 100 | THK200 라인메탈판넬 | -        | 100 | THK200 라인메탈판넬                       | -                     | -   | 경량철골 천정틀(M-BAR)           | THK9.5 석고보드 2P / 수성페인트 2회 | 3,050 | 01   |     |
| HALL           | THK70 무근콘크리트 / THK27 시멘트몰탈  | THK3 데코타일            | 100 | THK20 시멘트몰탈   | 수성페인트 2회 | 100 | THK20 시멘트몰탈                         | 수성페인트 2회              | -   | 경량철골 천정틀(M-BAR)           | THK9.5 석고보드 2P / 수성페인트 2회 | 4,450 | 02A  |     |
|                |                             |                      |     | THK9.5 석고보드   |          |     | THK9.5 석고보드                         |                       |     |                           |                           |       | 02B  |     |
| 어린이 놀이시설장      | THK120 무근콘크리트 / THK27 시멘트몰탈 | THK3 데코타일            | 150 | THK20 시멘트몰탈   | 수성페인트 2회 | 100 | THK20 시멘트몰탈                         | 수성페인트 2회              | -   | 경량철골 천정틀(M-BAR)           | THK9.5 석고보드 2P / 수성페인트 2회 | 4,400 | 03A  |     |
|                |                             |                      |     | THK9.5 석고보드   |          |     | THK9.5 석고보드                         |                       |     |                           |                           |       | 03B  |     |
| 카운터            | THK120 무근콘크리트 / THK27 시멘트몰탈 | THK3 데코타일            | 150 | THK9.5 석고보드   | 수성페인트 2회 | 100 | THK9.5 석고보드                         | 수성페인트 2회              | -   | 경량철골 천정틀(M-BAR)           | THK9.5 석고보드 / 수성페인트 2회    | 4,400 | 03B  |     |
| 락커룸            | THK120 무근콘크리트 / THK27 시멘트몰탈 | THK3 데코타일            | 150 | THK9.5 석고보드   | 수성페인트 2회 | 100 | THK9.5 석고보드                         | 수성페인트 2회              | -   | 경량철골 천정틀(M-BAR)           | 지정텍스                      | 3,000 | 04   |     |
| 화장실(남), 화장실(여) | 액체방수 / 구배몰탈                 | THK5 자기질타일 (300X300) | 150 | -             | -        | -   | 1.08 시멘트 벽돌쌓기 / 액체방수(h=1,200), 보호몰탈 | THK7 도기질벽타일 (300X600) | 30  | 경량철골 천정틀 (AL CLIP-BAR)    | PVC 천정재                   | 3,000 | 05   |     |
| 수유실            | THK120 무근콘크리트 / THK27 시멘트몰탈 | THK3 데코타일            | 150 | THK9.5 석고보드   | 수성페인트 2회 | 100 | THK9.5 석고보드                         | 수성페인트 2회              | -   | 경량철골 천정틀(M-BAR)           | 지정텍스                      | 3,000 | 04   |     |
| 펌프실            | THK100 무근콘크리트               | 에폭시 페인트              | 100 | -             | -        | -   | THK200 콘크리트 웅벽 / THK20 시멘트 몰탈       | 수성페인트 2회              | 20  | THK200 콘크리트 / THK20 시멘트몰탈 | 수성페인트 2회                  | 4,350 | 06   |     |
| 소화수조           | -                           | 에폭시 방수               | 50  | -             | -        | -   | -                                   | 에폭시 방수                | -   | -                         | 에폭시 방수                    | -     | 07   |     |
|                |                             |                      |     |               |          |     |                                     |                       |     |                           |                           |       |      |     |
PROJECT TITLE

리틀 포레스트  
봉뜨락 조성사업

PROJECT NO

NOTE

KEY PLAN

DESIGN CORP.



ADD. 대구광역시 동구 장동로 81, 5F  
TEL. 053.716.0776 FAX. 0505.720.0776  
E-mail. e-ul2020@naver.com  
Web. eul2020 / 0776

APPROVED BY  
대표이사/건축사 권오섭

CHECKED BY

DRAWN BY


DATE  
2023. 04.

DRAWING TITLE

실내재료 마감표

SCALE  
A3 : 1/ NONE

DRAWING NO.  
A02- 021

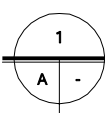

# 실내재료마감 상세도-1

축척 : 1/NONE(A1) , 1/NONE(A3)

PROJECT TITLE

리틀 포레스트  
봉뜨락 조성사업

PROJECT NO

NOTE

KEY PLAN

DESIGN CORP.

**이음** (주)이음건축사사무소

ADD. 대구광역시 중구 장동로 81, 5F  
TEL. 053.716.0776 FAX. 0505.720.0776  
E-mail. e-ul2020@naver.com  
Web. eul2020 / 0776

APPROVED BY  
대표이사 / 건축사 권오섭

CHECKED BY

DRAWN BY

DATE  
2023. 04.


DRAWING TITLE  
실내재료마감 상세도-1

SCALE  
A3 : 1/ 10

DRAWING NO.  
A02-022


구 분 01 방풍실

상세도

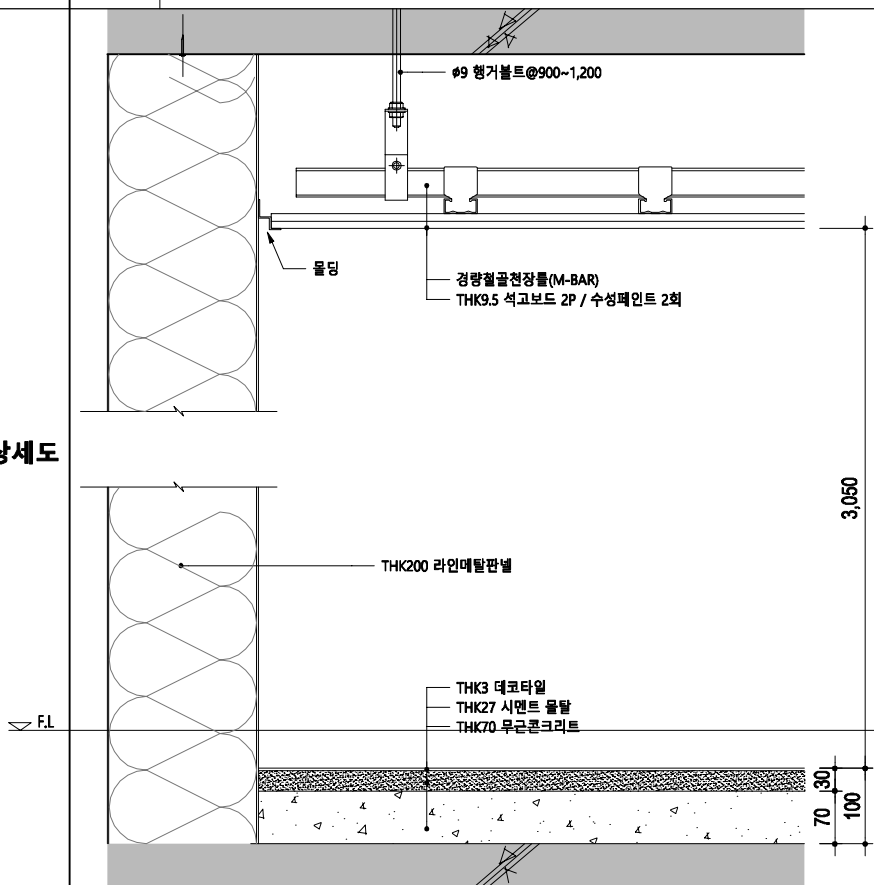


02A HALL

상세도

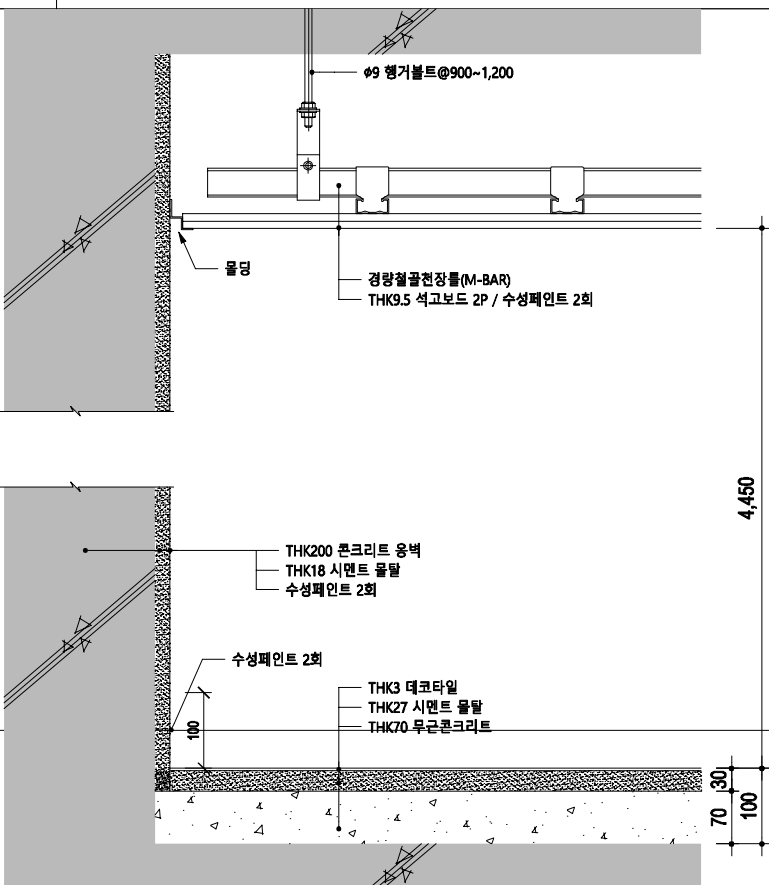


02B HALL

상세도

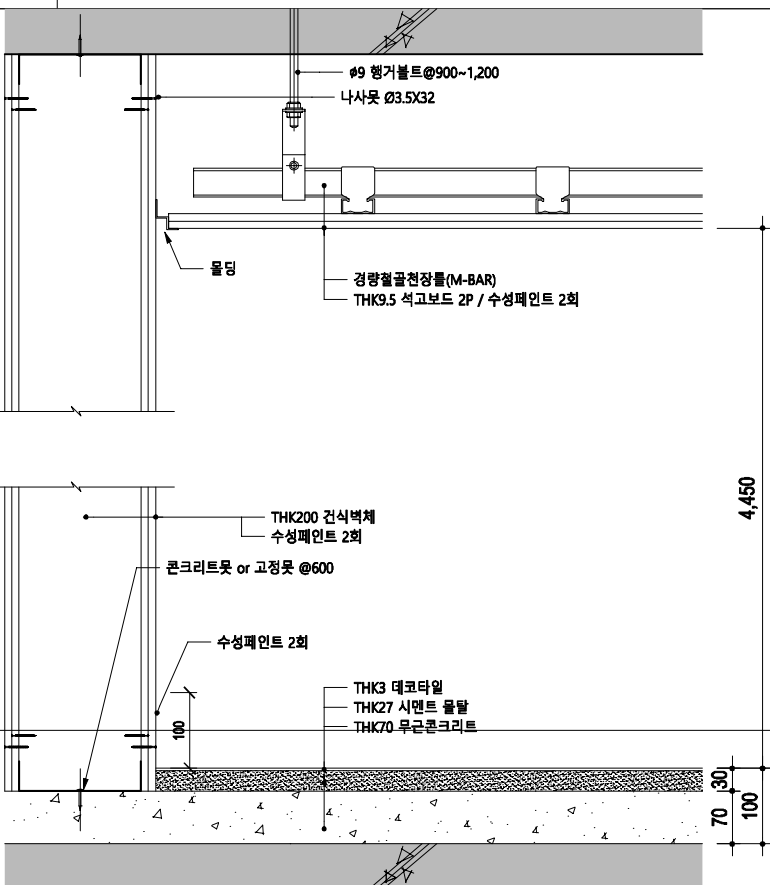


구 분 03A 어린이 놀이시설장

상세도

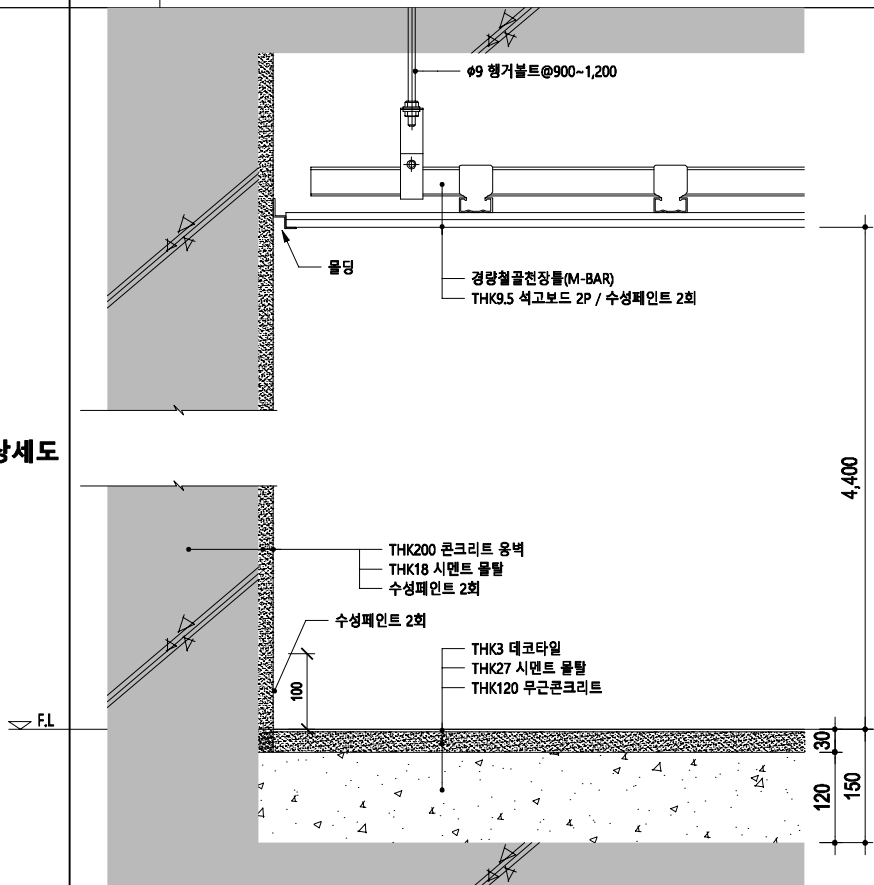


03B 어린이 놀이시설장, 카운터


상세도

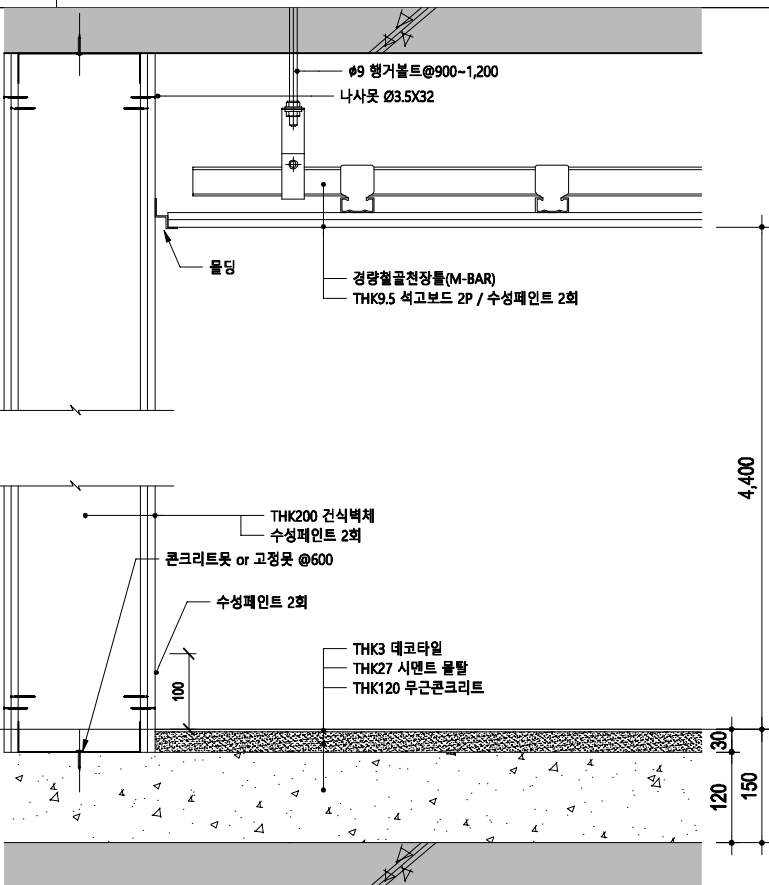




04 락카룸, 수유실

상세도

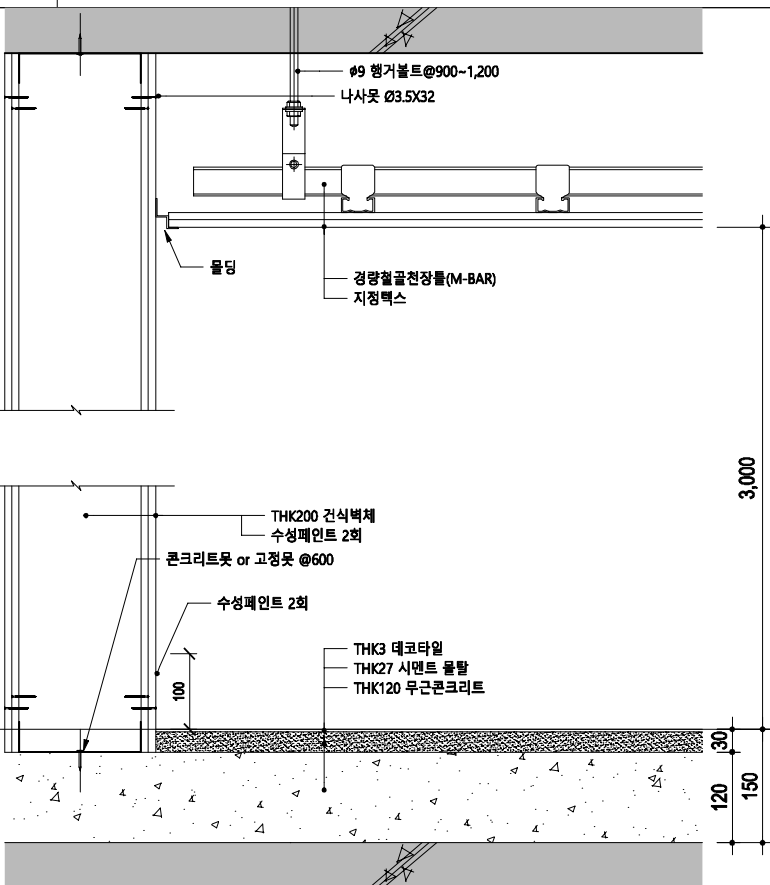

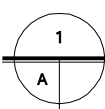

실내재료마감 상세도-2
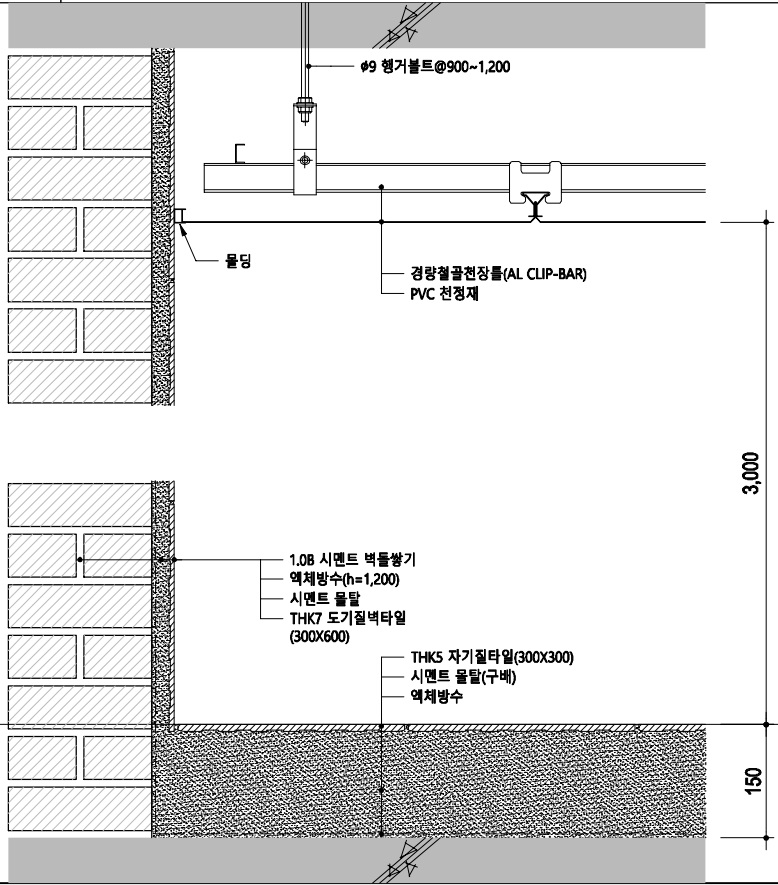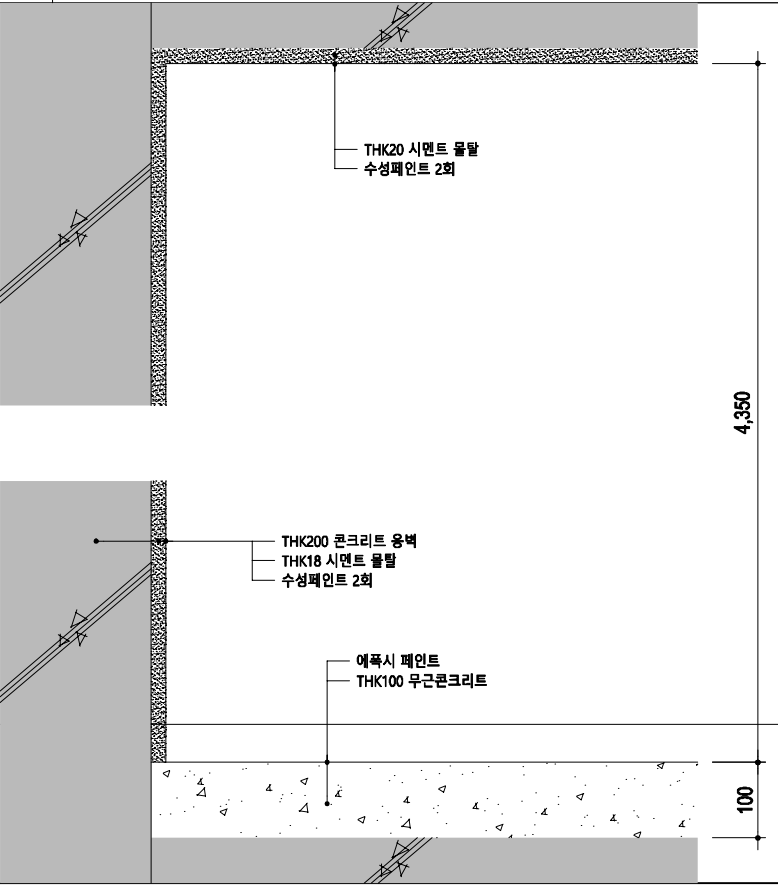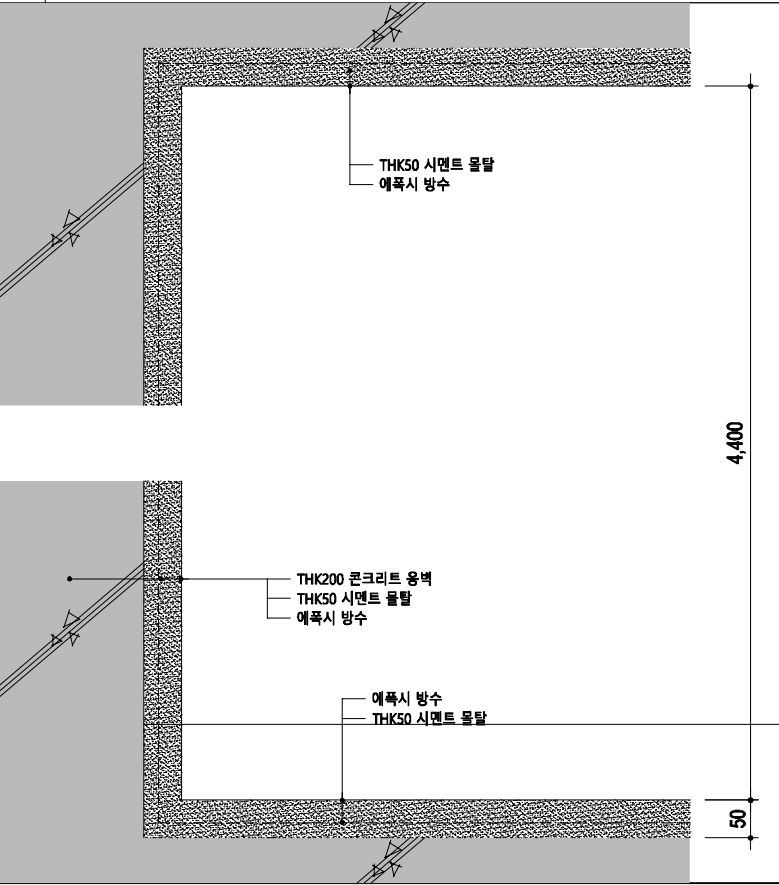
| 구 분 |       | 05 화장실 (남), 화장실 (여)                                                                 | 06 펌프실                                                                               | 07 소화수조                                                                              |
|-----|-------|-------------------------------------------------------------------------------------|--------------------------------------------------------------------------------------|--------------------------------------------------------------------------------------|
| 상세도 |       |  |  |  |
|     | ▽ F.L |                                                                                     |                                                                                      |                                                                                      |
| 구 분 |       |                                                                                     |                                                                                      |                                                                                      |
| 상세도 |       |                                                                                     |                                                                                      |                                                                                      |
|     | ▽ F.L |                                                                                     |                                                                                      |                                                                                      |

PROJECT TITLE

리틀 포레스트  
봉뜨락 조성사업

PROJECT NO

NOTE

KEY PLAN

DESIGN CORP.



ADD. 대구광역시 중구 장동로 81, 5F  
TEL. 053.716.0776 FAX. 0505.720.0776  
E-mail. e-ul2020@naver.com  
Web. eul2020 / 0776

APPROVED BY  
대표이사/건축사 권오섭

CHECKED BY

DRAWN BY

DATE  
2023. 04.

DRAWING TITLE

실내재료마감 상세도-2

SCALE  
A3 : 1/ 10

DRAWING NO.  
A02- 023

PROJECT TITLE

리틀 포레스트  
봉뜨락 조성사업

PROJECT NO

NOTE

KEY PLAN

DESIGN CORP.

**이엘** (주)이엘건축사사무소

ADD. 대구광역시 중구 장동로 81, 5F  
TEL. 053.716.0776 FAX. 0505.720.0776  
E-mail. e-ul2020@naver.com  
Web. eul2020 / 0776

APPROVED BY  
대표이사/건축사 권오섭

CHECKED BY

DRAWN BY

DATE

2023. 04.

DRAWING TITLE



1층 평면도  
(변경후)

SCALE

A3 : 1/ 150


DRAWING NO.

A02- 101B

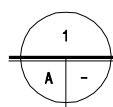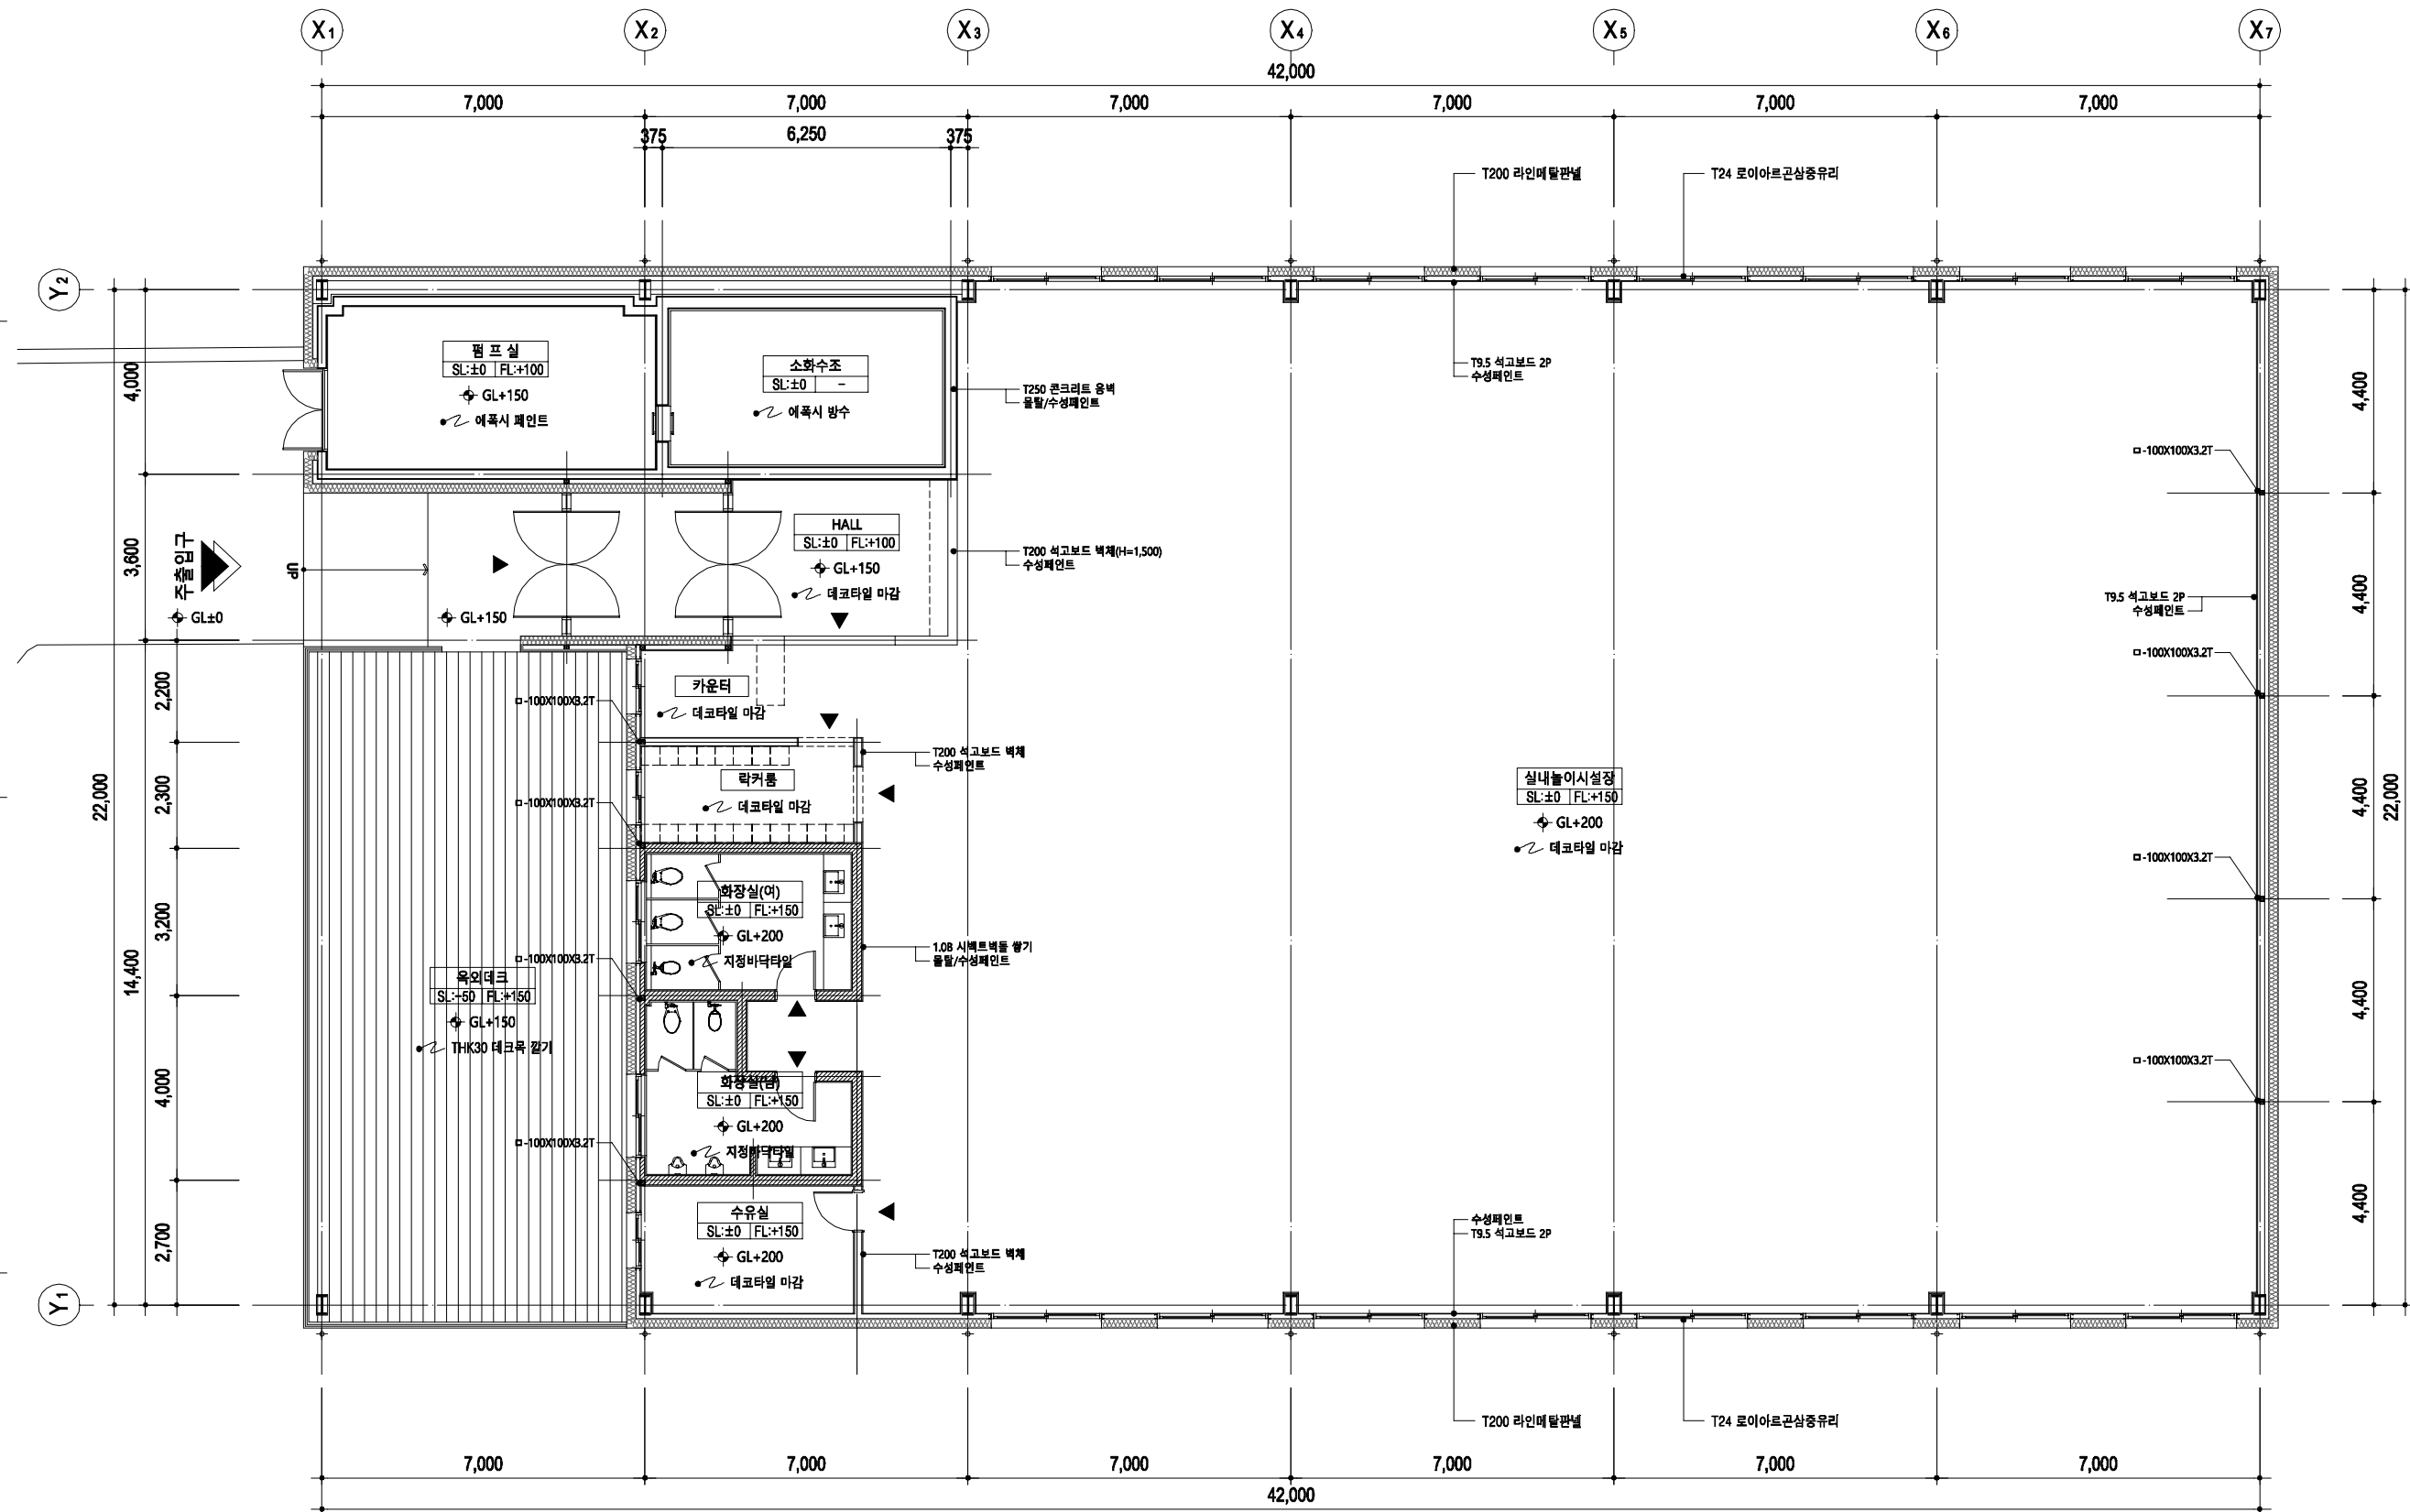


1층 평면도(변경후)


축척 A1:1/75, A3:1/150

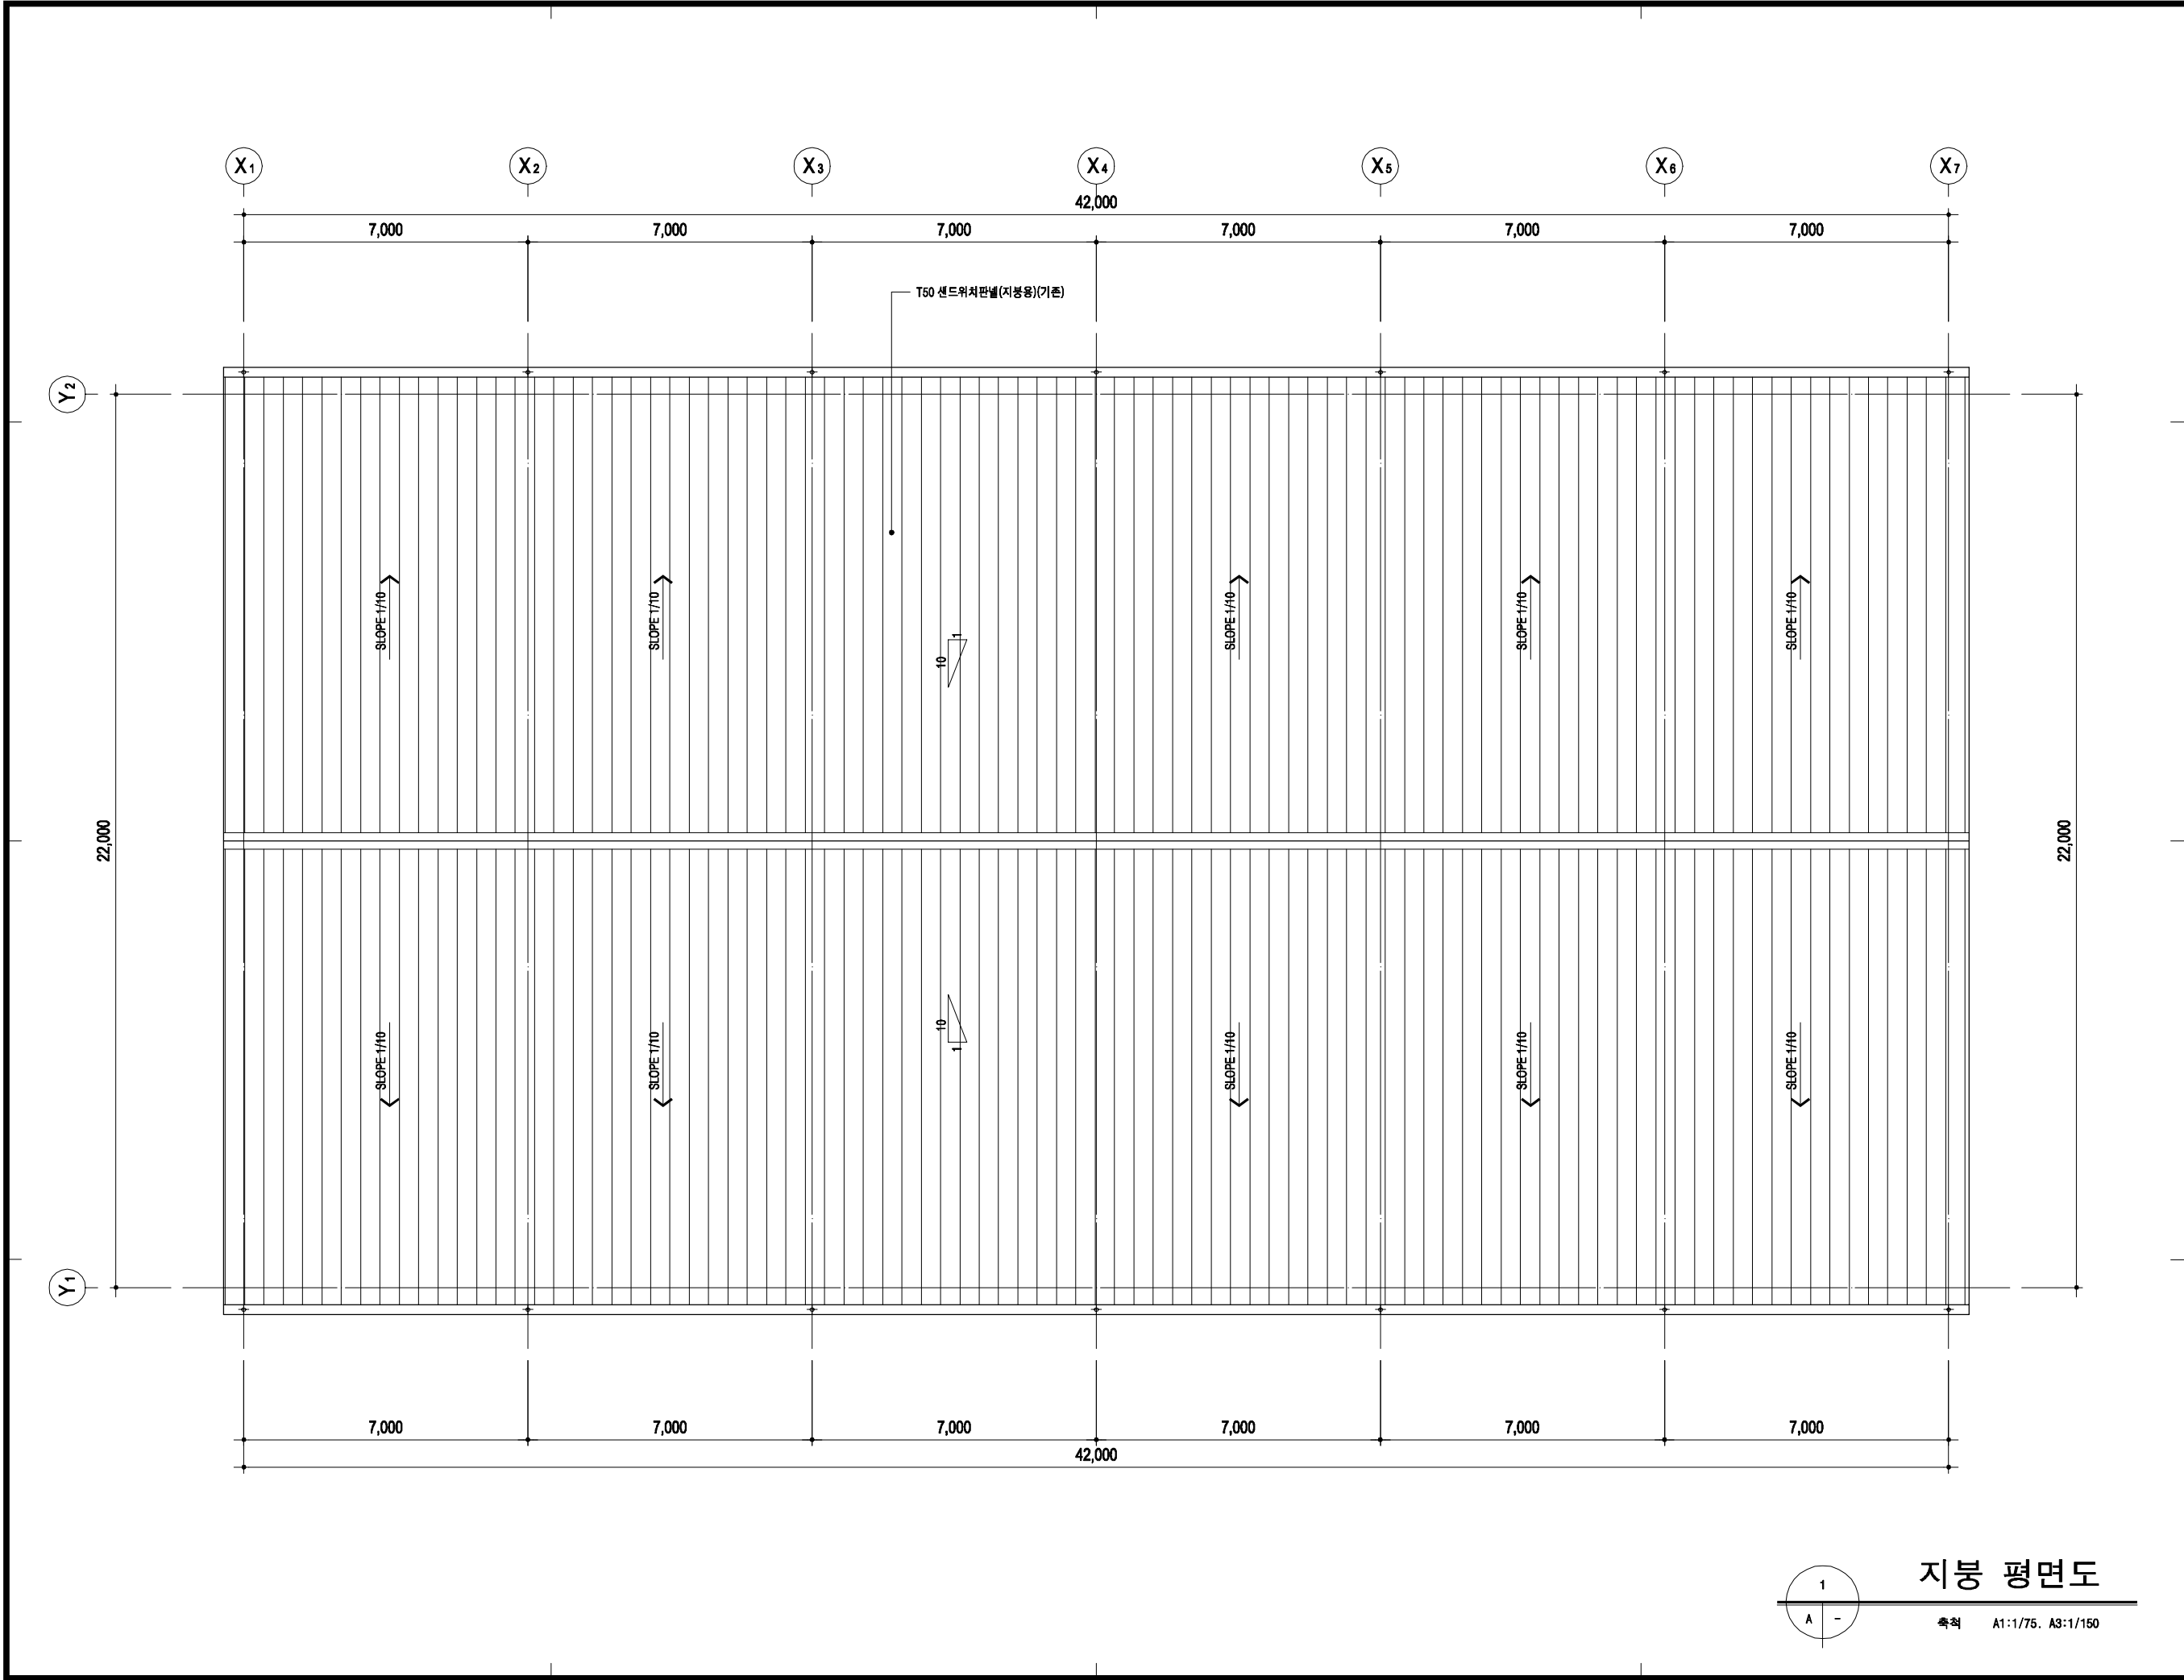

|               |   |
|---------------|---|
| PROJECT TITLE | 리틀 포레스트<br>봉뜨락 조성사업   |
| PROJECT NO    |   |
| NOTE          |   |
| KEY PLAN      |   |
| DESIGN CORP.  | <b>이음</b> (주)이음건축사사무소<br>ADD. 대구광역시 중구 장동로 81, 5F<br>TEL. 053.716.0776 FAX. 0505.720.0776<br>E-mail. e-ul2020@naver.com<br>Web. eul2020 / 0776 |
| APPROVED BY   | 대표이사 / 건축사 권오섭   |
| CHECKED BY    |   |
| DRAWN BY      |   |
| DATE          | 2023. 04.   |
| DRAWING TITLE | 지붕 평면도   |
| SCALE         | A3 : 1/ 150   |
| DRAWING NO.   | A02- 102   |

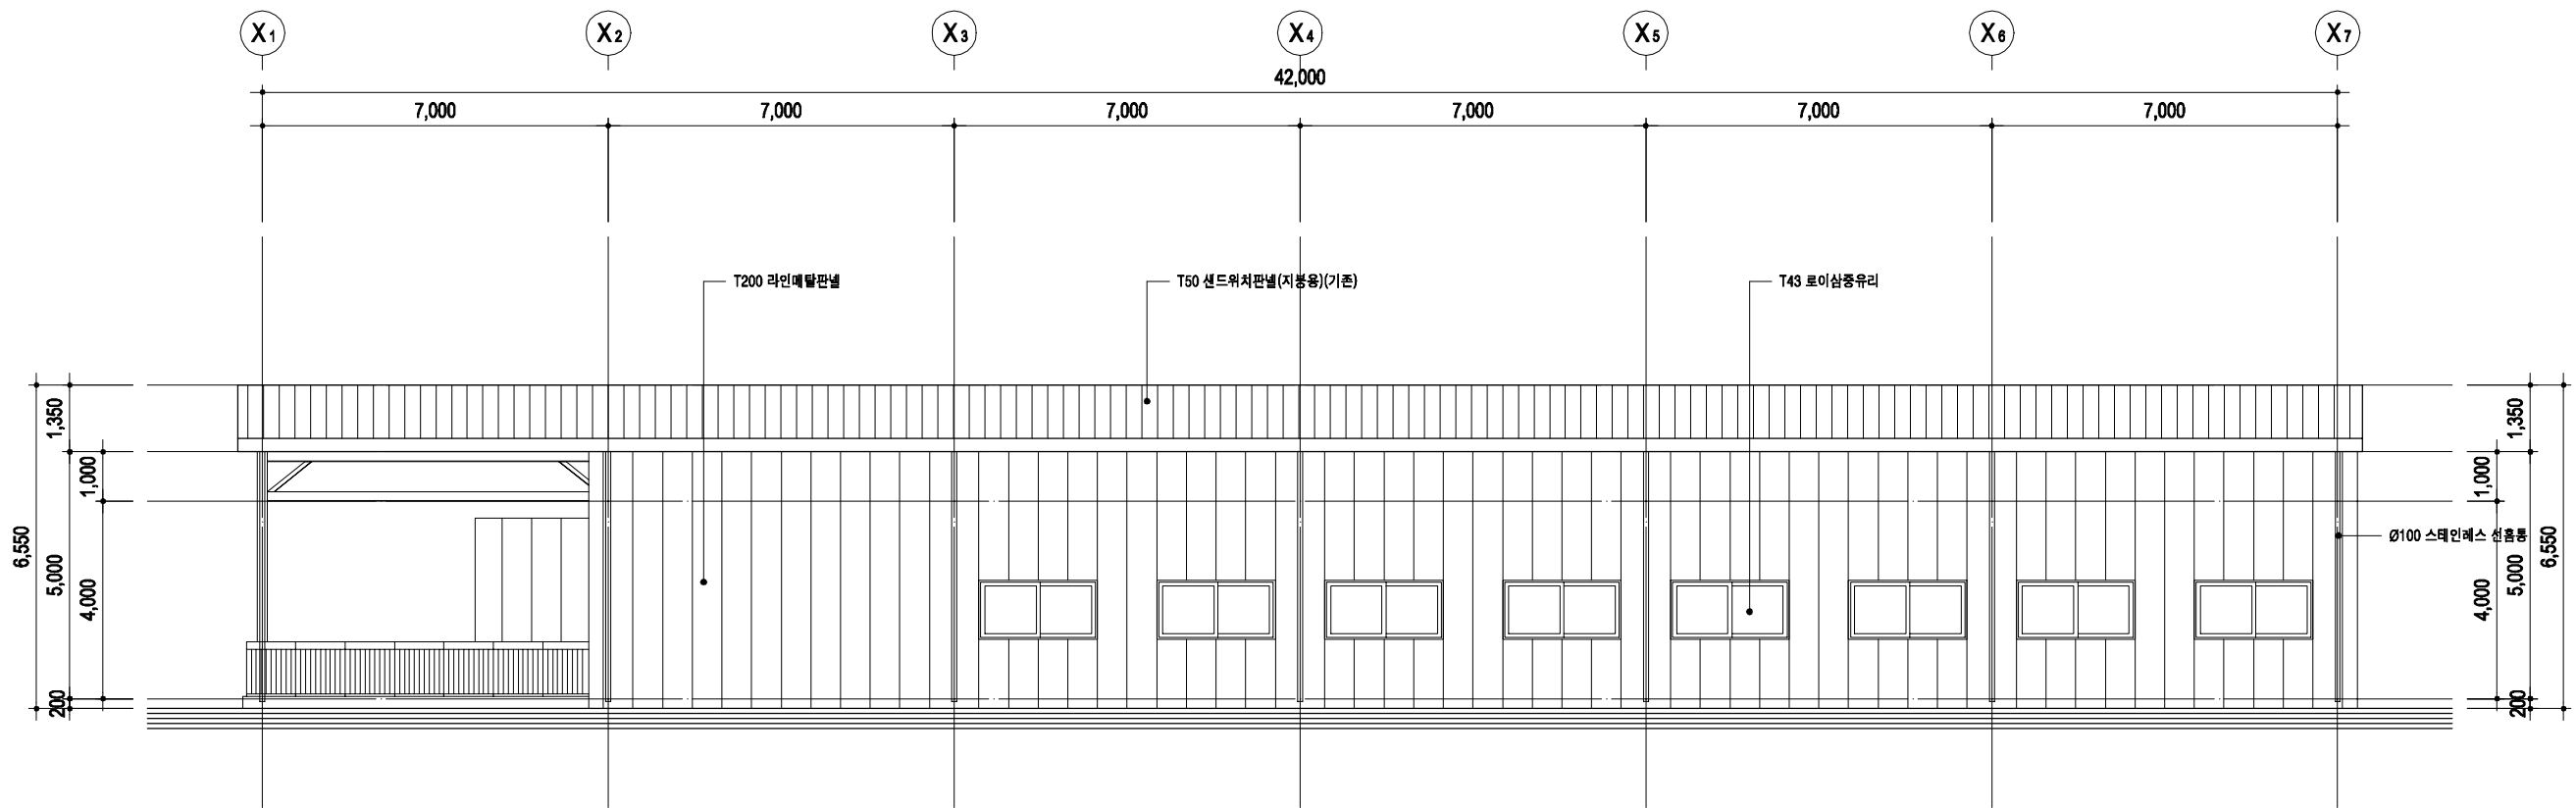

정면도  
축척 A1:1/75, A3:1/150

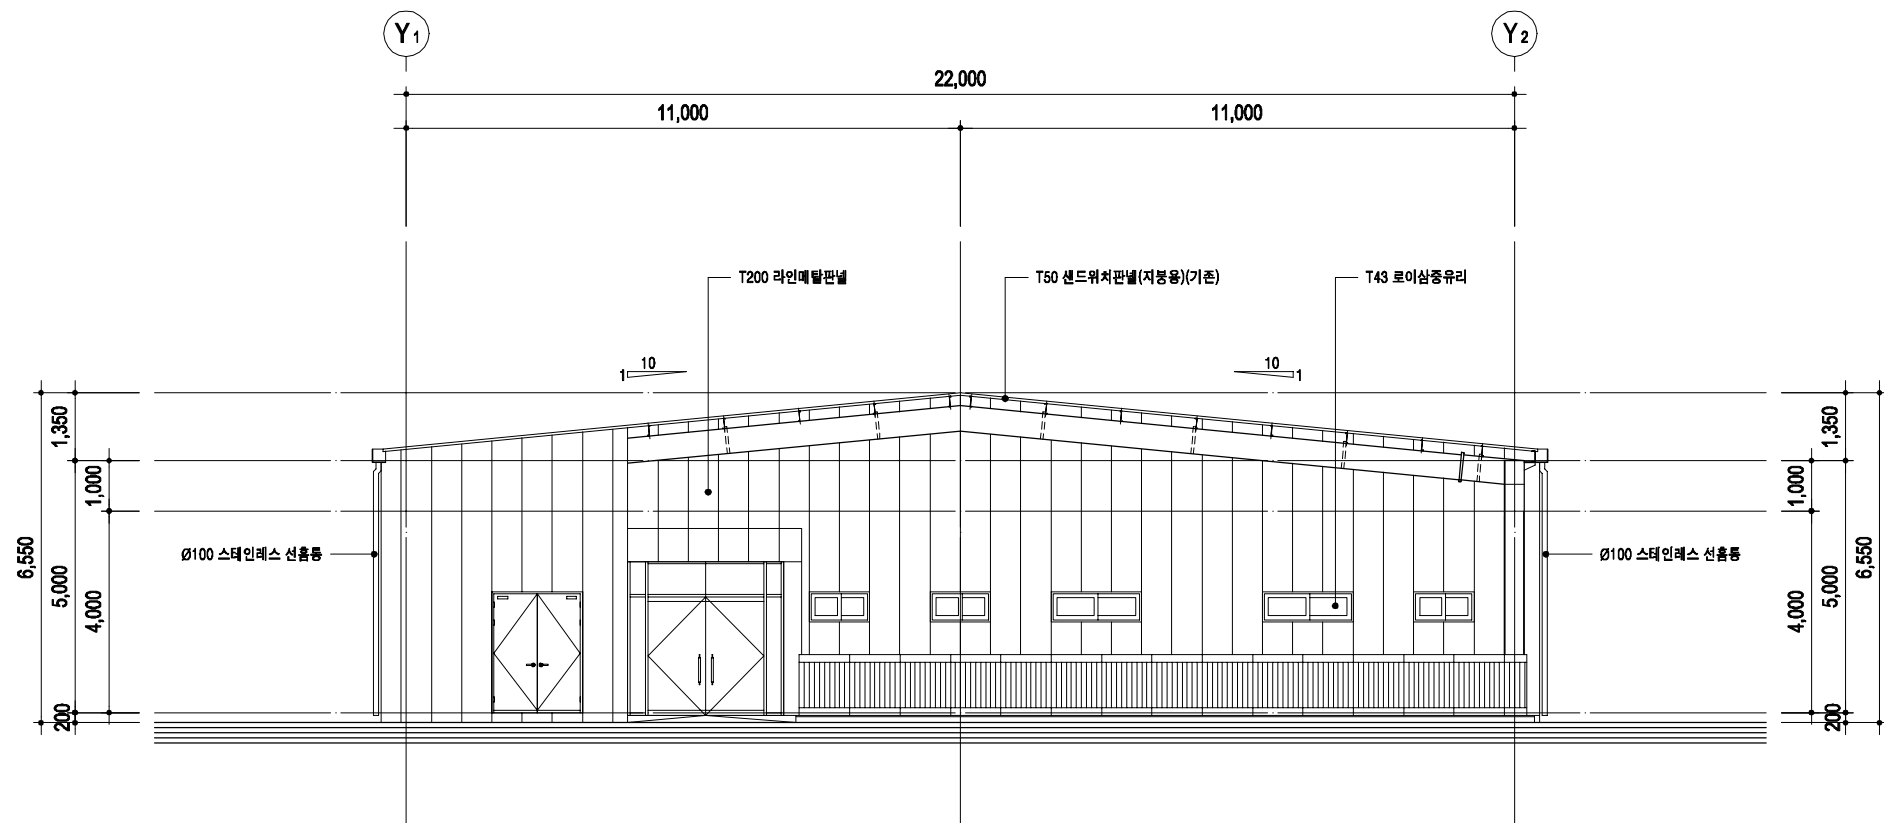

우측면도  
축척 A1:1/75, A3:1/150


PROJECT TITLE

리틀 포레스트  
봉뜨락 조성사업

PROJECT NO

NOTE

KEY PLAN

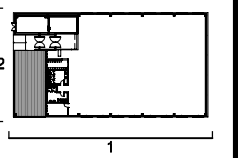

DESIGN CORP.

이음 (주)이음건축사사무소

ADD. 대구광역시 중구 장동로 81, 5F  
TEL. 053.716.0776 FAX. 0505.720.0776  
E-mail. e-ul2020@naver.com  
Web. eul2020 / 0776

APPROVED BY

대표이사/건축사 권오섭

CHECKED BY

DRAWN BY

DATE

2023. 04.

DRAWING TITLE


입면도-1

SCALE


A3 : 1/ 150

DRAWING NO.

A02- 201

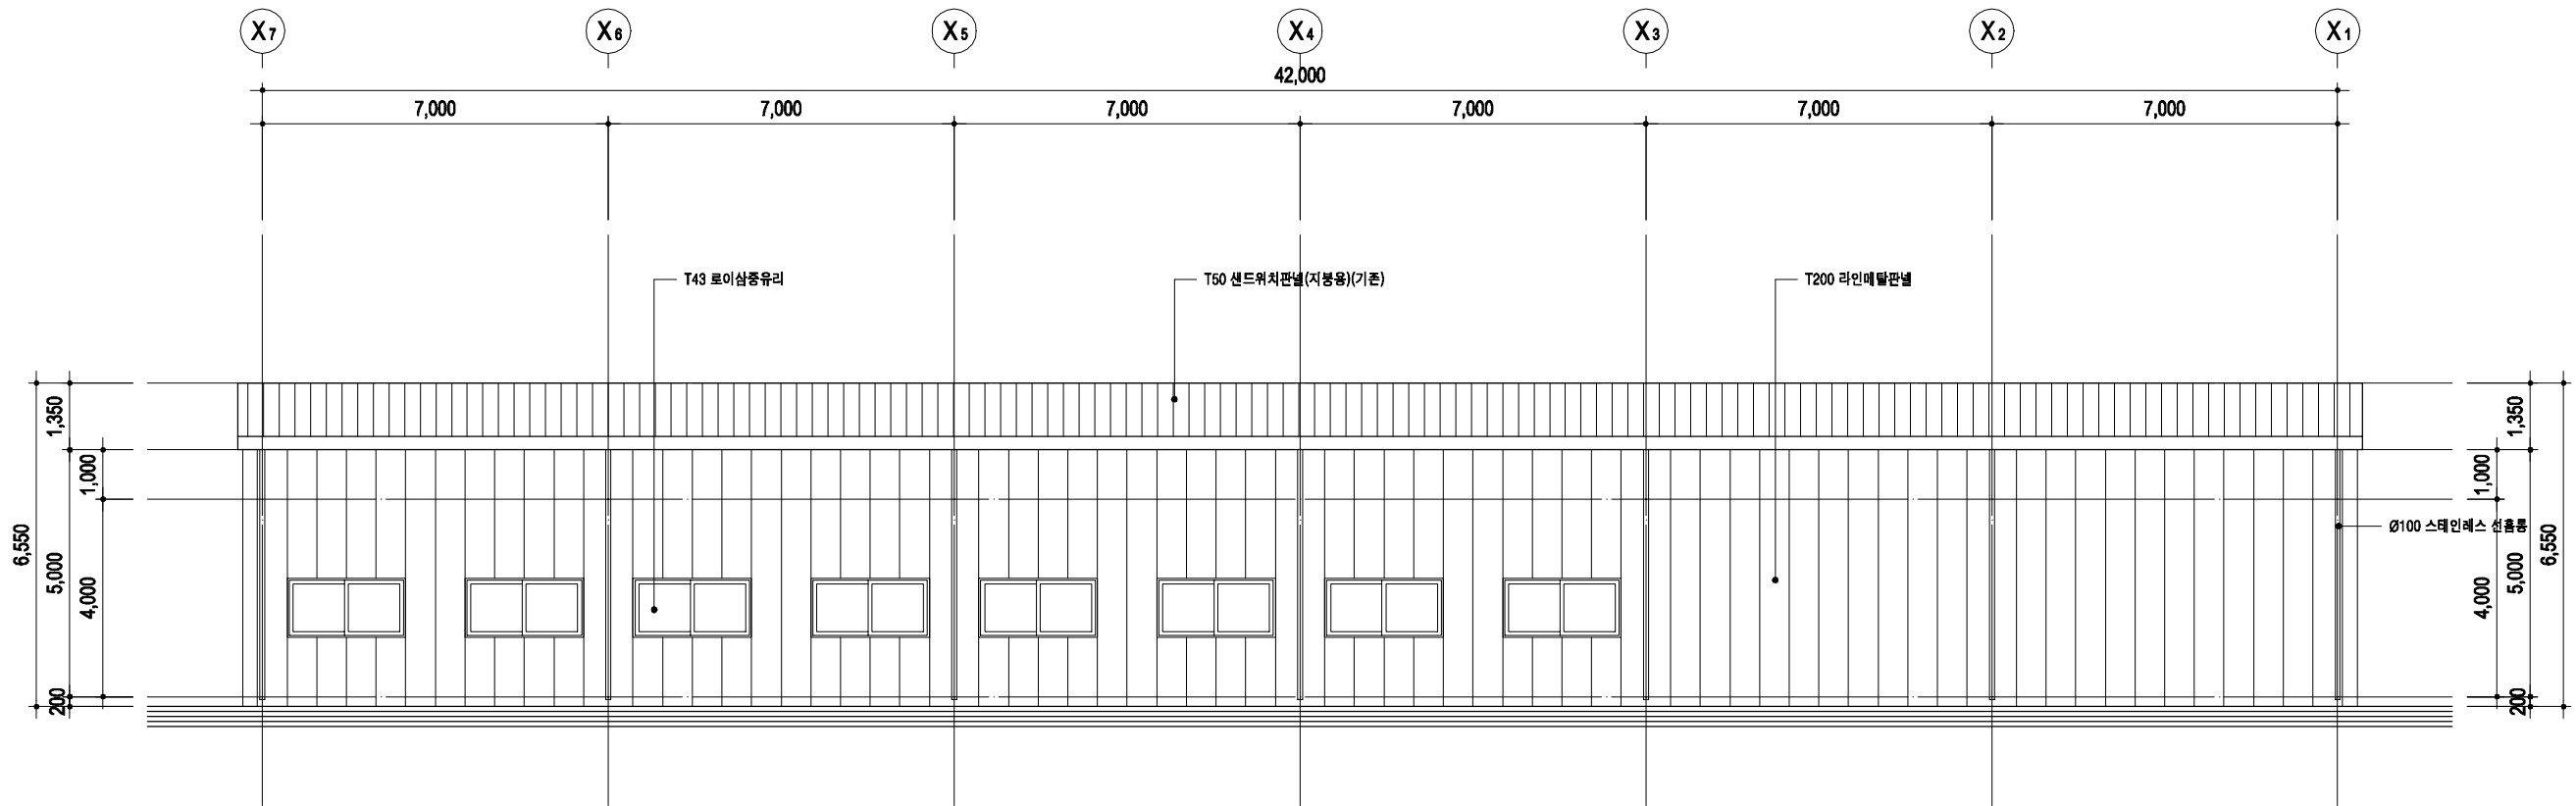

배면도  
축척 A1:1/75, A3:1/150

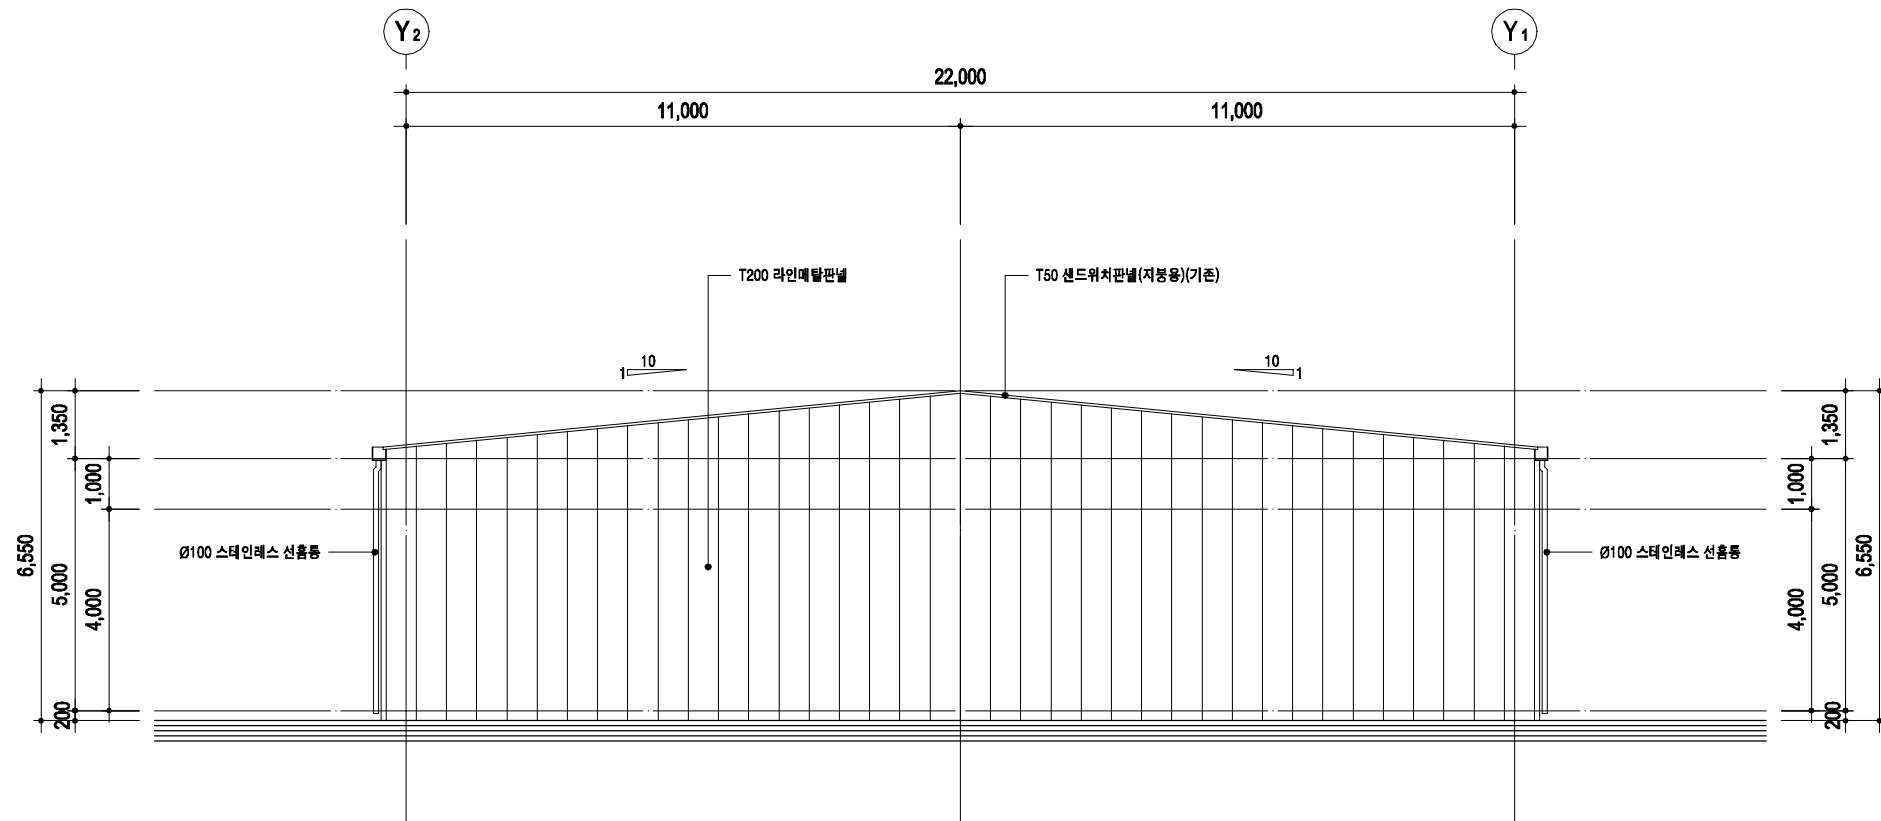

좌측면도  
축척 A1:1/75, A3:1/150

PROJECT TITLE  
리틀 포레스트  
봉뜨락 조성사업

PROJECT NO

NOTE

KEY PLAN

DESIGN CORP.  
이을건축사사무소

ADD. 대구광역시 중구 장동로 81, 5F  
TEL. 053.716.0776 FAX. 0505.720.0776  
E-mail. e-ul2020@naver.com  
Web. eul2020 / 0776

APPROVED BY  
대표이사/건축사 권오섭

CHECKED BY

DRAWN BY

DATE  
2023. 04.

DRAWING TITLE  
입면도-2

SCALE  
A3 : 1/ 150

DRAWING NO.  
A02- 202


PROJECT TITLE

리틀 포레스트  
봉뜨락 조성사업

PROJECT NO

NOTE

KEY PLAN

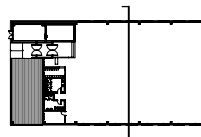

DESIGN CORP.

**이음** (주)이음건축사사무소

ADD. 대구광역시 중구 장동로 81, 5F  
TEL. 053.716.0776 FAX. 0505.720.0776  
E-mail. e-ul2020@naver.com  
Web. eul2020 / 0776

APPROVED BY  
대표이사/건축사 권오섭

CHECKED BY

DRAWN BY


DATE  
2023. 04.

DRAWING TITLE

주단면도-1

SCALE  
A3 : 1/ 100

DRAWING NO.  
A02- 301

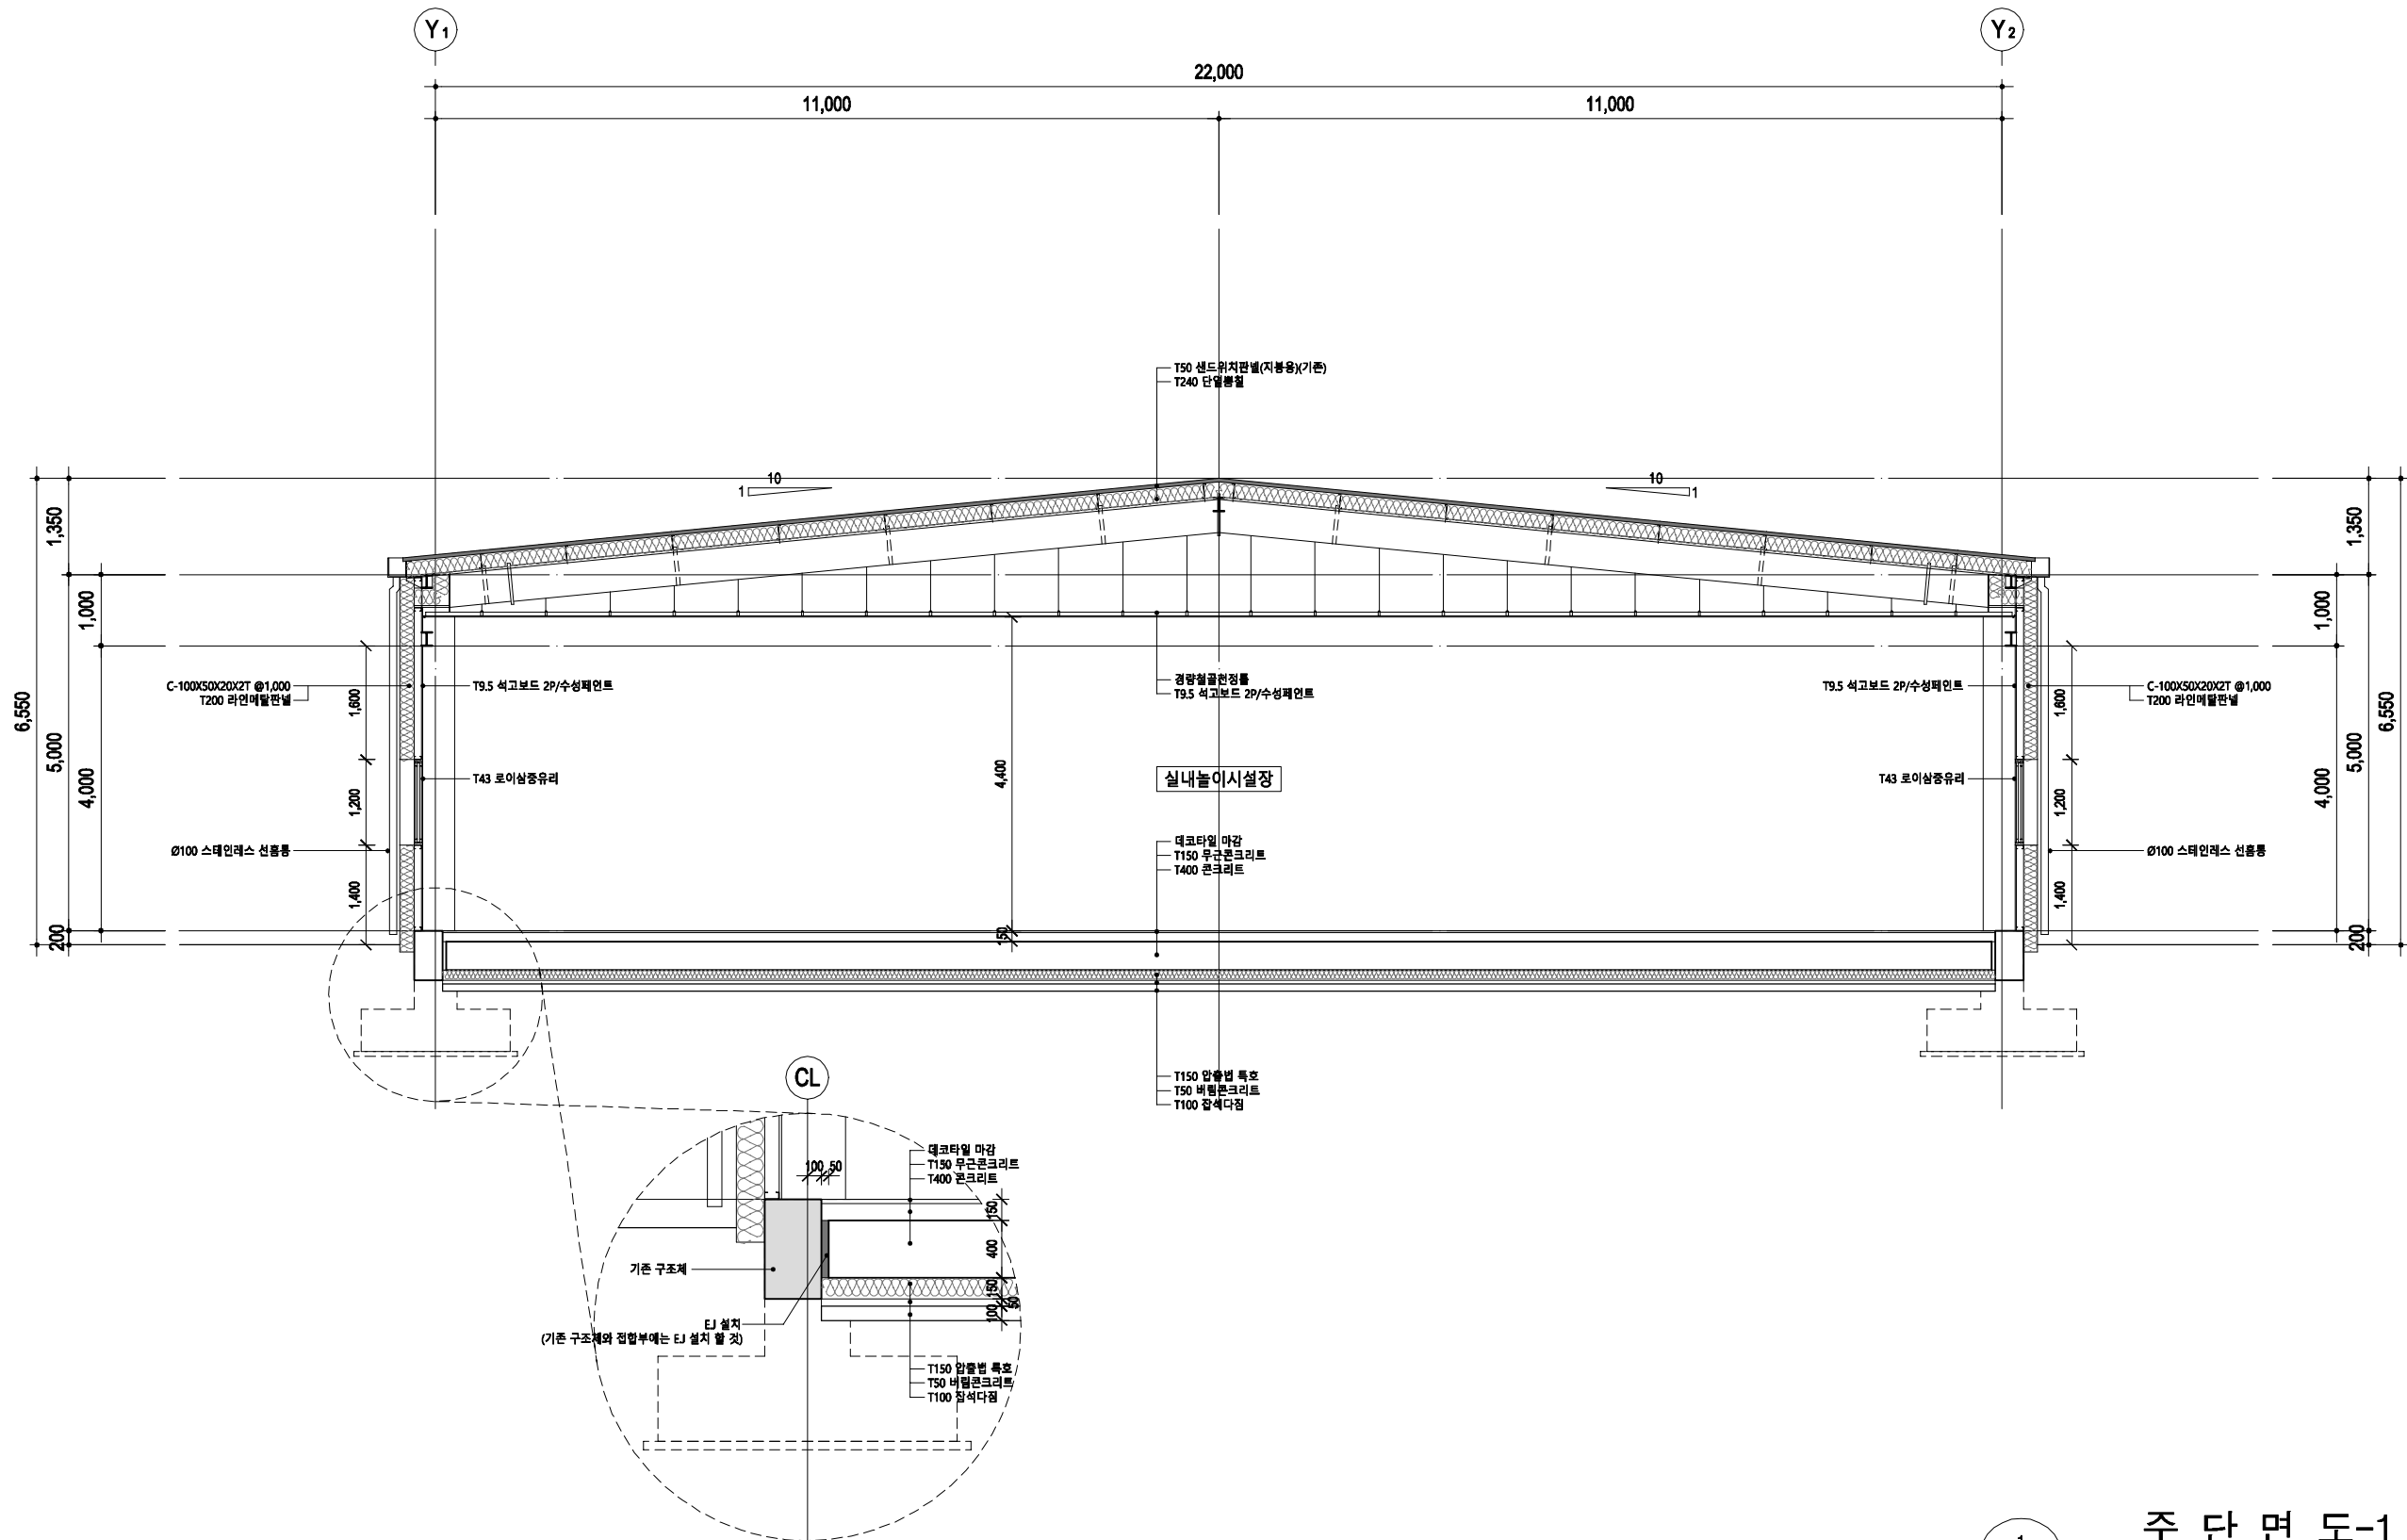


주 단 면 도-1

축척 A1:1/50, A3:1/100

리틀 포레스트  
봄뜨락 조성사업

## NOTE

DRAWING NO. **A02-302**

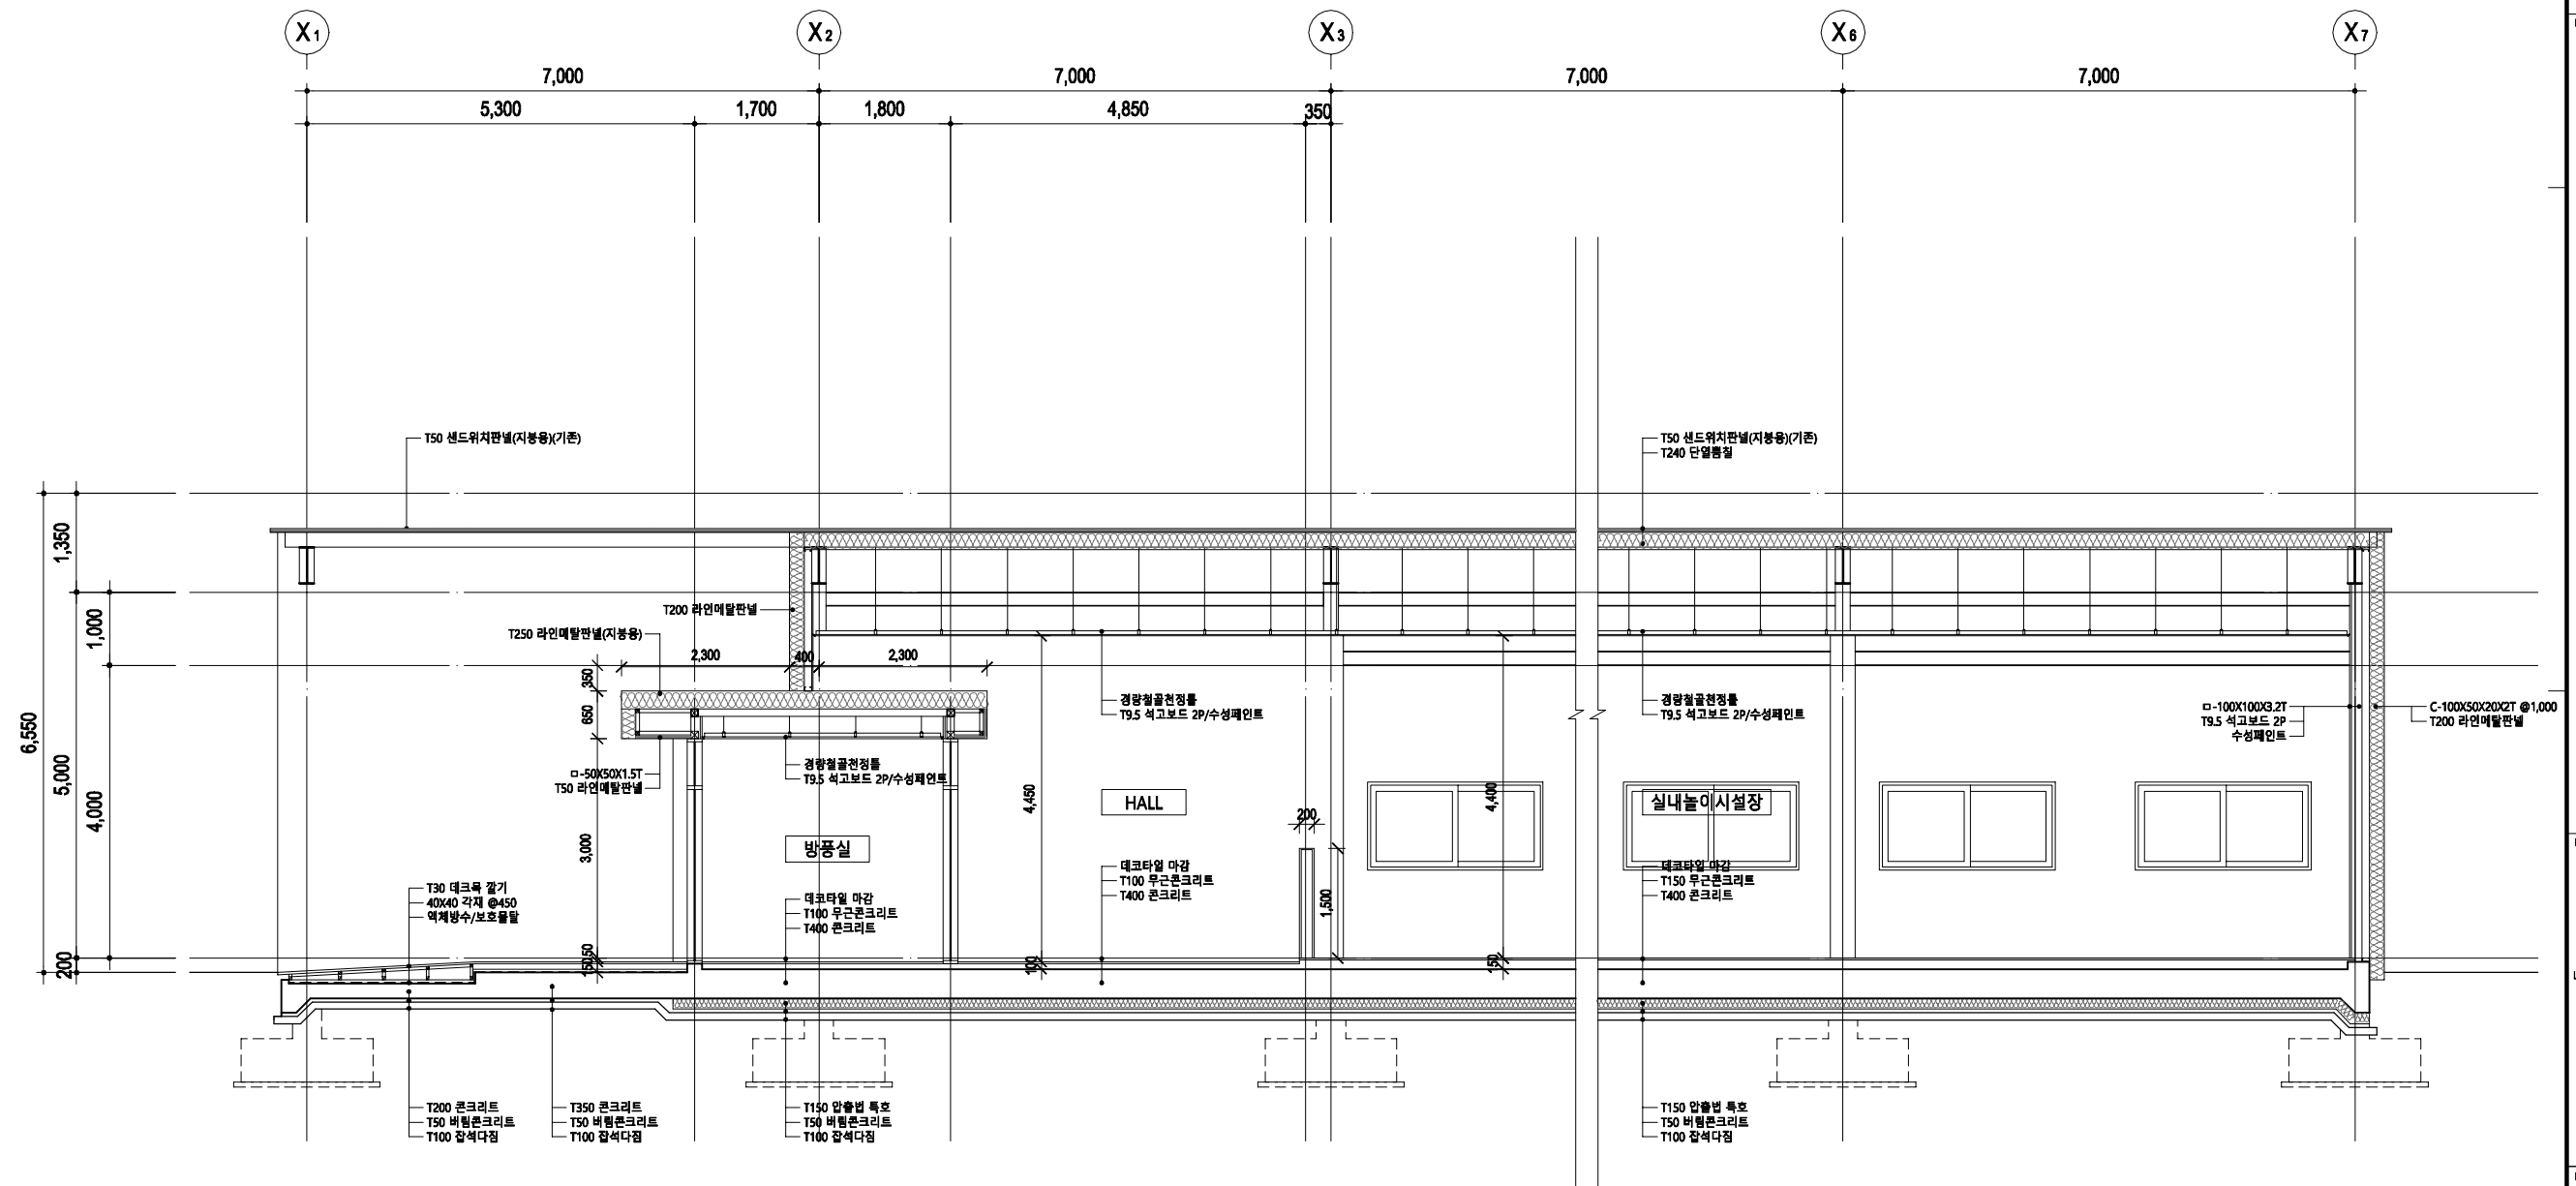

주 단 면 도-2

축척 A1:1/50. A3:1/100


PROJECT TITLE

리틀 포레스트  
봉뜨락 조성사업

PROJECT NO

NOTE

KEY PLAN

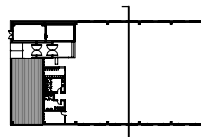

DESIGN CORP.

**이음** (주)이음건축사사무소

ADD. 대구광역시 중구 장동로 81, 5F  
TEL. 053.716.0776 FAX. 0505.720.0776  
E-mail. e-ul2020@naver.com  
Web. eul2020 / 0776

APPROVED BY

대표이사/건축사 권오섭

CHECKED BY

DRAWN BY

DATE

2023. 04.

DRAWING TITLE



주단면도-3

SCALE

A3 : 1/ 100

DRAWING NO.

A02- 303

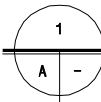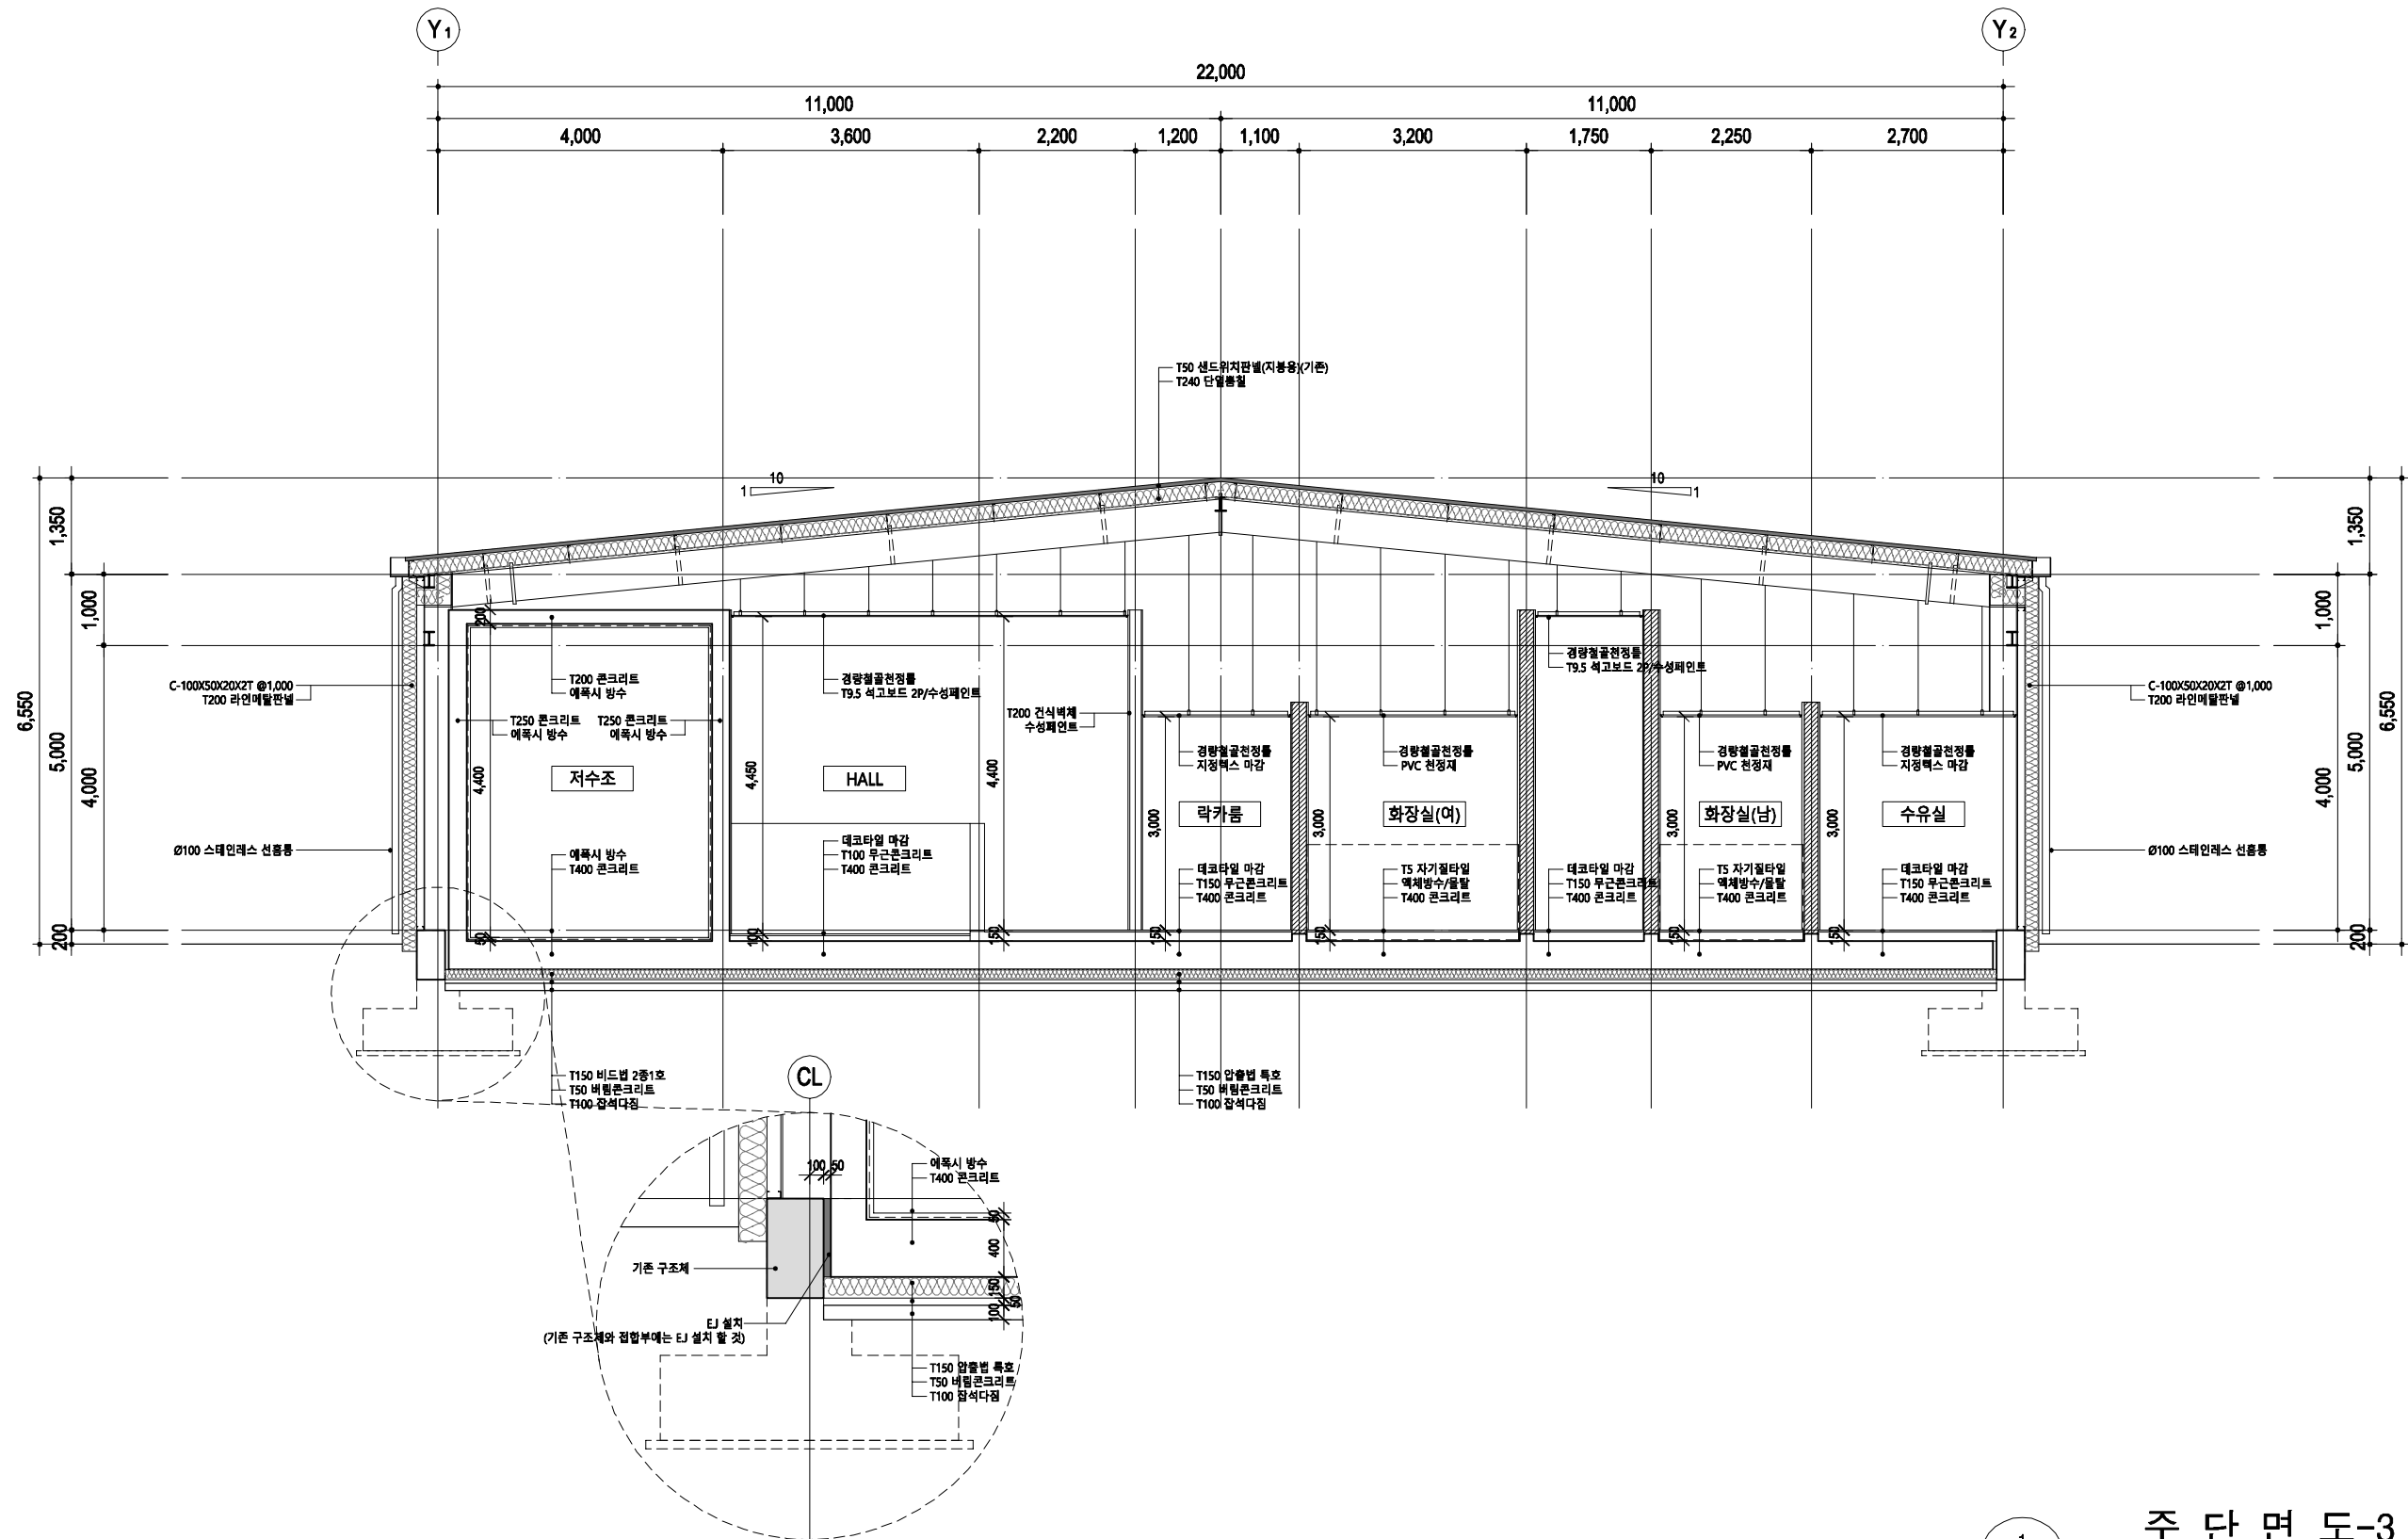

주 단 면 도-3

축척 A1:1/50, A3:1/100


PROJECT TITLE

리틀 포레스트  
봉뜨락 조성사업

PROJECT NO

NOTE

KEY PLAN

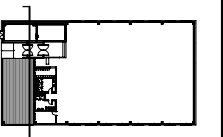

DESIGN CORP.

**이음** (주)이음건축사사무소

ADD. 대구광역시 중구 장동로 81, 5F  
TEL. 053.716.0776 FAX. 0505.720.0776  
E-mail. e-ul2020@naver.com  
Web. eul2020 / 0776

APPROVED BY

대표이사 / 건축사 권오섭

CHECKED BY

DRAWN BY

DATE

2023. 04.

DRAWING TITLE


주단면도-4

SCALE

A3 : 1/ 100

DRAWING NO.

A02- 304

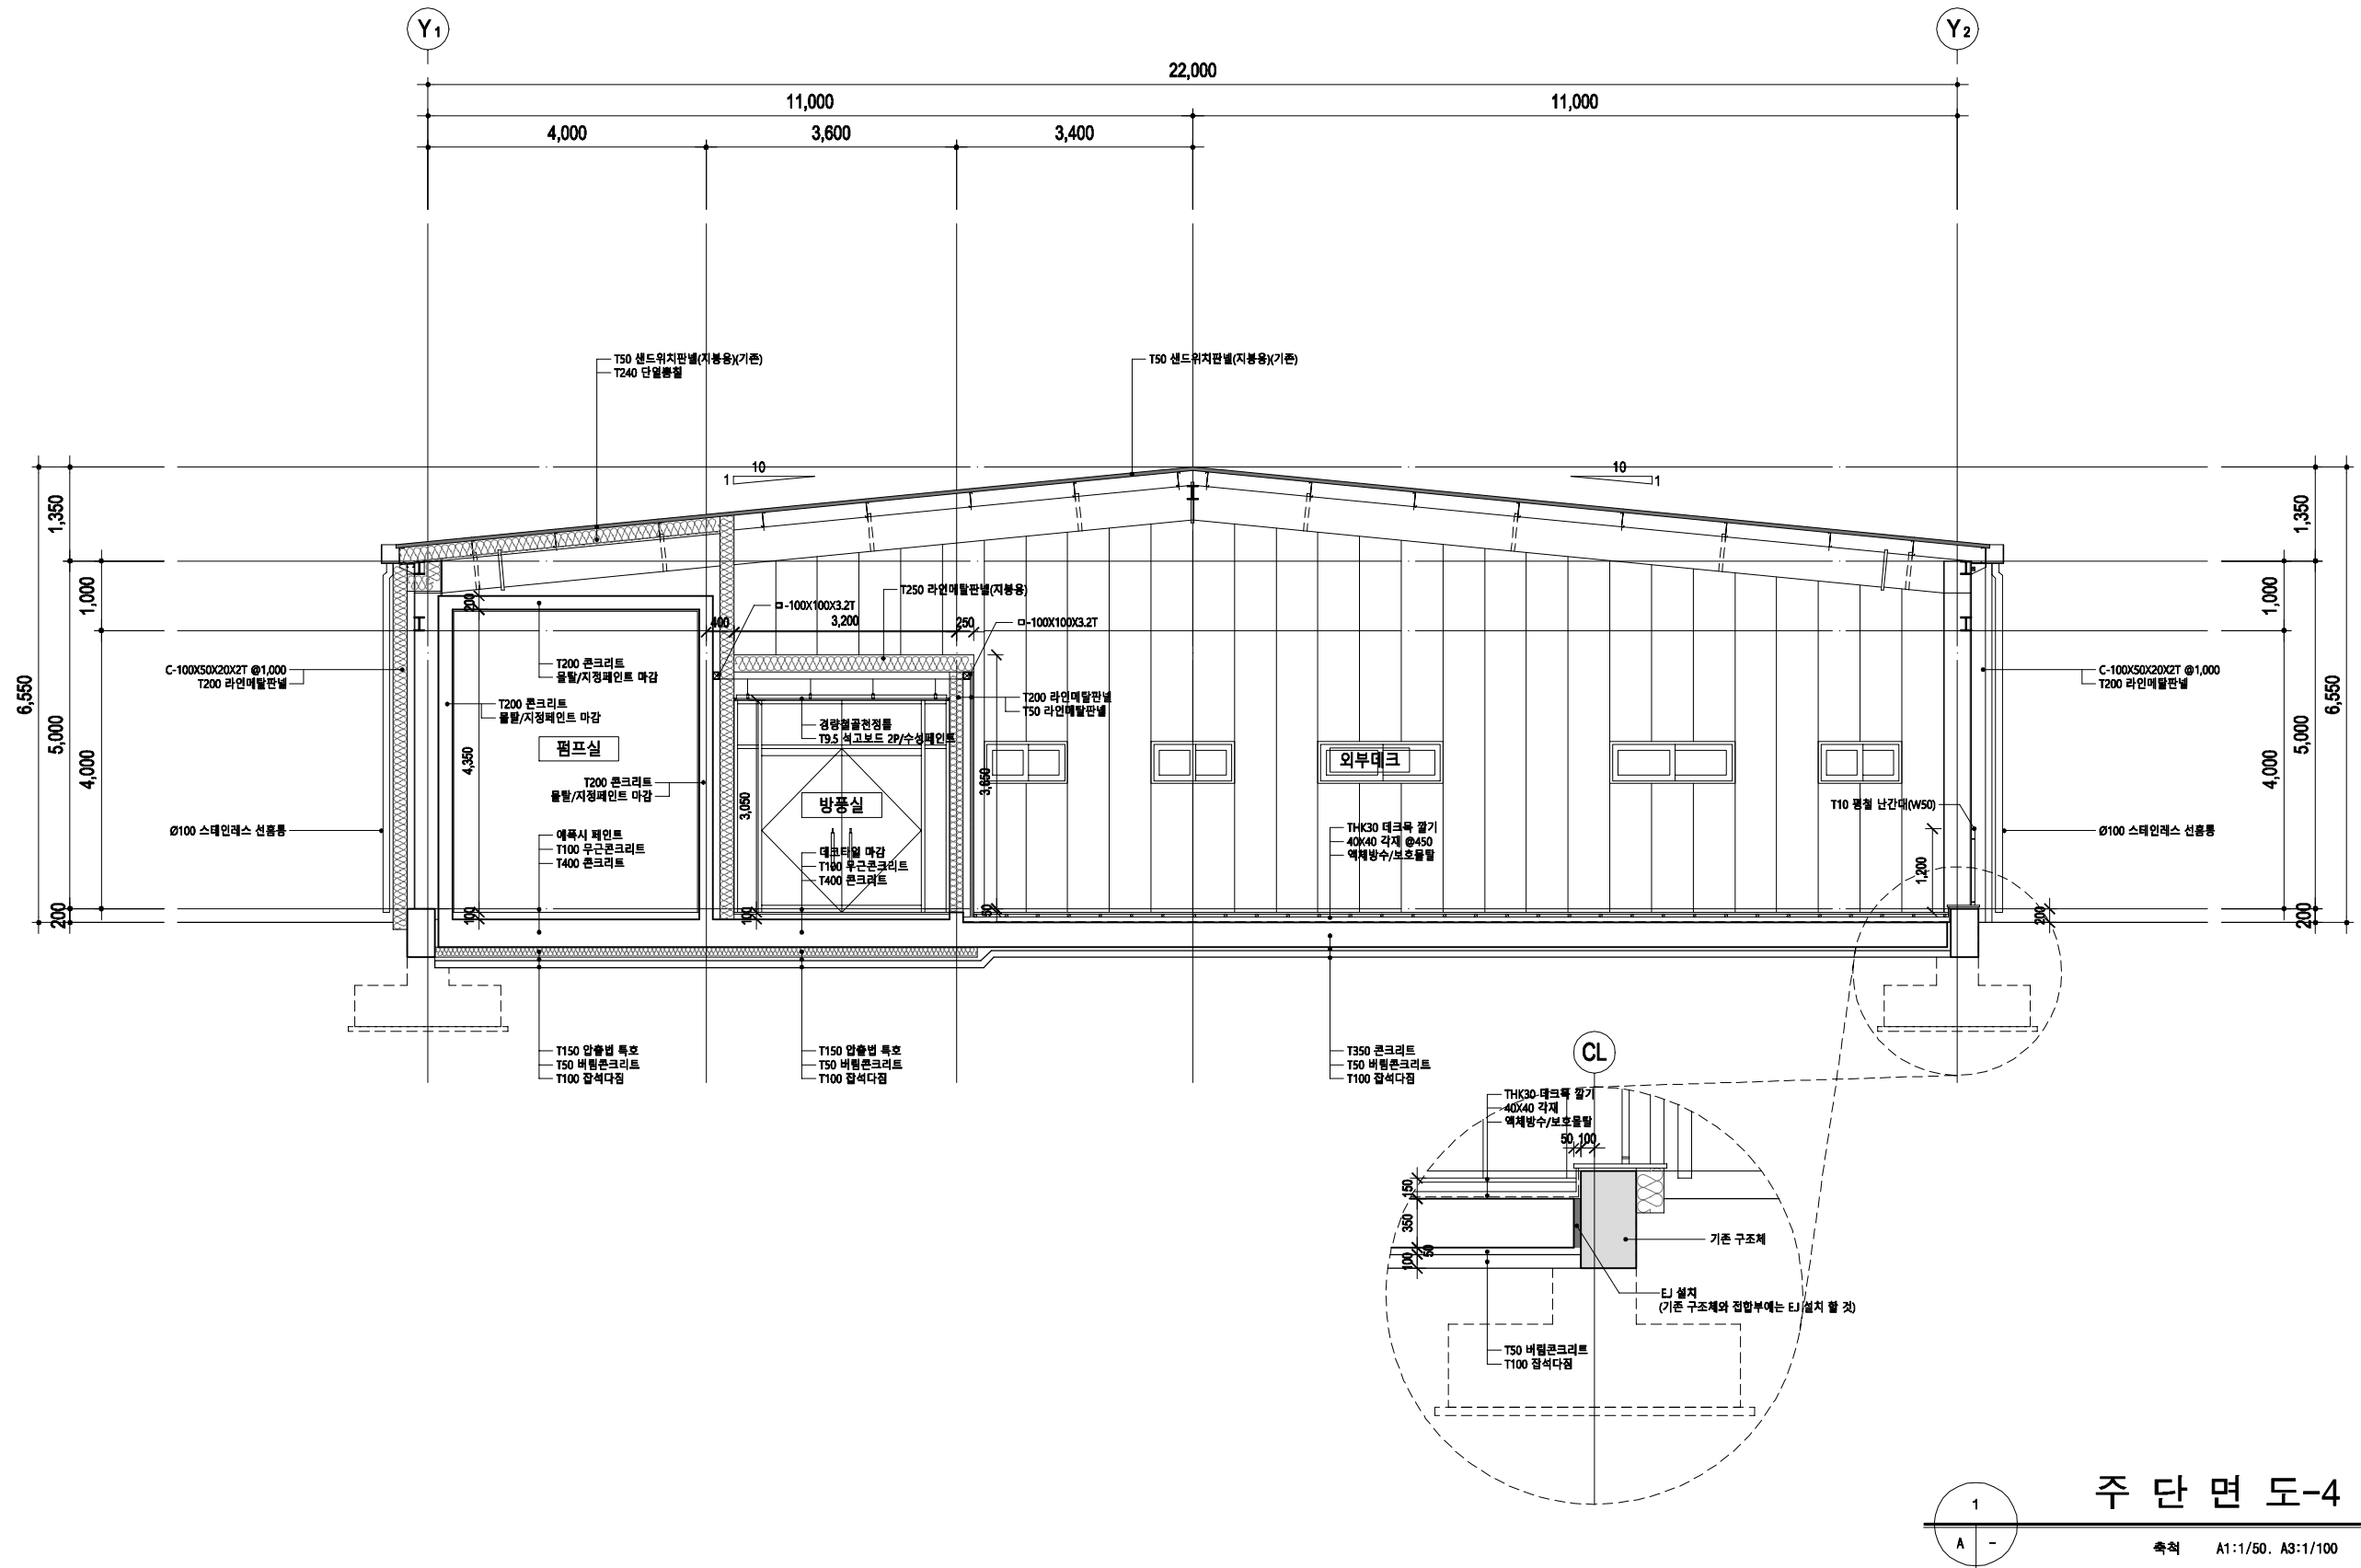

주 단 면 도-4


축척 A1:1/50, A3:1/100

리틀 포레스트  
봉뜨락 조성사업

## NOTE

The floor plan shows a large rectangular room with a smaller rectangular area on the left side. This smaller area contains several smaller rectangular shapes, possibly representing furniture or equipment. There are several small circles, likely representing doors or windows, along the perimeter of the room. A small rectangular area is also visible in the top left corner.

DRAWING NO. A02-305

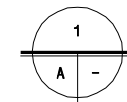

축척 A1:1/50. A3:1/100


PROJECT TITLE

리틀 포레스트  
봉뜨락 조성사업

PROJECT NO

NOTE

KEY PLAN

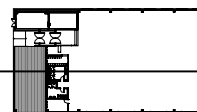

DESIGN CORP.

**이음** (주)이음건축사사무소

ADD. 대구광역시 동구 장동로 81, 5F  
TEL. 053.716.0776 FAX. 0505.720.0776  
E-mail. e-ul2020@naver.com  
Web. eul2020 / 0776

APPROVED BY  
대표이사/건축사 권오섭

CHECKED BY

DRAWN BY



DATE  
2023. 04.

DRAWING TITLE

주단면도-6


SCALE  
A3 : 1/ 100

DRAWING NO.  
A02- 306

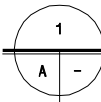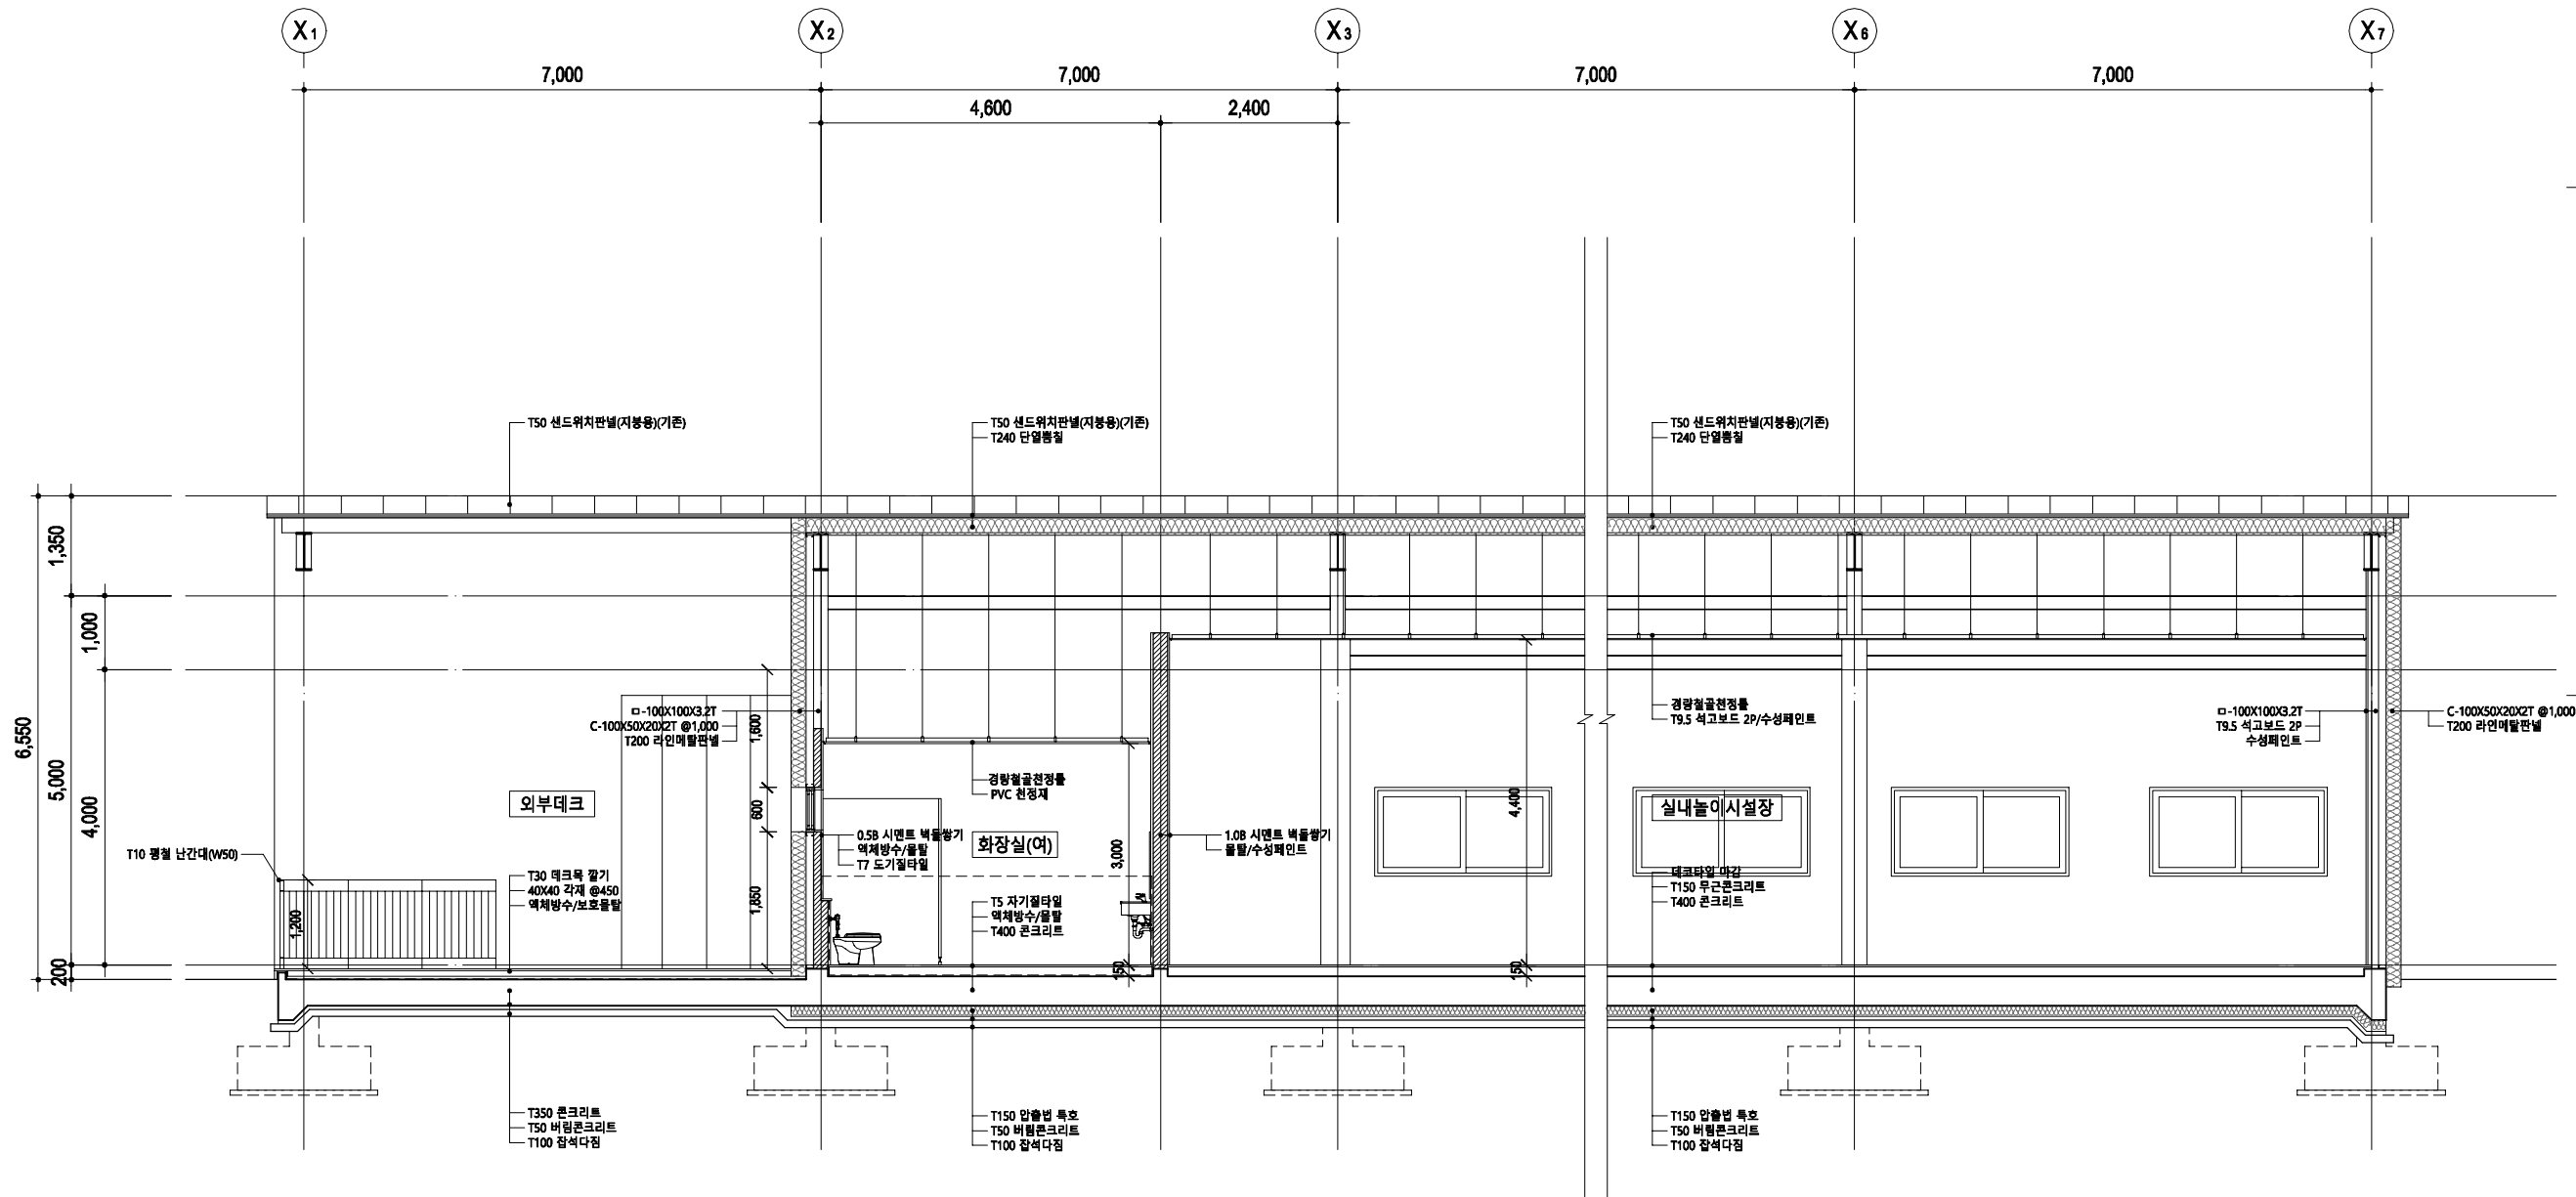


주 단 면 도-6

축척 A1:1/50, A3:1/100

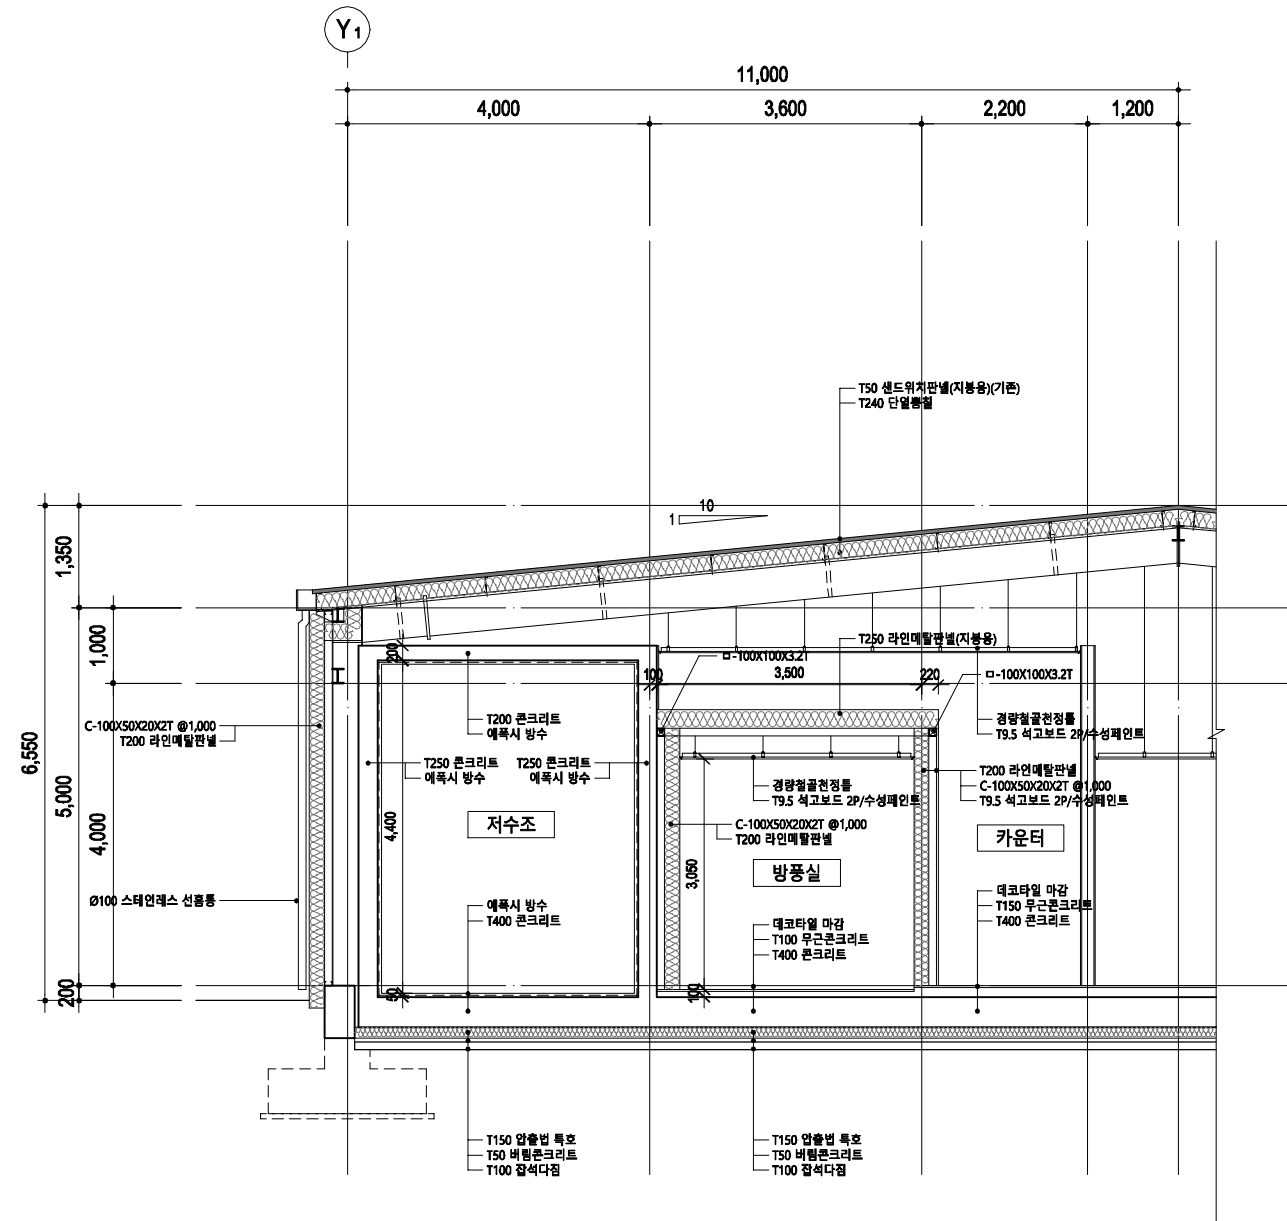


부분단면 상세도-1

축척 A1:1/50. A3:1/100

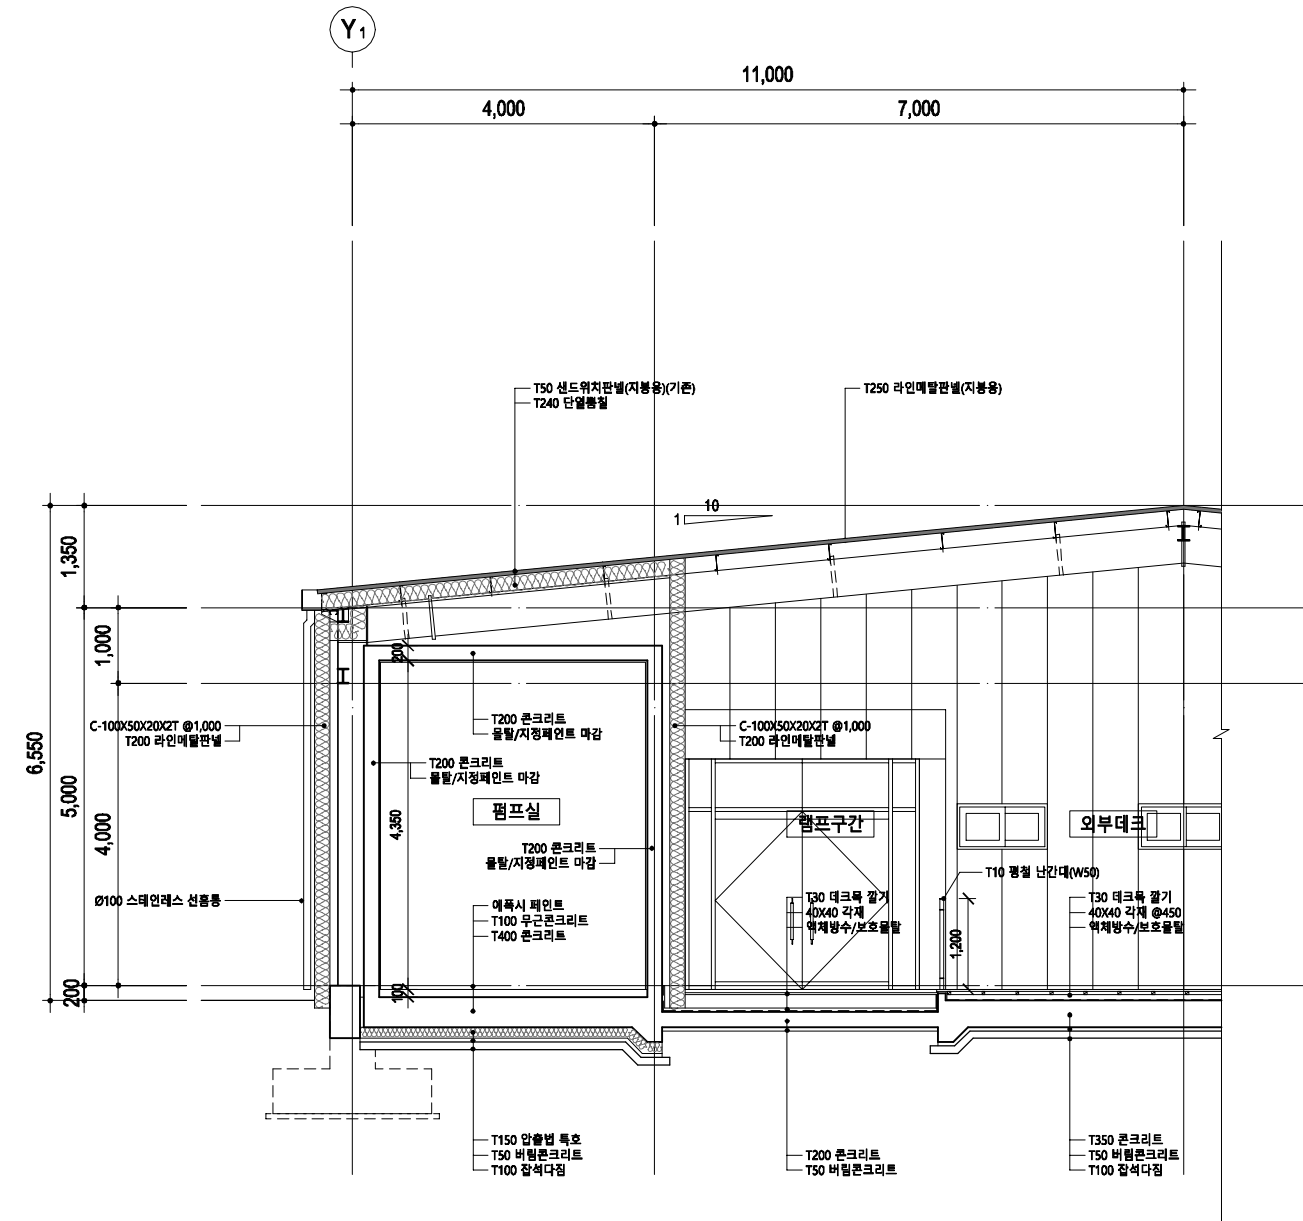

부분단면 상세도-2

축척 A1:1/50. A3:1/100

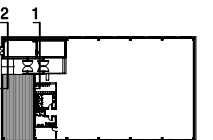


PROJECT TITLE

리틀 포레스트  
봉뜨락 조성사업

PROJECT NO

NOTE

KEY PLAN

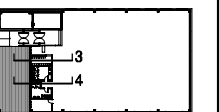

DESIGN CORP.

**이음** (주)이음건축사사무소

ADD. 대구광역시 중구 장동로 81, 5F  
TEL. 053.716.0776 FAX. 0505.720.0776  
E-mail. e-ul2020@naver.com  
Web. eul2020 / 0776

APPROVED BY  
대표이사/건축사 권오섭

CHECKED BY



DRAWN BY

DATE  
2023. 04.

DRAWING TITLE  
부분단면 상세도-3,4



SCALE  
A3 : 1/ 100

DRAWING NO.  
A02- 312

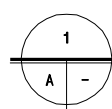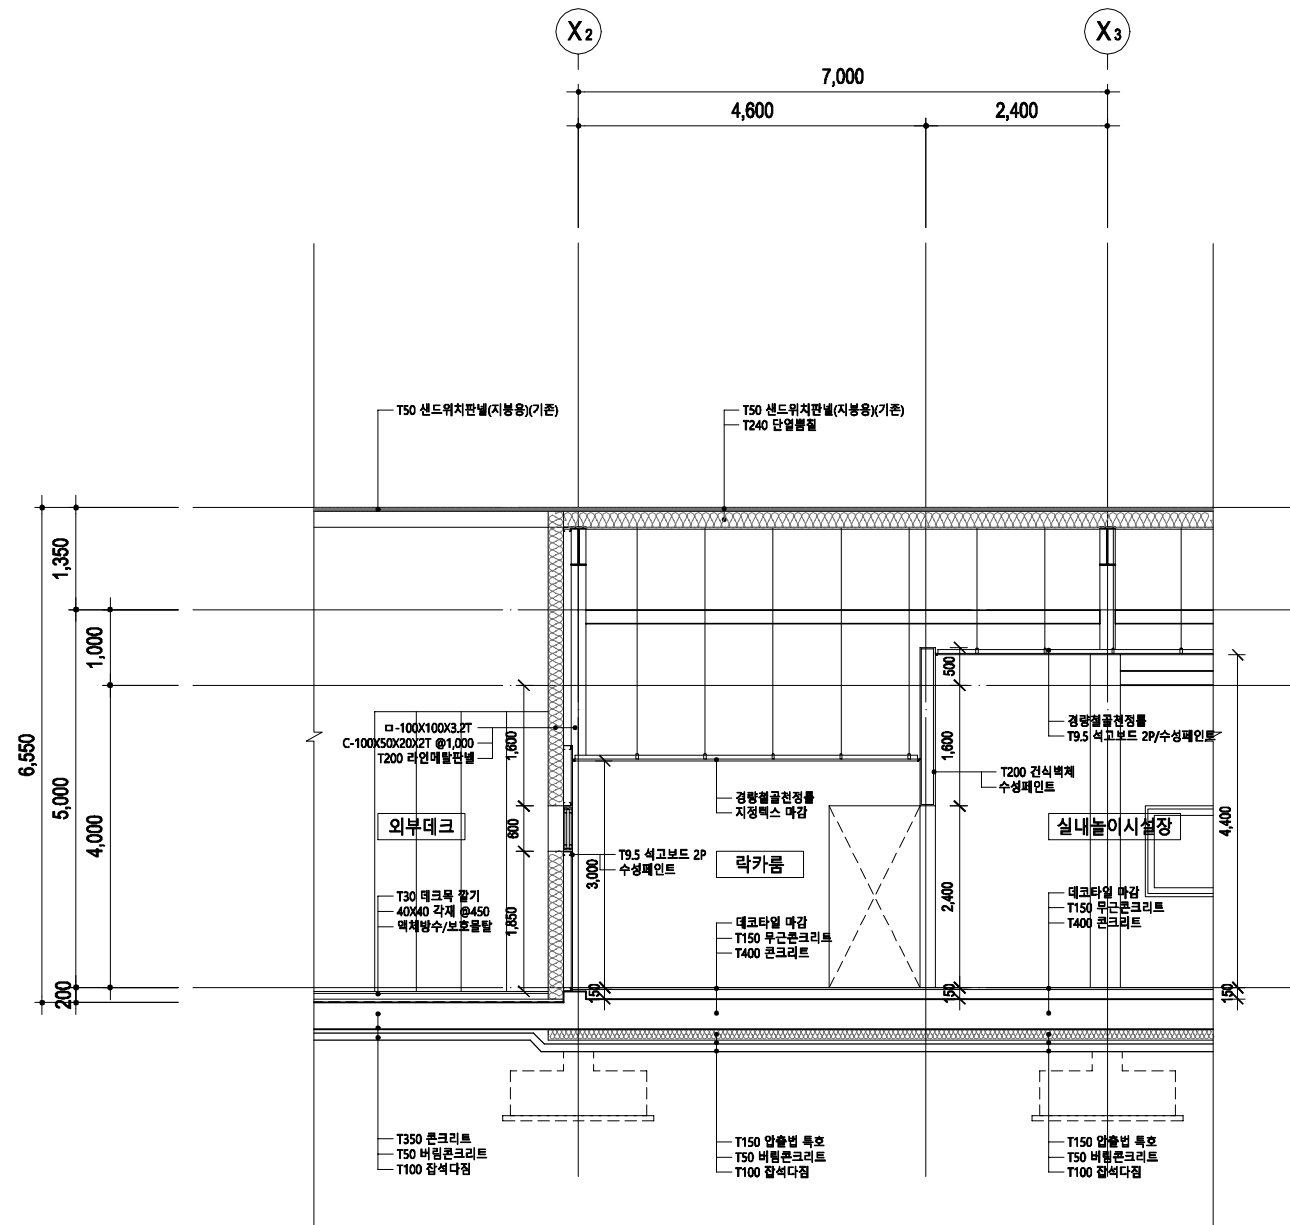


부분단면 상세도-3

축척 A1:1/50, A3:1/100

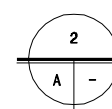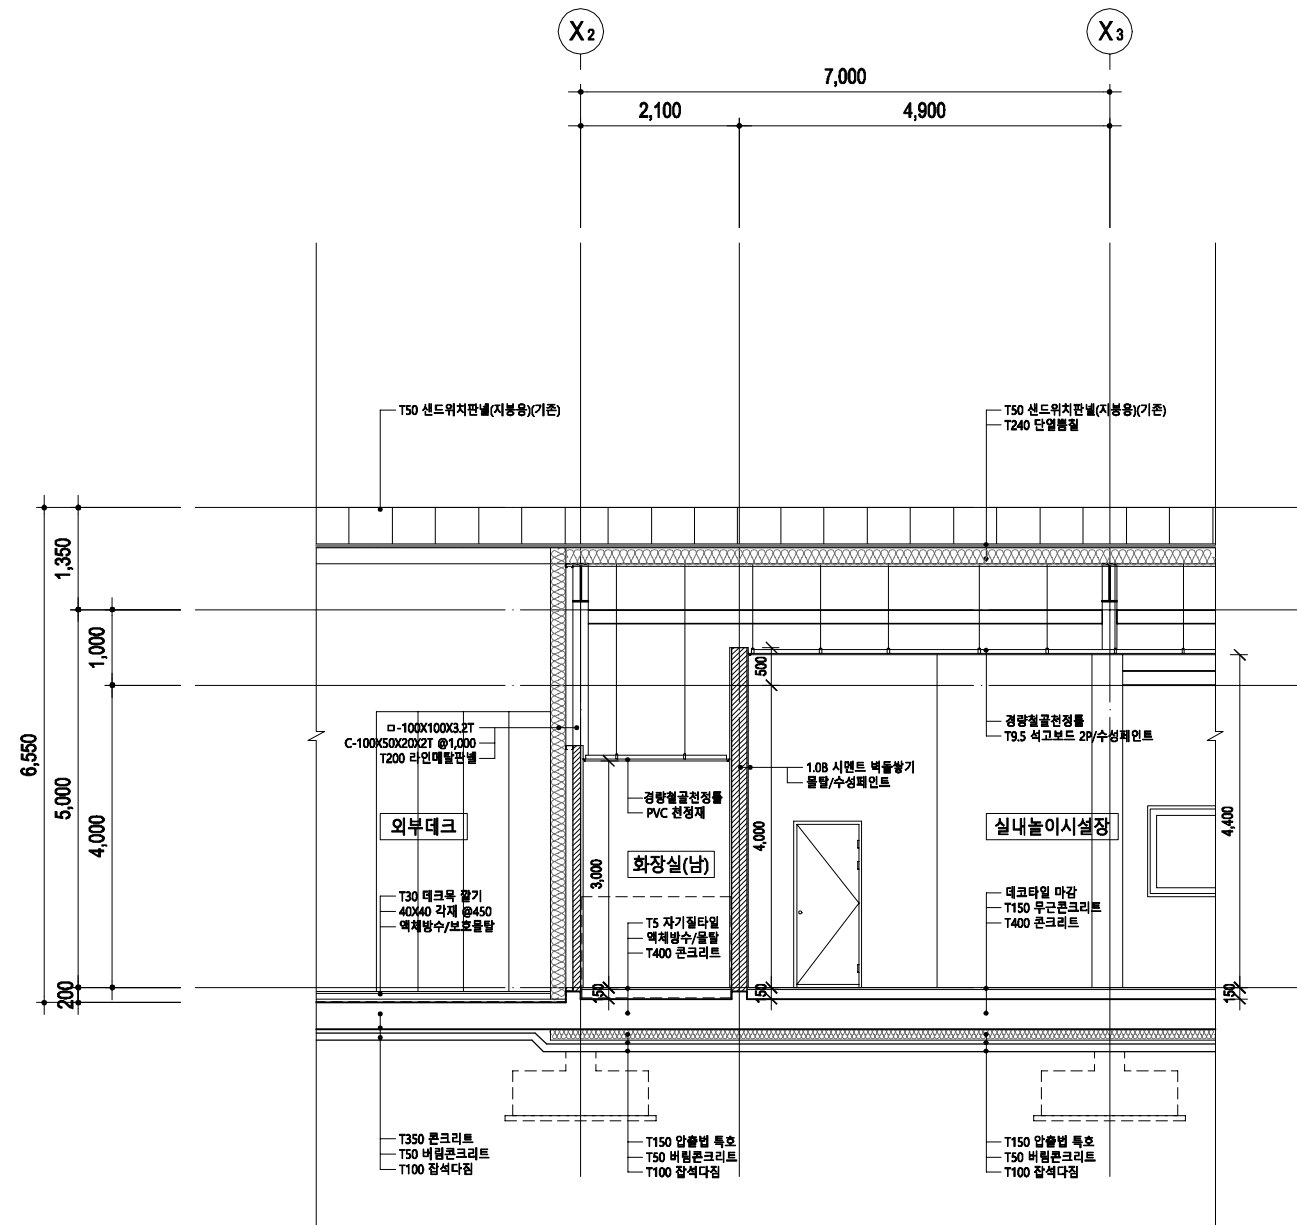


부분단면 상세도-4

축척 A1:1/50, A3:1/100

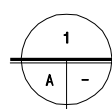

축척 A1:1/50. A3:1/100

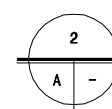

축척 A1:1/50. A3:1/100

**이원** (주)이을건축사사무소

APPROVED BY  
대표이사/건축사 권 오 섭

CHECKED BY \_\_\_\_\_

DRAWN BY

DATE 2023. 04.


|               |  |
|---------------|--|
| DRAWING TITLE |  |
|---------------|--|

부분단면 상세도-5,6

SCALE A3 : 1/ 100

DRAWING NO. **A02-313**



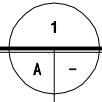

창호일람표(변경후)

축척 A1:1/40, A3:1/80

| 부 호       | 1                                                         | 1F | RF | 계  | 부 호                                                       | 1  | 1F | RF | 계 | 부 호                                                       | 2  | 1F | RF | 계 | 부 호                         | 1  | 1F | RF | 계 |
|-----------|-----------------------------------------------------------|----|----|----|-----------------------------------------------------------|----|----|----|---|-----------------------------------------------------------|----|----|----|---|-----------------------------|----|----|----|---|
| 개 소       | AD                                                        | 2  | -  | 2  | 개 소                                                       | SD | 1  | -  | 1 | 개 소                                                       | SD | 1  | -  | 1 | 개 소                         | PD | 3  | -  | 3 |
| 벽면 마감 기준선 |                                                           |    |    |    |                                                           |    |    |    |   |                                                           |    |    |    |   |                             |    |    |    |   |
| 위 치       | 방창실                                                       |    |    |    | 점프실                                                       |    |    |    |   | 소화수조                                                      |    |    |    |   | 화장실 (남), 화장실 (여), 수유실       |    |    |    |   |
| 재 료       | 150mm 알루미늄 커튼월창 + 세이프도어                                   |    |    |    | 프레임 : 1.6T 아연도강판, 문짝 : 0.8T 아연도강판(양면)                     |    |    |    |   | 프레임 : 1.6T 아연도강판, 문짝 : 0.8T 아연도강판(양면)                     |    |    |    |   | 문틀: 플라스틱 문틀                 |    |    |    |   |
| 철 물       | 기타부속철물 일체                                                 |    |    |    | 부속철물포함, 단열두께 20mm 이상                                      |    |    |    |   | 부속철물포함                                                    |    |    |    |   | 기타부속철물일체                    |    |    |    |   |
| 유 리       | 12mm 강화유리문 / FIX 8mm 강화유리                                 |    |    |    | -                                                         |    |    |    |   | -                                                         |    |    |    |   | -                           |    |    |    |   |
| 마 감       | 창틀주위 우레탄충진, 창틀주위 10x10 수밀코킹                               |    |    |    | 지정도장                                                      |    |    |    |   | 지정도장                                                      |    |    |    |   | 창틀주위 우레탄충진, 창틀주위 10x10 수밀코킹 |    |    |    |   |
| 부 호       | 1                                                         | 1F | RF | 계  | 부 호                                                       | 2  | 1F | RF | 계 | 부 호                                                       | 3  | 1F | RF | 계 | 부 호                         |    |    |    |   |
| 개 소       | AW                                                        | 16 | -  | 16 | 개 소                                                       | AW | 2  | -  | 2 | 개 소                                                       | AW | 3  | -  | 3 | 개 소                         |    |    |    |   |
| 벽면 마감 기준선 |                                                           |    |    |    |                                                           |    |    |    |   |                                                           |    |    |    |   |                             |    |    |    |   |
| 위 치       | 어린이 놀이시설장                                                 |    |    |    | 화장실 (남), 화장실 (여)                                          |    |    |    |   | 카운터, 락커룸, 수유실                                             |    |    |    |   |                             |    |    |    |   |
| 재 료       | 150mm AL 단열미서기단창                                          |    |    |    | 150mm AL 단열미서기단창                                          |    |    |    |   | 150mm AL 단열미서기단창                                          |    |    |    |   |                             |    |    |    |   |
| 철 물       | 부속철물 일체 / 방충망(내부)                                         |    |    |    | 부속철물 일체 / 방충망(내부)                                         |    |    |    |   | 부속철물 일체 / 방충망(내부)                                         |    |    |    |   |                             |    |    |    |   |
| 유 리       | 43mm 로이삼중유리 5LE(SKN145II(H/S))+14AR+SCL+14AR+5LE(PLA ONE) |    |    |    | 43mm 로이삼중유리 5LE(SKN145II(H/S))+14AR+SCL+14AR+5LE(PLA ONE) |    |    |    |   | 43mm 로이삼중유리 5LE(SKN145II(H/S))+14AR+SCL+14AR+5LE(PLA ONE) |    |    |    |   |                             |    |    |    |   |
| 마 감       | 창틀주위 우레탄충진, 창틀주위 10x10 수밀코킹                               |    |    |    | 창틀주위 우레탄충진, 창틀주위 10x10 수밀코킹                               |    |    |    |   | 창틀주위 우레탄충진, 창틀주위 10x10 수밀코킹                               |    |    |    |   |                             |    |    |    |   |
| 부 호       |                                                           |    |    |    |                                                           |    |    |    |   |                                                           |    |    |    |   |                             |    |    |    |   |
| 개 소       |                                                           |    |    |    |                                                           |    |    |    |   |                                                           |    |    |    |   |                             |    |    |    |   |
| 벽면 마감 기준선 |                                                           |    |    |    |                                                           |    |    |    |   |                                                           |    |    |    |   |                             |    |    |    |   |
| 위 치       |                                                           |    |    |    |                                                           |    |    |    |   |                                                           |    |    |    |   |                             |    |    |    |   |
| 재 료       |                                                           |    |    |    |                                                           |    |    |    |   |                                                           |    |    |    |   |                             |    |    |    |   |
| 철 물       |                                                           |    |    |    |                                                           |    |    |    |   |                                                           |    |    |    |   |                             |    |    |    |   |
| 유 리       |                                                           |    |    |    |                                                           |    |    |    |   |                                                           |    |    |    |   |                             |    |    |    |   |
| 마 감       |                                                           |    |    |    |                                                           |    |    |    |   |                                                           |    |    |    |   |                             |    |    |    |   |

PROJECT TITLE

리틀 포레스트  
봉뜨락 조성사업

PROJECT NO

NOTE

KEY PLAN

DESIGN CORP.



ADD. 대구광역시 중구 장동로 81, 5F  
TEL. 053.716.0776 FAX. 0505.720.0776  
E-mail. e-ul2020@naver.com  
Web. eul2020 / 0776

APPROVED BY  
대표이사 / 건축사 권오섭

CHECKED BY


DRAWN BY

DATE  
2023. 04.

DRAWING TITLE  
창호일람표  
(변경후)

SCALE  
A3 : 1/ 80


DRAWING NO.  
A02- 402

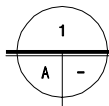


# 화장실 전개도-1

축척 A1:1/30, A3:1/60


화장실(여) 확대 평면도

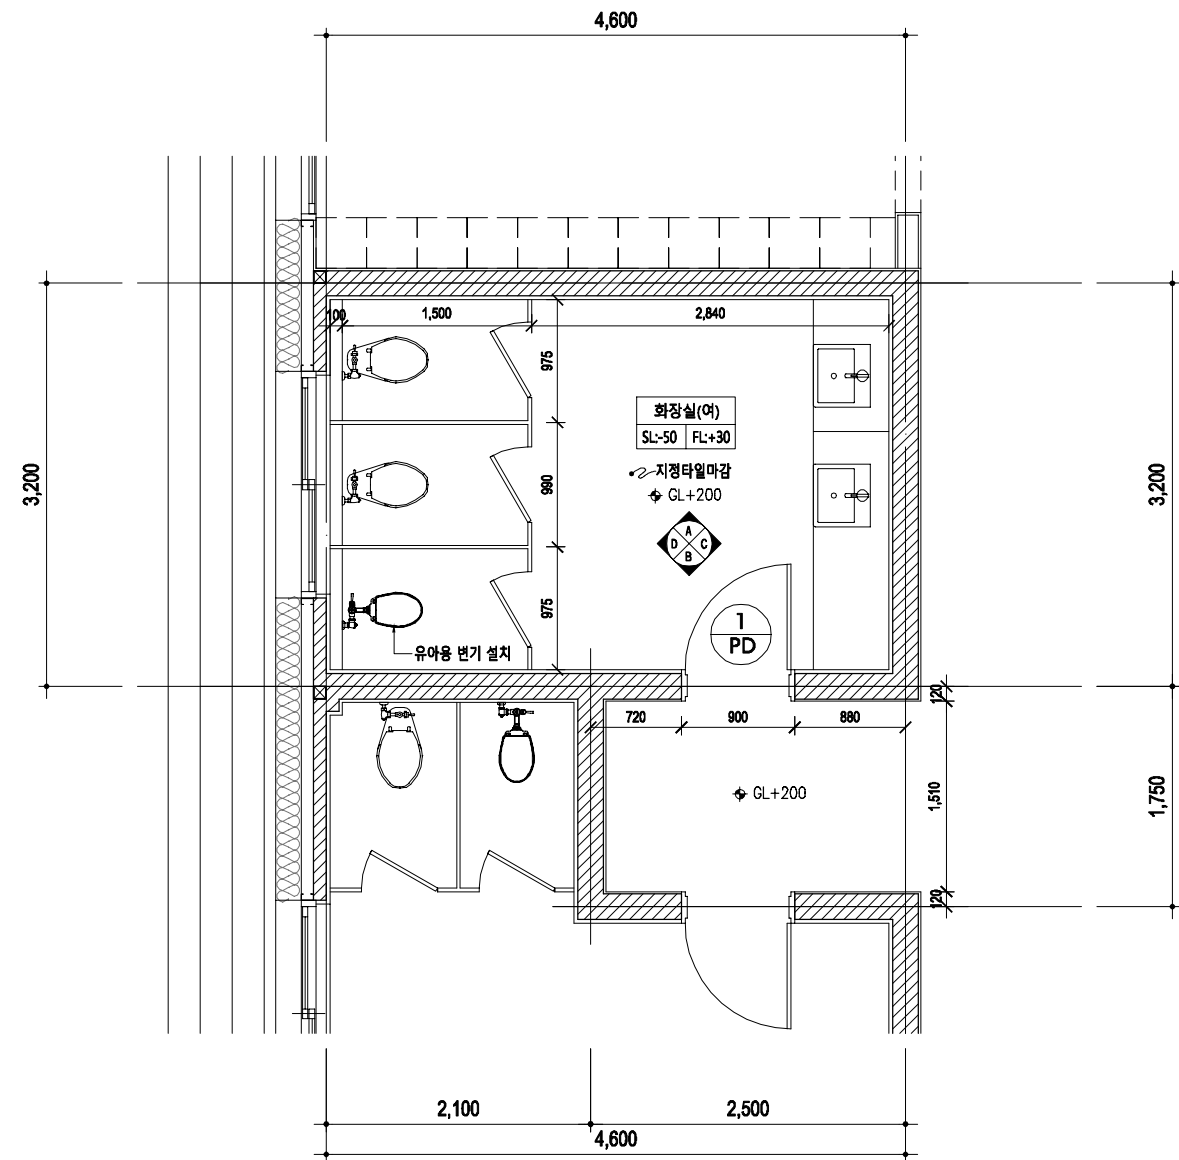


화장실(여) "A"전개도

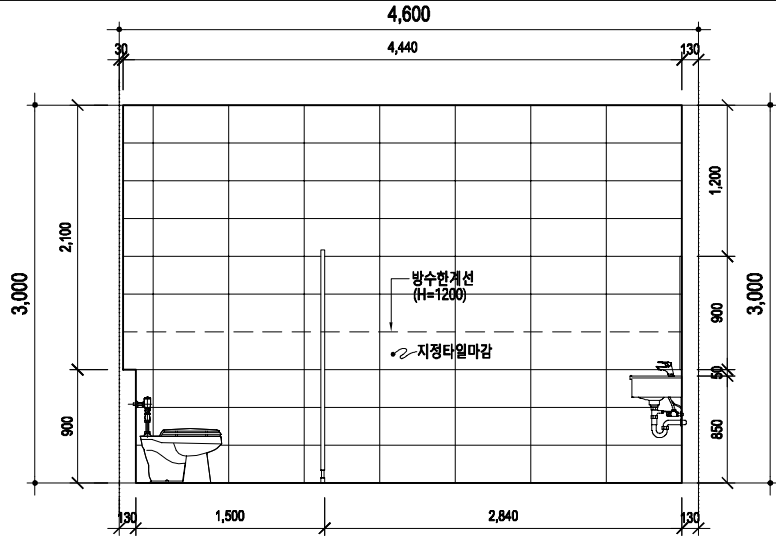


화장실(여) "B"전개도

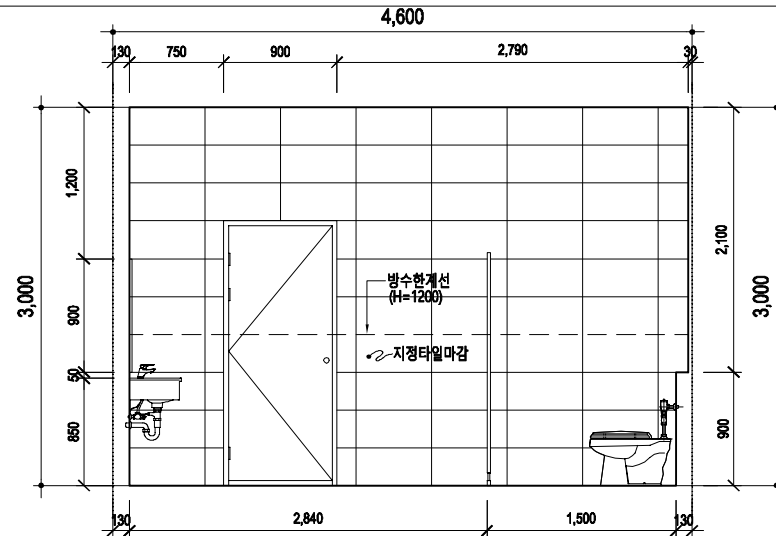

화장실(여) "C"전개도

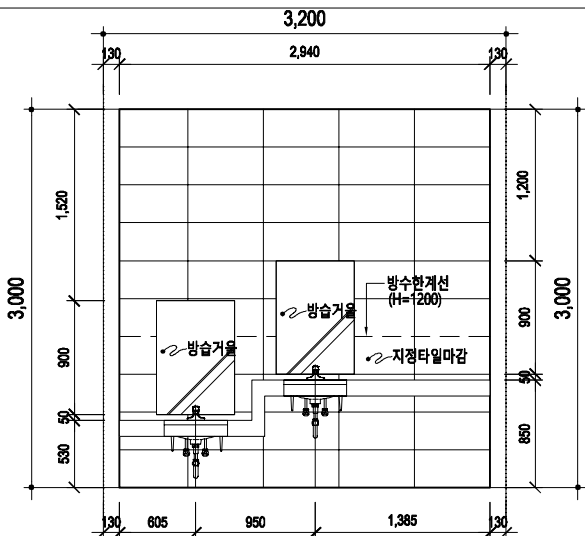

화장실(여) "D"전개도

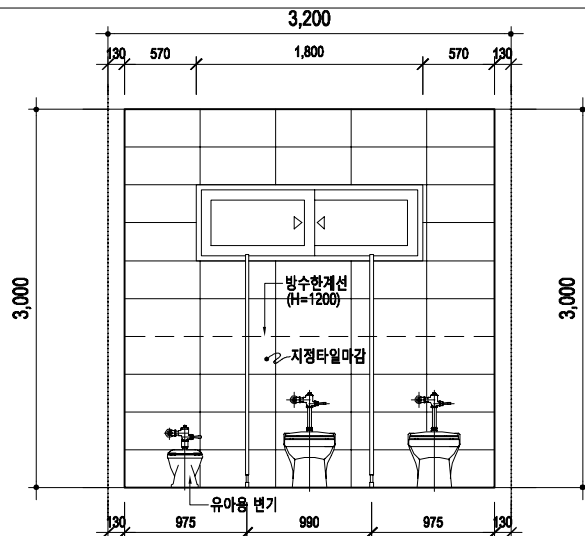

PROJECT TITLE

리틀 포레스트  
봉뜨락 조성사업

PROJECT NO

NOTE

KEY PLAN

DESIGN CORP.

**이음** (주)이음건축사사무소

ADD. 대구광역시 중구 장동로 81, 5F  
TEL. 053.716.0776 FAX. 0505.720.0776  
E-mail. e-ul2020@naver.com  
Web. eul2020 / 0776

APPROVED BY  
대표이사/건축사 권오섭

CHECKED BY

DRAWN BY


DATE 2023. 04.

DRAWING TITLE

화장실 전개도-1

SCALE A3 : 1/ 60


DRAWING NO. A02- 501

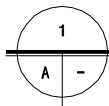


# 화장실 전개도-2

축척 A1:1/30, A3:1/60


## 화장실(남) 확대 평면도

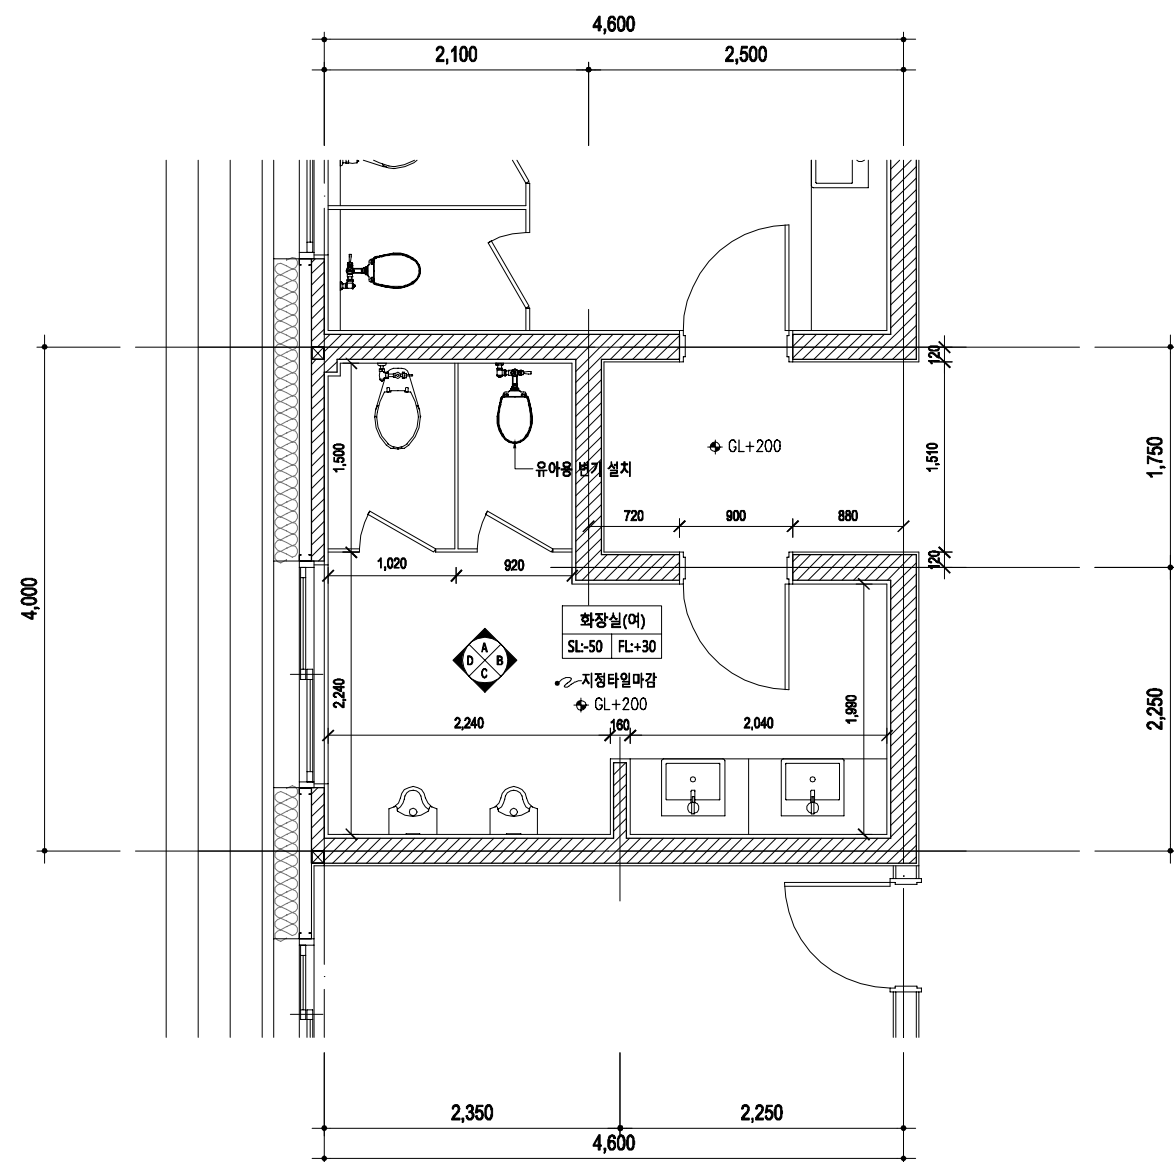


## 화장실(남) "A"전개도

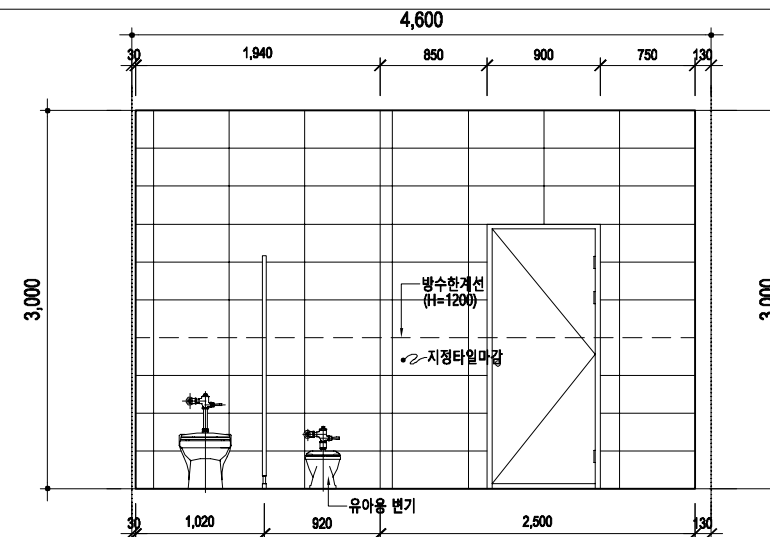


## 화장실(남) "B"전개도

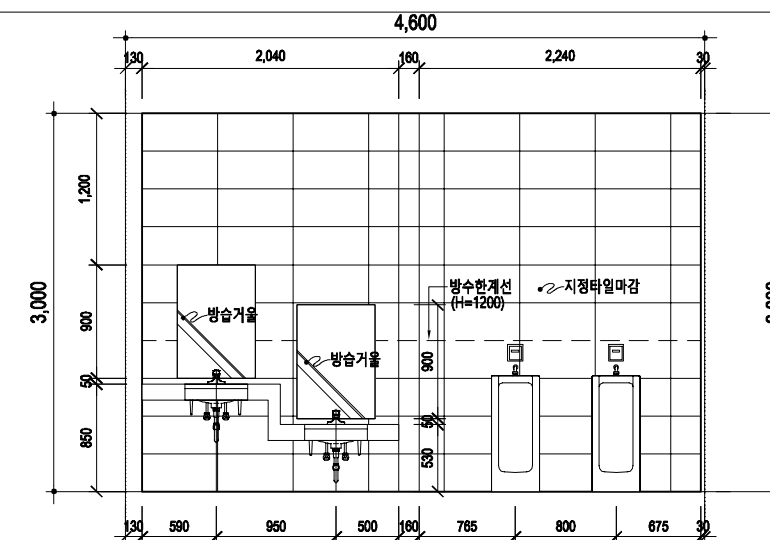

## 화장실(남) "C"전개도

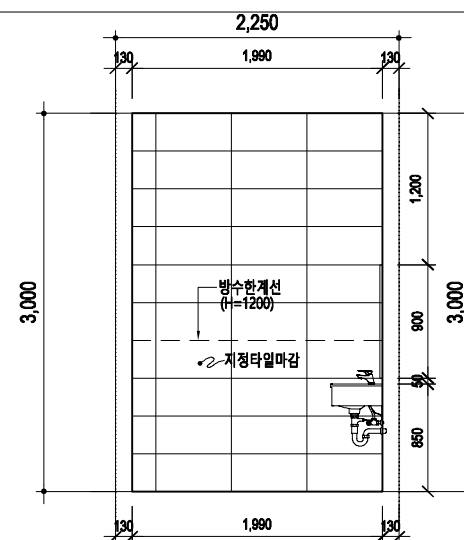

## 화장실(남) "D"전개도

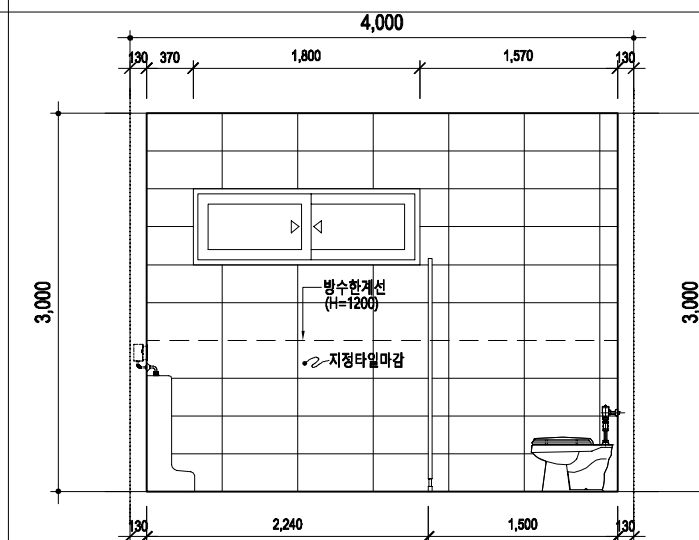

PROJECT TITLE

리틀 포레스트  
봉뜨락 조성사업

PROJECT NO

NOTE

KEY PLAN

DESIGN CORP.

**이음** (주)이음건축사사무소

ADD. 대구광역시 중구 장동로 81, 5F  
TEL. 053.716.0776 FAX. 0505.720.0776  
E-mail. e-ul2020@naver.com  
Web. eul2020 / 0776

APPROVED BY  
대표이사/건축사 권오섭

CHECKED BY

DRAWN BY

DATE  
2023. 04.

DRAWING TITLE

화장실 전개도-2

SCALE  
A3 : 1/ 60

DRAWING NO.  
A02- 502

### # 지역별 형별 성능 관계 내역 - 1 (중부1지역)

구분

W1

외 벽 (외 기 직 접)

외 부

내 부

319

200

100

19

</

리틀 포레스트  
봉뜨락 조성사업

PROJECT NO

**NOTE**

## KEY PLAN

DESIGN CORP.



ADD. 대구광역시 동구 장동로 81, 5F  
TEL. 053.716.0776 FAX. 0505.720.0776  
E-mail. e-ul2020@naver.com  
Web. eul2020 / 0776

APPROVED BY  
대표이사/건축사 권 오 섭

DRAWN BY

2023. 04.

**DRAWING TITLE**

### 형별성능관계내역-1

SCALE

A3 : 1/ 10

DRAWING NO. **A**

A02-901

### # 지역별 형별 성능 관계 내역 - 2 (중부1지역)

[illegible]리틀 포레스트  
봉뜨락 조성사업

PROJECT NO

**NOTE**

## KEY PLAN

DESIGN CORP.

**이을건축사사무소**  
ADD. 대구광역시 동구 장동로 81, 5F  
TEL. 053.716.0776 FAX. 0505.720.0776  
E-mail. e-ul2020@naver.com  
Web. eul2020 / 0776

APPROVED BY  
대표이사/건축사 권오섭

DRAWN BY




DATE 2023. 04.

|                      |
|----------------------|
| <b>DRAWING TITLE</b> |
|----------------------|

SCALE A3 : 1/ 20

DRAWING NO. **A02-902**

# 지역별 형별 성능 관계 내역 - 3 (중부1지역)
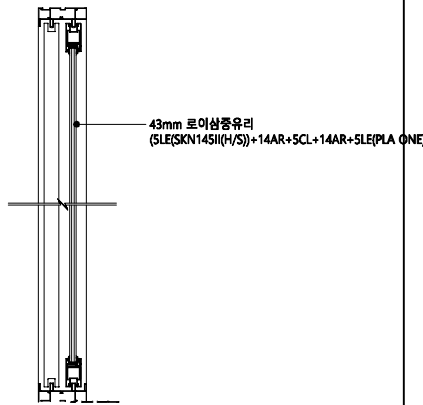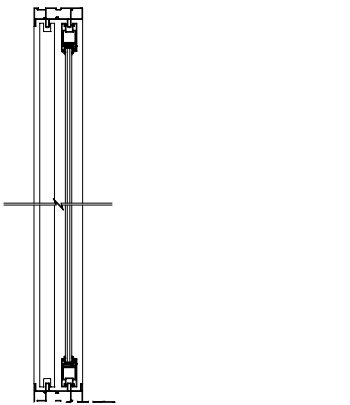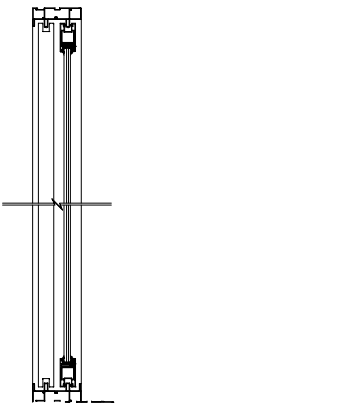
| 구분                                   |    | G1                                                                                |  | 알루미늄 미서기창                                                                           |  | D1                                                                                  |                   | 방풍구조문 |                              | D2  |     | 철제문               |  |                                 |  |     |
|--------------------------------------|----|-----------------------------------------------------------------------------------|--|-------------------------------------------------------------------------------------|--|-------------------------------------------------------------------------------------|-------------------|-------|------------------------------|-----|-----|-------------------|--|---------------------------------|--|-----|
| 단<br>면<br>구<br>조                     |    | 외 측                                                                               |  | 내 측                                                                                 |  | 외 측                                                                                 |                   | 내 측   |                              | 외 측 |     | 내 측               |  |                                 |  |     |
|                                      |    |  |  |  |  |  |                   |       |                              |     |     |                   |  |                                 |  |     |
| 열<br>관<br>류<br>율<br>계<br>산<br>결<br>과 | 번호 | 구 분                                                                               |  | 내 용                                                                                 |  | 번호                                                                                  | 구 분               |       | 내 용                          |     | 번호  | 구 분               |  | 내 용                             |  |     |
|                                      | 1  | 두 겹                                                                               |  | 43mm 로이삼중유리<br>SLE(SKN145II(H/S))+14AR+5CL+14AR+5LE(PLA ONE)                        |  | 1                                                                                   | 두 겹               |       | THK12 강화유리문 / FIX: THK8 강화유리 |     | 1   | 두 겹               |  | -                               |  |     |
|                                      | 2  | 종 류                                                                               |  | 미서기창, 아르곤 주입+로이유리(소프트코팅)                                                            |  | 2                                                                                   | 종 류               |       | 방풍구조문                        |     | 2   | 종 류               |  | 철제문                             |  |     |
|                                      | 3  | 프 레 임                                                                             |  | 알루미늄                                                                                |  | 3                                                                                   | 프 레 임             |       | 알루미늄                         |     | 3   | 프 레 임             |  | 1.6T 아연도강판, 문짝 : 0.8T 아연도강판(양면) |  |     |
|                                      | 4  | 기밀성 등급(KS F 2292)                                                                 |  | 1 등급 (1 m³/hm²미만)                                                                   |  | 4                                                                                   | 기밀성 등급(KS F 2292) |       | 1 등급 (1 m³/hm²미만)            |     | 4   | 기밀성 등급(KS F 2292) |  | 1 등급 (1 m³/hm²미만)               |  |     |
|                                      |    |                                                                                   |  |                                                                                     |  |                                                                                     |                   |       |                              |     |     |                   |  |                                 |  |     |
|                                      |    | 적용열관류율(W/m².K)                                                                    |  | 0.979                                                                               |  |                                                                                     | 적용열관류율(W/m².K)    |       | 1.500                        |     |     | 적용열관류율(W/m².K)    |  | 1.244                           |  |     |
|                                      |    | 기준열관류율(W/m².K)                                                                    |  | 1.300 이하                                                                            |  | 중부1                                                                                 | 기준열관류율(W/m².K)    |       | 1.500 이하                     |     | 중부1 | 기준열관류율(W/m².K)    |  | 1.500 이하                        |  | 중부1 |
|                                      | 구분 |                                                                                   |  |                                                                                     |  |                                                                                     |                   |       |                              |     |     |                   |  |                                 |  |     |
| 단<br>면<br>구<br>조                     |    |                                                                                   |  |                                                                                     |  |                                                                                     |                   |       |                              |     |     |                   |  |                                 |  |     |
|                                      |    |                                                                                   |  |                                                                                     |  |                                                                                     |                   |       |                              |     |     |                   |  |                                 |  |     |
| 열<br>관<br>류<br>율<br>계<br>산<br>결<br>과 | 번호 | 구 분                                                                               |  | 내 용                                                                                 |  | 번호                                                                                  | 구 분               |       | 내 용                          |     | 번호  | 구 분               |  | 내 용                             |  |     |
|                                      |    |                                                                                   |  |                                                                                     |  |                                                                                     |                   |       |                              |     |     |                   |  |                                 |  |     |
|                                      |    | 적용열관류율(W/m².K)                                                                    |  |                                                                                     |  |                                                                                     | 적용열관류율(W/m².K)    |       |                              |     |     | 적용열관류율(W/m².K)    |  |                                 |  |     |
|                                      |    | 기준열관류율(W/m².K)                                                                    |  |                                                                                     |  |                                                                                     | 기준열관류율(W/m².K)    |       |                              |     |     | 기준열관류율(W/m².K)    |  |                                 |  |     |
|                                      |    |                                                                                   |  |                                                                                     |  |                                                                                     |                   |       |                              |     |     |                   |  |                                 |  |     |

PROJECT TITLE  
리틀 포레스트  
봉뜨락 조성사업

PROJECT NO

NOTE

KEY PLAN

DESIGN CORP.  
**이음** (주)이음건축사사무소

ADD. 대구광역시 동구 장동로 81, 5F  
TEL. 053.716.0776 FAX. 0505.720.0776  
E-mail: eul2020@naver.com  
Web. eul2020 / 0776

APPROVED BY  
대표이사 / 건축사 권오섭  
CHECKED BY


DRAWN BY

DATE  
2023. 04.

DRAWING TITLE  
외피 전개도-1 (외벽)

SCALE  
A3 : 1/ 150

DRAWING NO.  
A02-904

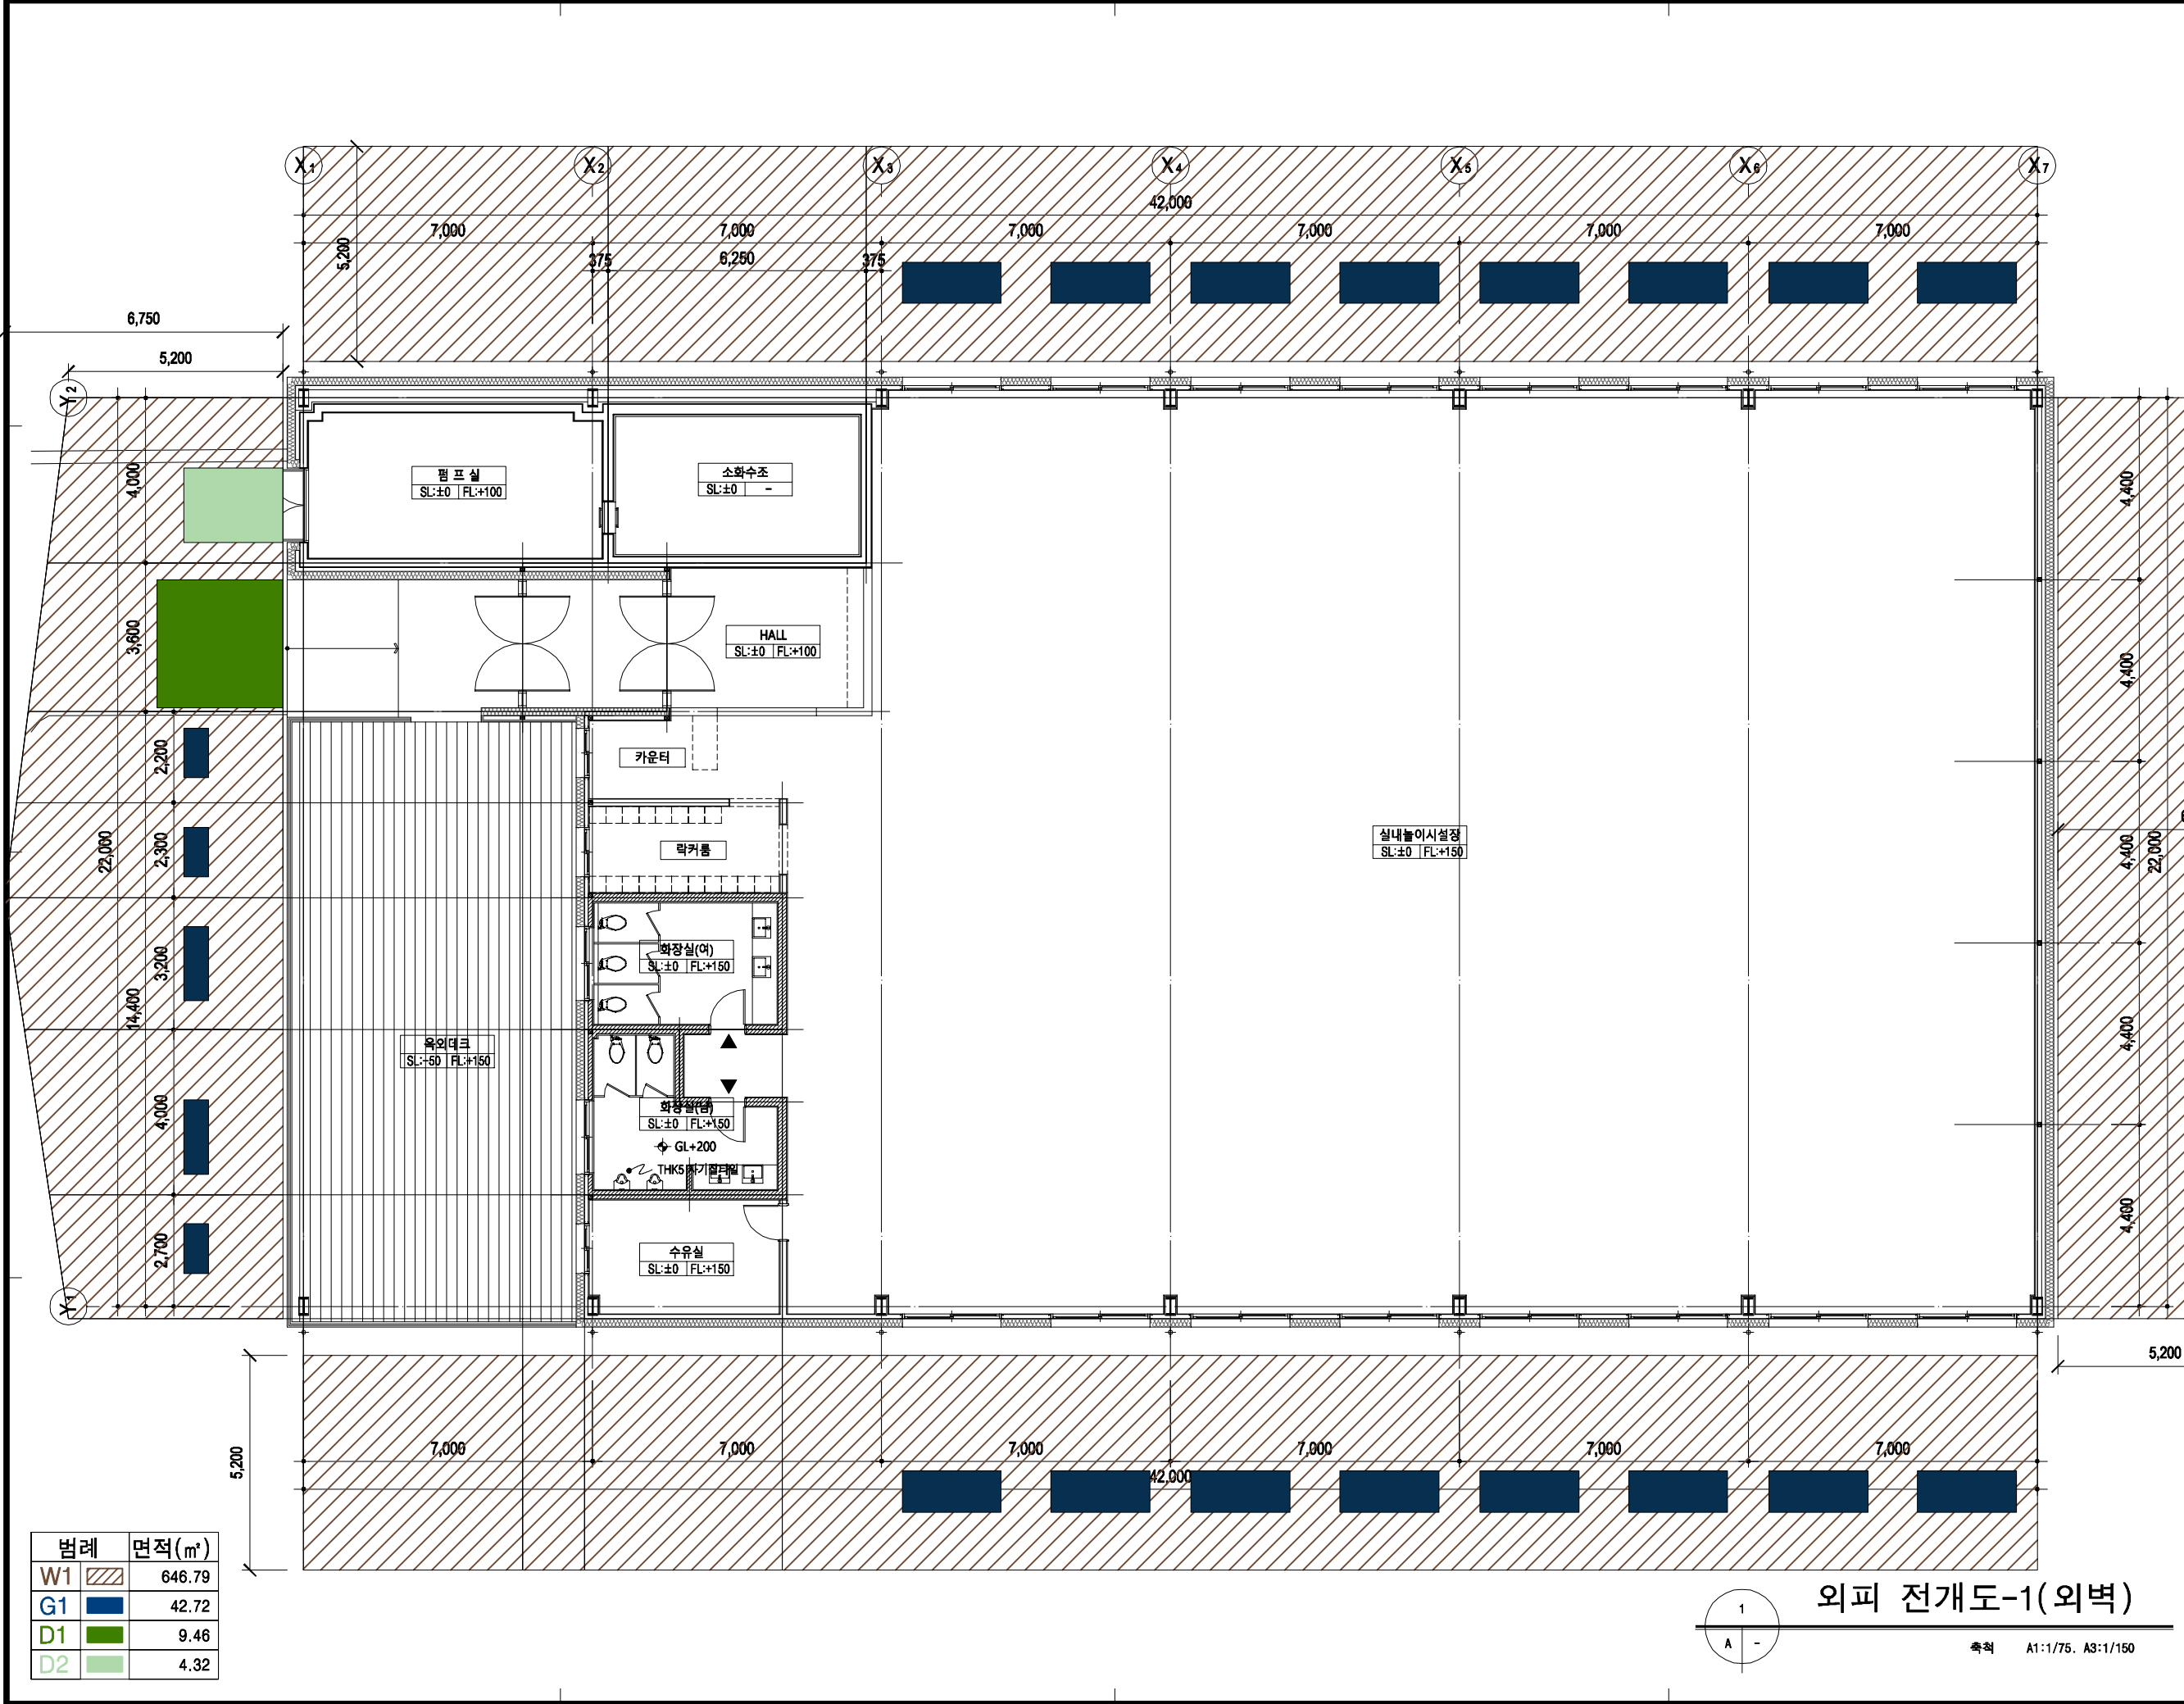

PROJECT TITLE

리틀 포레스트  
봉뜨락 조성사업

PROJECT NO

NOTE

KEY PLAN

DESIGN CORP.

**이음** (주)이음건축사사무소

ADD. 대구광역시 동구 장동로 81, 5F  
TEL. 053.716.0776 FAX. 0505.720.0776  
E-mail. e-ul2020@naver.com  
Web. eul2020 / 0776

APPROVED BY  
대표이사 / 건축사 권오섭

CHECKED BY


DRAWN BY

DATE  
2023. 04.


DRAWING TITLE  
외피 전개도-2  
(바닥)

SCALE  
A3 : 1/ 150

DRAWING NO.  
A02-905

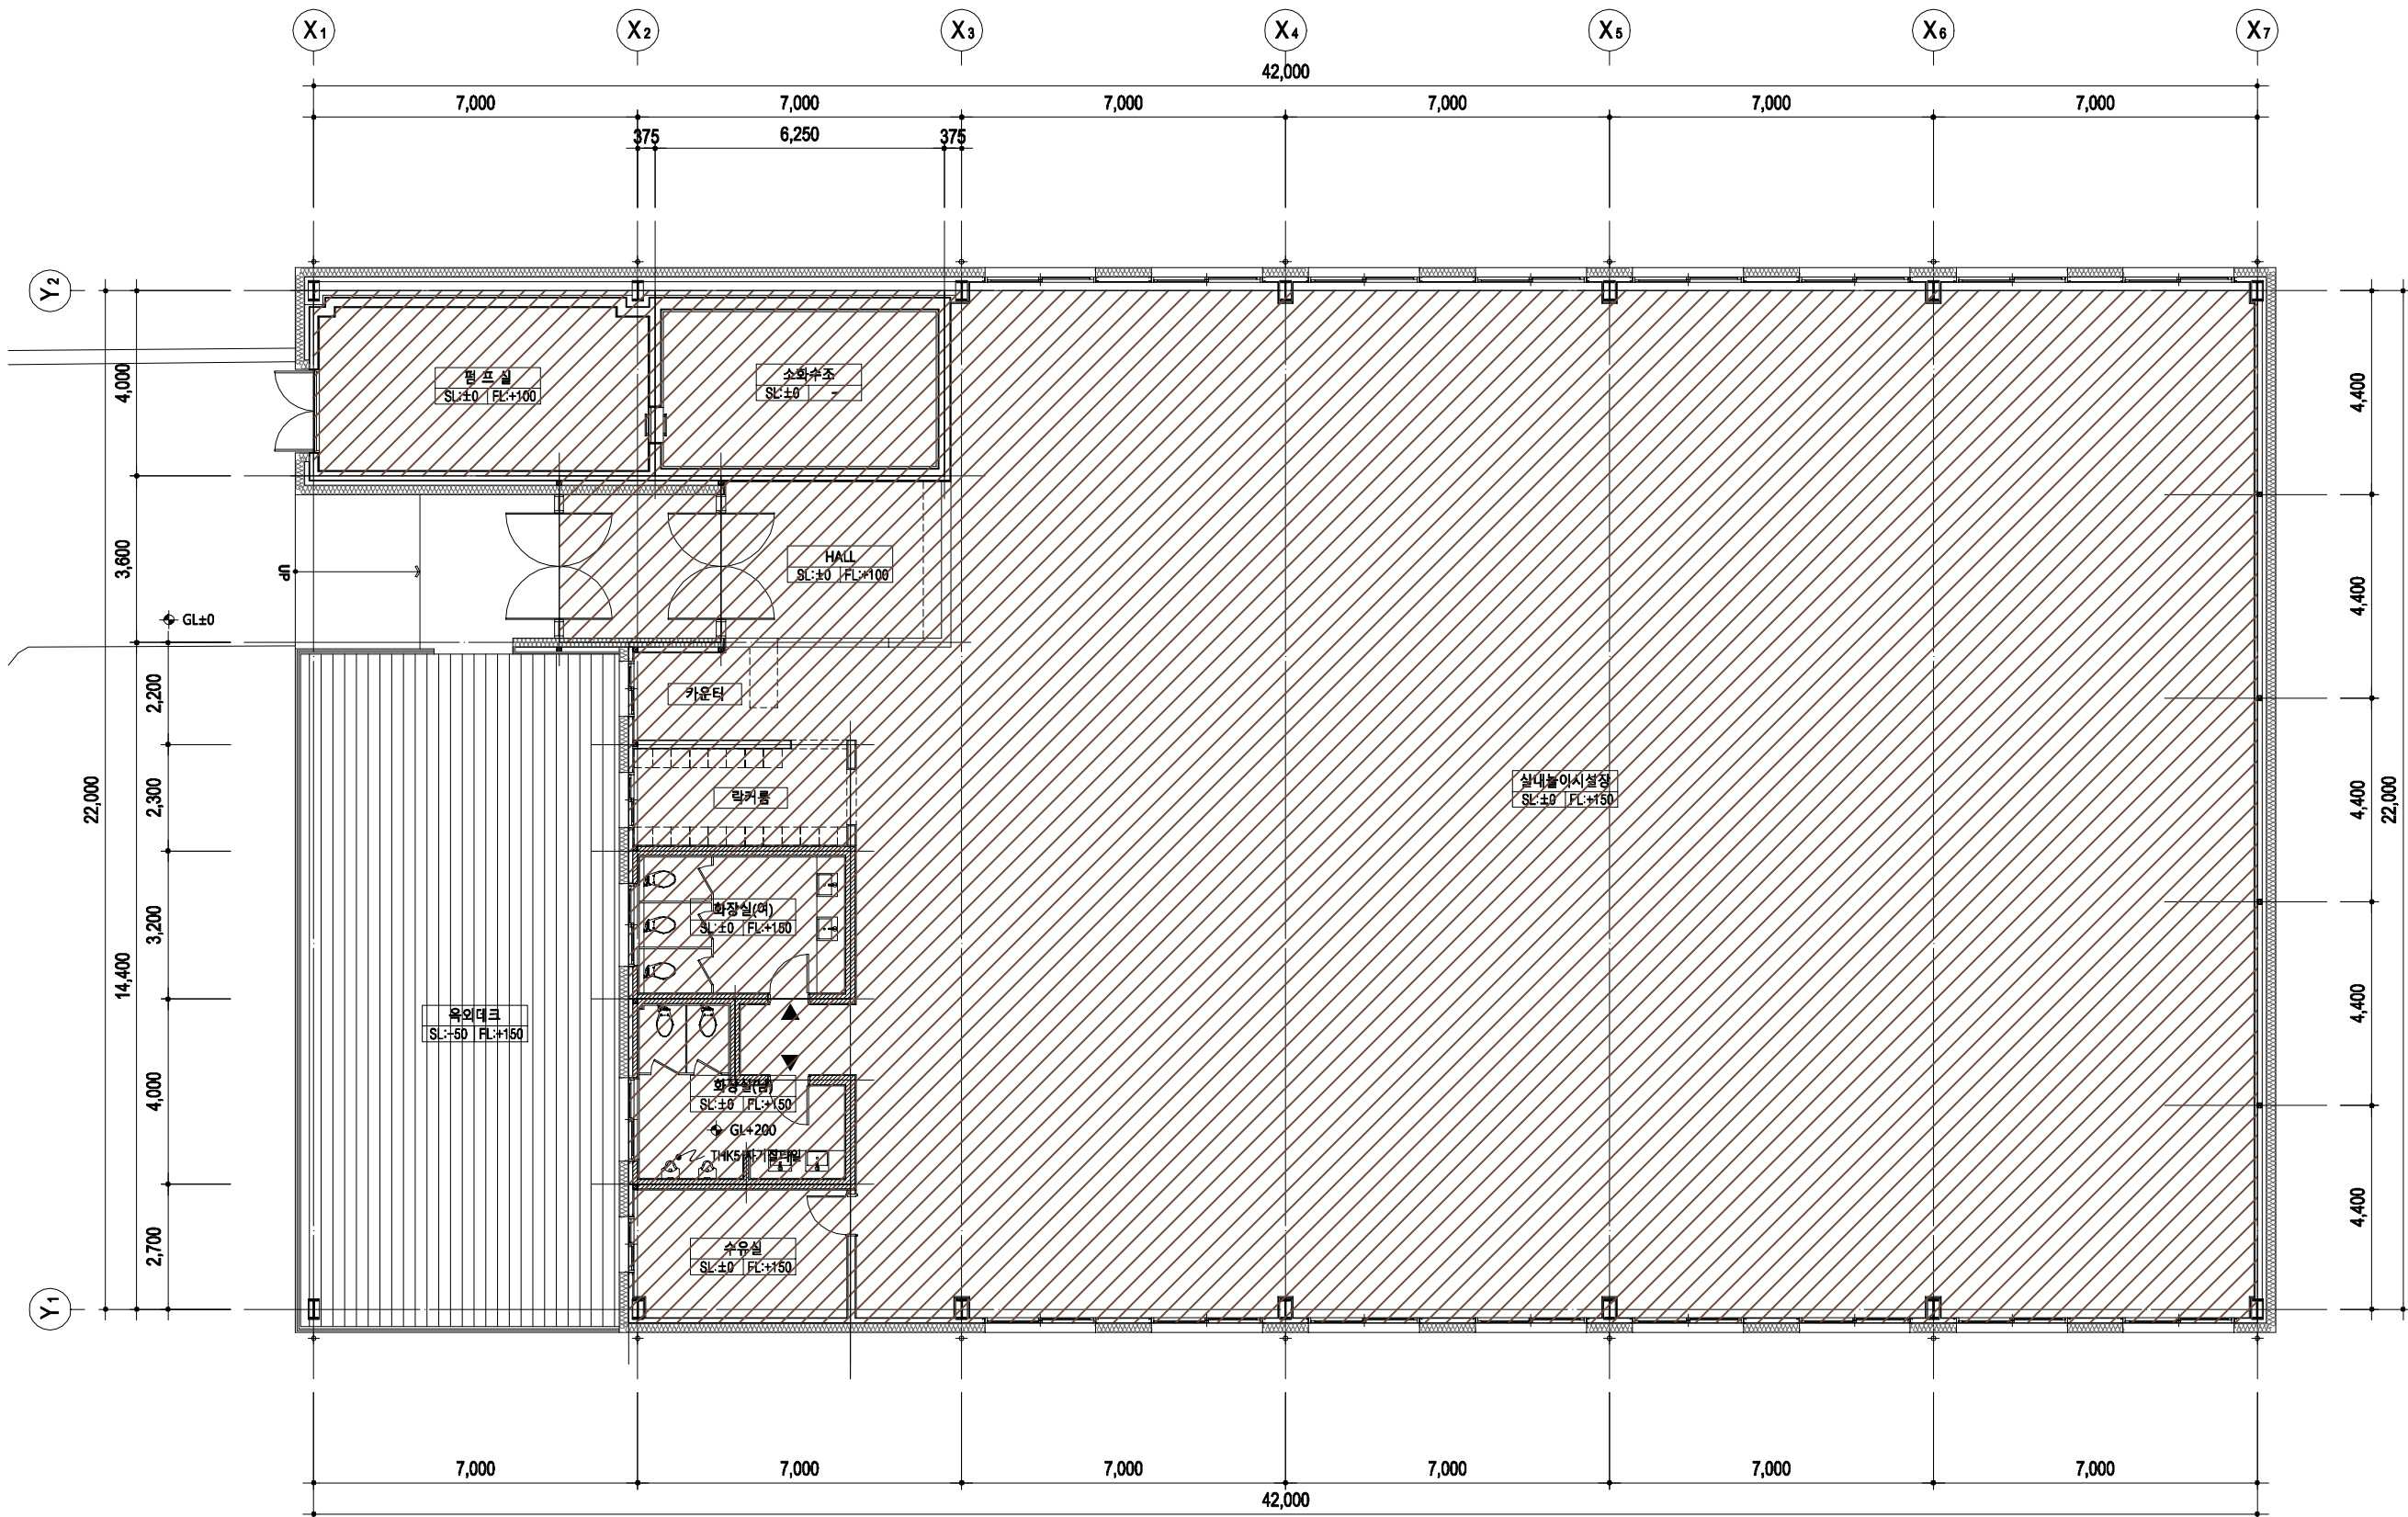

| 범례 | 면적(m²) |
|----|--------|
| F1 | 817.56 |
| R1 | -      |

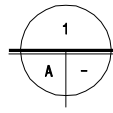

외피 전개도-2(바닥)

축척 A1:1/75, A3:1/150

PROJECT TITLE  
리틀 포레스트  
봄뜨락 조성사업

PROJECT NO

NOTE

KEY PLAN

DESIGN CORP.  
**이원** (주)이원건축사사무소  
ADD. 대구광역시 동구 장동로 81, 5F  
TEL. 053.716.0776 FAX. 0505.720.0776  
E-mail. e-ul2020@naver.com  
Web. eul2020 / 0776

APPROVED BY  
대표이사 / 건축사 권오섭

CHECKED BY


DRAWN BY

DATE  
2023. 04.

DRAWING TITLE  
외피 전개도-3 (지붕)


SCALE  
A3 : 1/ 150

DRAWING NO.  
A02-906

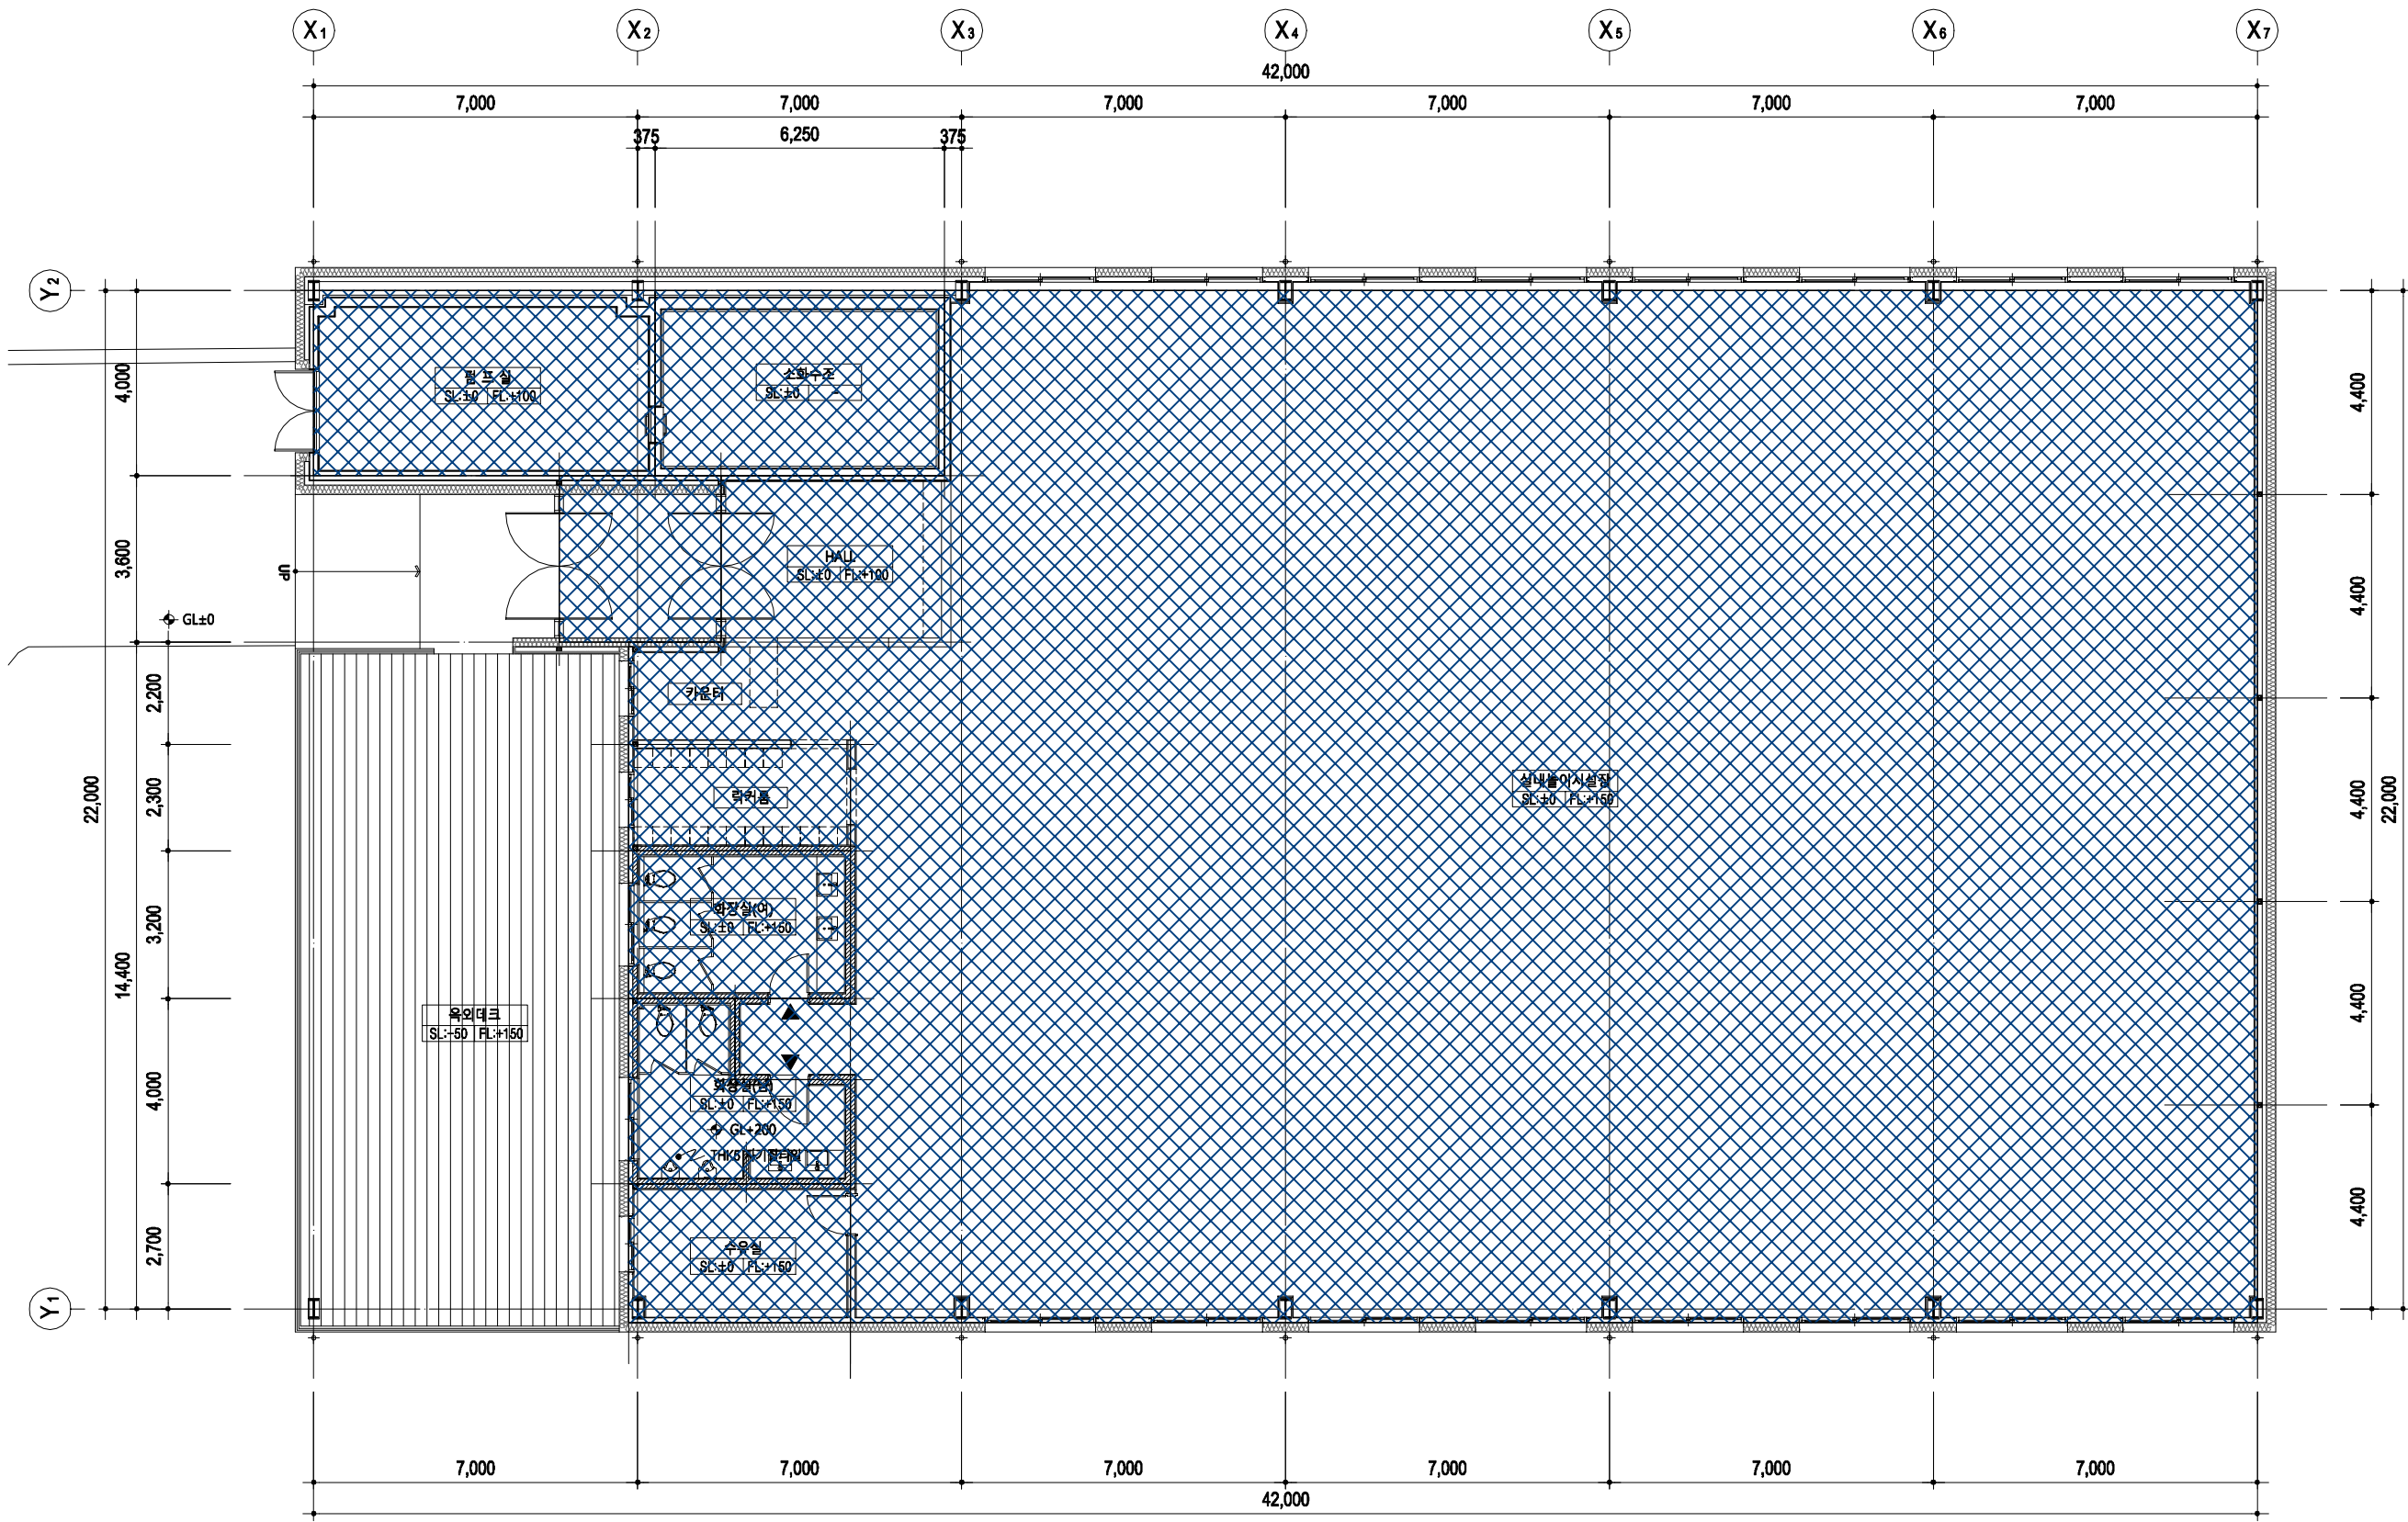


| 범례 | 면적(m²) |
|----|--------|
| F1 | -      |
| R1 | 825.74 |

경사지붕 면적반영

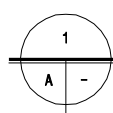


외피 전개도-3(지붕)

축척 A1:1/75, A3:1/150

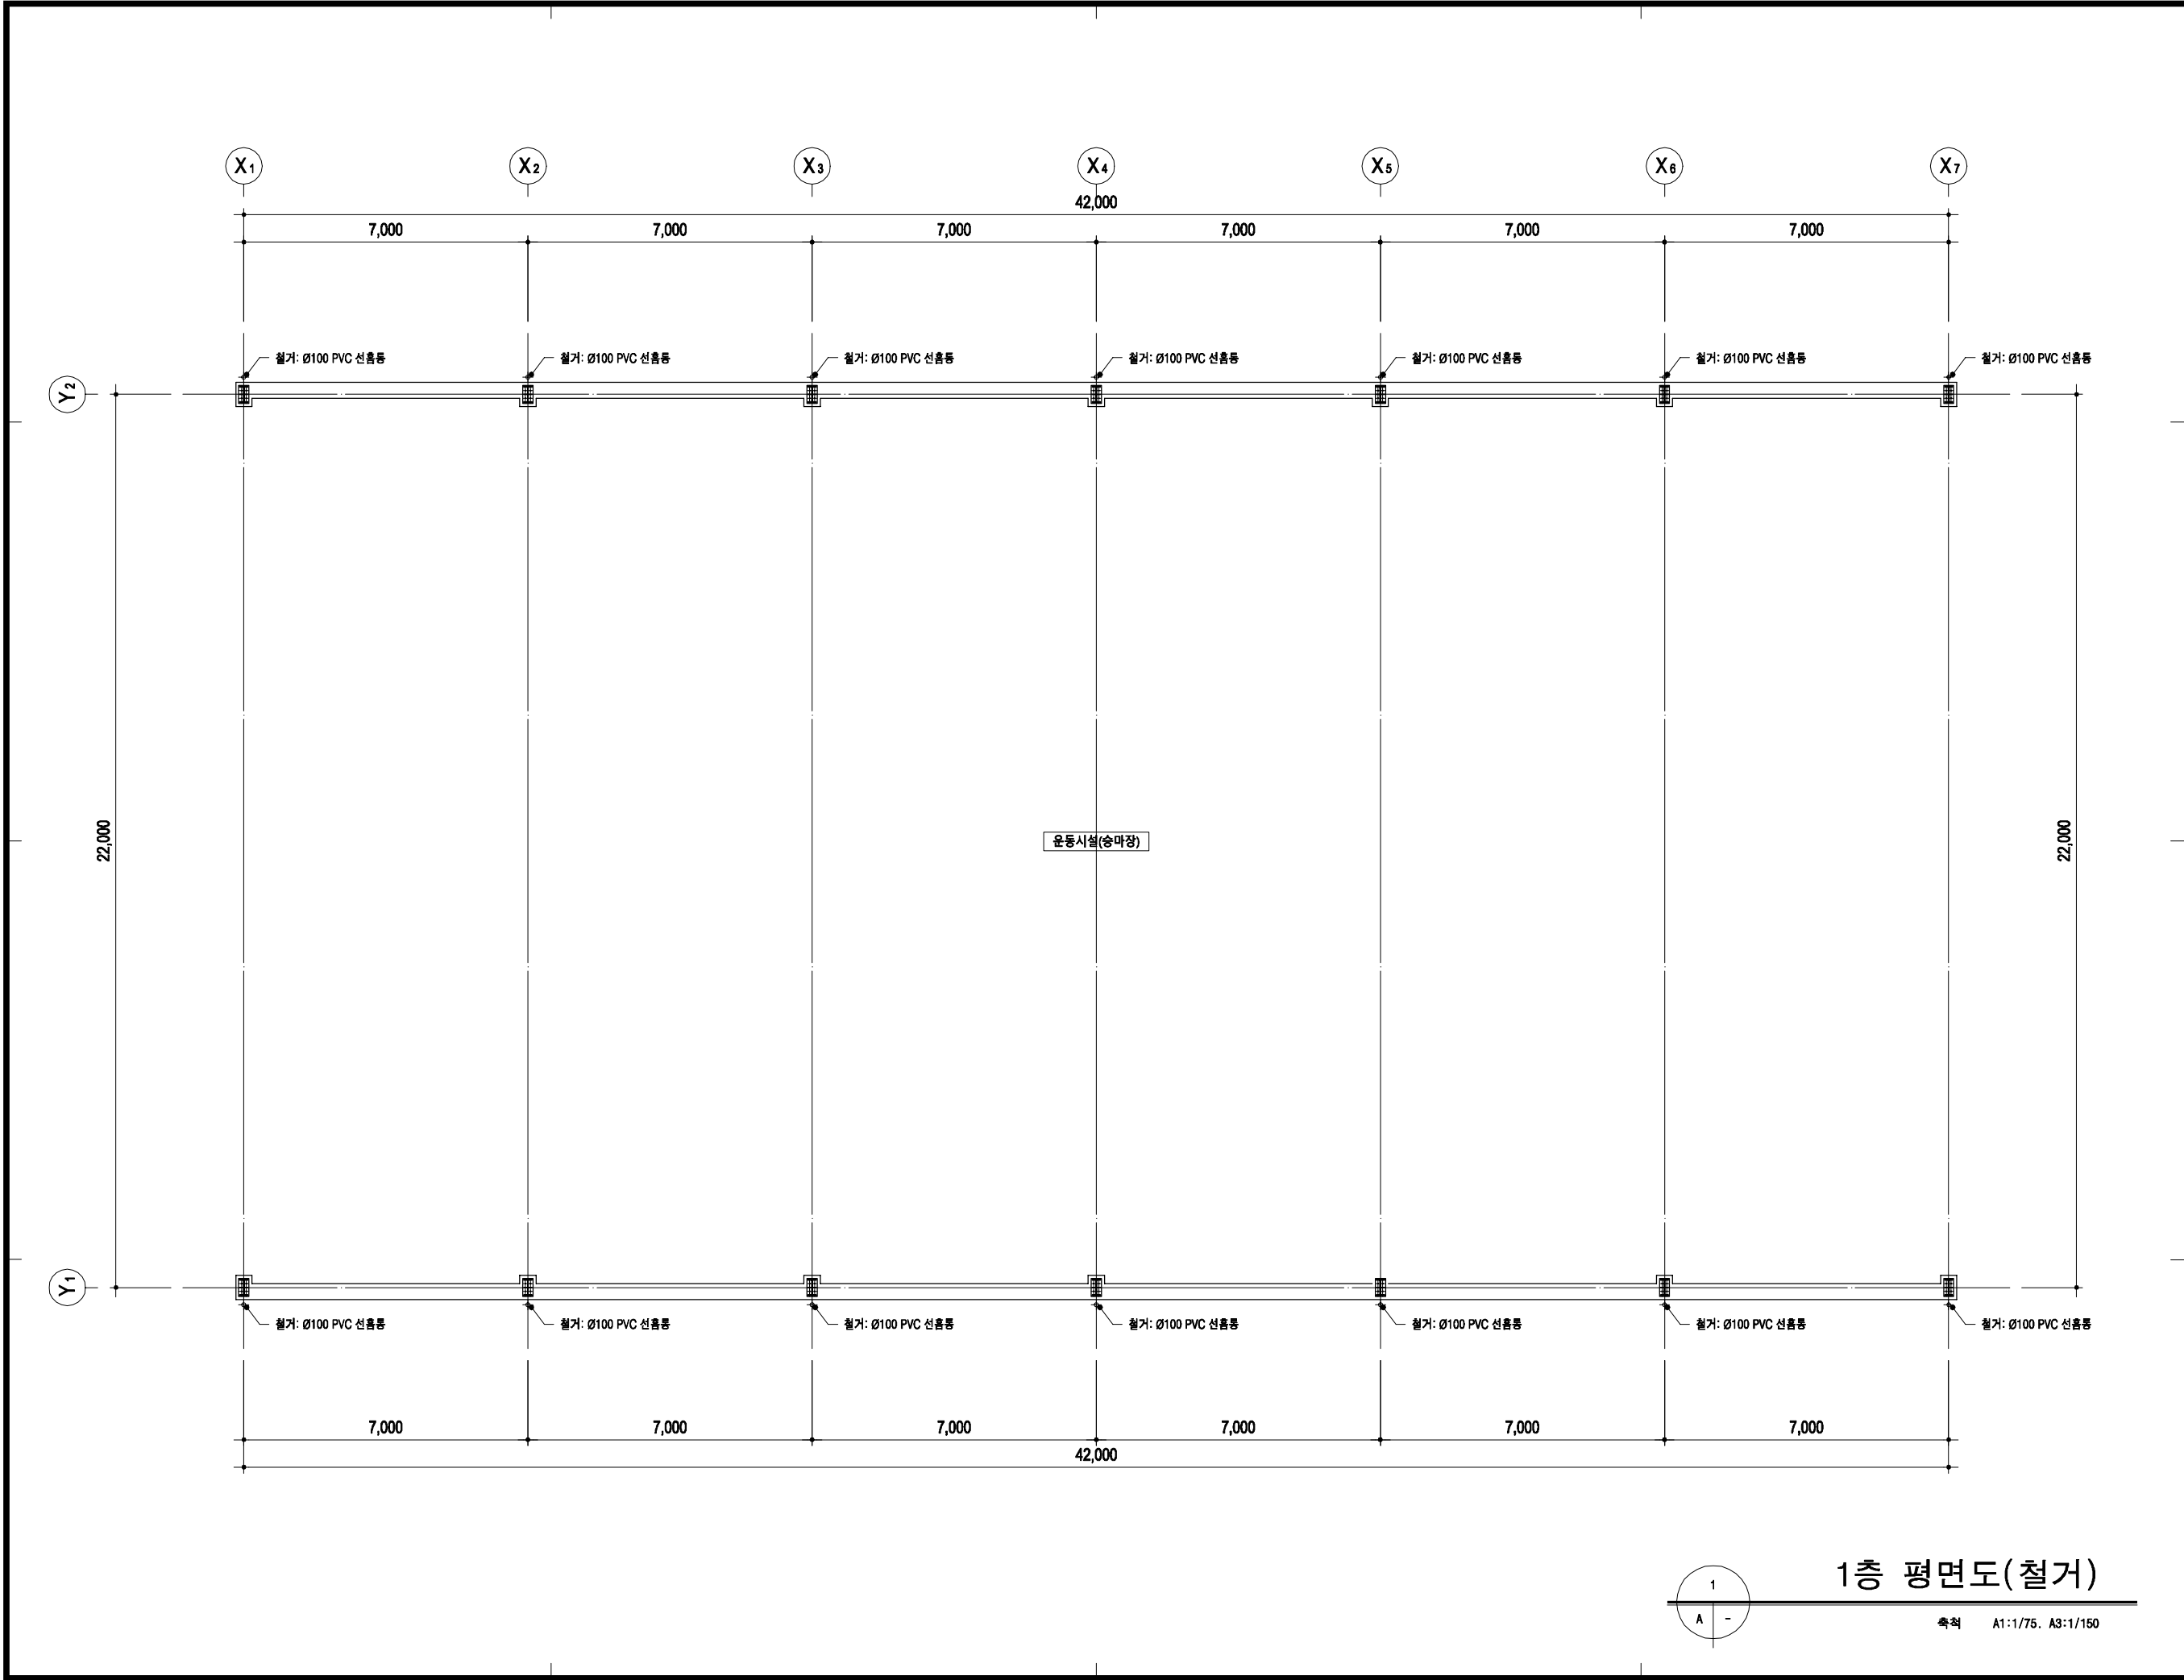


|               |   |
|---------------|---|
| PROJECT TITLE | 리틀 포레스트<br>봉뜨락 조성사업   |
| PROJECT NO    |   |
| NOTE          |   |
| KEY PLAN      |   |
| DESIGN CORP.  | <b>이음</b> (주)이음건축사사무소<br>ADD. 대구광역시 동구 장동로 81, 5F<br>TEL. 053.716.0776 FAX. 0505.720.0776<br>E-mail. e-ul2020@naver.com<br>Web. eul2020 / 0776 |
| APPROVED BY   | 대표이사/건축사 권오섭   |
| CHECKED BY    |   |
| DRAWN BY      |   |
| DATE          | 2023. 04.   |
| DRAWING TITLE | 1층 평면도(철거)   |
| SCALE         | A3 : 1/ 150   |
| DRAWING NO.   | A02- 1001   |

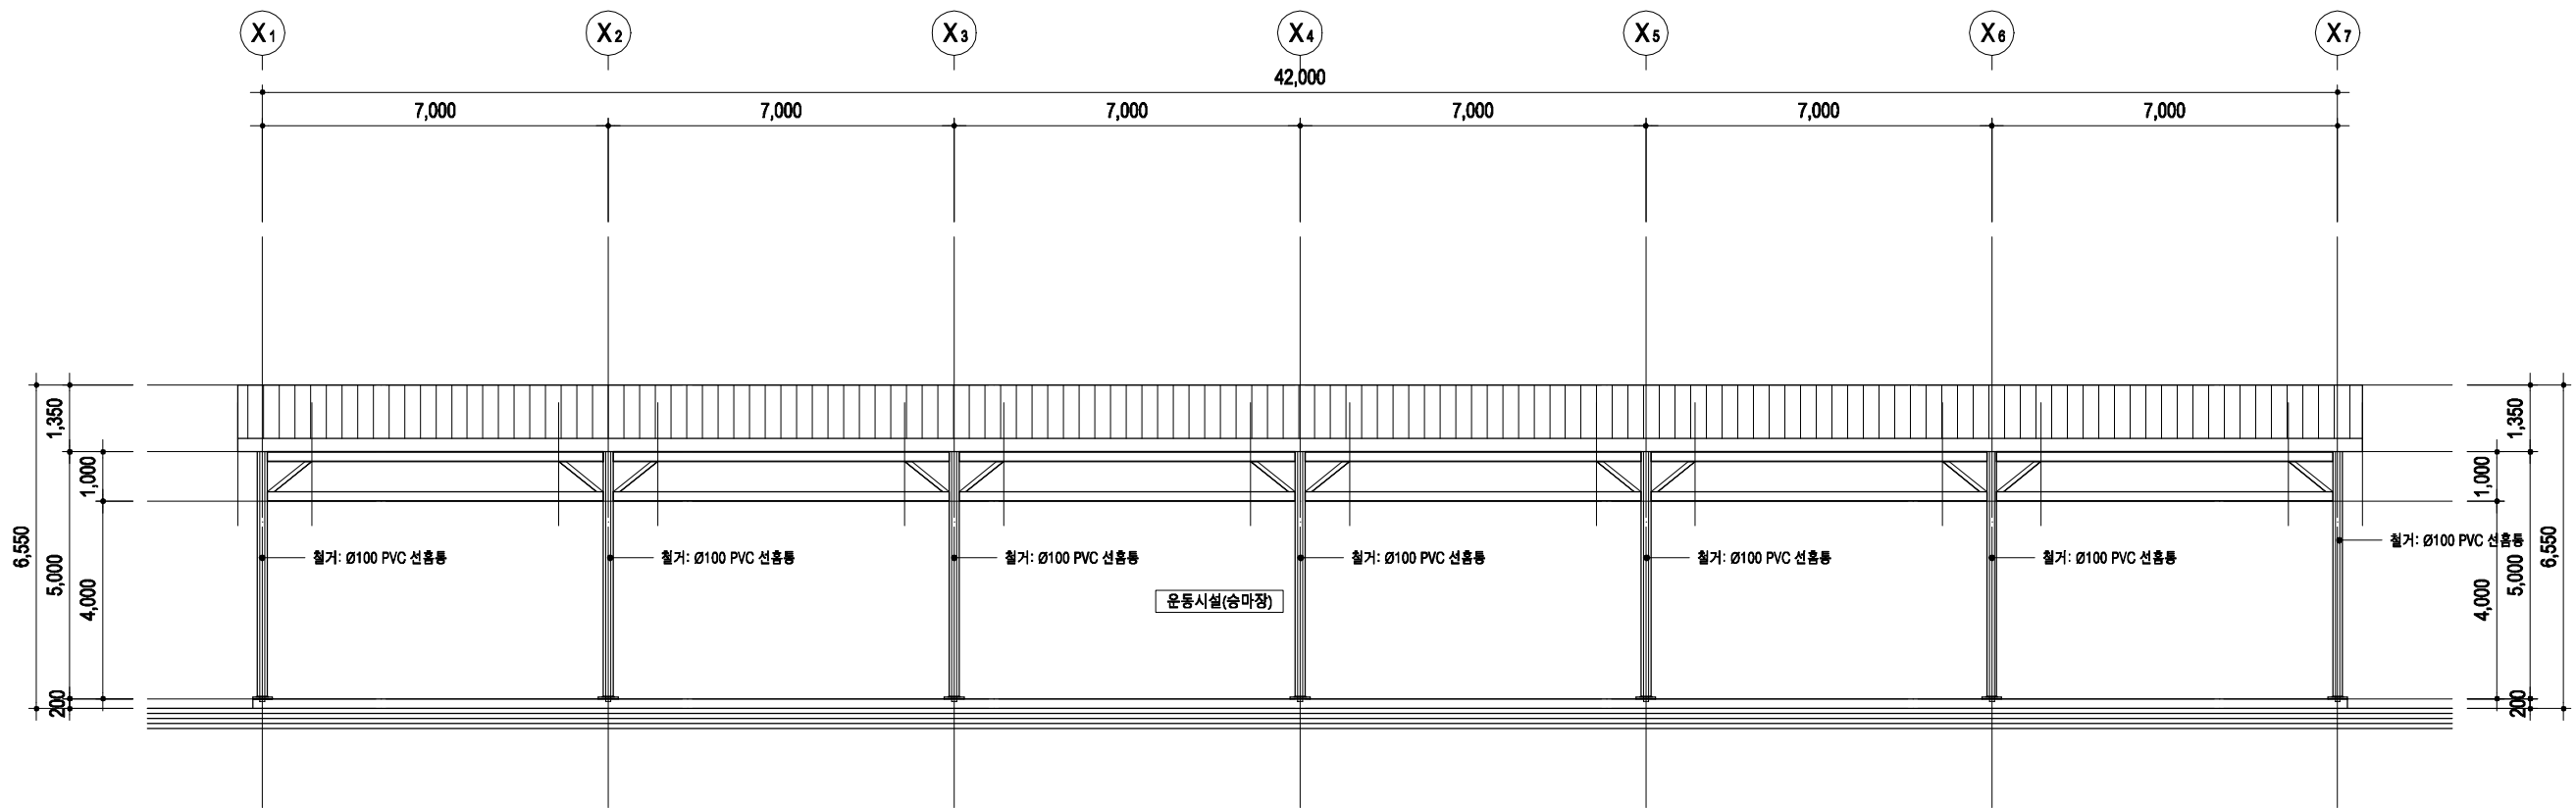

정면도(철거)

축척 A1:1/75, A3:1/150

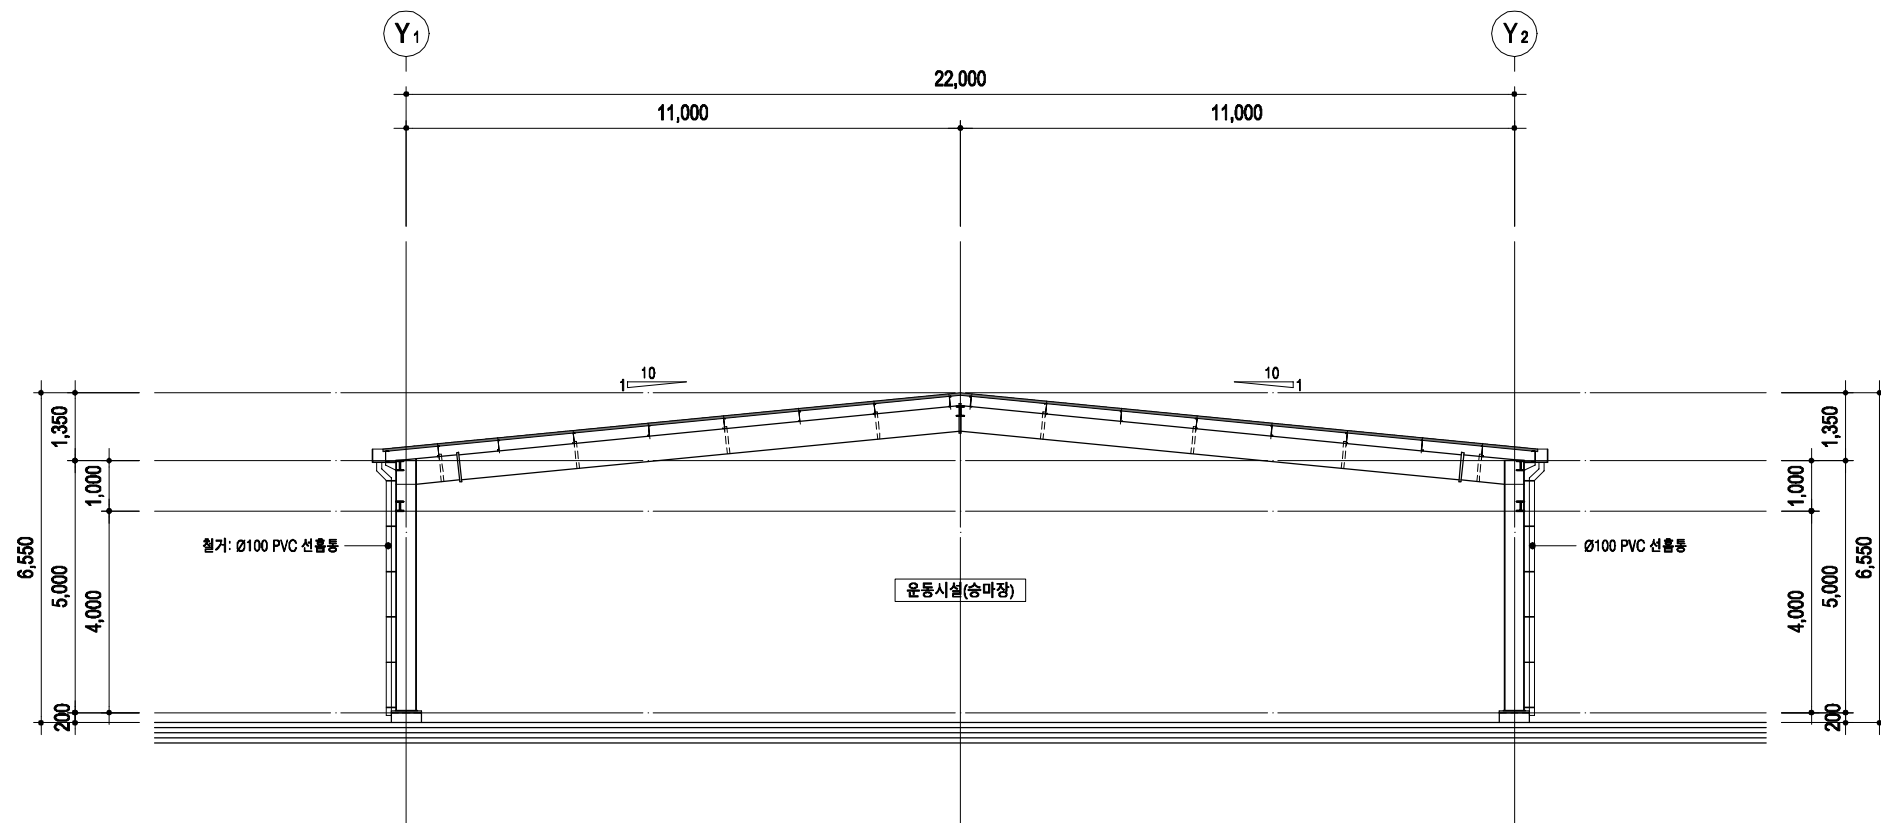

우측면도(철거)

축척 A1:1/75, A3:1/150

PROJECT TITLE  
리틀 포레스트  
봉뜨락 조성사업

PROJECT NO

NOTE

KEY PLAN

DESIGN CORP.  
**이음** (주)이음건축사사무소  
ADD. 대구광역시 동구 장동로 81, 5F  
TEL. 053.716.0776 FAX. 0505.720.0776  
E-mail. e-ul2020@naver.com  
Web. eul2020 / 0776

APPROVED BY  
대표이사 / 건축사 권오섭

CHECKED BY


DRAWN BY

DATE  
2023. 04.

DRAWING TITLE  
입면도-1  
(철거)


SCALE  
A3 : 1/ 150

DRAWING NO.  
A02- 1002

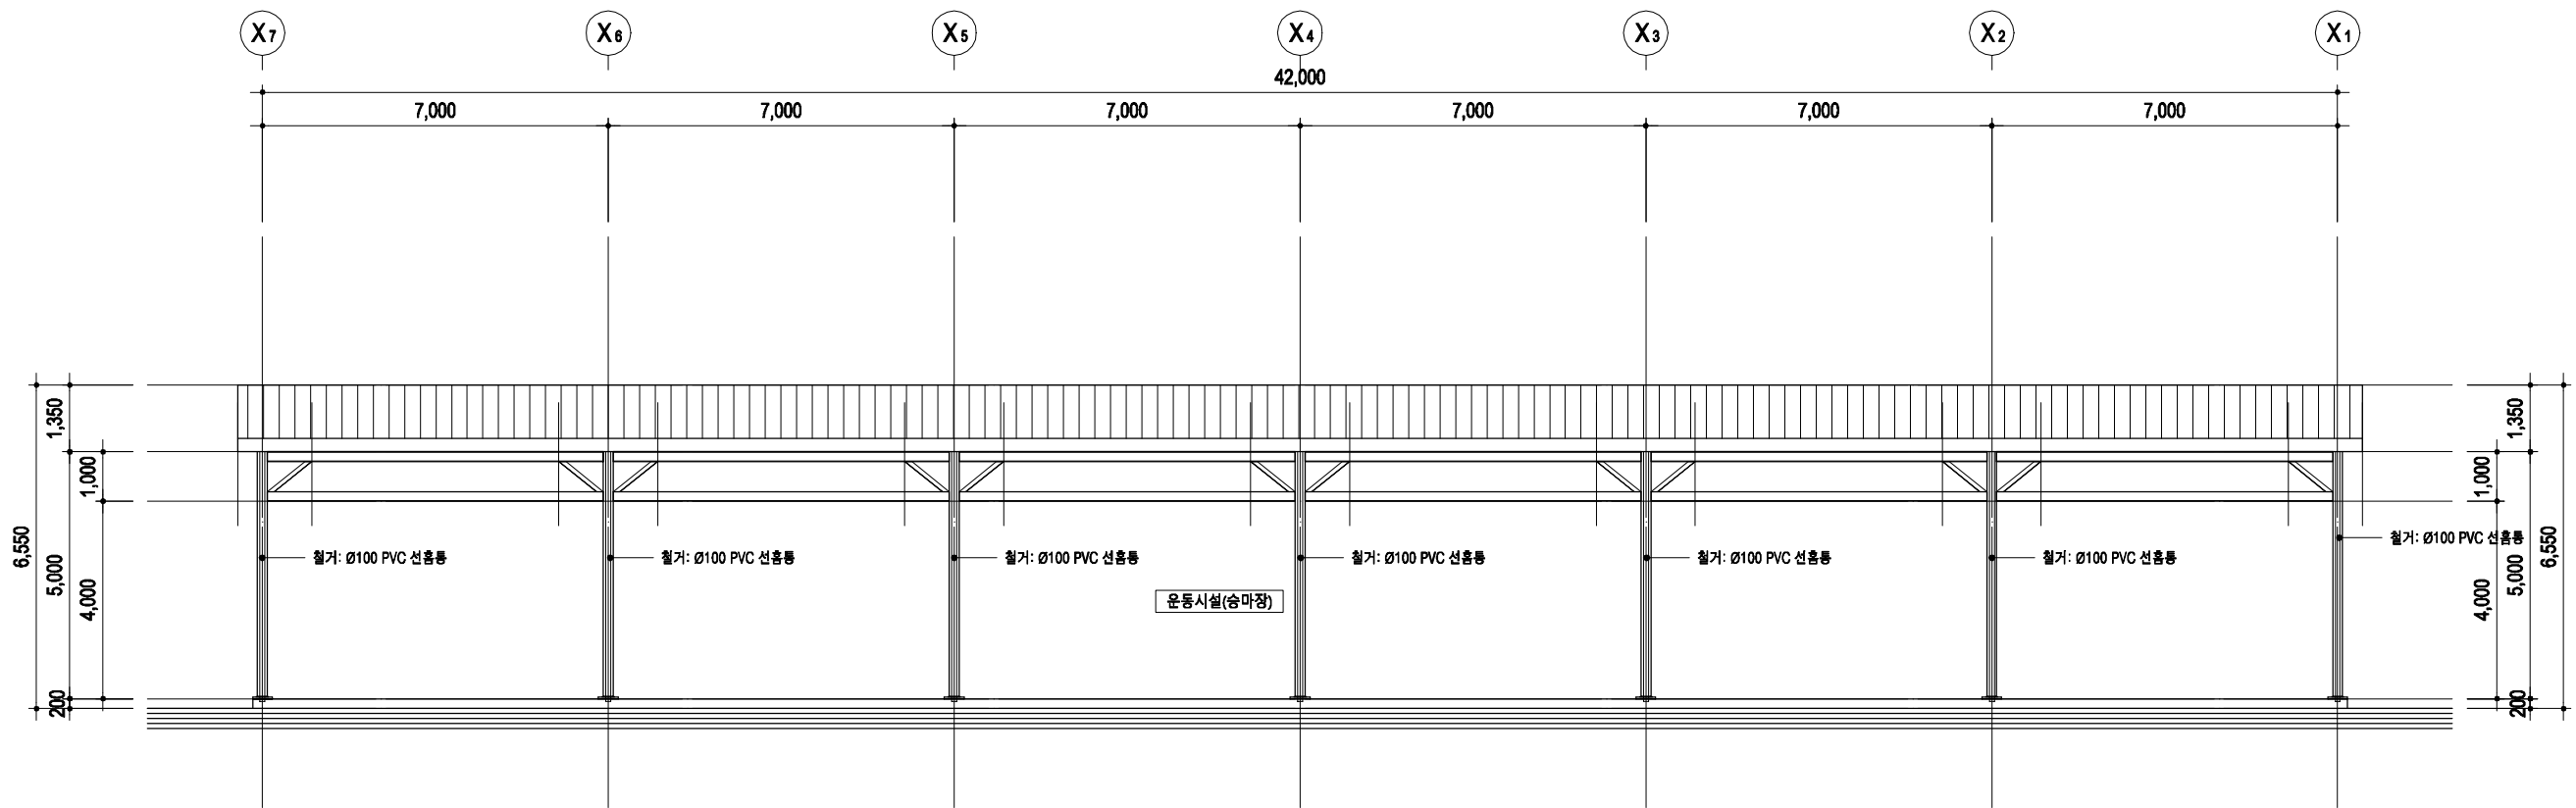

배면도(철거)

축척 A1:1/75, A3:1/150

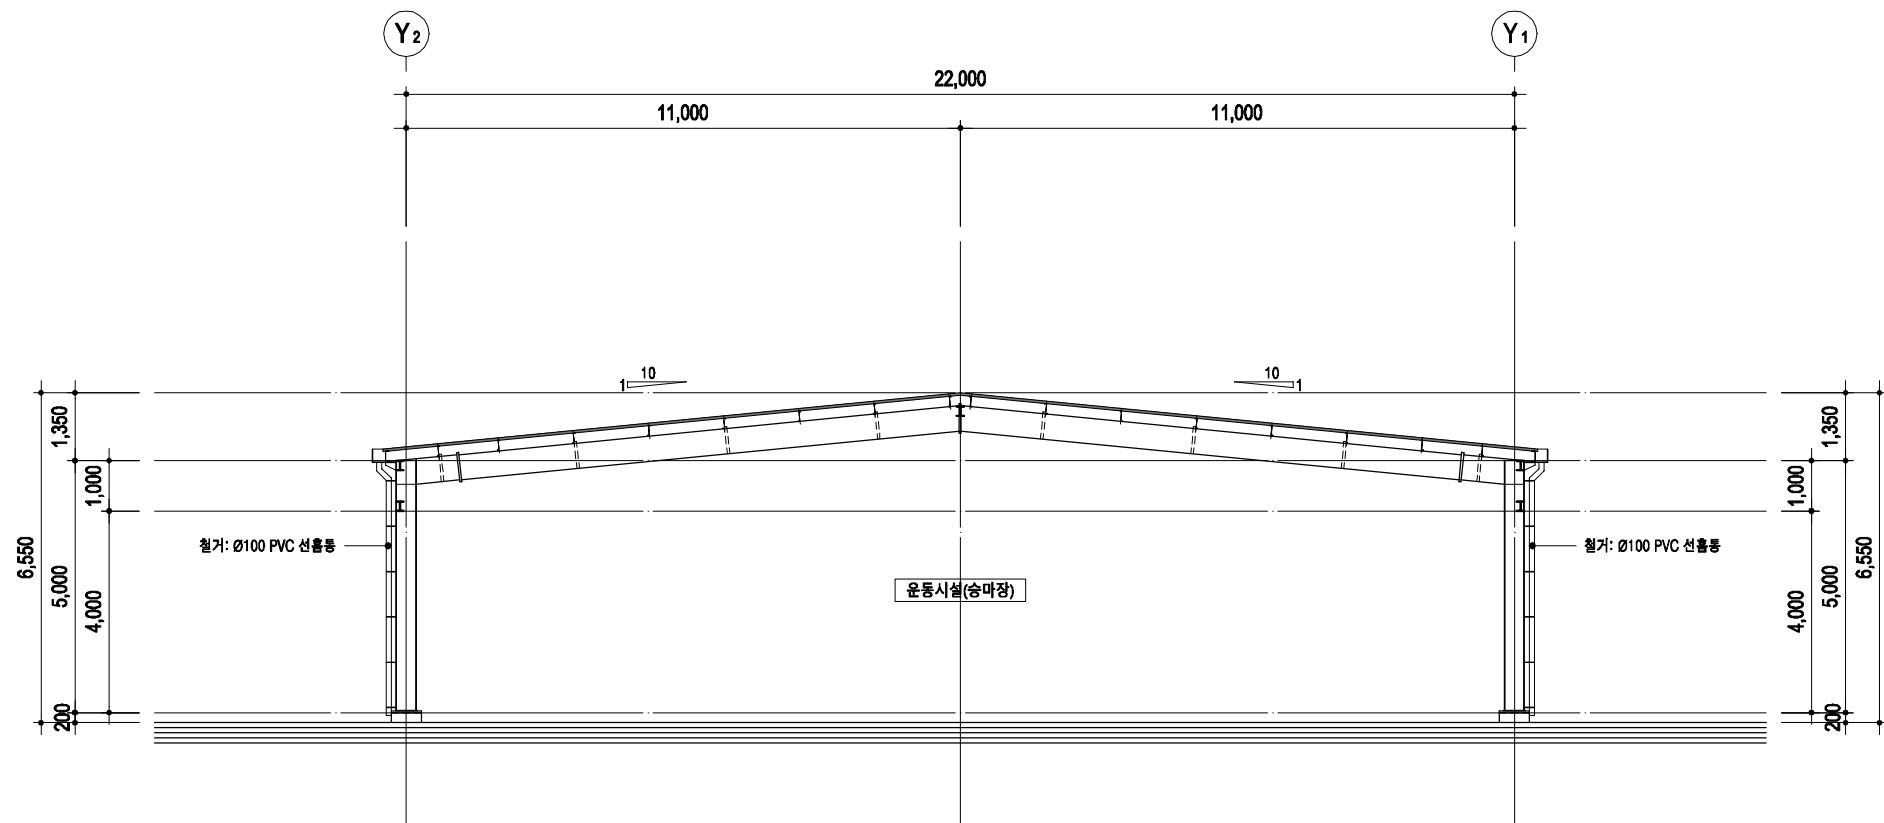

좌측면도(철거)

축척 A1:1/75, A3:1/150

PROJECT TITLE

리틀 포레스트  
봉뜨락 조성사업

PROJECT NO

NOTE

KEY PLAN

DESIGN CORP.

이음 (주)이음건축사사무소

ADD. 대구광역시 동구 장동로 81, 5F  
TEL. 053.716.0776 FAX. 0505.720.0776  
E-mail. e-ul2020@naver.com  
Web. eul2020 / 0776

APPROVED BY  
대표이사/건축사 권오섭

CHECKED BY

DRAWN BY

DATE 2023. 04.

DRAWING TITLE

입면도-2  
(철거)

SCALE A3 : 1/ 150

DRAWING NO. A02- 1003

PROJECT TITLE

리틀 포레스트  
봉뜨락 조성사업

PROJECT NO

NOTE

KEY PLAN

DESIGN CORP.

**이음** (주)이음건축사사무소

ADD. 대구광역시 동구 장동로 81, 5F  
TEL. 053.716.0776 FAX. 0505.720.0776  
E-mail. e-ul2020@naver.com  
Web. eul2020 / 0776

APPROVED BY  
대표이사/건축사 권오섭

CHECKED BY


DRAWN BY

DATE  
2023. 04.

DRAWING TITLE  
기초 구조평면도

SCALE  
A3 : 1/ 150

DRAWING NO.  
S01- 101

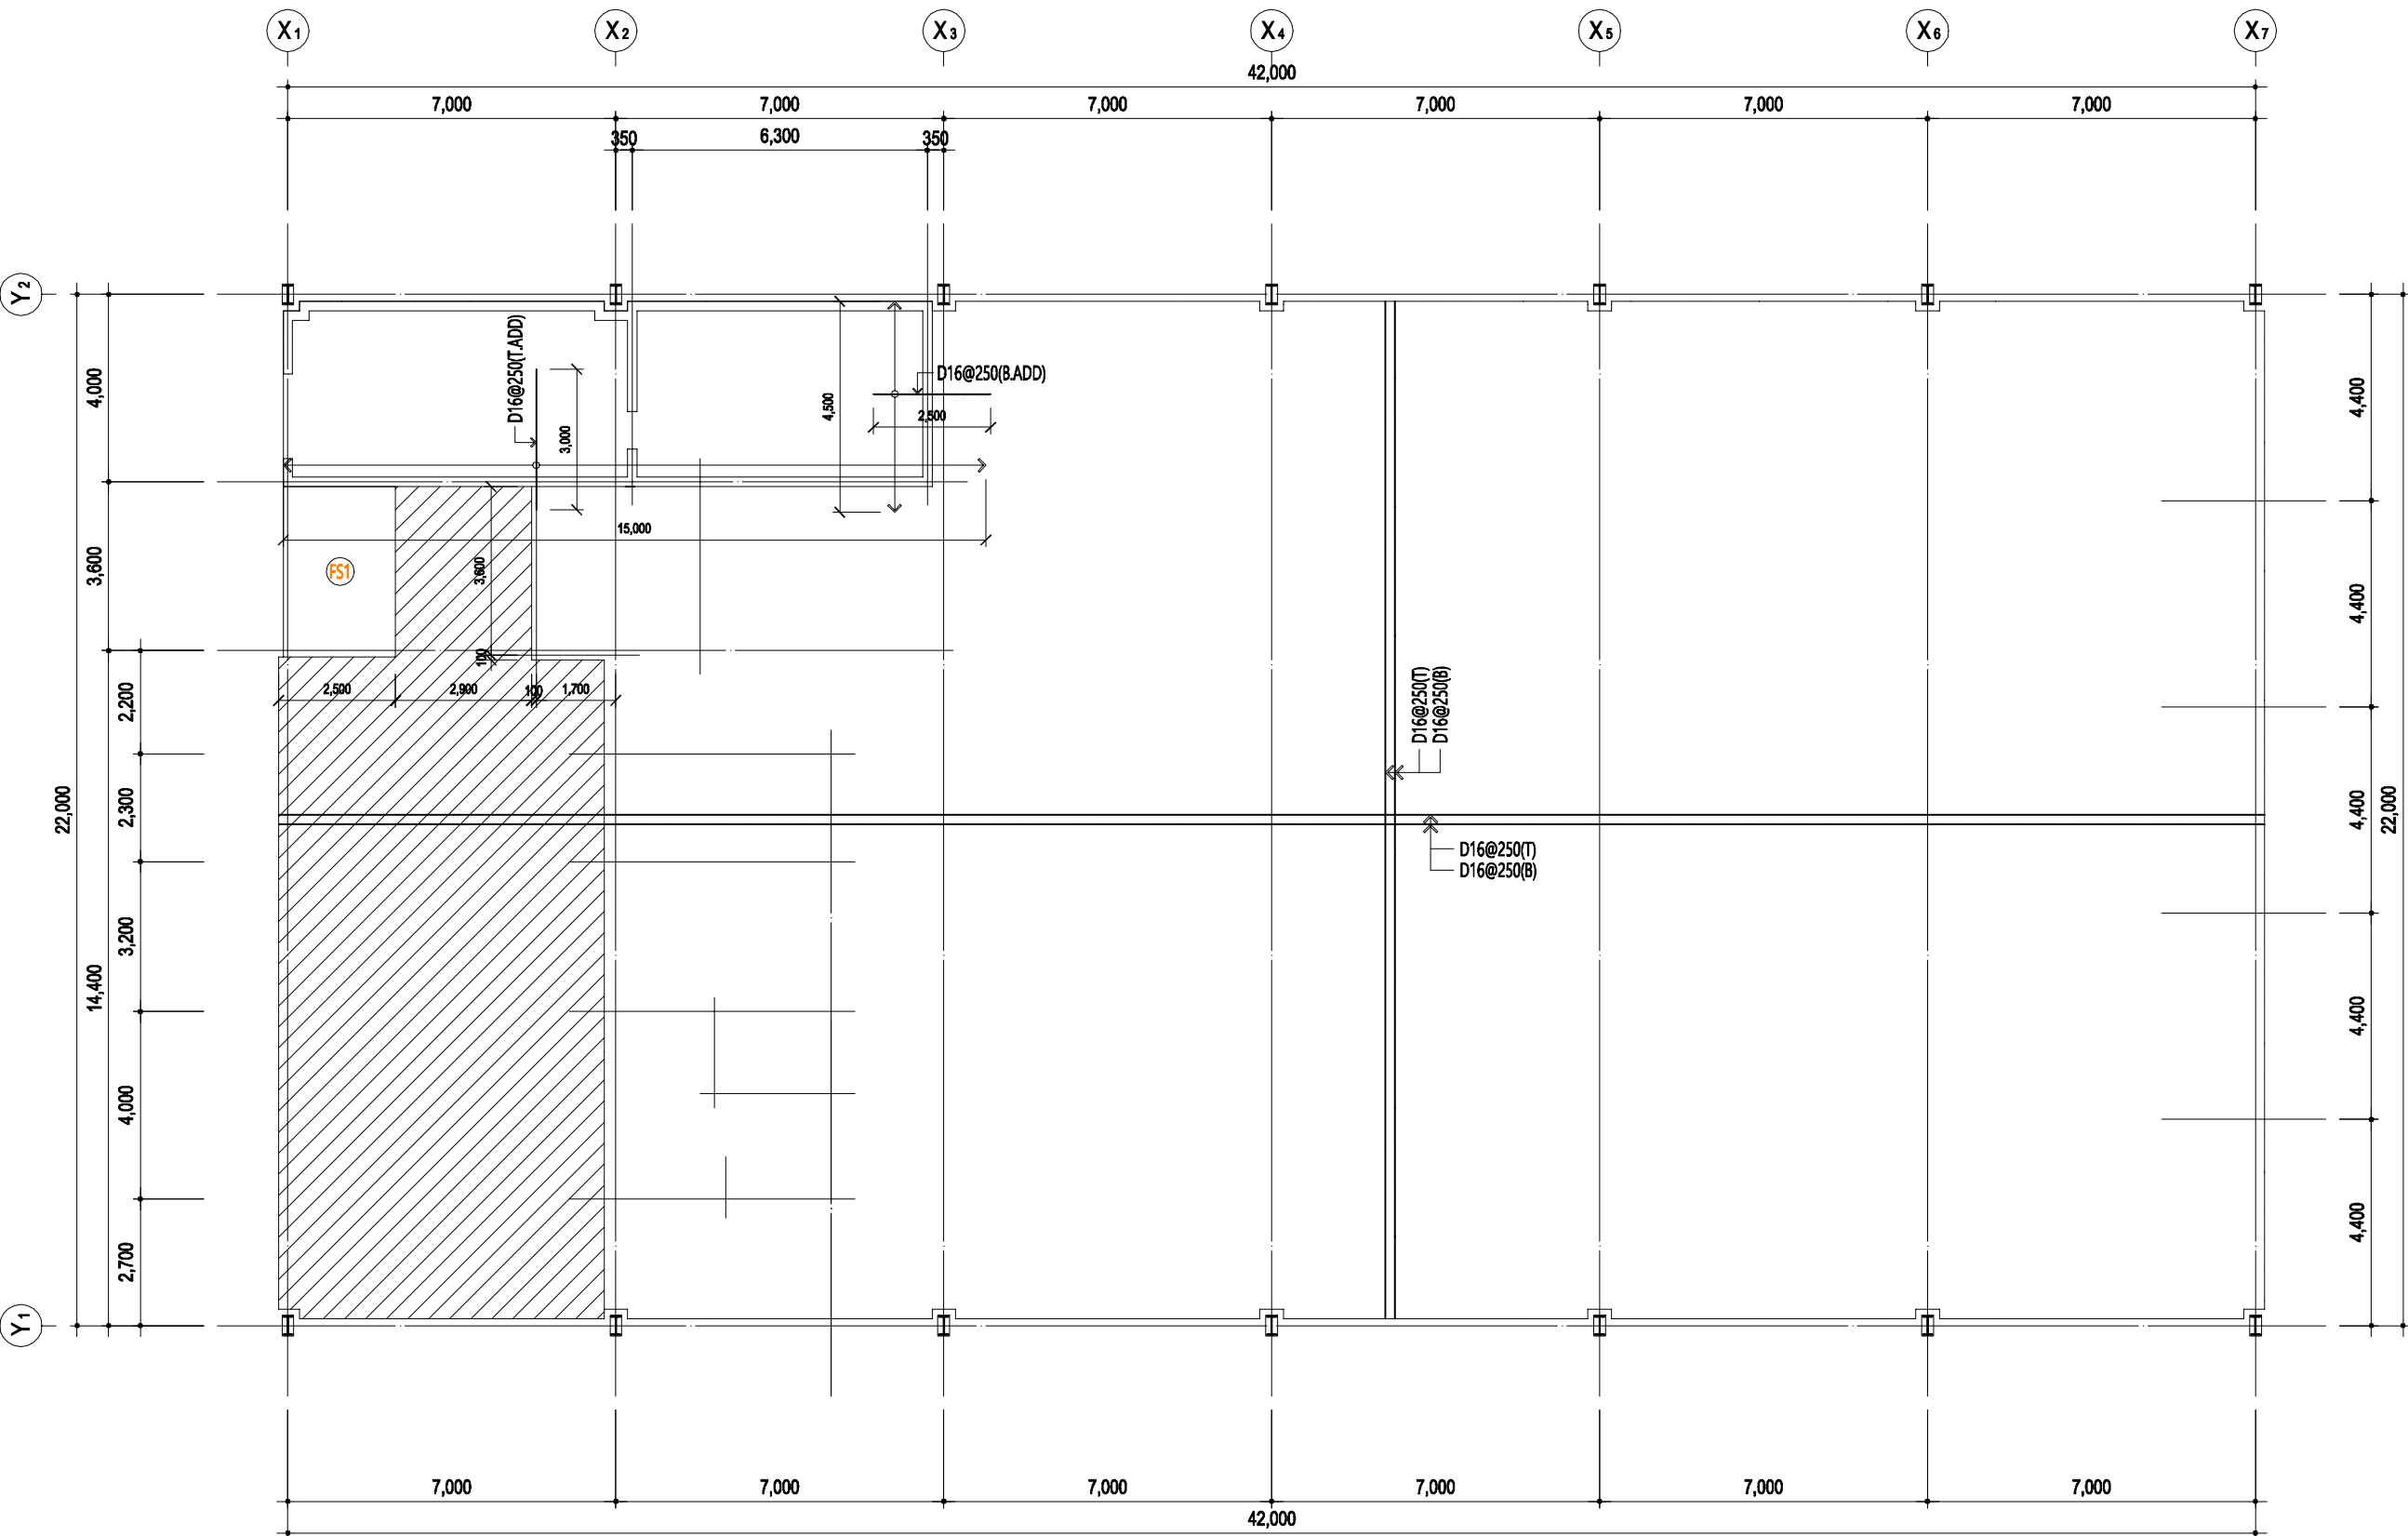

\*\*\* NOTE \*\*\*


\* fck = 27MPa

\* fy = 400MPa

\* MAT THK = 400mm


▨ = 350mm

\* 지반의 허용 지내력 = 100kN/m²

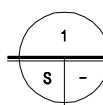


기초 구조평면도

축척 A1:1/75, A3:1/150

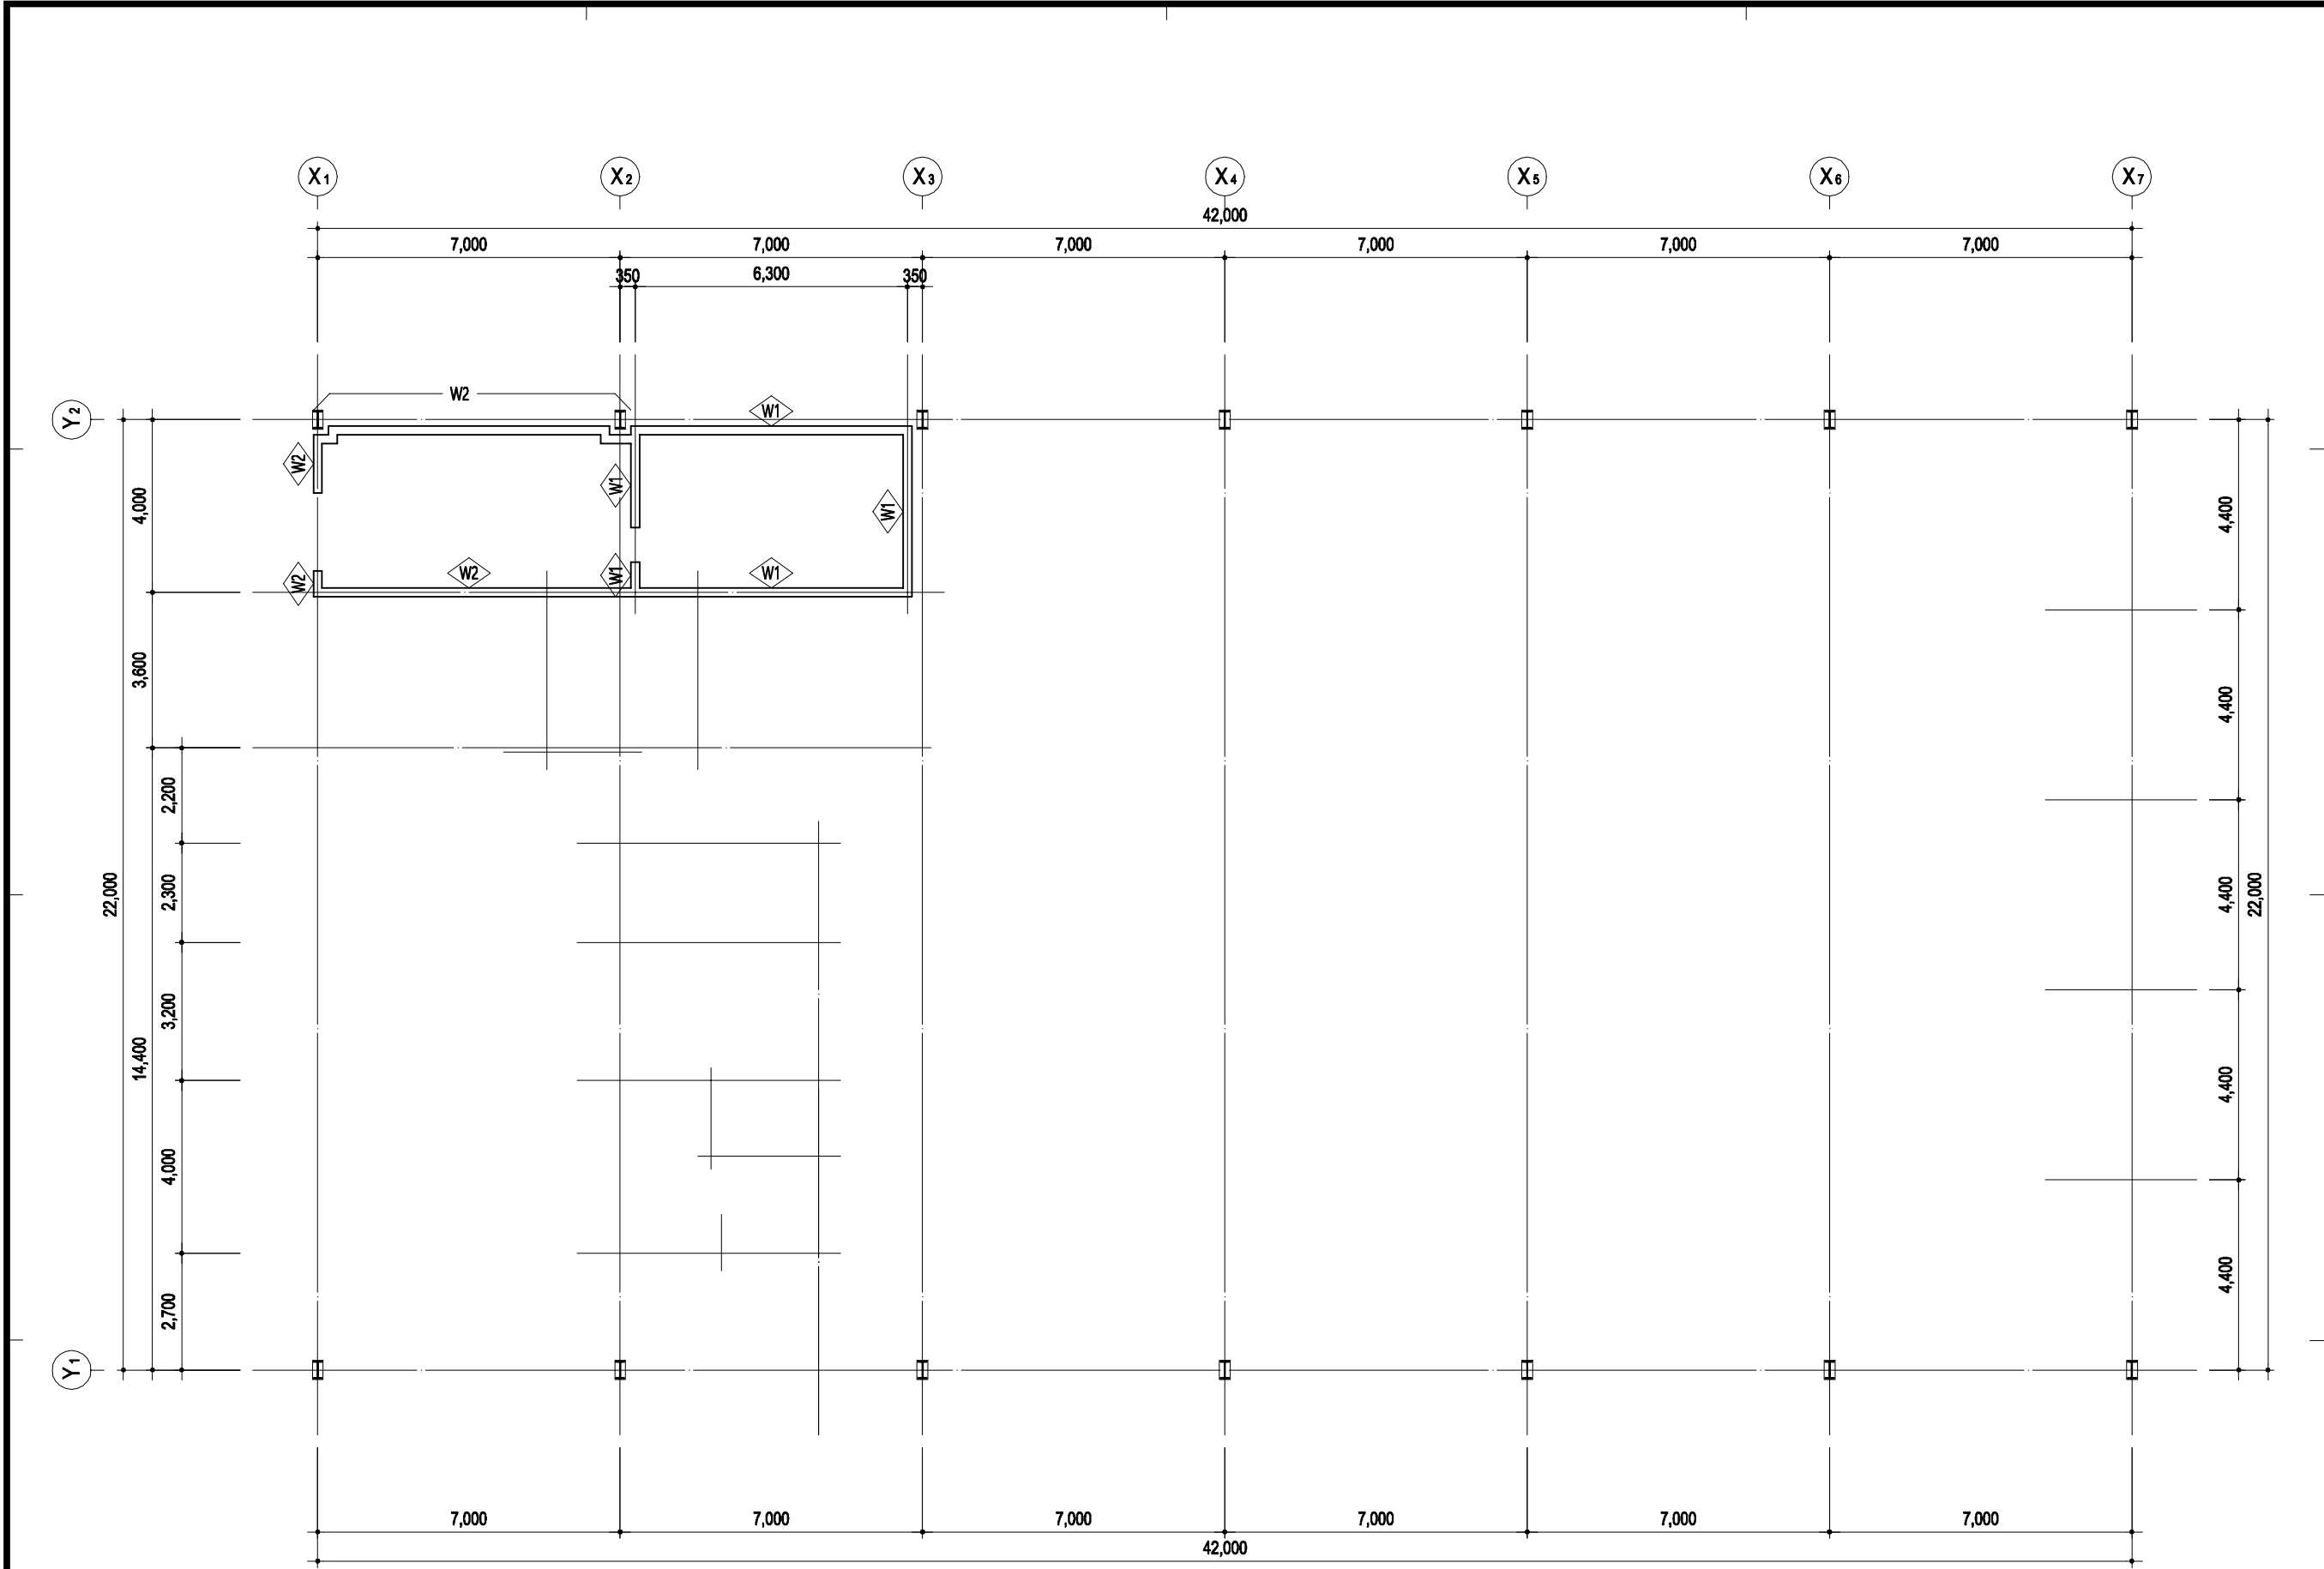



\*\*\* NOTE \*\*\*  
\* fck = 30MPa  
\* fy = 400MPa

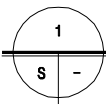


1층 구조평면도

축척 A1:1/75, A3:1/150

|               |   |
|---------------|---|
| PROJECT TITLE | 리틀 포레스트<br>봉뜨락 조성사업   |
| PROJECT NO    |   |
| NOTE          |   |
| KEY PLAN      |   |
| DESIGN CORP.  | <b>이음</b> (주)이음건축사사무소<br>ADD. 대구광역시 중구 장동로 81, 5F<br>TEL. 053.716.0776 FAX. 0505.720.0776<br>E-mail. e-ul2020@naver.com<br>Web. eul2020 / 0776 |
| APPROVED BY   | 대표이사 / 건축사 권오섭   |
| CHECKED BY    |   |
| DRAWN BY      |   |
| DATE          | 2023. 04.   |
| DRAWING TITLE | 1층 구조평면도   |
| SCALE         | A3 : 1/ 150   |
| DRAWING NO.   | S01- 102   |

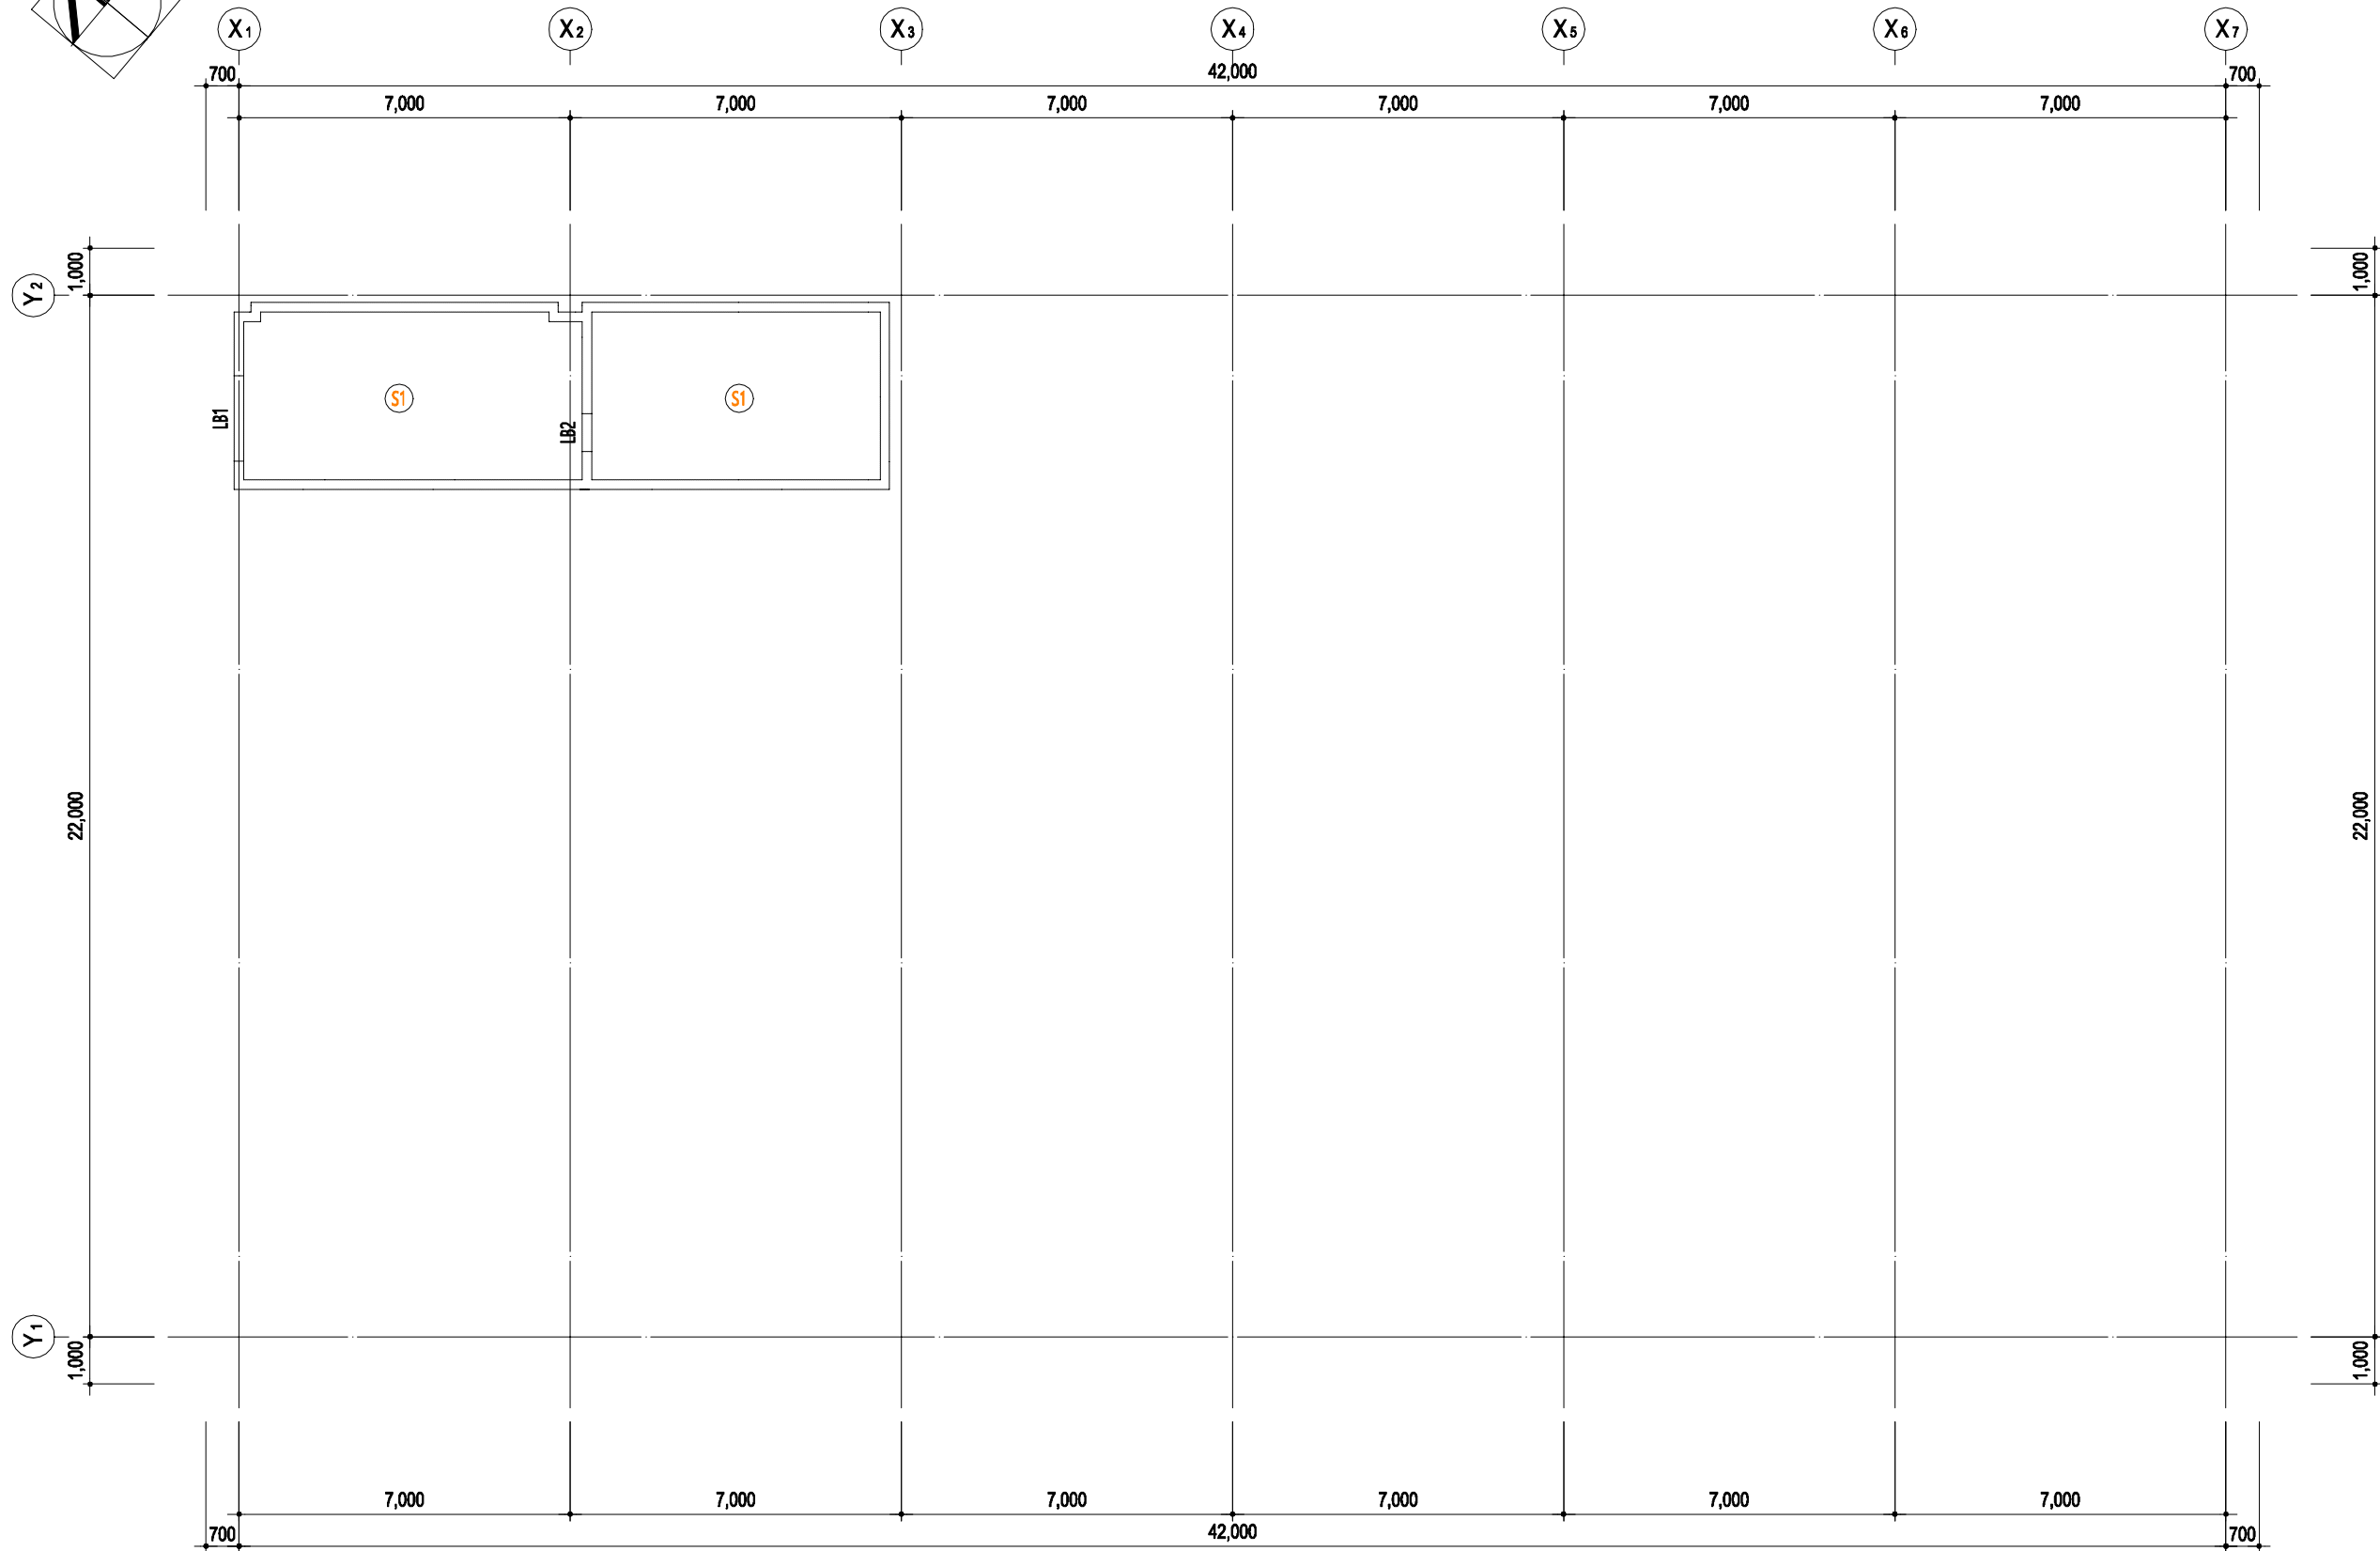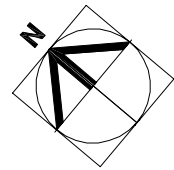

\*\*\* NOTE \*\*\*  
\* fck = 30MPa  
\* fy = 400MPa

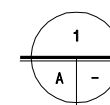

지붕 구조평면도

축척 A1:1/75, A3:1/150

PROJECT TITLE

리틀 포레스트  
봉뜨락 조성사업

PROJECT NO

NOTE

KEY PLAN

DESIGN CORP.



ADD. 대구광역시 동구 장동로 81, 5F  
TEL. 053.716.0776 FAX. 0505.720.0776  
E-mail. e-ul2020@naver.com  
Web. eul2020 / 0776

APPROVED BY  
대표이사 / 건축사 권오섭

CHECKED BY

DRAWN BY


DATE 2023. 04.

DRAWING TITLE

지붕 구조평면도



SCALE A3 : 1/ 150

DRAWING NO. S01- 103

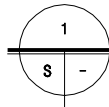

보 일람표

축척 A1:1/30, A3:1/60
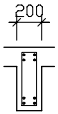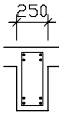
| 부 호      | LB1                                                                               |  | LB2                                                                                 |  |  |  |  |  |  |  |
|----------|-----------------------------------------------------------------------------------|--|-------------------------------------------------------------------------------------|--|--|--|--|--|--|--|
| 위 치      | ALL                                                                               |  | ALL                                                                                 |  |  |  |  |  |  |  |
| 형 태      |  |  |  |  |  |  |  |  |  |  |
| TOP BAR  | 4-D13                                                                             |  | 4-D13                                                                               |  |  |  |  |  |  |  |
| BOT BAR  | 4-D13                                                                             |  | 4-D13                                                                               |  |  |  |  |  |  |  |
| STIRRUP  | D10@200                                                                           |  | D10@200                                                                             |  |  |  |  |  |  |  |
| SKIN BAR | -                                                                                 |  | -                                                                                   |  |  |  |  |  |  |  |

PROJECT TITLE

리틀 포레스트  
봉뜨락 조성사업

PROJECT NO

NOTE

\* fck = 30 MPa

\* fy = 400 MPa

KEY PLAN

DESIGN CORP.



ADD. 대구광역시 동구 장동로 81, 5F  
TEL. 053.716.0776 FAX. 0505.720.0776  
E-mail. e-ul2020@naver.com  
Web. eul2020 / 0776

APPROVED BY

대 표 이 사 / 건 축 사 권 오 섭

CHECKED BY

DRAWN BY

DATE

2023. 04.

DRAWING TITLE


보 일람표

SCALE

A3 : 1/ 60


DRAWING NO.

S02- 101

 


DRAWING NO. S02- 102

[illegible]

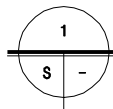

벽체 배근도

축척 A1:1/15, A3:1/30

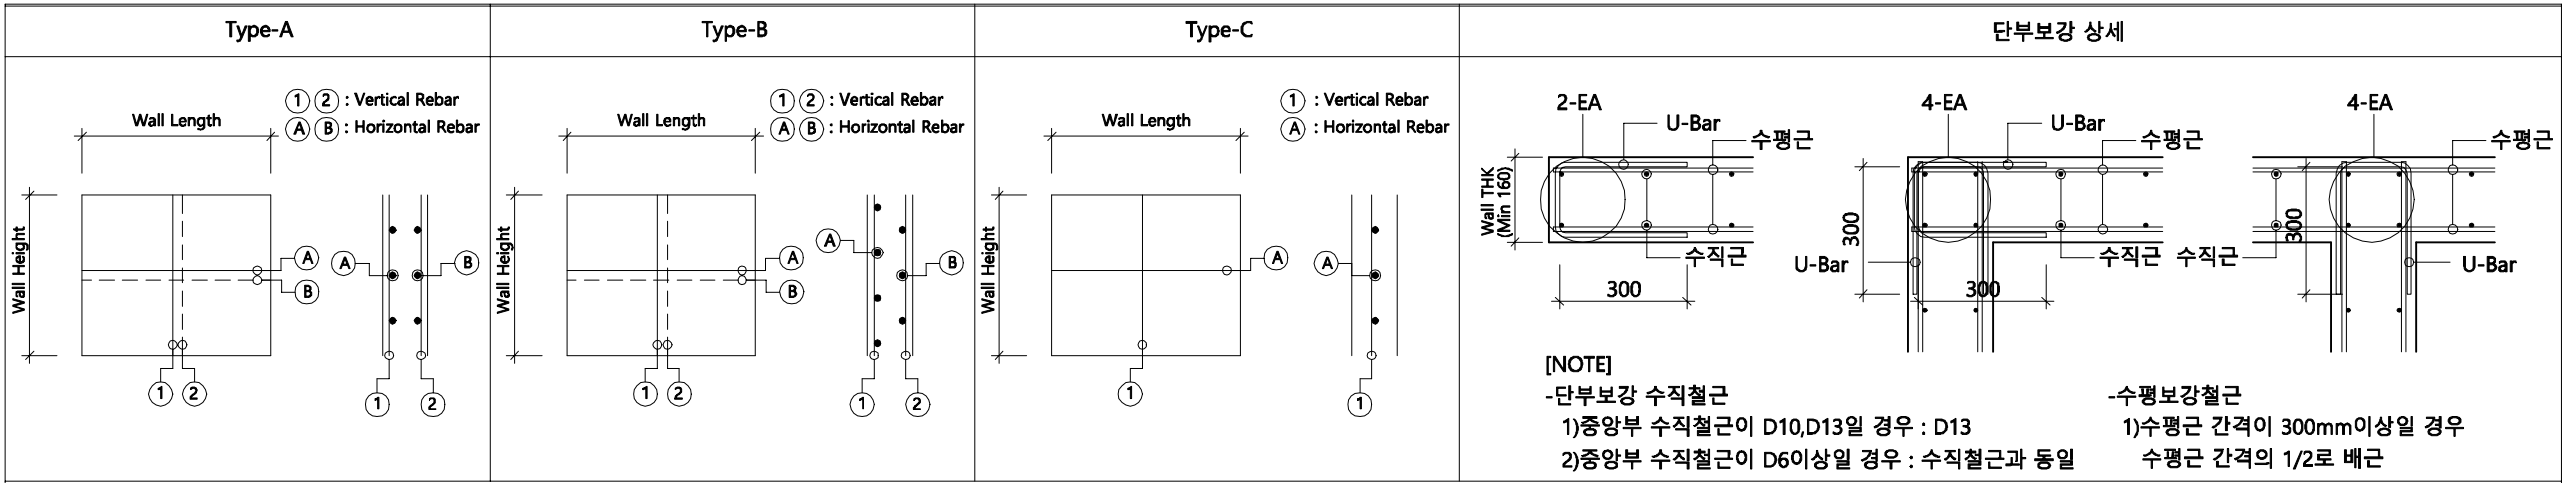

WALL REBAR LIST

| W1 (TYPE-A) |      |         |         |       |     |      |      |      |     |     |      |      |      |     |     |      |      |      |     |
|-------------|------|---------|---------|-------|-----|------|------|------|-----|-----|------|------|------|-----|-----|------|------|------|-----|
| ST.         | THK. | VER.    | HOR.    | END   | ST. | THK. | VER. | HOR. | END | ST. | THK. | VER. | HOR. | END | ST. | THK. | VER. | HOR. | END |
| 전층          | 250  | D16@200 | D13@200 | 4-D13 | 전층  |      |      |      |     | 전층  |      |      |      |     | 전층  |      |      |      |     |

| W2 (TYPE-A) |      |         |         |       |     |      |      |      |     |     |      |      |      |     |     |      |      |      |     |
|-------------|------|---------|---------|-------|-----|------|------|------|-----|-----|------|------|------|-----|-----|------|------|------|-----|
| ST.         | THK. | VER.    | HOR.    | END   | ST. | THK. | VER. | HOR. | END | ST. | THK. | VER. | HOR. | END | ST. | THK. | VER. | HOR. | END |
| 전층          | 200  | D13@200 | D10@200 | 4-D13 | 전층  |      |      |      |     | 전층  |      |      |      |     | 전층  |      |      |      |     |

PROJECT TITLE

리를 포레스트  
봉뜨락 조성사업

PROJECT NO

NOTE

1. 콘크리트 설계기준강도  
(KS F 2405 제령28일 압축강도)  
: f<sub>ck</sub>=30MPa

2. 철근의 항복강도(KS D 3504)  
: f<sub>y</sub>=400MPa(SD400)

2. 단배근의 경우 일반적인 형태이므로  
건축에 맞추어 시공할 것.  
단, 두께 및 형태가 상이할 경우  
구조설계자와 협의 후 시공할 것.

KEY PLAN

DESIGN CORP.



ADD. 대구광역시 동구 장동로 81, 5F  
TEL. 053.716.0776 FAX. 0505.720.0776  
E-mail. e-ul2020@naver.com  
Web. eul2020 / 0776

APPROVED BY  
대표이사/건축사 권오섭

CHECKED BY

DRAWN BY

DATE  
2023. 04.

DRAWING TITLE

벽체 배근도

SCALE  
A3 : 1/ 30

DRAWING NO.  
S02- 103