

리틀 포레스트 봉뜨락 조성공사

(소 방)

봉 화 군

PROJECT TITLE

리틀포레스트
뽕뜨락 조성공사

PROJECT NO

NOTE

도면목록표(소방)

도면번호	도 면 명	축 척 (A1)	축 척 (A3)	비 고
F - 00	도면목록표(소방)	1 / NO	1 / NO	
F - 01	소방공사 일반 시방서	1 / NO	1 / NO	
F - 02	소방 간선 계통도	1 / NO	1 / NO	
F - 03	근린생활시설 1층 소방 설비 신설 평면도	1 / 50	1 / 100	
F - 04	근린생활시설 1층 소방 설비 철거 평면도	1 / 50	1 / 100	
F - 05	놀이시설 1층 소방 설비 신설 평면도	1 / 75	1 / 150	
F - 06	놀이시설 1층 소방 설비 철거 평면도	1 / 75	1 / 150	
F - 07	소방 각종 상세도	1 / NO	1 / NO	

KEY PLAN

DESIGN CORP.



ADD. 대구광역시 동구 장동로 81, 5F
TEL. 053.716.0776 FAX. 0505.720.0776
E-mail. e-ul2020@naver.com
Web. eul2020 / 0776

APPROVED BY

대 표 이 사 / 건 축 사 권 오 섭

CHECKED BY

DRAWN BY

DATE

2024.

DRAWING TITLE

도면목록표(소방)


SCALE

A1: 1/NO, A3: 1/NO

DRAWING NO.

F - 00

(주) 대 림 엔 지 니 어 링
일반소방시설설계업 (제 2018-01-00139호)
대 표 이 사 : 김 동 수
소방 설비 기사(전기,기계분야): 고 창 수
T E L : (0 5 3) - 9 4 1 - 4 9 1 6

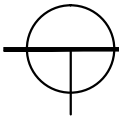

소방공사 일반 시방서

SCALE: 1/NO(A1),1/NO(A3)

1. 특 기 사 항

- 특기없는 전선관은 HI-PVC전선관을 사용하며 단 노출 전선관은 STEEL배관으로 시공하여야 한다.
(감지기 전선관은 HI-PVC전선관을 사용하여야 한다.)
- 관의 곡률반경은 관의 6배이상으로 하고 굴곡각도는 90°이하 이어야하며 1구간의 굴곡개소는 2개소의 합계는 180°이내 이어야 한다.
- 전선관의 접속은 카프링을 사용하고 BOX와의 연결은 콘넥터를 사용하여 접속한다.
- 후렉시를 추브와 BOX의 연결은 STEEL후렉시를 콘넥터를 사용하여야 하며 절단부에는 PVC RPING을 삽입한후 TAPING하여 전선피복이 손상되지 않도록 하여야 한다.
- 8각 및 4각 박스는 STEEL제품을 사용하여 카바는 필히 부착하여야 한다.
- 배관이 1구간에 30m를 초과하거나 현장사정상 필요로 하는곳에는 JIONT BOX 또는 PULL BOX를 설치하여야 한다.
- 전선관내부는 입선전에 관내부를 깨끗이 청소후에 전선을 입선하여야 한다.
- 콘크리트 매입배관시공시에는 이물질이 침투하지않도록 관말구에 PIPE 또는 나무막기등으로 마감처리 한다.
- 노출되는 전선관은 반드시 STEFL PIPE를 사용하여 시공한다.
- 노출되는 전선관지지는 세틀 또는 행가를 사용하여 1.5m마다 견고히 지지하여야 한다.

2. 일 반 사 항

- 본 공사는 소방시설 설치 유지 및 안전관리에 관한법률, 동 법률시행령, 소방시설공사업법, 동 공사업시행령, 화재안전기준 및 부속도면에 의거 시공하여야 한다.
- 본 공사는 소방시설공사업법에 의거 면허된 업체에서 시공 하여야 하며 준공 검사를 득하여야 한다.
- 발신기 및 수신기의 조작스위치는 바닥에서 0.8m 이상, 1.5m 이하의 높이에 설치하여야 한다.
- 본공사 제반수속은 수급자가 공사착공과 동시에 필요한 관계관청(소방서, 이와관련된 관공서등)의 수속(신고, 허가, 검사등)을 필하여야 하며 상기 수속에 필요한 제반비용은 수급자가 부담하여야 한다
- 본공사를 시공하는 수급자는 부득이 하게 준공도서변경을 할시 감독관 또는 감리자와 협의후 시공자가 작성 제출한다.
- 수신기는 사람이 상시 근무하는 장소에 설치할것.다만,사람이 상시근무하는 장소가 없는 경우에는 관계인이 쉽게 접근할 수 있고 관리가 용이한 장소에 설치할수 있으며 수신기가 설치된 장소에는 경계구역 일람도를 비치하여야 한다.
- 감지기 회로의 끝부분에 도통 시험이 용이하도록 중단저항을 설치하여야 한다.
- 감지기 사이의 회로배선은 승배선식으로 하여야 한다.
- 감지기 회로의 배선에 있어서하나의 공통선에 7개 이하의 경계구역으로 접속하여야 한다.
- 감지기의 하단과 그부착면과의 거리는 0.3m (연기감지기에 있어서는 0.6m) 이하로 설치 하여야 한다.
- 감지기는 천정 또는 반자의 옥내에 면하는 부분에 설치하여야 한다.
- 소방용으로 사용되는 전원은 별개의 회로를 사용하고 각각의 소방시설명을 명기하여야 한다.
- 피난구 유도등은 바닥에서 1.5m 이상의 곳에 설치하여야 한다.
- 통로 유도등은 바닥에서 0.5m 이하의 높이에 설치하며, 조명도는 0.5m 떨어진 바닥에서 측정하여 1룩스 이상이어야 한다.
- 복도통로유도등은 구부러진 모퉁이 및 보행거리 20m마다 설치하며, 바닥에 설치하는 통로유도등은 하중에 따라 파괴되지 아니하는 강도의 것으로 하여야 한다.
- 거실통로유도등은 거실의 통로에 설치하는 것으로, 단 거실의 통로가 벽체 등으로 구획된 경우에는 복도통로유도등을 설치하여야 한다.
- 거실통로유도등은 바닥으로부터 높이 1.5m 이상의 위치에 설치할 것. 다만, 거실통로에 기둥이 설치된 경우에는 기둥부분의 바닥으로부터 높이 1.5m 이하의 위치에 설치할 수 있다.
- 지하층에 한하여 피난구 유도등의 전,후에 안내표지판을 설치하여야 한다.
- 유도등의 전원은 축전지 또는 교류전압의 옥내간선으로 하고, 전원까지의 배선은 전용으로 하여야 한다.
- 유도등의 비상전원은 축전지로 하여야 하며 유도등을 20분이상 유효하게 작동시킬수 있는 용량으로 한다.
- 화재 발생 시 하나의 층의 지구음향장치(경종) 배선이 단락되어도 다른 층의 화재통보에 지장이 없도록 각 층 배선 상에 유효한 조치를 할 것. - 단차대(2차측)에서 지구음향장치(경종) 사이에 FUSE를 설치할 것.
- 자동화재탐지설비는 음향장치외에 별도의 청각장애인용 시각경보 장치를 설치하도록 한다.
- 청각장애인용 시각경보장치는 한국소방검정공사 또는 법제42조의 규정에 따라 성능시험업무를 위탁받은 기관에서 검증받은 것으로서 다음각목의 기준에 따라 설치하여야 한다.
 - 복도, 통로, 청각장애인용 객실 및 공용으로 사용하는 거실(로비, 회의실, 강의실, 식당, 휴게실 등을 말한다.)에 설치하며, 각 부분으로부터 유효하게 경보를 발할 수 있는 위치에 설치할 것
 - 공연장, 집회장, 관람장 또는 이와 유사한 장소에 설치하는 경우에는 시선이 집중되는 무대부 부분등에 설치할 것
 - 설치높이는 바닥으로부터 2m 이상 2.5m 이하의 장소에 설치할 것
 - 시각경보장치의 광원은 전용의 축전설비에 의하여 점등되도록 할 것.

3. 소방시설의 내진설계

가. 제어반은 다음 각 호의 기준에 따라 설치하여야 한다.

- 벽면에 설치하는 경우 직경 8mm 이상의 고정용 볼트를 4개 이상 고정하여야 한다.
- 바닥에 설치하는 경우 지진하중에 의해 전도가 발생하지 않도록 설치하여야 한다.
- 수계소화설비에 사용되는 수신기 및 증계기는 지진발생 시 전도되지 않도록 설치하여야 한다.

나. 함은 다음 각 호의 기준에 따라 설치하여야 한다.

- 함은 지진 시 개폐에 장애가 발생하지 않아야 한다.
- 노출형 함이 설치되는 벽면은 충분한 강도를 가져야하고 노출형 함은 중량 1000Kg이하인 설비로 분류하여 아래의 기준에 따라 바닥면에 고정하여야 한다.

- 가동중량 1,000Kg 이하인 설비는 바닥면에 고정되는 길이가 긴 변의 양쪽 모서리에 직경 12mm이상의 앵커볼트로 고정하여야 하며 앵커볼트의 근입 길이는 10cm 이상이어야 한다.

- 비내력벽에는 함을 설치하지 않는다.

다. 비상전원은 다음 각 호의 기준에 따라 설치하여야 한다.

- 비상전원을 위한 비상발전장치의 경우 아래의 기준에 따라 설치하여야 한다.

- 가동중량 1,000Kg 이하인 설비는 바닥면에 고정되는 길이가 긴 변의 양쪽 모서리에 직경 12mm이상의 앵커볼트로 고정하여야 하며 앵커볼트의 근입 길이는 10cm 이상이어야 한다.
- 가동중량 1,000Kg 이상의 설비는 바닥면에 고정되는 길이가 긴 변의 양쪽 모서리에 직경 20mm이상의 앵커볼트로 고정하여야 하며 앵커볼트의 근입 길이는 10cm 이상이어야 한다.

- 예비전원은 지진발생시 전도되지 않도록 설치하여야 한다.

심 별	명 칭	설 치 높 이
	피난구유도등 - 소형 (벽부형)	MH:1500mm 이상
	피난구유도등 - 대형 (벽부형)	MH:1500mm 이상
	거실 통로 유도등 - 대형 (천장형)	천장면
	통로유도등 - 단방향 (거실용)	MH:1500mm 이상
	경보셋트 수동 발신기	MH:1500mm 이하
	스프링클러설비 - 알람벨브	설비공사분
	전자 싸이렌	MH:1500mm 이상
	자동화재 주 수신기 P형 1급 15회로용 (복합형)	MH:800mm~MH:1500mm
	4각박스 및 PULL BOX	천장면
	전선관 및 전선의 천장 매입 배관 배선 표기	
	전선관 및 전선의 천장 노출 배관 배선 표기	
	전선관 및 전선의 바닥 배관 배선 표기	
	전선관 및 전선의 지중 배설 배관 배선 표기	
	전선관 및 전선의 입상,입하 표기	

(주) 대 림 엔 지 니 어 링
일반소방시설설계업 (제 2018-01-00139호)
대 표 이 사 : 김 동 수
소방 설비 기사(전기,기계분야): 고 창 수
T E L : (0 5 3) - 9 4 1 - 4 9 1 6

PROJECT TITLE

리틀포레스트
뽕뜨락 조성공사

PROJECT NO

NOTE

KEY PLAN

DESIGN CORP.

이림 (주)이름건축사사무소

ADD. 대구광역시 동구 장동로 81, 5F
TEL. 053.716.0776 FAX. 0505.720.0776
E-mail. e-ul2020@naver.com
Web. eul2020 / 0776

APPROVED BY
대 표 이 사 / 건 축 사 권 오 섭

CHECKED BY

DRAWN BY

DATE
2024.

DRAWING TITLE

소방공사 일반 시방서

SCALE
A1: 1/NO, A3: 1/NO

DRAWING NO.
F - 01

PROJECT TITLE

리틀포레스트
뽕뜨락 조성공사

PROJECT NO

NOTE

KEY PLAN

DESIGN CORP.

이엘 (주)이엘건축사사무소

ADD. 대구광역시 동구 장동로 81, 5F
TEL. 053.716.0776 FAX. 0505.720.0776
E-mail. e-ul2020@naver.com
Web. eul2020 / 0776

APPROVED BY
대표이사 / 건축사 권오섭

CHECKED BY

DRAWN BY

DATE
2024.

DRAWING TITLE

소방 간선 계통도

SCALE
A1: 1/NO, A3: 1/NO


DRAWING NO.
F - 02

소방 간선 계통도

SCALE: 1/NO(A1),1/NO(A3)

놀이시설

지붕층

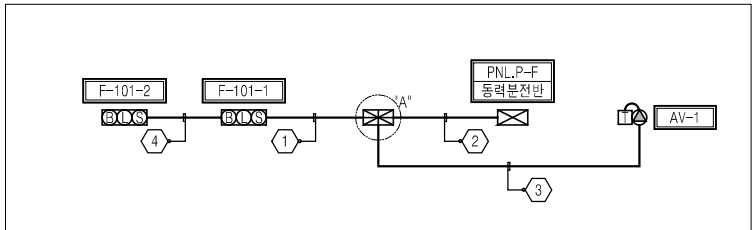

1층



G.L

A 자동화재 주 수신기(복합형)
P형 1급 15회로용
(비상경보: 2회로, 스프링클러(알람벨브): 2회로,
T/S: 4회로, P/S: 3회로, L/S: 1회로, 예비: 3회로)
MH:1300mm
오동작 방지회로 내장형
감시 제어반 내장

CABLE SCHEDULE

NO.	FROM	TO	CABLE & CONDUIT	REMARK
①	*A*	F-101-1	HFIX 8-2.5" 28C	비상경보
②		PNL,P-F	F-FR-8 30/C 2.5" 54C	소방펌프
③		AV-1	HFIX 4-2.5" 28C	알람벨브
④	F-101-1	F-101-2	HFIX 7-2.5" 28C	비상경보

(주) 대림엔지니어링
일반소방시설설계업 (제 2018-01-00139호)
대표이사 : 김동수
소방설비기사(전기,기계분야): 고창수
TEL : (0 5 3) - 9 4 1 - 4 9 1 6

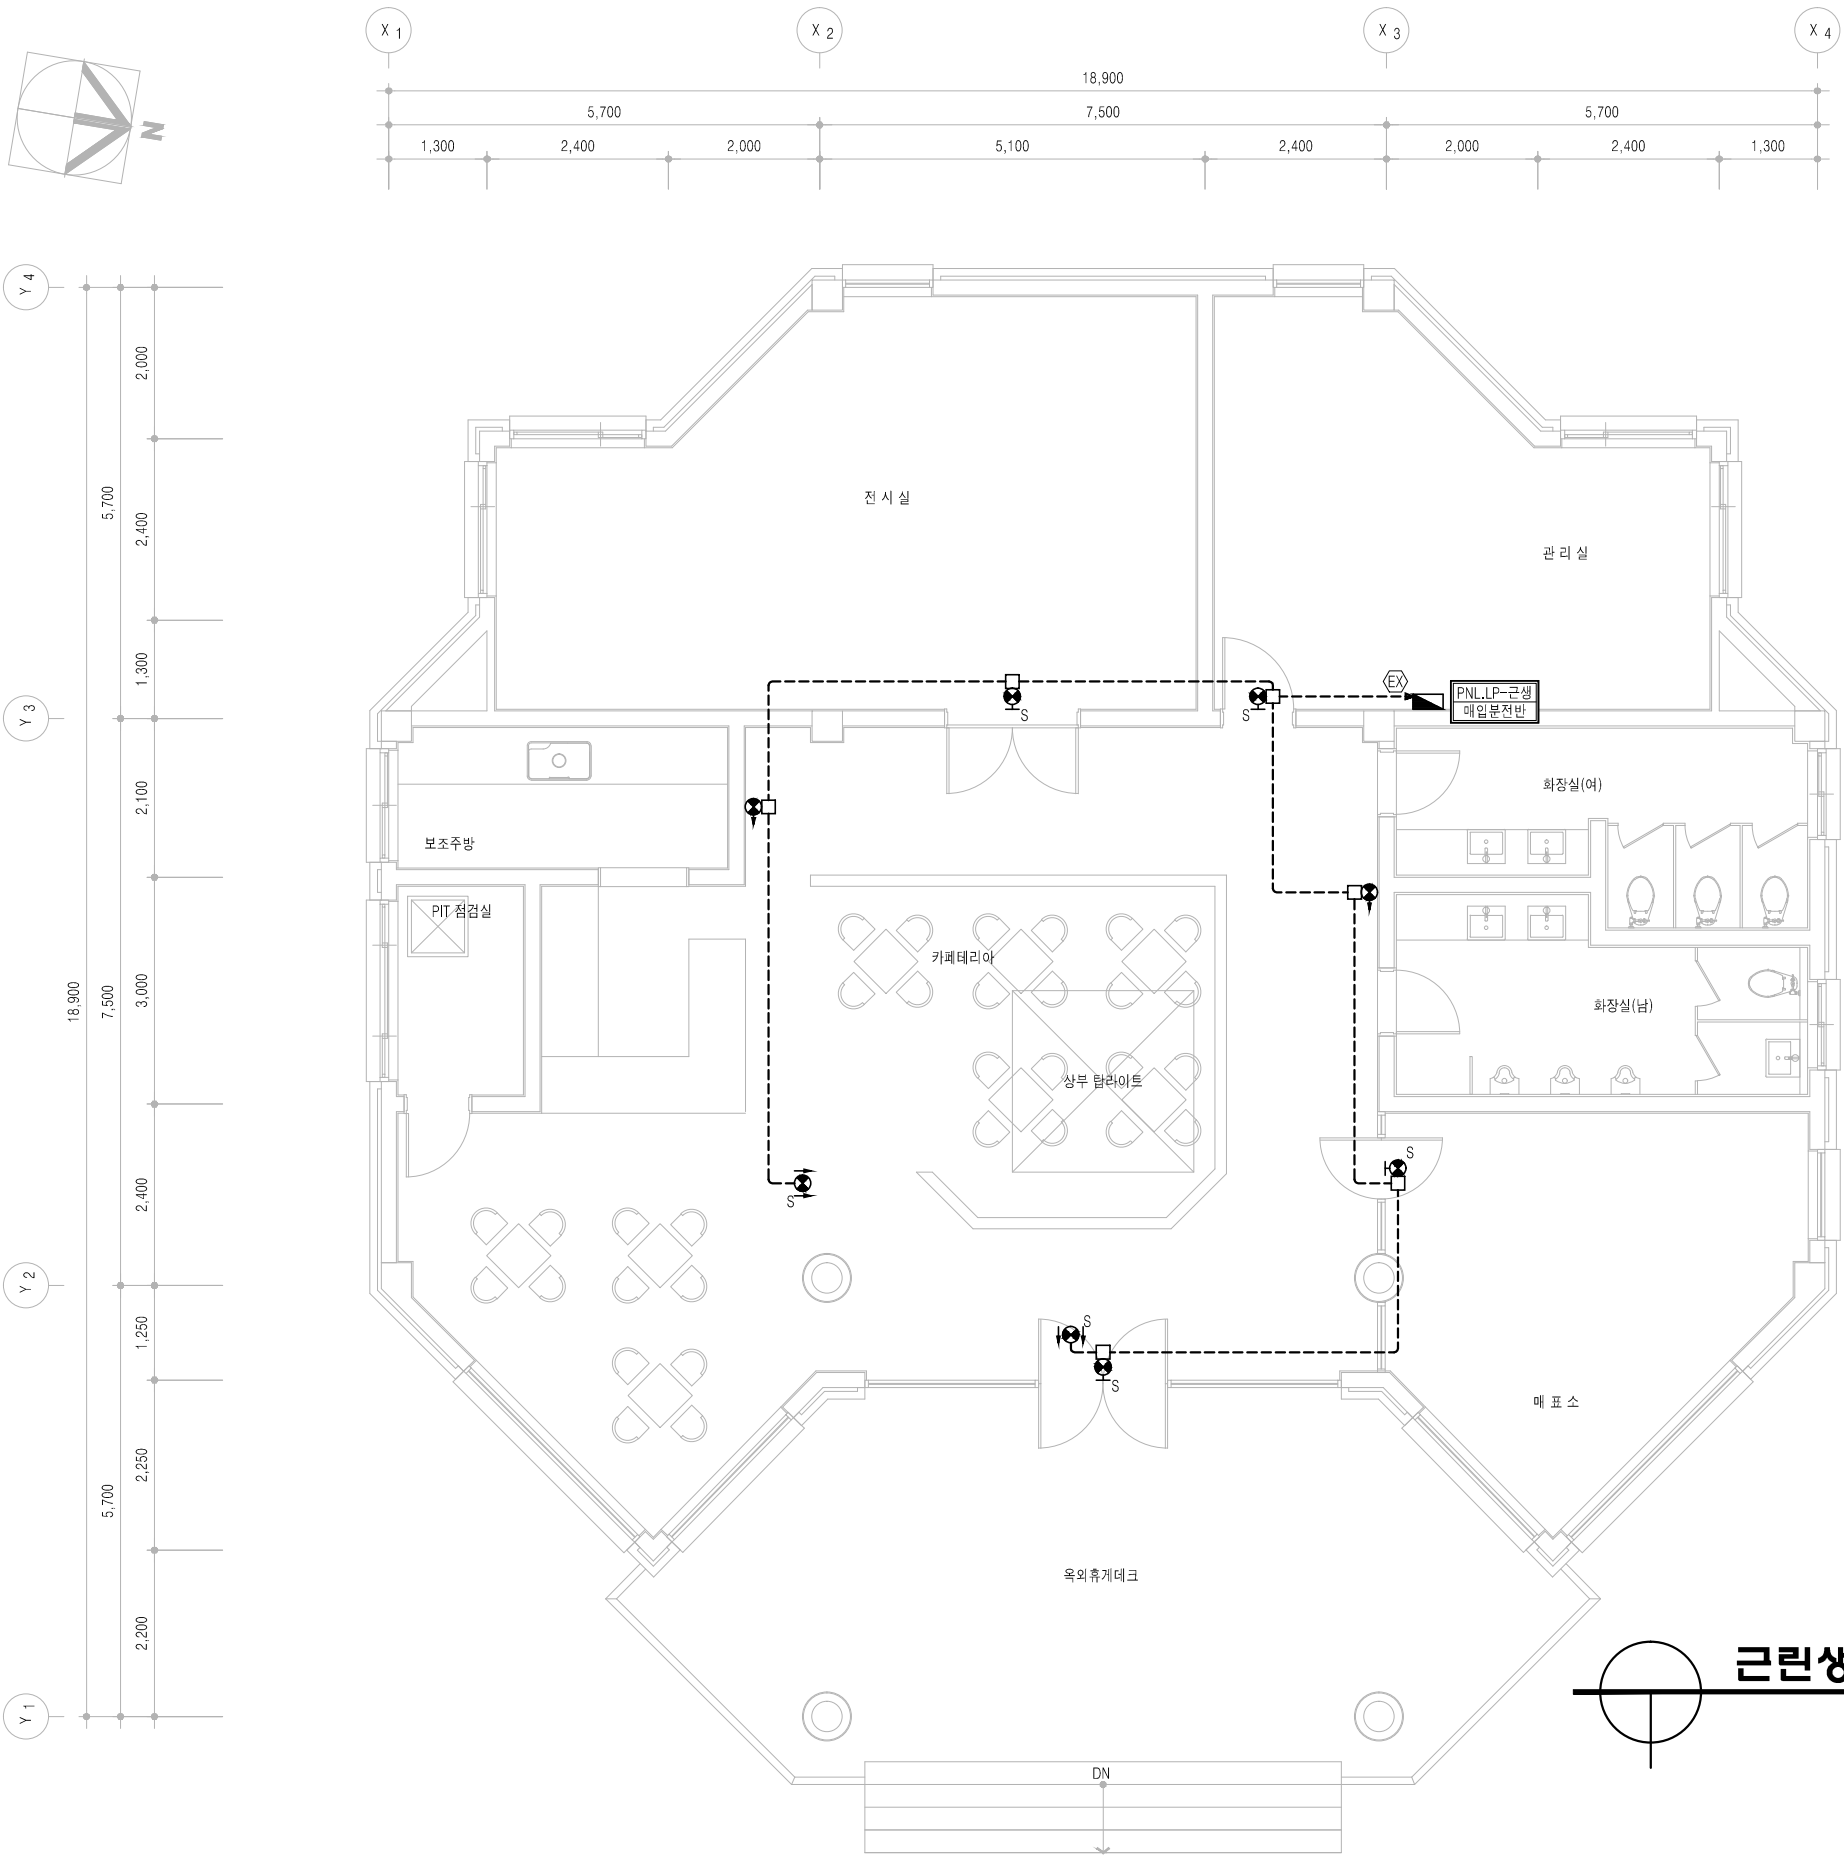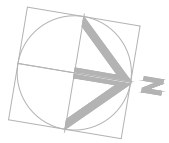

LEGEND & NOTE

심 별	명 칭	규 격	수 량	비 고
☼ S	피난구 유도등	소형 (벽부형)	4 EA	신 설
☼ S	거실 통로 유도등 - 양방향	소형 (천장형)	2 EA	신 설
☼	거실 통로 유도등 - 단방향	벽부형	2 EA	신 설

1. 특기없는 유도등 배관 배선은 공히 아래와 같다.
----- HFIX 2-2.5" & 2.5" (E) 16C

2. 시공 전 반드시 발주처 및 감독관과 협의 후 시공에 임한다.
3. 콘크리트 슬라브 및 벽체 매입배관은 난연CD관을 사용한다.
4. 노출되는 배관은 STEEL관이나 1종금속제가요전선관으로 시공하며, 부속품은 금속재질로 한다.
5. 노출되는 배관은 1.5[M]마다 새들이나 PIPE HANGER로 견고히 지지한다.

근린생활시설 1층 소방 설비 신설 평면도

SCALE: 1/50(A1), 1/100(A3)

(주) 대 림 엔 지 니 어 링
일반소방시설설계업 (제 2018-01-00139호)
대 표 이 사 : 김 동 수
소방 설비 기사(전기,기계분야): 고 창 수
TEL : (0 5 3) - 9 4 1 - 4 9 1 6

PROJECT TITLE
**리틀포레스트
뽕뜨락 조성공사**

PROJECT NO

NOTE

KEY PLAN

DESIGN CORP.
이림 (주)이름건축사사무소
ADD. 대구광역시 동구 장동로 81, 5F
TEL. 053.716.0776 FAX. 0505.720.0776
E-mail. e-ul2020@naver.com
Web. eul2020 / 0776

APPROVED BY
대 표 이 사 / 건 축 사 권 오 섭

CHECKED BY



DRAWN BY

DATE
2024.

DRAWING TITLE
**근린생활시설 1층
소방 설비 신설 평면도**

SCALE
A1: 1/50, A3: 1/100

DRAWING NO.
F - 03

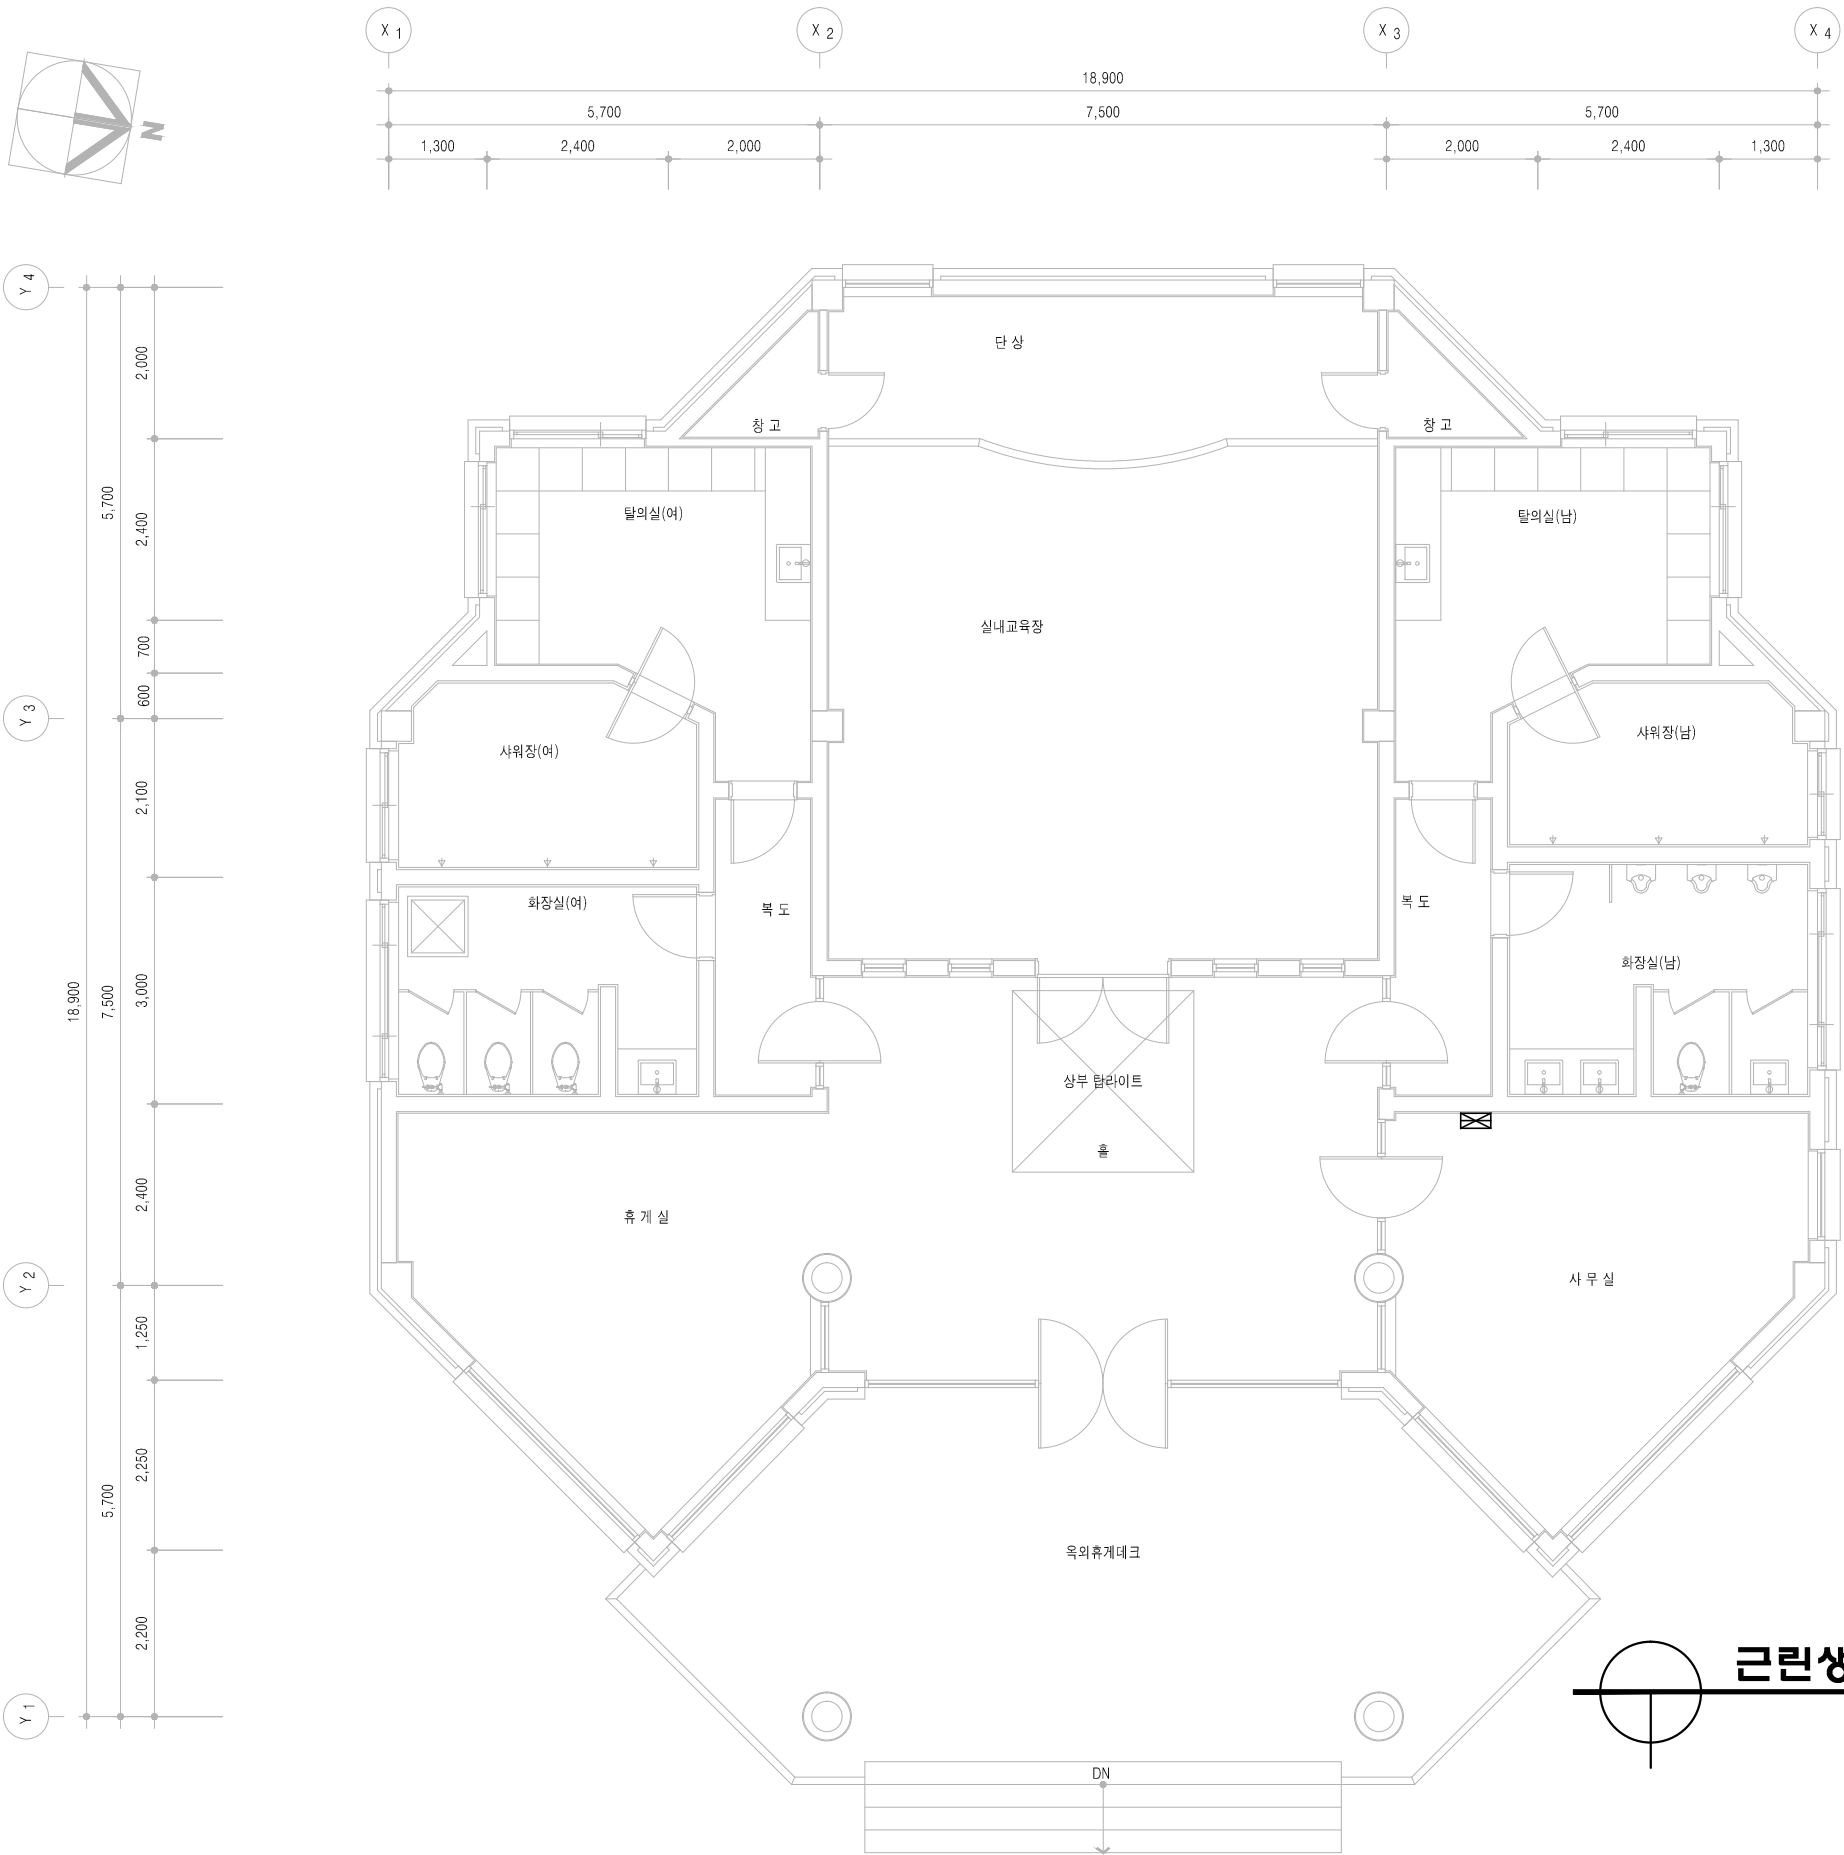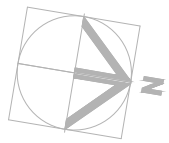

LEGEND & NOTE

심 별	명 칭	규 격	수 량	비 고
☒	비상경보 주 수신기 P형 1급	5회로용	1 EA	철 거
* 시공 시 기존 시설물에 주의하여 시공하며, 파손 발생 시 시공자가 반드시 원상 복구 하여야 한다.				
* 시공 전 반드시 발주처 및 감독관과 협의 후 시공에 임한다.				

근린생활시설 1층 소방 설비 철거 평면도
SCALE: 1/50(A1), 1/100(A3)

(주) 대 림 엔 지 니 어 링
일반소방시설설계업 (제 2018-01-00139호)
대 표 이 사 : 김 동 수
소방 설비 기사(전기,기계분야): 고 창 수
TEL : (0 5 3) - 9 4 1 - 4 9 1 6

PROJECT TITLE
**리틀포레스트
뽕뜨락 조성공사**

PROJECT NO

NOTE

KEY PLAN

DESIGN CORP.
이림 (주)이음건축사사무소
ADD. 대구광역시 동구 장동로 81, 5F
TEL. 053.716.0776 FAX. 0505.720.0776
E-mail. e-ul2020@naver.com
Web. eul2020 / 0776

APPROVED BY
대 표 이 사 / 건 축 사 권 오 섭

CHECKED BY


DRAWN BY

DATE
2024.

DRAWING TITLE
근린생활시설 1층
소방 설비 철거 평면도

SCALE
A1: 1/50, A3: 1/100

DRAWING NO.
F - 04

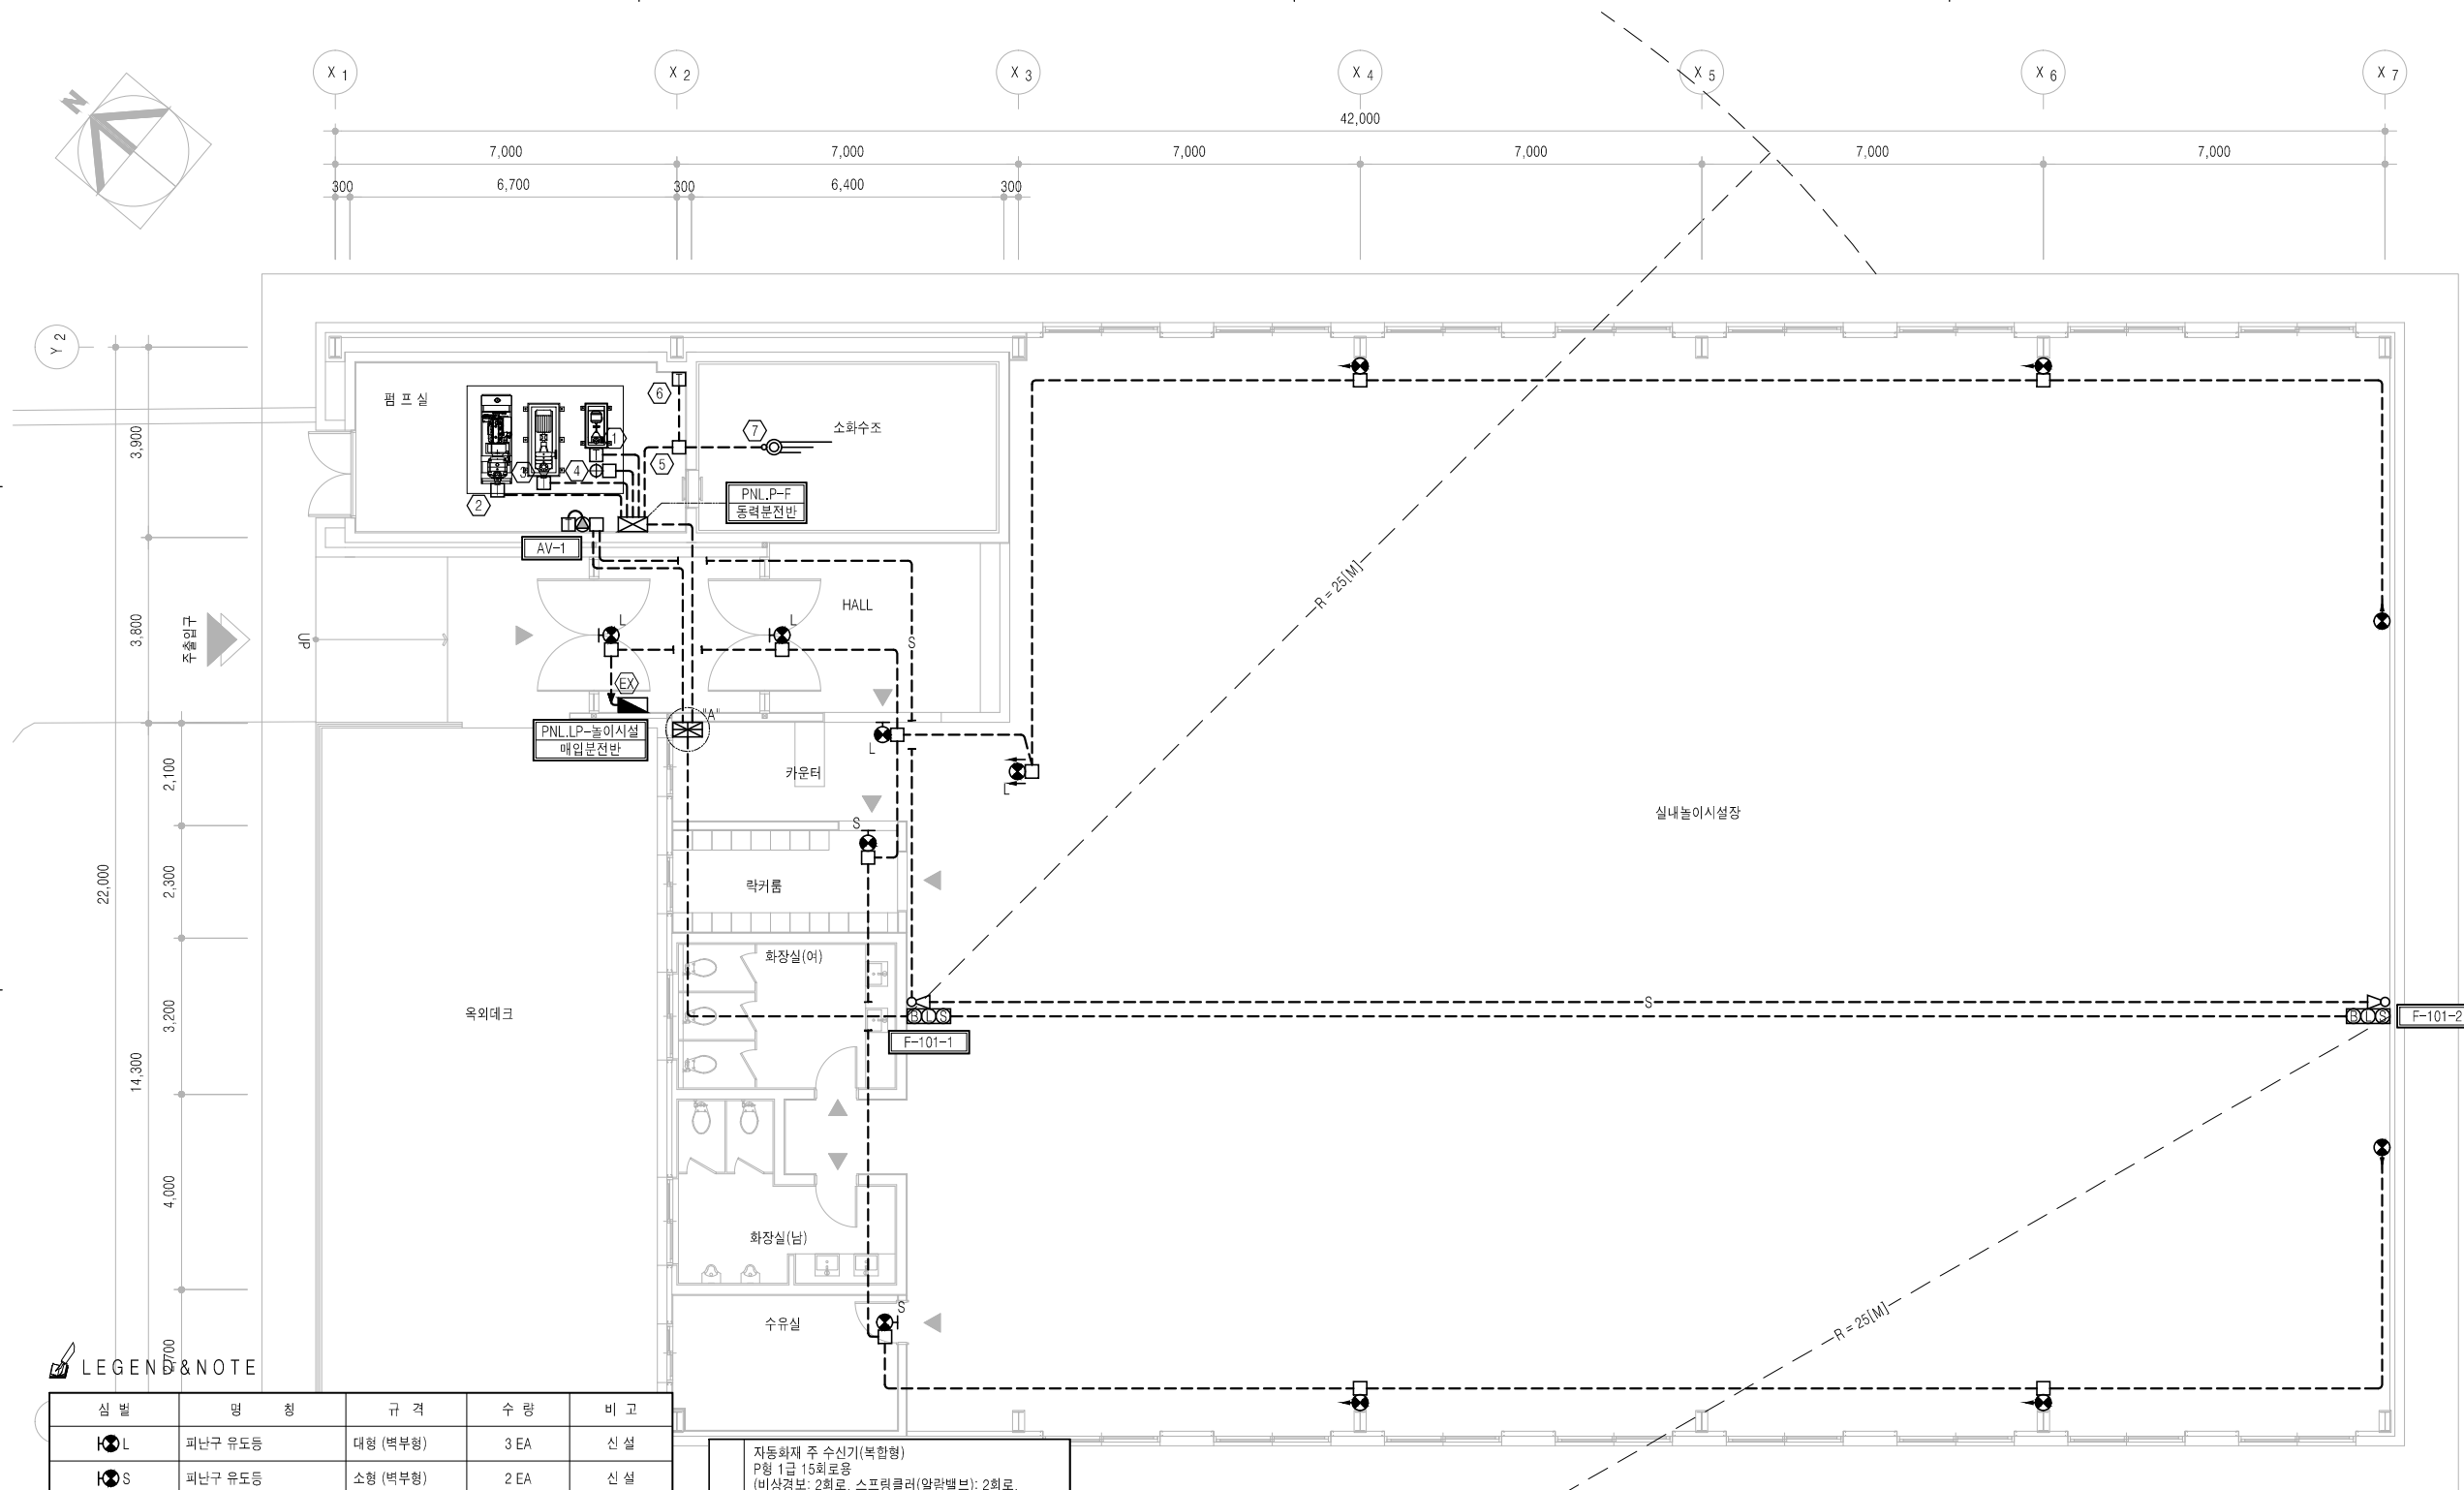

LEGEND & NOTE

심	별	명	청	규	격	수	량	비	고
●	L	피난구 유도등	대형 (벽부형)	3	EA	신	설		
●	S	피난구 유도등	소형 (벽부형)	2	EA	신	설		
●	L	거실 통로 유도등 - 양방향	대형 (천장형)	1	EA	신	설		
●	S	거실 통로 유도등 - 단방향	벽부형	6	EA	신	설		
●	●	경보 셋트 수동 발신기	-	2	EA	신	설		
●	●	자동화재 주 수신기 P형 1급	15회로용 (복합형)	1	EA	신	설		
●	●	스프링클러설비	알람벨브	1	EA	설	비	공	사
●	●	전자싸이렌	-	2	EA	신	설		

- 특기없는 유도등 배선은 공히 아래와 같다.
----- HFIX 2-2.5" & 2.5" (E) 16C
- 특기없는 알람벨브 배선은 공히 아래와 같다.
----- HFIX 3-1.5" 16C
- 특기없는 전자싸이렌 배선은 공히 아래와 같다.
----- HFIX 2-2.5" & 2.5" (E) 16C
- 시공 전 반드시 발주처 및 감독관과 협의 후 시공에 임한다.
- 콘크리트 슬라브 및 벽체 매입배관은 난연CD관을 사용한다.
- 노출되는 배관은 STEEL관이나 1종금속체가요전선관으로 시공하며, 부속품은 금속재질로 한다.
- 노출되는 배관은 1.5[M]마다 세들이나 PIPE HANGER로 견고히 지지한다.


"A"
자동화재 주 수신기(복합형)
P형 1급 15회로용
(비상경보: 2회로, 스프링클러(알람벨브): 2회로,
T/S: 4회로, P/S: 3회로, L/S: 1회로, 예비: 3회로)
MH: 1300mm
오동작 방지회로 내장형
감시 제어반 내장

기 호	FROM	기기명	FEEDER
①	PNL.P-F	소화 주 펌프 (스프링클러용)	F-FR-8 6/C 2.5" 28C
②	PNL.P-F	소화 예비펌프-연진펌프 (스프링클러용)	F-FR-8 6/C 2.5" 28C
③	PNL.P-F	소화 보조 펌프 (스프링클러용)	F-FR-8 6/C 2.5" 28C
④	PNL.P-F	전자식 압력 스위치	F-FR-8 6/C 2.5" 28C
⑤	PNL.P-F	소화수조	F-FR-8 5/C 2.5" 28C
⑥	PNL.P-F	소화수조 탬퍼스위치	F-FR-8 5/C 2.5" 28C
⑦	PNL.P-F	소화수조 Level Switch	F-FR-8 5/C 2.5" 28C


놀이시설 1층 소방 설비 신설 평면도

SCALE: 1/75(A1), 1/150(A3)

(주) 대림엔지니어링
일반소방시설설계업 (제 2018-01-00139호)
대표이사 : 김동수
소방설비 기사(전기, 기계분야): 고창수
TEL : (0 5 3) - 9 4 1 - 4 9 1 6

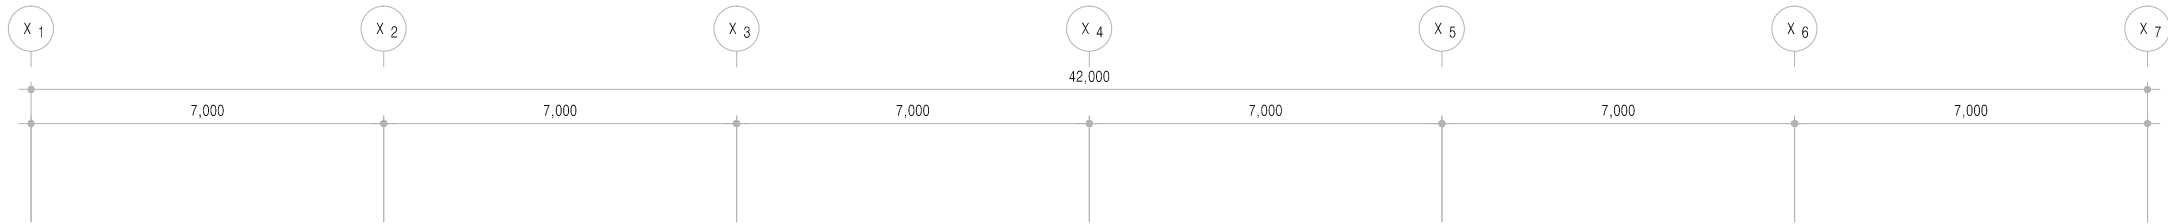

Y 2

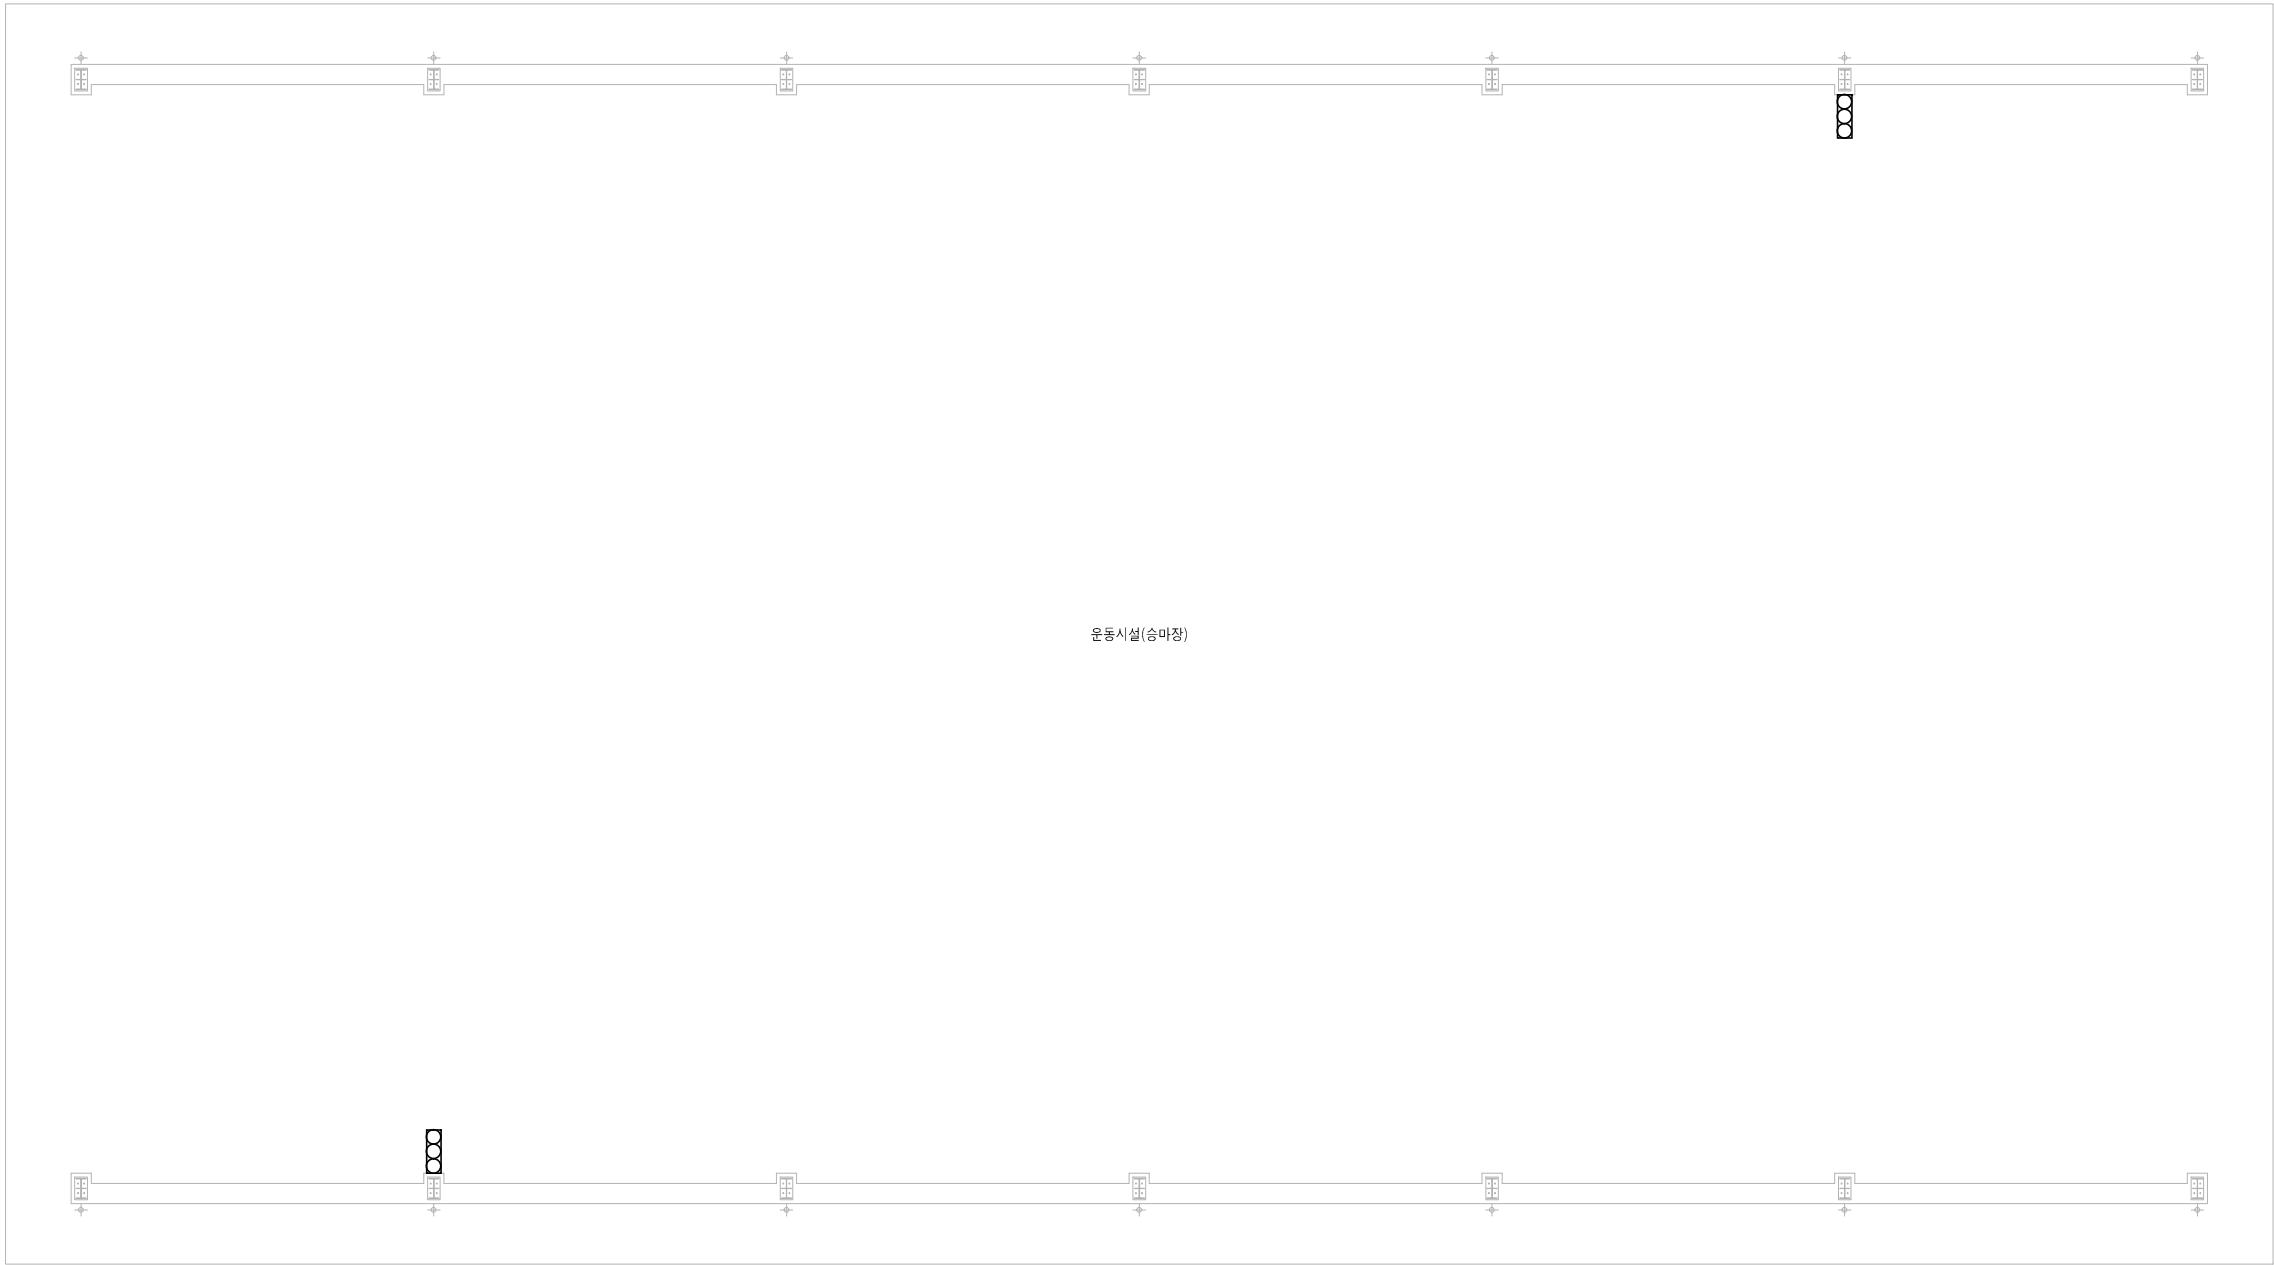


22,000

Y 1



LEGEND & NOTE

심 별	명 칭	규 격	수 량	비 고
○○○	경보셋트수동발신기	-	2 EA	철 거
* 시공 시 기존 시설물에 주의하여 시공하며, 파손 발생 시 시공자가 반드시 원상 복구 하여야 한다. * 시공 전 반드시 발주처 및 감독관과 협의 후 시공에 임한다.				

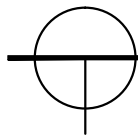

놀이시설 1층 소방 설비 철거 평면도

SCALE: 1/75(A1), 1/150(A3)

(주) 대 립 엔 지 니 어 링
일반소방시설설계업 (제 2018-01-00139호)
대 표 이 사 : 김 동 수
소방 설비 기사(전기,기계분야): 고 창 수
TEL : (0 5 3) - 9 4 1 - 4 9 1 6

PROJECT TITLE

리틀포레스트
붕뜨락 조성공사

PROJECT NO

NOTE

KEY PLAN

DESIGN CORP.



ADD. 대구광역시 동구 장동로 81, 5F
TEL. 053.716.0776 FAX. 0505.720.0776
E-mail. e-ul2020@naver.com
Web. eul2020 / 0776

APPROVED BY

대 표 이 사 / 건 축 사 권 오 섭

CHECKED BY

DRAWN BY

DATE

2024.

DRAWING TITLE

놀이시설 1층
소방 설비 철거 평면도

SCALE

A1: 1/75, A3: 1/150

DRAWING NO.

F - 06

소방 각종 상세도
SCALE: 1/NO(A1), 1/NO(A3)

차동식 감지기

정온식 감지기

연기 감지기

차동식 감지기

정온식 감지기

연기 감지기

감지기 설치 상세도 (경사지붕)

감지기 설치 상세도 (박스타임)

(벽부노출형)

A. 사용전압	AC 220V용
B. 표시면	녹색바탕에 백색글씨

	W	H	D	LAMP	BAT
소형	141	165	13	1.5W	4.8V 350mAh
중형	221	245	13	3.5W	4.8V 600mAh
대형	261	285	13	4.5W	4.8V 1.3Ah

• 피난구유도등은 규격별로 한국소방검정공사 검정 합격품을 사용함
• 피난방향이 필요한 경우에는 피난방향을 표시한 것을 사용함
• 유도등의 크기는 제작업체에 따라 상이할수 있음

(천장노출형)

A. 사용전압	AC 220V용
B. 표시면	녹색바탕에 백색글씨

	W	H	D	LAMP	BAT
소형	229	147	33	1.8W	3.6V 350mAh
중형	268	227	33	3.0W	4.8V 600mAh
대형	308	267	33	5.0W	4.8V 1300mAh

• 피난구유도등은 규격별로 한국소방검정공사 검정 합격품을 사용함
• 피난방향이 필요한 경우에는 피난방향을 표시한 것을 사용함
• 유도등의 크기는 제작업체에 따라 상이할수 있음

고휘도 피난구 유도등 (벽부형-LED)

고휘도 피난구 유도등 (천장형-LED)

수동 발신기 셋트

수동발신기함 내부 결선도

P형 1급 비상경보 주수신기

(주) 대 림 엔 지 니 어 링
일반소방시설설계업 (제 2018-01-00139호)
대 표 이 사 : 김 동 수
소방 설비 기사(전기,기계분야): 고 창 수
TEL : (0 5 3) - 9 4 1 - 4 9 1 6

PROJECT TITLE
**리틀포레스트
뽕뜨락 조성공사**

PROJECT NO

NOTE

KEY PLAN

DESIGN CORP.
이엘 (주)이엘건축사사무소
ADD. 대구광역시 동구 장동로 81, 5F
TEL. 053.716.0776 FAX. 0505.720.0776
E-mail. e-ul2020@naver.com
Web. eul2020 / 0776

APPROVED BY
대 표 이 사 / 건 축 사 권 오 섭

CHECKED BY

DRAWN BY

DATE
2024.

DRAWING TITLE
소방 각종 상세도

SCALE
A1: 1/NO, A3: 1/NO

DRAWING NO.
F - 07